# SITE DETAILS:

STREET ADDRESS
Villas 68 & 69 - Laguna Retirement Estate
13-21 Lake Weyba Drive, Noosaville, Qld 4566

COUNCIL RECORDS ADDRESS
25 Nannygai Street, Noosaville, Qld 4566

RPD
Lot 1 on SP 141238
Parish - Weyba
County - March

LOCAL AUTHORITY
Noosa Shire Council

SITE AREA
5.275 Ha




| ISSUE | DATE | DESCRIPTION |
|---|---|---|
| A | 01/09/25 | ISSUED FOR APPROVALS |

© COPYRIGHT NOTICE
Copyright of this drawing and design is held permanently by Carma Building Group Pty Ltd. Unauthorised use of this drawing and / or design, or any variation thereof, will trigger immediate legal proceedings.

carma building group
Suite 2 / 199 Gympie Tce, Noosaville Q 45(
T 07 5447 1250 F 07 5470 2586
E admin@carmabuildinggroup.com.au

PROJECT
VILLAS 68 & 69
LAGUNA ESTATE
13 LAKE WEYBA DRIVE
NOOSAVILLE


CLIENT
LAGUNA RETIREMENT ESTATE

DRAWING TITLE
SITE PLAN

| SCALE | @ ORIGINAL SIZ |
|---|---|
| 1:1500 | A3 |
| DATE | DRAW |
| AUGUST 2025 | MW |

DRAWING STATUS
FOR CONSTRUCTION

| DRAWING NO. | ISSU |
|---|---|
| LRV068 WD-02 | A |

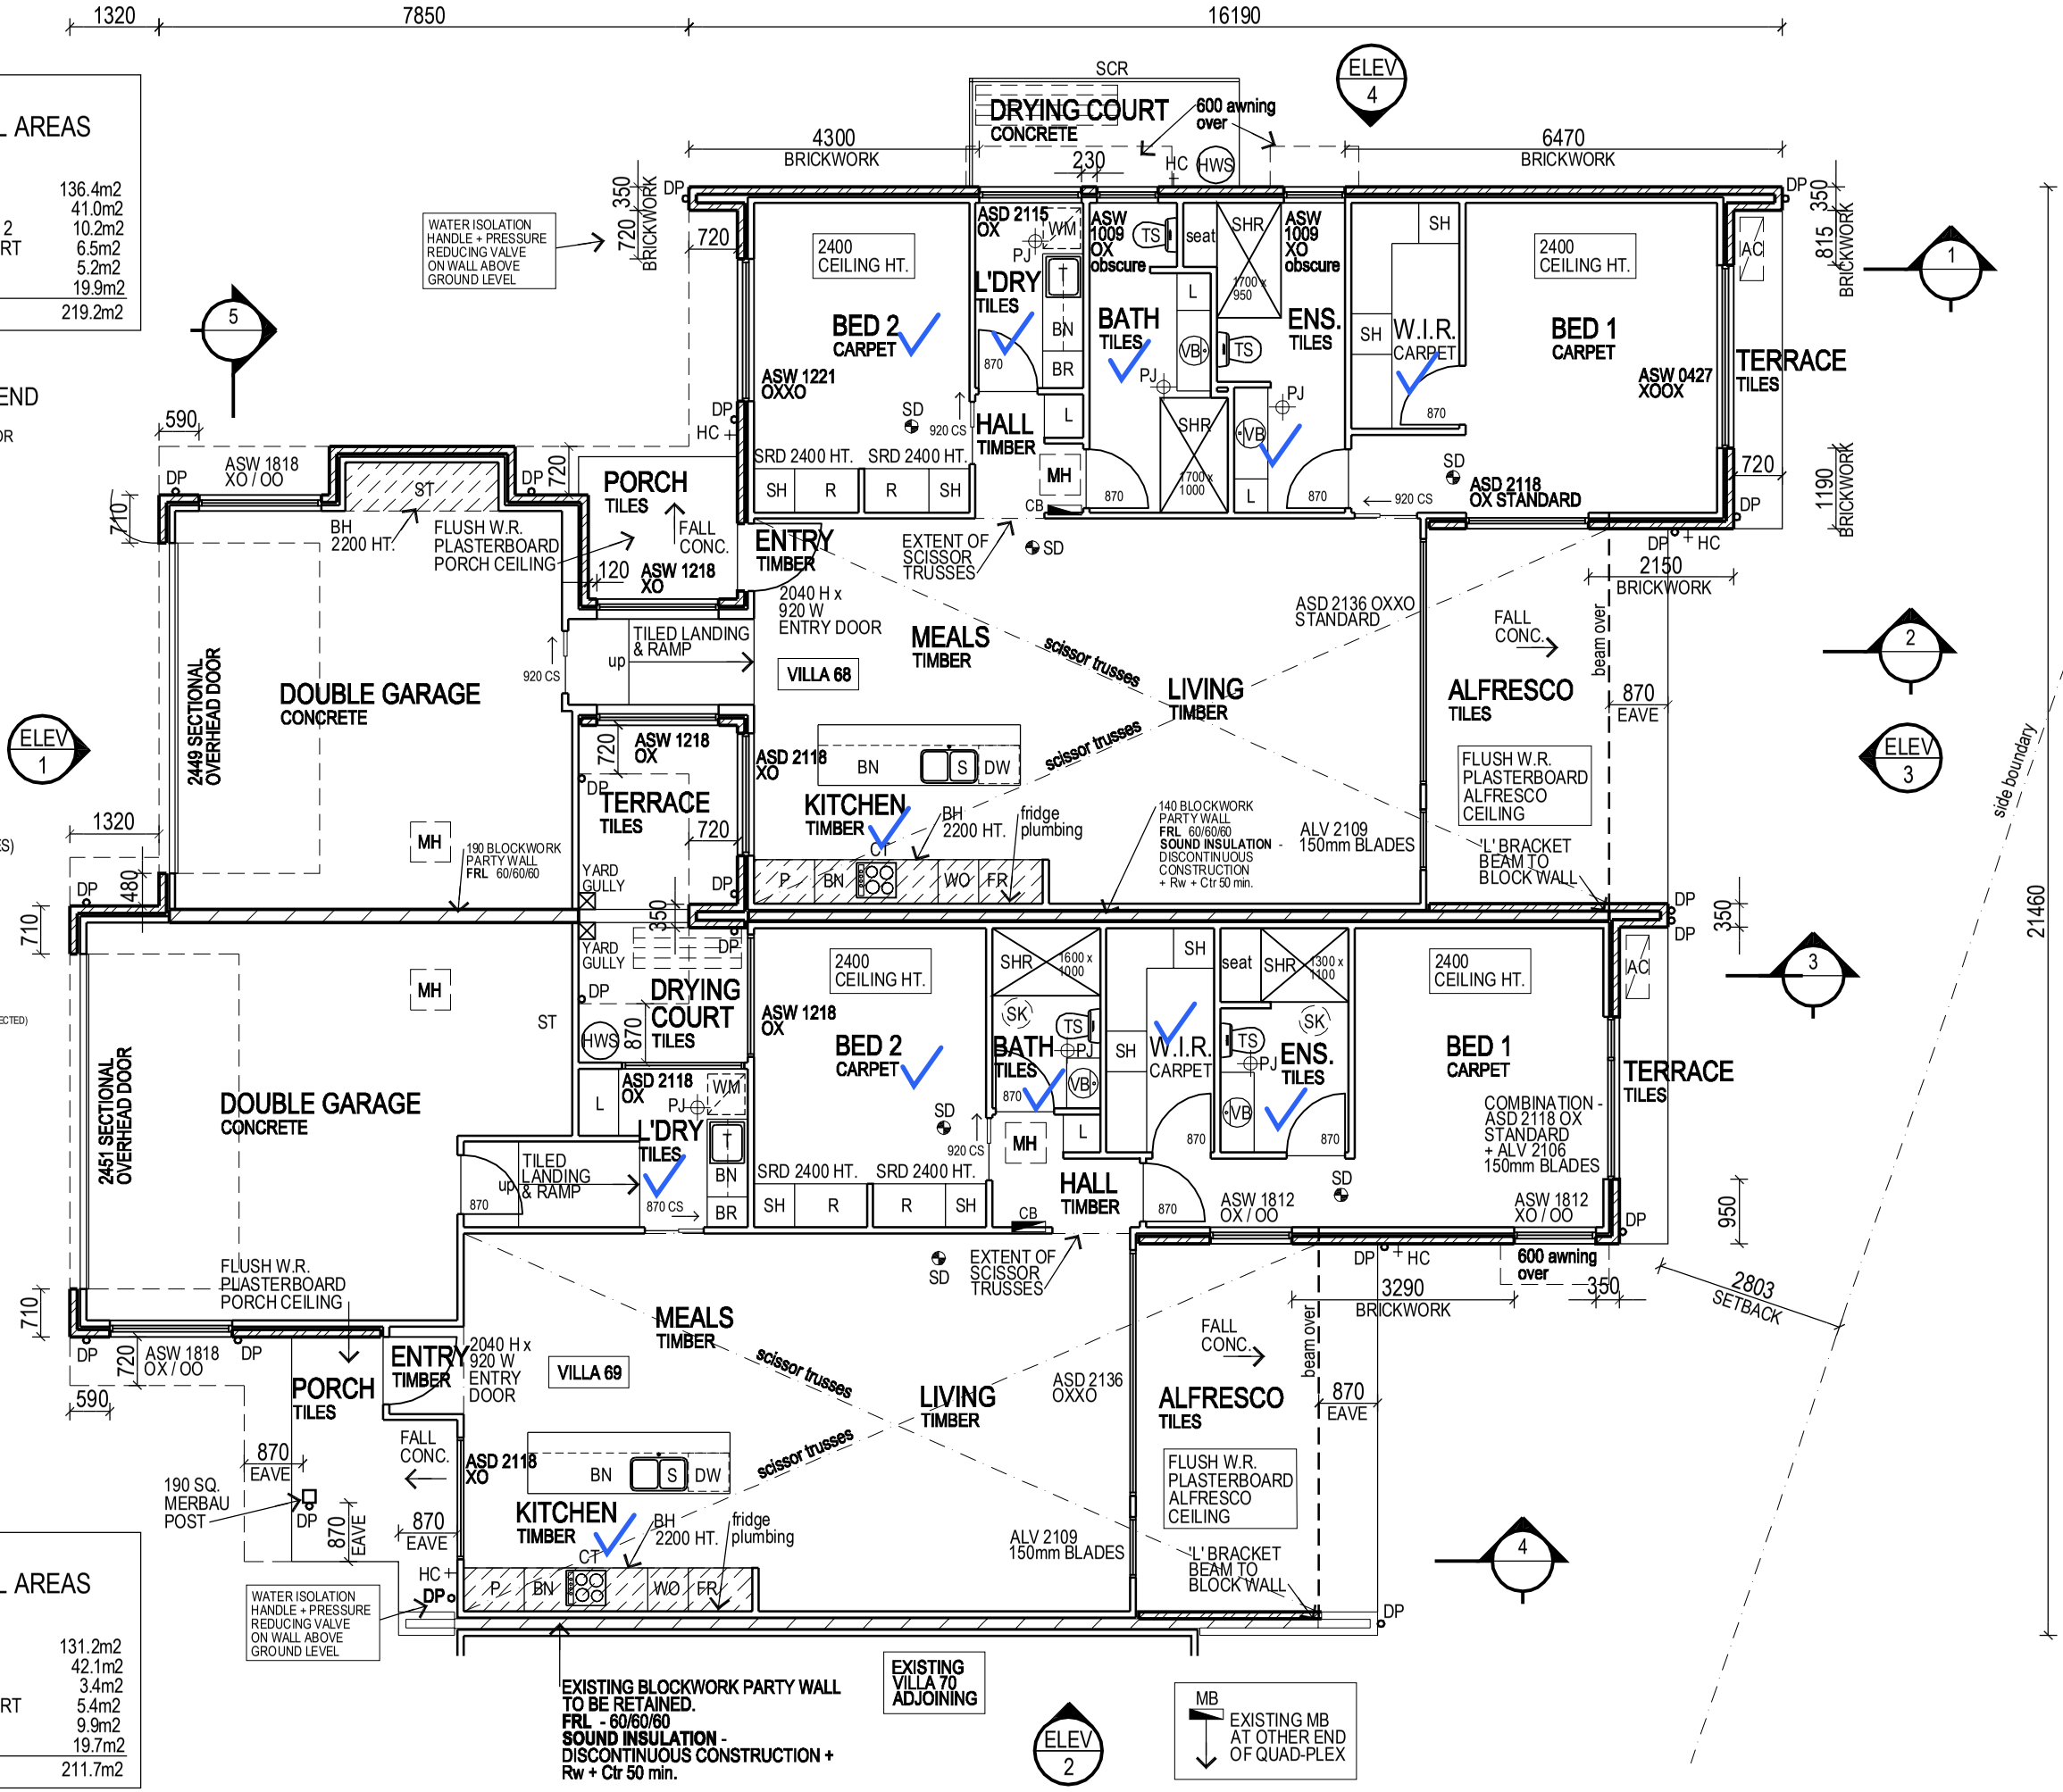


## VILLA 68 INTERNAL AREAS

EXCL. EAVES

| | |
|---|---|
| VILLA | 136.4m2 |
| GARAGE | 41.0m2 |
| TERRACES x 2 | 10.2m2 |
| DRYING COURT | 6.5m2 |
| PORCH | 5.2m2 |
| ALFRESCO | 19.9m2 |
| TOTAL - V68 | 219.2m2 |

## FLOOR PLAN ABBREVIATIONS & LEGEND

| | |
|---|---|
| AC | AIRCONDITIONER CONDENSOR |
| APPL | APPLIANCE CUPBD |
| BAL | BALUSTRADE |
| BB | BRICK BASE |
| BH | BULKHEAD OVER |
| BL | BLOCKWORK |
| BN | BENCH |
| BR | BROOM CUPBD |
| BS | BASIN |
| BTH | BATH |
| CB | CIRCUIT BOARD |
| CL | CLOTHESLINE |
| CS | CAVITY SLIDING DOOR |
| CT | COOKTOP |
| DP | DOWNPIPE |
| DW | DISHWASHER SPACE |
| ED | EXISTING DOOR |
| EG | EAVES GUTTER |
| EW | EXISTING WINDOW |
| FNC | FENCE |
| FR | REFRIGERATOR SPACE |
| FW | FLOOR WASTE |
| GB | GAS BOTTLES |
| GT | GATE |
| HC | HOSE COCK |
| HWS | HOT WATER SYSTEM |
| L | LINEN CUPBOARD (4 SHELVES) |
| LAT | LATTICE PANEL |
| LC | LINEN CHUTE |
| MB | METER BOX |
| MH | MANHOLE 800 X 800 |
| ORG | OVERFLOW RELIEF GULLY |
| P | PANTRY |
| PJ | PLUMBING JUNCTION POINT |
| R | WARDROBE |
| S | SINK |
| SCR | SCREEN |
| SD | SMOKE DETECTOR (INTERCONNECTED) |
| SH | SHELVES |
| SHR | SHOWER |
| SK | SKYLIGHT |
| SOB | SHOWER OVER BATH |
| SP | STEEL POST |
| SRD | SLIDING ROBE DOORS |
| SS | SERVICES SHAFT |
| T | LAUNDRY TUB |
| TP | TIMBER POST |
| TS | TOILET SUITE |
| UBO | UNDER BENCH OVEN |
| VB | VANITY BASIN |
| WM | WASHING MACHINE SPACE |
| WMT | WATER MAINS TAP |
| WO | WALL OVEN |
| WR | WINE RACK |
| WT | WATER TANK |

## VILLA 69 INTERNAL AREAS

EXCL. EAVES

| | |
|---|---|
| VILLA | 131.2m2 |
| GARAGE | 42.1m2 |
| TERRACE | 3.4m2 |
| DRYING COURT | 5.4m2 |
| PORCH | 9.9m2 |
| ALFRESCO | 19.7m2 |
| TOTAL - V69 | 211.7m2 |

| ISSUE | DATE | DESCRIPTION |
|---|---|---|
| A | 01/09/25 | ISSUED FOR APPROVALS |
| B | 06/01/26 | VILLA 69 ENSUITE SHOWER SIZE |
| C | 02/03/26 | VILLA 68 150mm WIDER |

© COPYRIGHT NOTICE
Copyright of this drawing and design is held permanently by Carma Building Group Pty Ltd. Unauthorised use of this drawing and / or design, or any variation thereof, will trigger immediate legal proceedings.


carma building group
Suite 2 / 199 Gympie Tce, Noosaville Q 45(
T 07 5447 1250 F 07 5470 2586
E admin@carmabuildinggroup.com.au

PROJECT
VILLAS 68 & 69
LAGUNA ESTATE
13 LAKE WEYBA DRIVE
NOOSAVILLE

CLIENT
LAGUNA RETIREMENT ESTATE

DRAWING TITLE
FLOOR PLAN

| | |
|---|---|
| SCALE | @ ORIGINAL SIZ |
| 1:100 | A3 |
| DATE | DRAW |
| AUGUST 2025 | MW |
| DRAWING STATUS | |
| FOR CONSTRUCTION | |
| DRAWING NO. | ISSU |
| LRV068 WD-03 | C |

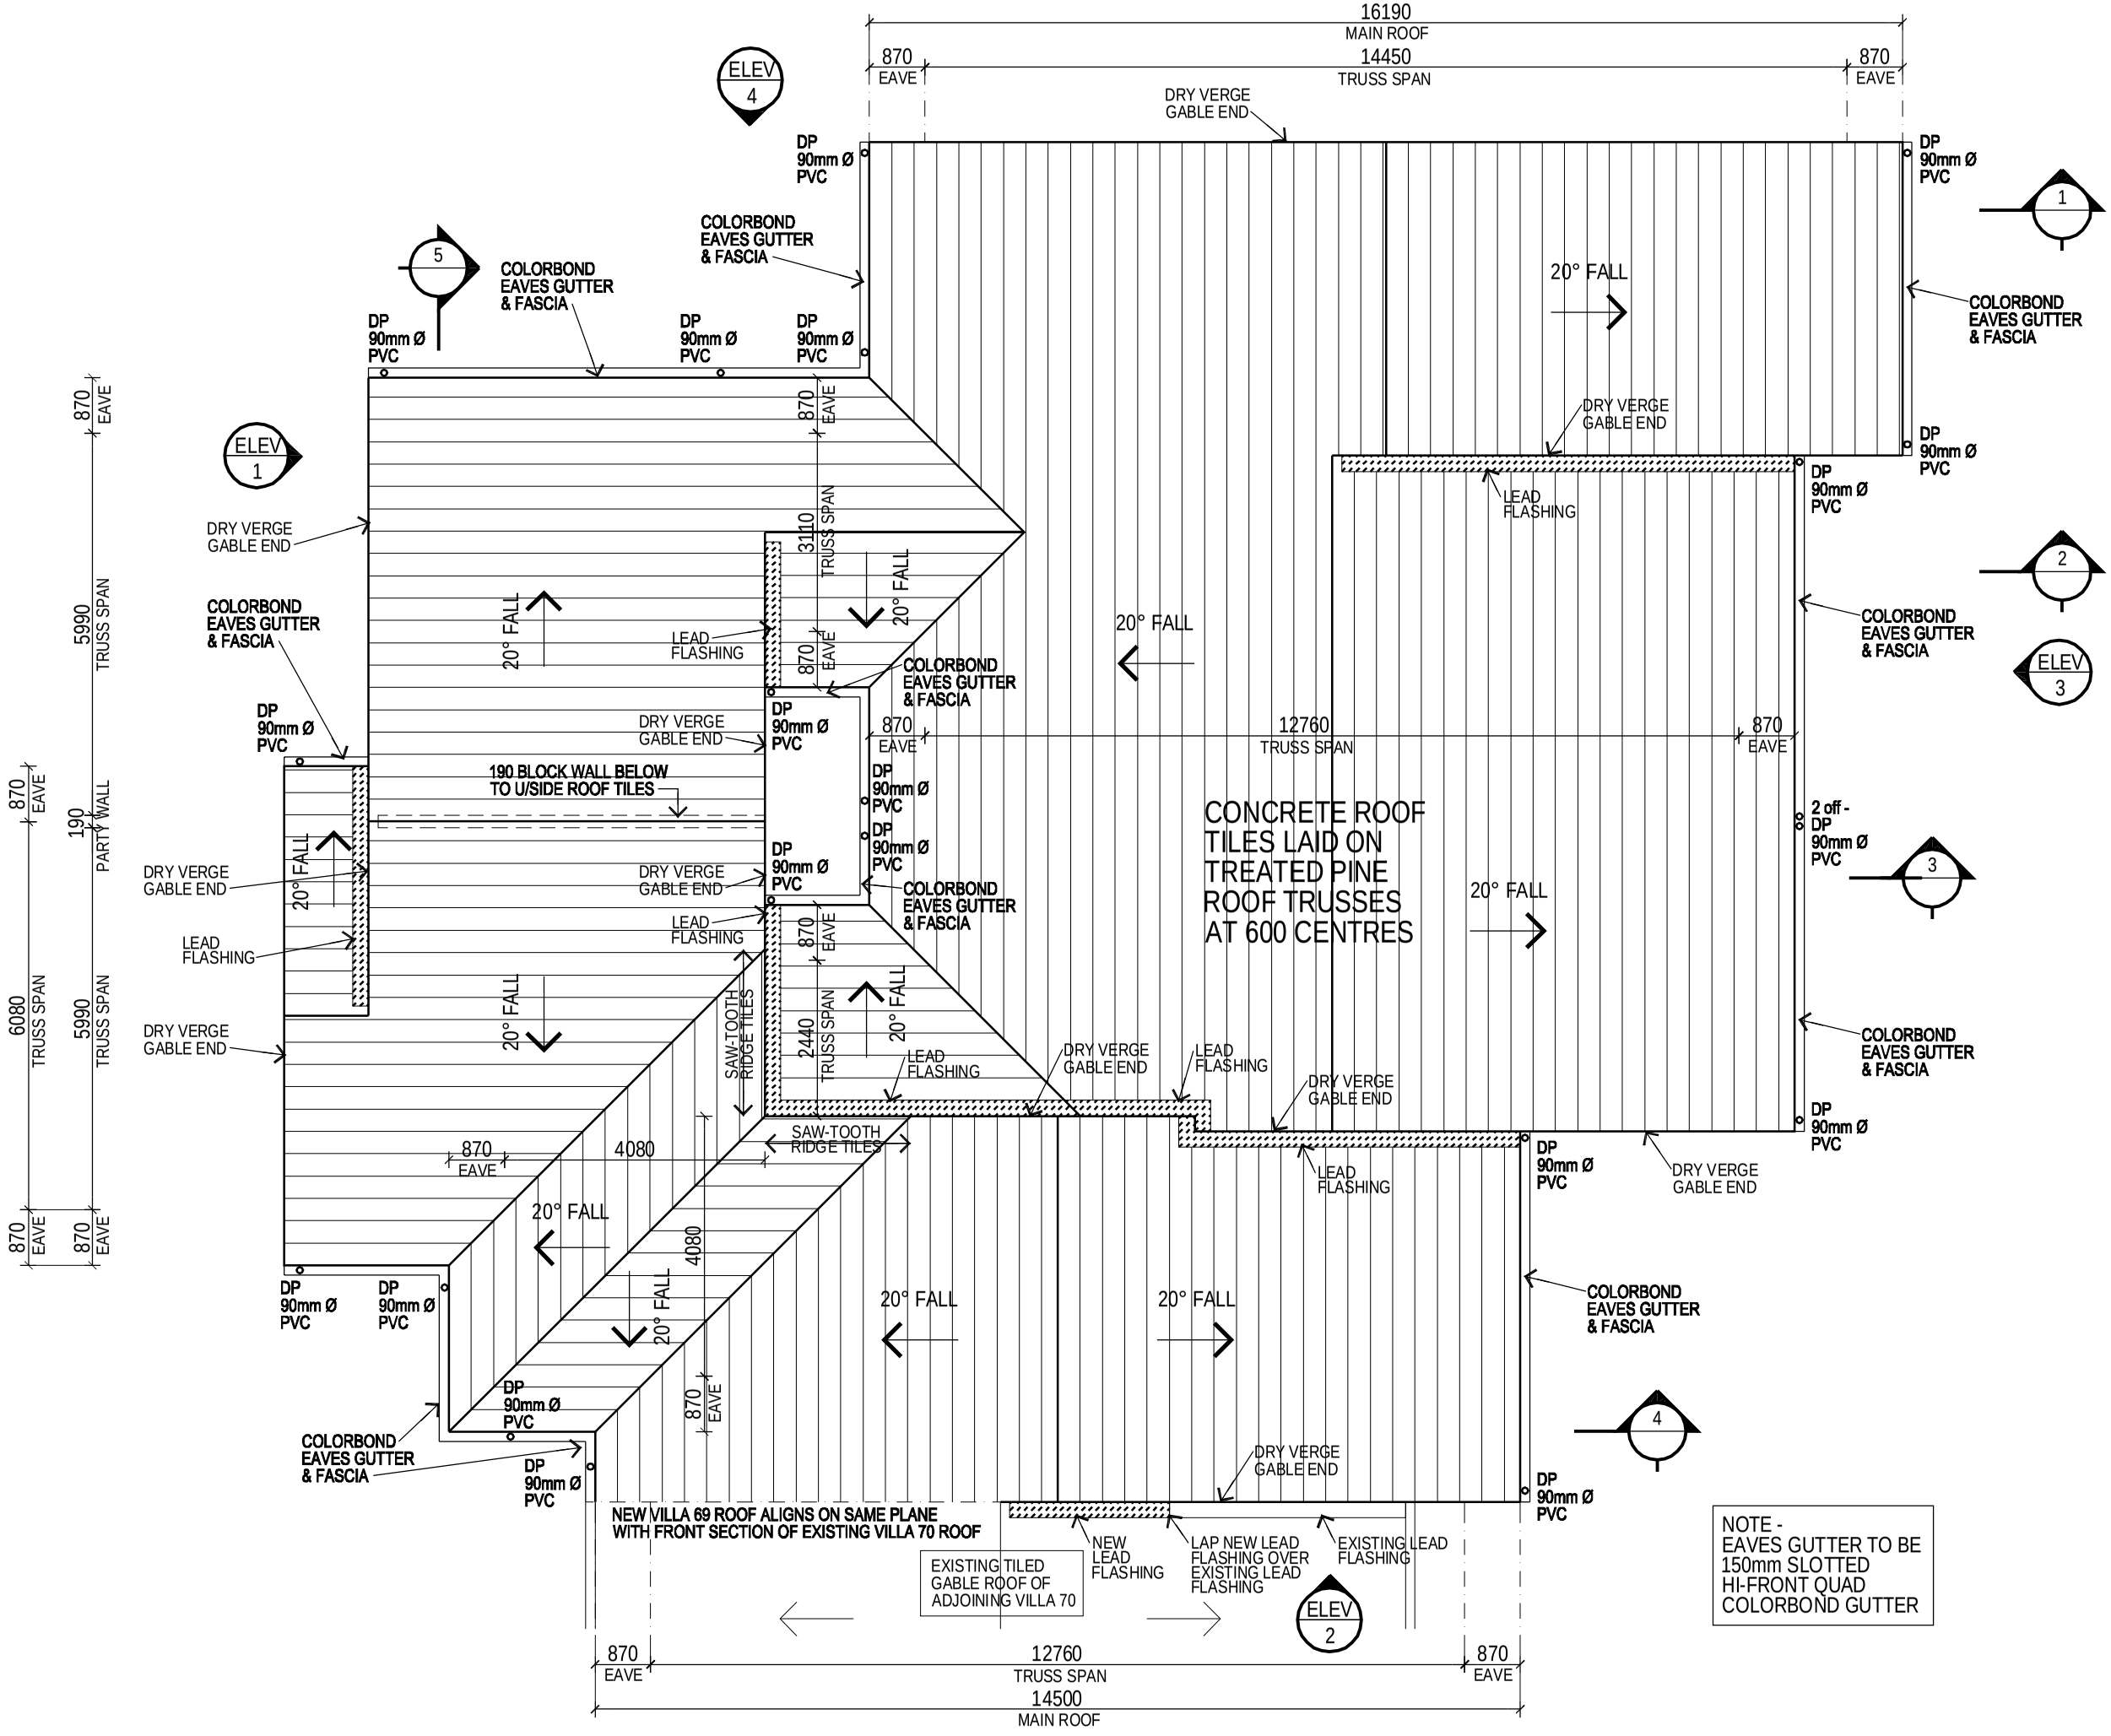


| ISSUE | DATE | DESCRIPTION |
|---|---|---|
| A | 01/09/25 | ISSUED FOR APPROVALS |

© COPYRIGHT NOTICE
Copyright of this drawing and design is held permanently by Carma Building Group Pty Ltd. Unauthorised use of this drawing and / or design, or any variation thereof, will trigger immediate legal proceedings.

carma
building group
Suite 2 / 199 Gympie Tce, Noosaville Q 45
T 07 5447 1250 F 07 5470 2586
E admin@carmabuildinggroup.com.au

PROJECT
VILLAS 68 & 69
LAGUNA ESTATE
13 LAKE WEYBA DRIVE
NOOSAVILLE


CLIENT
LAGUNA RETIREMENT ESTATE

DRAWING TITLE
ROOF PLAN

| SCALE | @ ORIGINAL SIZ |
|---|---|
| 1:100 | A3 |
| DATE | DRAW |
| AUGUST 2025 | MW |

DRAWING STATUS
FOR CONSTRUCTION

| DRAWING NO. | ISSU |
|---|---|
| LRV068 WD-04 | A |

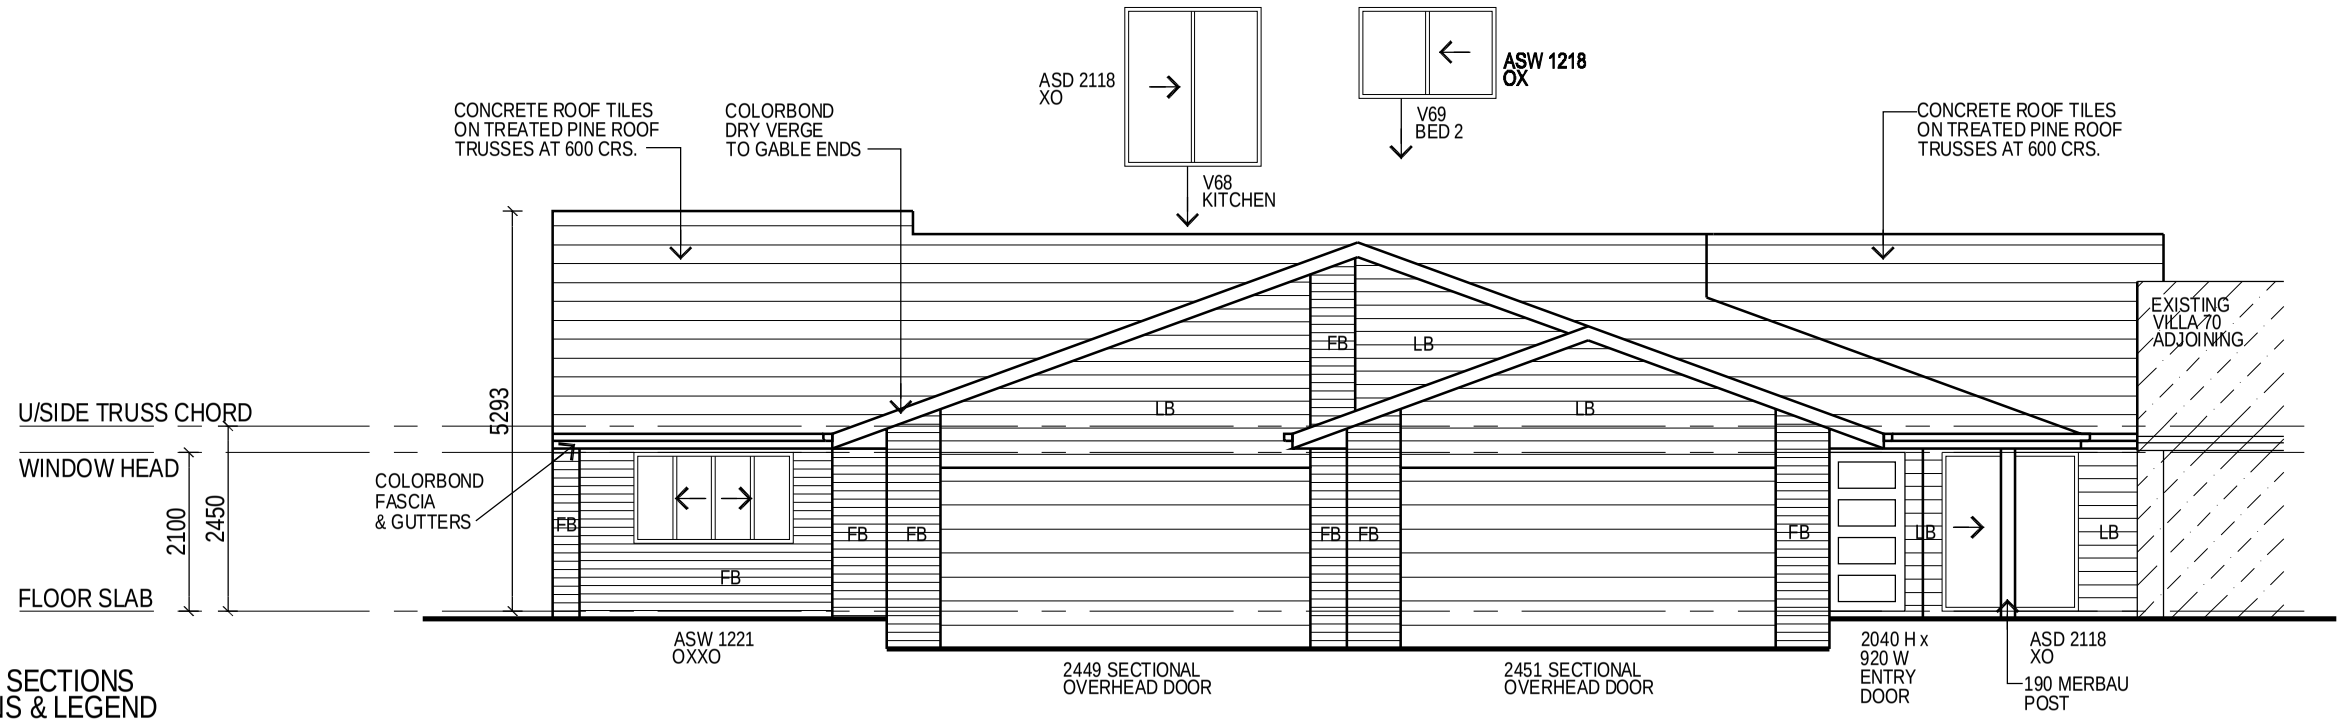


- ELEVATION 1

VILLAS 68 & 69 1:100


## ELEVATIONS & SECTIONS ABBREVIATIONS & LEGEND

### GENERAL ABBREVIATIONS

| | |
|---|---|
| AC | AXON CLADDING |
| AWN | AWNING (PROJECTION NOTED) |
| BAL | BALUSTRADE |
| CH | CEILING HEIGHT |
| FB | FACE BRICKWORK |
| FFL | FINISHED FLOOR LEVEL |
| FGL | FINISHED GROUND LEVEL |
| FNC | FENCE |
| LB | LINEABOARD CLADDING |
| NGL | NATURAL GROUND LINE |
| OH | OVERHANG |
| RB | RENDERED BLUEBOARD |
| RM | RENDERED MASONRY |
| SC | SHADOWCLAD CLADDING |
| SIF | STONE INLAY FEATURE |
| TOW | TOP OF WALL |
| WH | WINDOW HEAD |
| WL | WALL LIGHT |

### WINDOW ABBREVIATIONS

| | |
|---|---|
| AAW | ALUM. FRAMED AWNING WINDOW |
| ABD | ALUM. FRAMED BIFOLD STACKER DOOR |
| ABW | ALUM. FRAMED BIFOLD STACKER WINDOW |
| ACD | ALUM. FRAMED CASEMENT DOOR |
| ACW | ALUM. FRAMED CASEMENT WINDOW |
| ADH | ALUM. FRAMED DOUBLE HUNG WINDOW |
| AFD | ALUM. FRAMED FRENCH DOORS |
| AFG | ALUM. FRAMED FIXED GLAZING |
| ALV | ALUM. FRAMED LOUVRE WINDOW |
| ASD | ALUM. FRAMED SLIDING DOOR |
| ASH | ALUM.FRAMED SINGLE HUNG WINDOW |
| ASW | ALUM. FRAMED SLIDING WINDOW |
| CL | CLEAR GLAZING |
| OBS | OBSCURE GLAZING |
| SB | SOLAR BLOCK GLAZING |
| T | TINTED GLAZING |

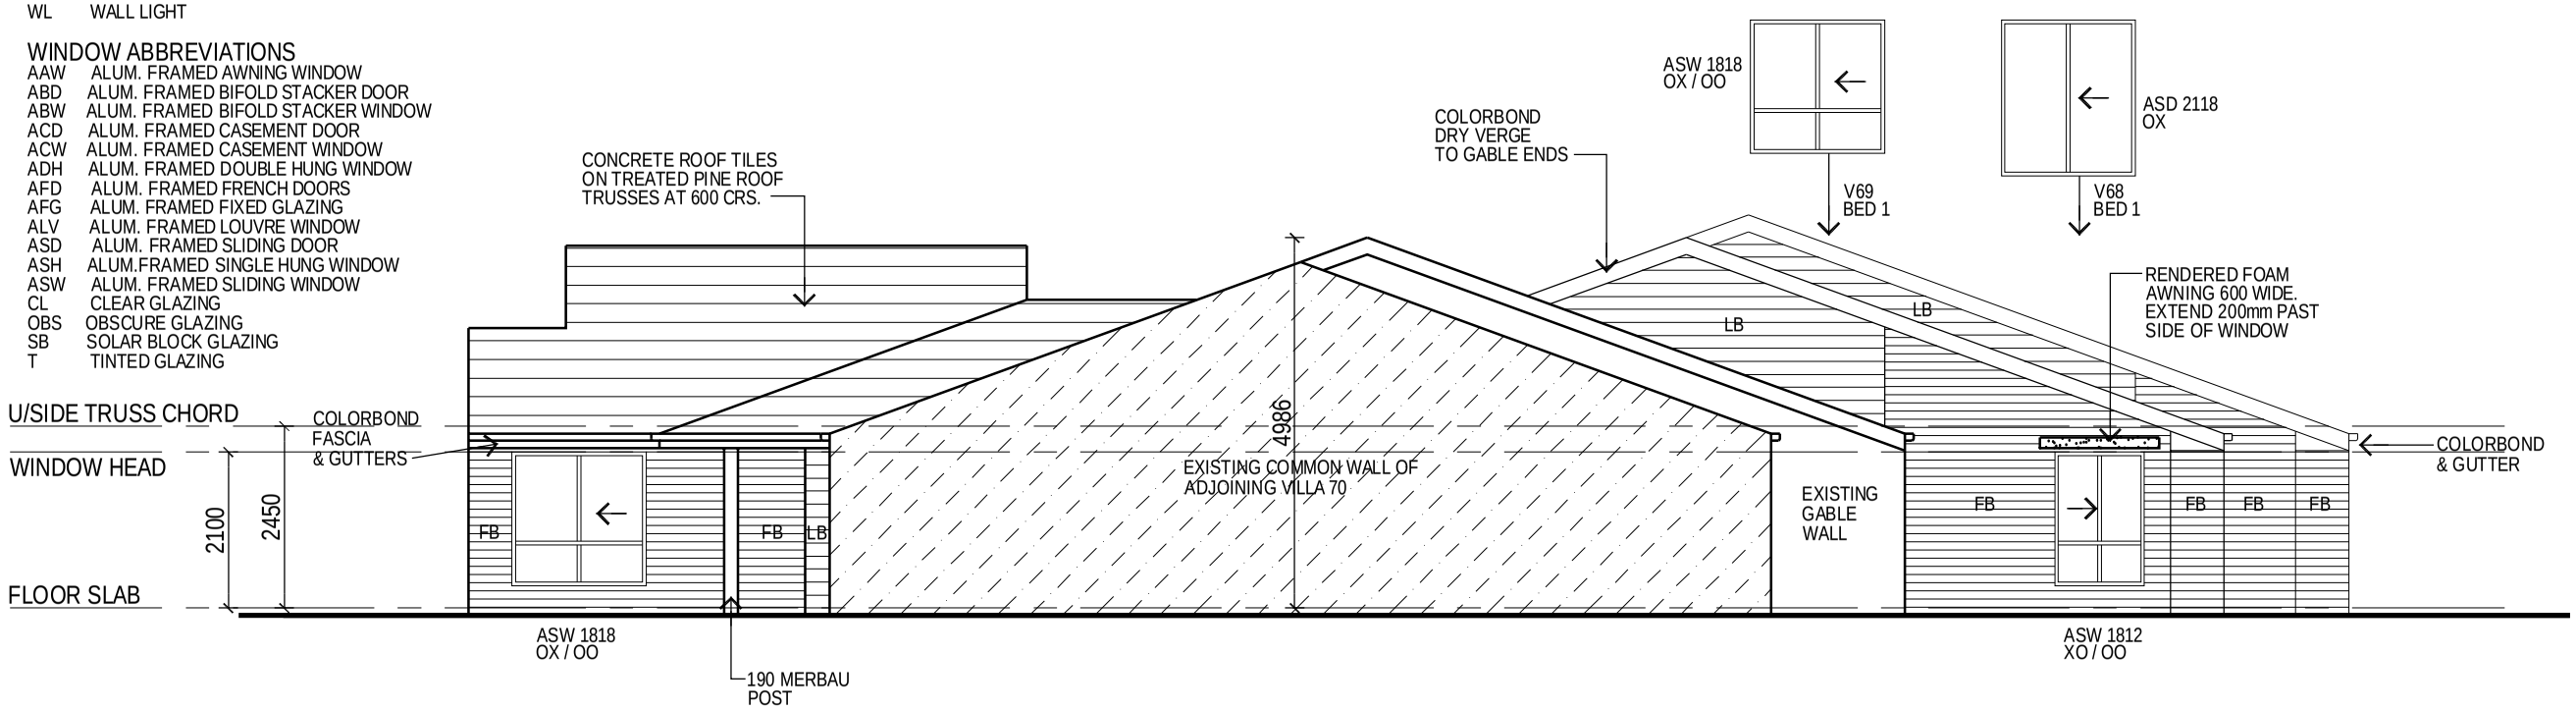


- ELEVATION 2

VILLAS 68 & 69 1:100

| ISSUE | DATE | DESCRIPTION |
|---|---|---|
| A | 01/09/25 | ISSUED FOR APPROVALS |

© COPYRIGHT NOTICE
Copyright of this drawing and design is held permanently by Carma Building Group Pty Ltd. Unauthorised use of this drawing and / or design, or any variation thereof, will trigger immediate legal proceedings.

carma building group
Suite 2 / 199 Gympie Tce, Noosaville Q 45(
T 07 5447 1250 F 07 5470 2586
E admin@carmabuildinggroup.com.au

PROJECT
VILLAS 68 & 69
LAGUNA ESTATE
13 LAKE WEYBA DRIVE
NOOSAVILLE


CLIENT
LAGUNA RETIREMENT ESTATE

DRAWING TITLE
ELEVATIONS
Sheet 1 of 2

| SCALE | @ ORIGINAL SIZ |
|---|---|
| 1:100 | A3 |
| DATE | DRAW |
| AUGUST 2025 | MW |

DRAWING STATUS
FOR CONSTRUCTION

| DRAWING NO. | ISSU |
|---|---|
| LRV068 WD-06 | A |

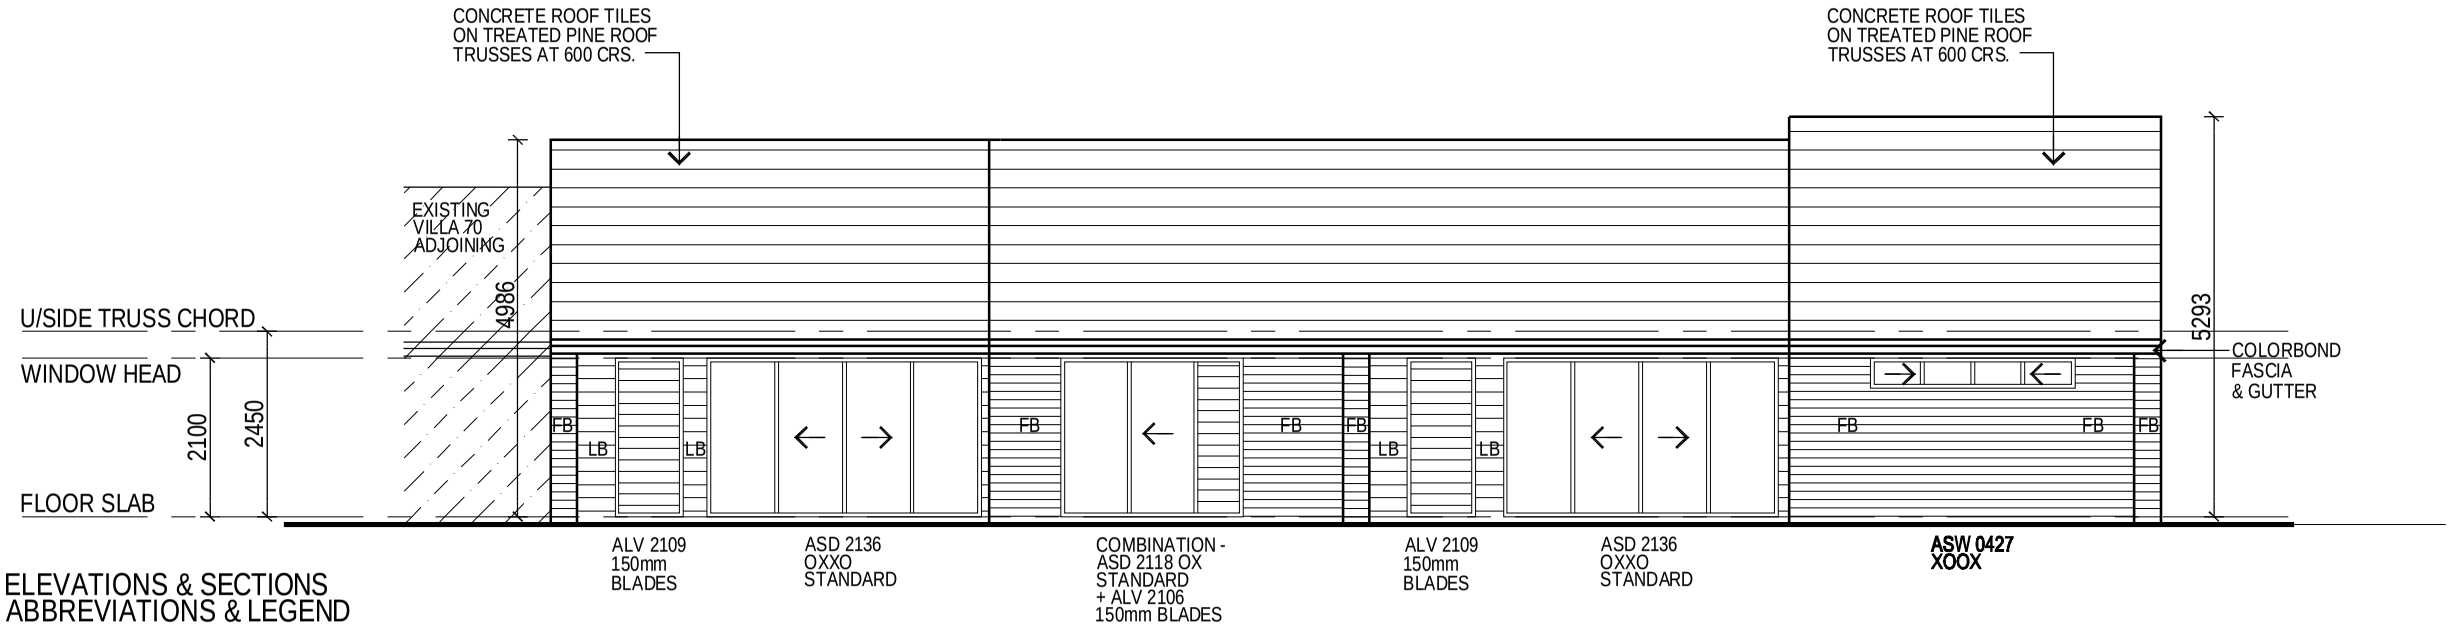


- ELEVATION 3

VILLAS 68 & 69 1:100


## ELEVATIONS & SECTIONS ABBREVIATIONS & LEGEND

### GENERAL ABBREVIATIONS

| | |
|---|---|
| AC | AXON CLADDING |
| AWN | AWNING (PROJECTION NOTED) |
| BAL | BALUSTRADE |
| CH | CEILING HEIGHT |
| FB | FACE BRICKWORK |
| FFL | FINISHED FLOOR LEVEL |
| FGL | FINISHED GROUND LEVEL |
| FNC | FENCE |
| LB | LINEABOARD CLADDING |
| NGL | NATURAL GROUND LINE |
| OH | OVERHANG |
| RB | RENDERED BLUEBOARD |
| RM | RENDERED MASONRY |
| SC | SHADOWCLAD CLADDING |
| SIF | STONE INLAY FEATURE |
| TOW | TOP OF WALL |
| WH | WINDOW HEAD |
| WL | WALL LIGHT |

### WINDOW ABBREVIATIONS

| | |
|---|---|
| AAW | ALUM. FRAMED AWNING WINDOW |
| ABD | ALUM. FRAMED BIFOLD STACKER DOOR |
| ABW | ALUM. FRAMED BIFOLD STACKER WINDOW |
| ACD | ALUM. FRAMED CASEMENT DOOR |
| ACW | ALUM. FRAMED CASEMENT WINDOW |
| ADH | ALUM. FRAMED DOUBLE HUNG WINDOW |
| AFD | ALUM. FRAMED FRENCH DOORS |
| AFG | ALUM. FRAMED FIXED GLAZING |
| ALV | ALUM. FRAMED LOUVRE WINDOW |
| ASD | ALUM. FRAMED SLIDING DOOR |
| ASH | ALUM.FRAMED SINGLE HUNG WINDOW |
| ASW | ALUM. FRAMED SLIDING WINDOW |
| CL | CLEAR GLAZING |
| OBS | OBSCURE GLAZING |
| SB | SOLAR BLOCK GLAZING |
| T | TINTED GLAZING |

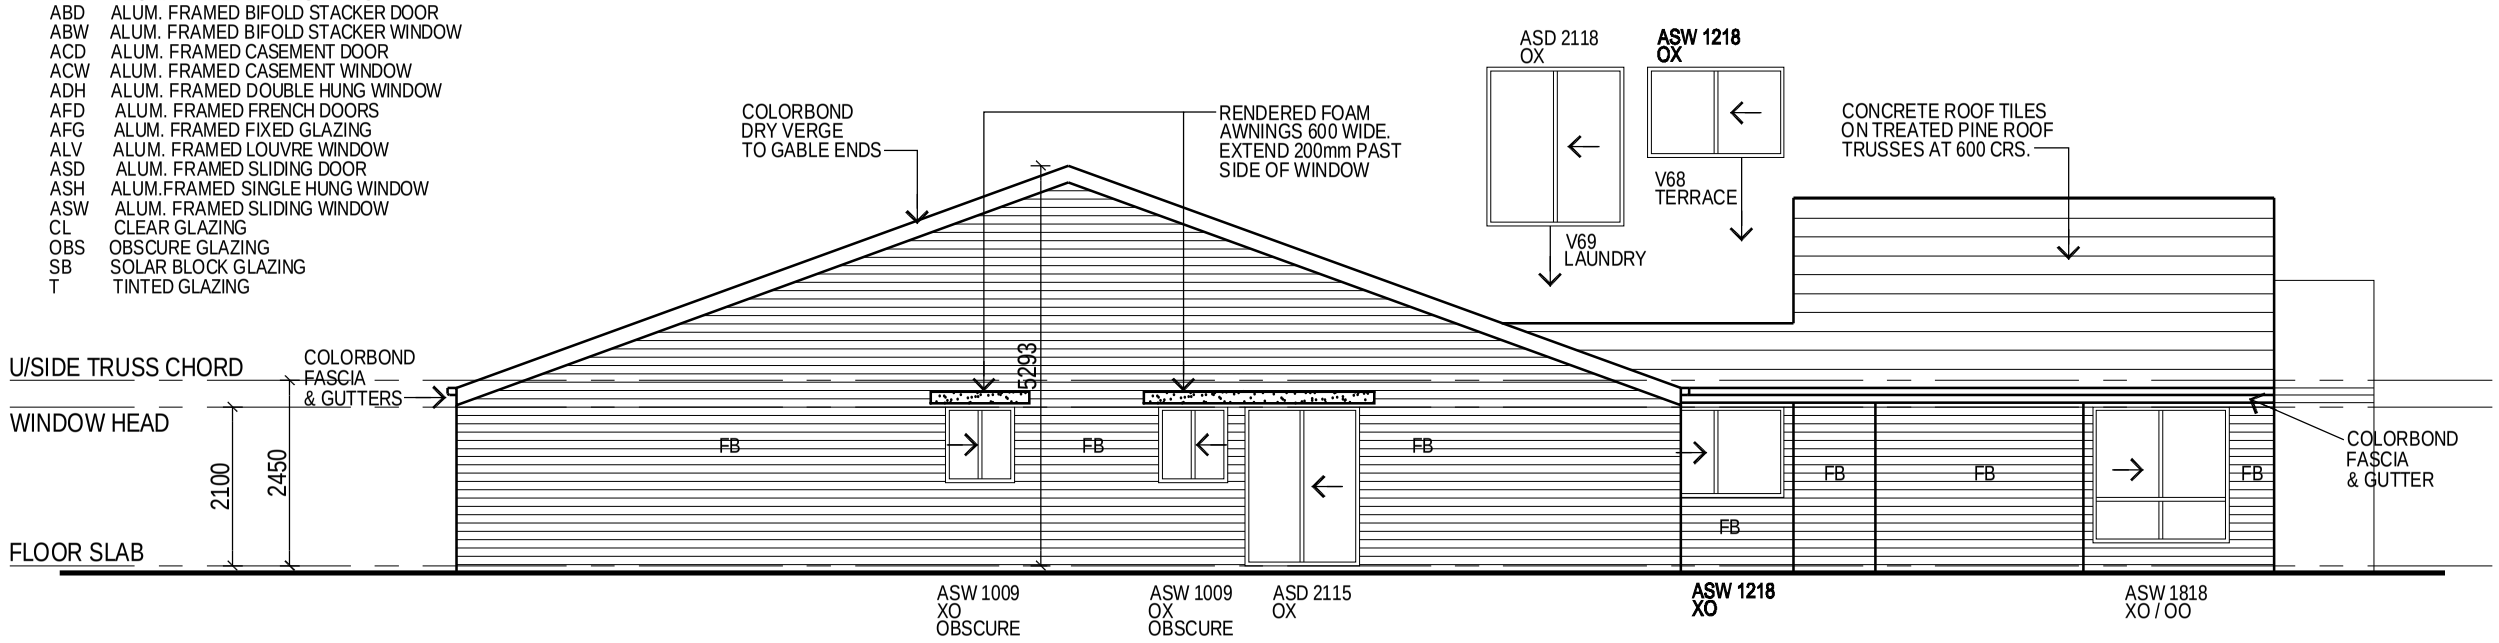


- ELEVATION 4

VILLAS 68 & 69 1:100

| ISSUE | DATE | DESCRIPTION |
|---|---|---|
| A | 01/09/25 | ISSUED FOR APPROVALS |

© COPYRIGHT NOTICE
Copyright of this drawing and design is held permanently by Carma Building Group Pty Ltd. Unauthorised use of this drawing and / or design, or any variation thereof, will trigger immediate legal proceedings.

carma building group
Suite 2 / 199 Gympie Tce, Noosaville Q 45(
T 07 5447 1250 F 07 5470 2586
E admin@carmabuildinggroup.com.au

PROJECT
VILLAS 68 & 69
LAGUNA ESTATE
13 LAKE WEYBA DRIVE
NOOSAVILLE

CLIENT
LAGUNA RETIREMENT ESTATE

DRAWING TITLE
ELEVATIONS
Sheet 2 of 2

| SCALE | @ ORIGINAL SIZ |
|---|---|
| 1:100 | A3 |
| DATE | DRAW |
| AUGUST 2025 | MW |

DRAWING STATUS
FOR CONSTRUCTION

| DRAWING NO. | ISSU |
|---|---|
| LRV068 WD-07 | A |


# ELEVATIONS & SECTIONS
# ABBREVIATIONS & LEGEND

## GENERAL ABBREVIATIONS


| | |
|---|---|
| AC | AXON CLADDING |
| AWN | AWNING (PROJECTION NOTED) |
| BAL | BALUSTRADE |
| CH | CEILING HEIGHT |
| FB | FACE BRICKWORK |
| FFL | FINISHED FLOOR LEVEL |
| FGL | FINISHED GROUND LEVEL |
| FNC | FENCE |
| LB | LINEABOARD CLADDING |
| NGL | NATURAL GROUND LINE |
| OH | OVERHANG |
| RB | RENDERED BLUEBOARD |
| RM | RENDERED MASONRY |
| SC | SHADOWCLAD CLADDING |
| SIF | STONE INLAY FEATURE |
| TOW | TOP OF WALL |
| WH | WINDOW HEAD |
| WL | WALL LIGHT |

## WINDOW ABBREVIATIONS


| | |
|---|---|
| AAW | ALUM. FRAMED AWNING WINDOW |
| ABD | ALUM. FRAMED BIFOLD STACKER DOOR |
| ABW | ALUM. FRAMED BIFOLD STACKER WINDOW |
| ACD | ALUM. FRAMED CASEMENT DOOR |
| ACW | ALUM. FRAMED CASEMENT WINDOW |
| ADH | ALUM. FRAMED DOUBLE HUNG WINDOW |
| AFD | ALUM. FRAMED FRENCH DOORS |
| AFG | ALUM. FRAMED FIXED GLAZING |
| ALV | ALUM. FRAMED LOUVRE WINDOW |
| ASD | ALUM. FRAMED SLIDING DOOR |
| ASH | ALUM.FRAMED SINGLE HUNG WINDOW |
| ASW | ALUM. FRAMED SLIDING WINDOW |
| CL | CLEAR GLAZING |
| OBS | OBSCURE GLAZING |
| SB | SOLAR BLOCK GLAZING |
| T | TINTED GLAZING |

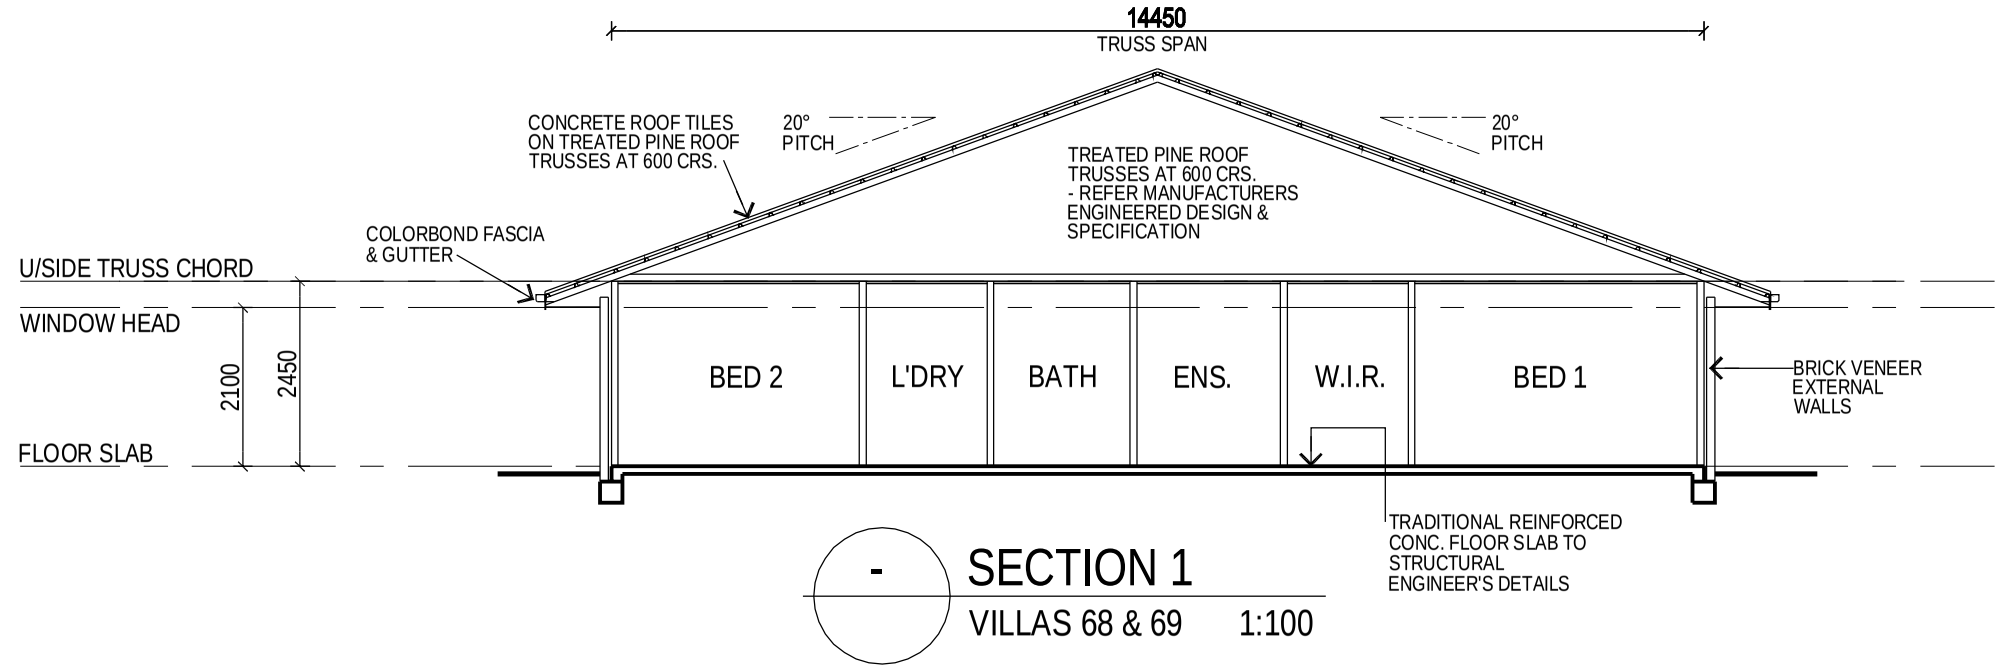


- SECTION 1
VILLAS 68 & 69 1:100

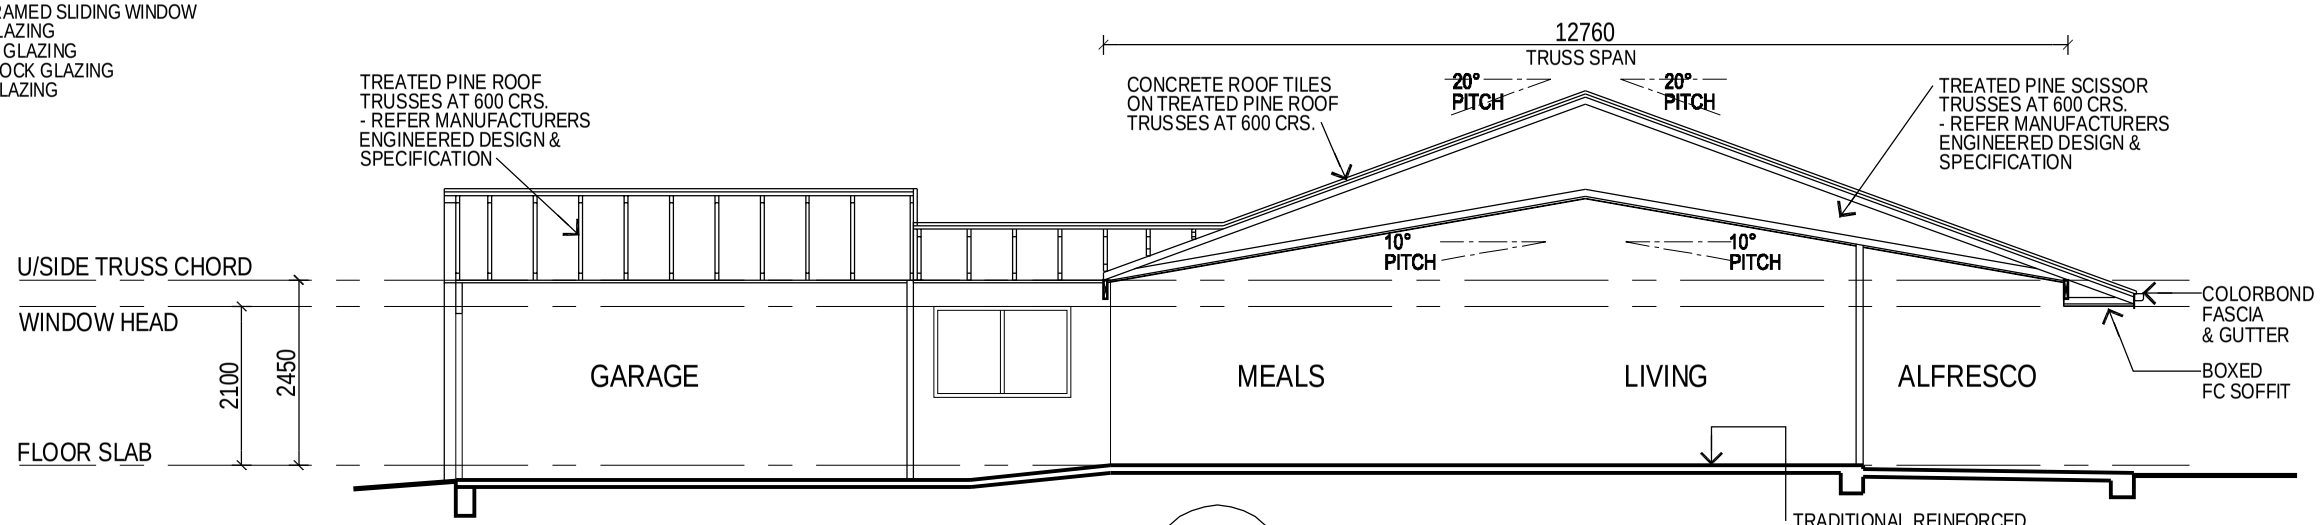


- SECTION 2
VILLAS 68 & 69 1:100

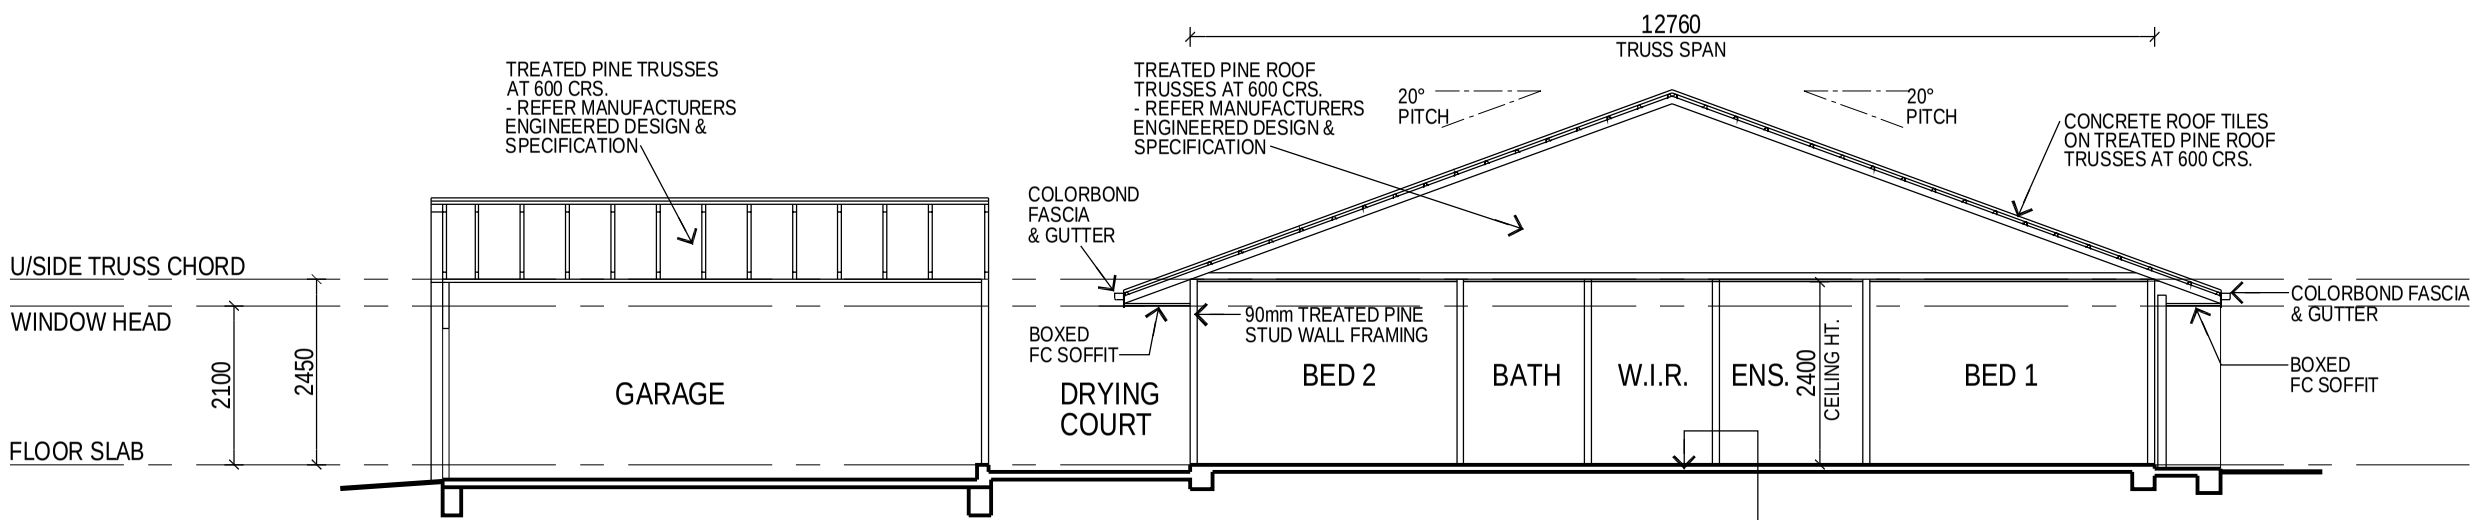


- SECTION 3
VILLAS 68 & 69 1:100

| ISSUE | DATE | DESCRIPTION |
|---|---|---|
| A | 01/09/25 | ISSUED FOR APPROVALS |

© COPYRIGHT NOTICE
Copyright of this drawing and design is held permanently by Carma Building Group Pty Ltd. Unauthorised use of this drawing and / or design, or any variation thereof, will trigger immediate legal proceedings.

carma building group
Suite 2 / 199 Gympie Tce, Noosaville Q 45
T 07 5447 1250 F 07 5470 2586
E admin@carmabuildinggroup.com.au

PROJECT
VILLAS 68 & 69
LAGUNA ESTATE
13 LAKE WEYBA DRIVE
NOOSAVILLE

CLIENT
LAGUNA RETIREMENT ESTATE

DRAWING TITLE
SECTIONS
Sheet 1 of 2

| SCALE | @ ORIGINAL SIZ |
|---|---|
| 1:100 | A3 |
| DATE | DRAW |
| AUGUST 2025 | MW |

DRAWING STATUS
FOR CONSTRUCTION

| DRAWING NO. | ISSU |
|---|---|
| LRV068 WD-08 | A |


## ELEVATIONS & SECTIONS ABBREVIATIONS & LEGEND

### GENERAL ABBREVIATIONS

| | |
|---|---|
| AC | AXON CLADDING |
| AWN | AWNING (PROJECTION NOTED) |
| BAL | BALUSTRADE |
| CH | CEILING HEIGHT |
| FB | FACE BRICKWORK |
| FFL | FINISHED FLOOR LEVEL |
| FGL | FINISHED GROUND LEVEL |
| FNC | FENCE |
| LB | LINEABOARD CLADDING |
| NGL | NATURAL GROUND LINE |
| OH | OVERHANG |
| RB | RENDERED BLUEBOARD |
| RM | RENDERED MASONRY |
| SC | SHADOWCLAD CLADDING |
| SIF | STONE INLAY FEATURE |
| TOW | TOP OF WALL |
| WH | WINDOW HEAD |
| WL | WALL LIGHT |


### WINDOW ABBREVIATIONS

| | |
|---|---|
| AAW | ALUM. FRAMED AWNING WINDOW |
| ABD | ALUM. FRAMED BIFOLD STACKER DOOR |
| ABW | ALUM. FRAMED BIFOLD STACKER WINDOW |
| ACD | ALUM. FRAMED CASEMENT DOOR |
| ACW | ALUM. FRAMED CASEMENT WINDOW |
| ADH | ALUM. FRAMED DOUBLE HUNG WINDOW |
| AFD | ALUM. FRAMED FRENCH DOORS |
| AFG | ALUM. FRAMED FIXED GLAZING |
| ALV | ALUM. FRAMED LOUVRE WINDOW |
| ASD | ALUM. FRAMED SLIDING DOOR |
| ASH | ALUM.FRAMED SINGLE HUNG WINDOW |
| ASW | ALUM. FRAMED SLIDING WINDOW |
| CL | CLEAR GLAZING |
| OBS | OBSCURE GLAZING |
| SB | SOLAR BLOCK GLAZING |
| T | TINTED GLAZING |

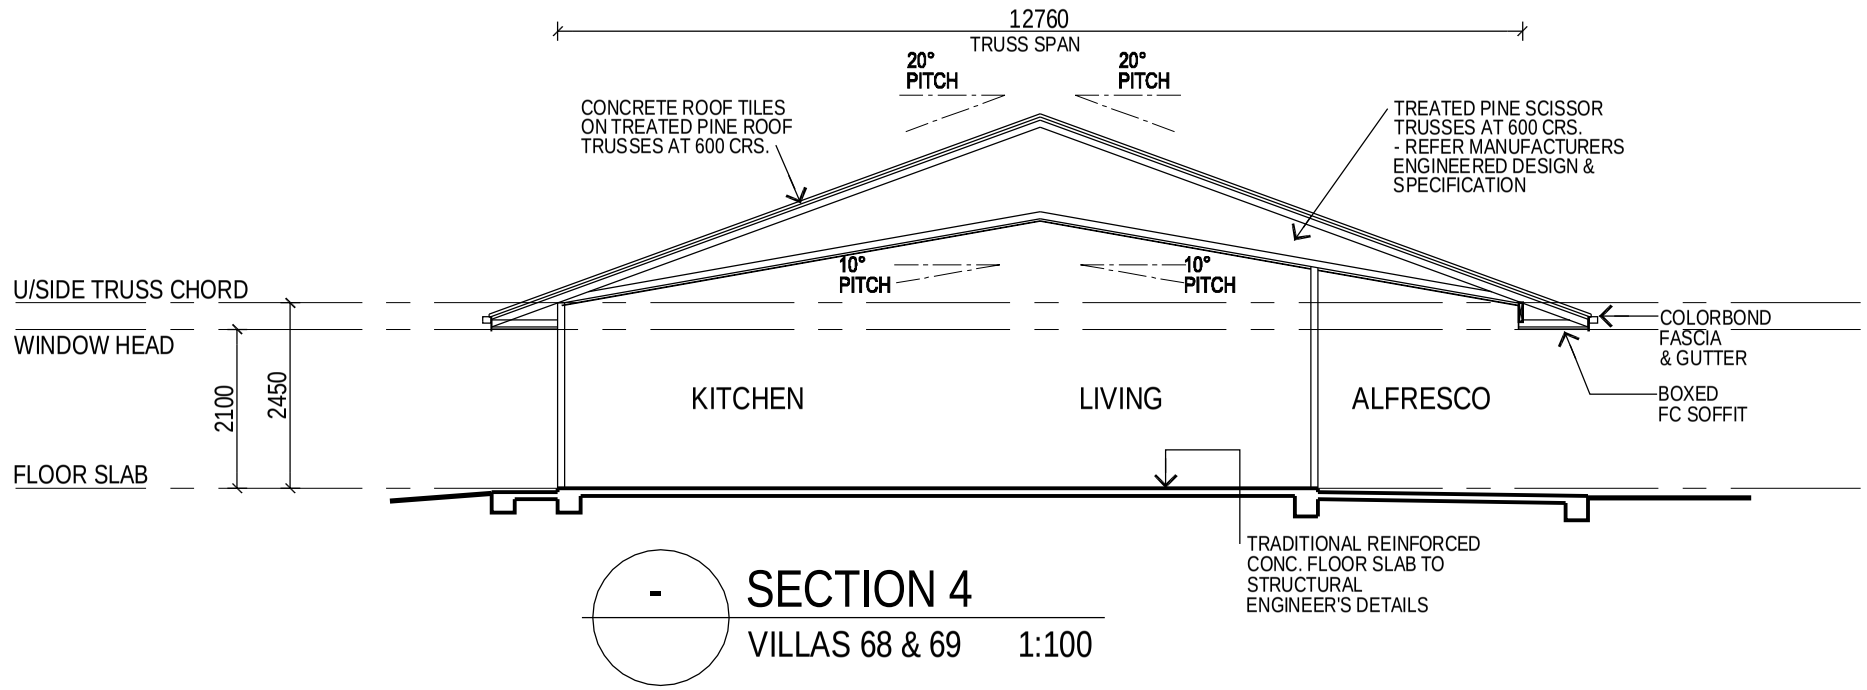


- SECTION 4

VILLAS 68 & 69 1:100

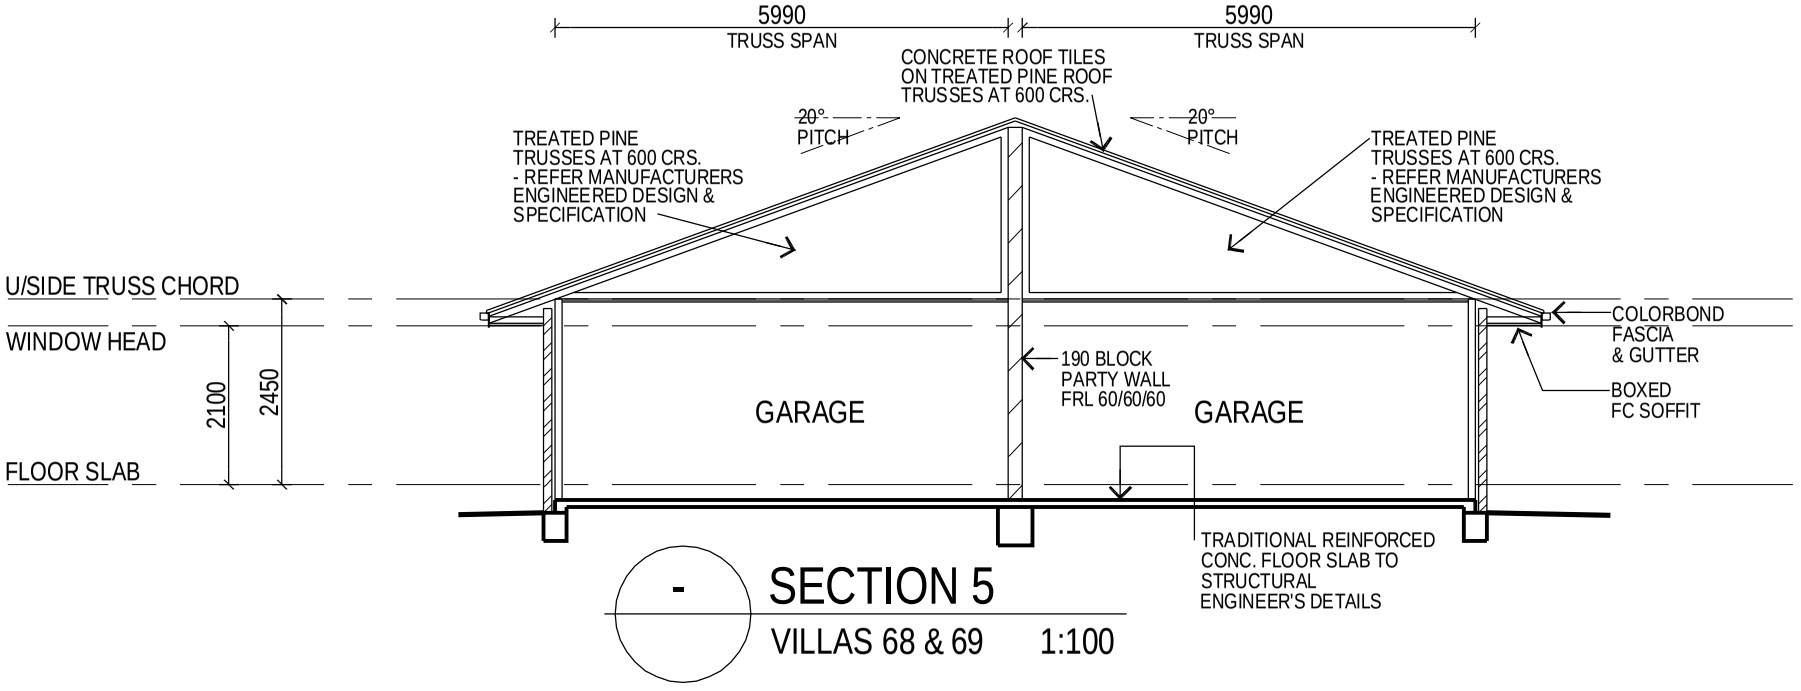


- SECTION 5

VILLAS 68 & 69 1:100

| ISSUE | DATE | DESCRIPTION |
|---|---|---|
| A | 01/09/25 | ISSUED FOR APPROVALS |


© COPYRIGHT NOTICE
Copyright of this drawing and design is held permanently by Carma Building Group Pty Ltd. Unauthorised use of this drawing and / or design, or any variation thereof, will trigger immediate legal proceedings.



carma building group
Suite 2 / 199 Gympie Tce, Noosaville Q 45
T 07 5447 1250 F 07 5470 2586
E admin@carmabuildinggroup.com.au


PROJECT
VILLAS 68 & 69
LAGUNA ESTATE
13 LAKE WEYBA DRIVE
NOOSAVILLE

CLIENT
LAGUNA RETIREMENT ESTATE

DRAWING TITLE
SECTIONS
Sheet 2 of 2


| SCALE | @ ORIGINAL SIZ |
|---|---|
| 1:100 | A3 |
| DATE | DRAW |
| AUGUST 2025 | MW |

DRAWING STATUS
FOR CONSTRUCTION


| DRAWING NO. | ISSU |
|---|---|
| LRV068 WD-09 | A |

## INTERIOR ELEVATIONS ABBREVIATIONS & LEGEND


| | |
|---|---|
| AP | APPLIANCE CUPBD. ROLLER SHUTTER |
| AR | ARCHITRAVE |
| BH | BULKHEAD |
| BN | BENCHTOP |
| BR | BROOM CUPBOARD |
| BSP | BATH SPOUT |
| BTH | BATH TUB |
| CD | CLOTHES DRYER |
| CO | CORNICE |
| CT | COOKTOP |
| DR | DRAWER |
| DV | DUCTED VACUUM INLET |
| DW | DISHWASHER |
| FR | FRIDGE RECESS |
| FT | FEATURE TILE |
| FW | FLOOR WASTE |
| GR | GRAB RAIL |
| GPO | GENERAL POWER OUTLET (DOUBLE) |
| KB | KICKBOARD |
| L | LINEN CUPBOARD |
| LAM | PLASTIC LAMINATE FINISH |
| MIR | MIRROR |
| MR | MICROWAVE RECESS |
| MXR | MIXER TAP |
| OH | OVERHEAD CUPBOARD |
| PB | PLASTERBOARD BULKHEAD |
| PL | PLASTERBOARD FINISH |
| PN | PANTRY |
| RBH | ROBE HOOK |
| RH | RANGEHOOD |
| SB | SHOWER BASKET |
| SCR | SHOWER SCREEN |
| SH | SHELF / SHELVES |
| SHR | SHOWER |
| SK | SKIRTING BOARD |
| SNK | SINK |
| SP | SPLASHBACK |
| SR | SHOWER ROSE |
| SRD | SLIDING ROBE DOORS |
| SSH | SHOWER SHELF |
| T | LAUNDRY TUB |
| TBS | TOILET BRUSH SET |
| TRG | TOWEL RING |
| TRH | TOILET ROLL HOLDER |
| TS | TOILET SUITE |
| TWL | TOWEL RAIL |
| VAN | VANITY BENCH |
| VB | VANITY BASIN |
| WM | WASHING MACHINE SPACE |
| WMT | WASHING MACHINE TAPS |
| WO | WALL OVEN |
| WR | WINE RACKS |
| WT | WALL TILES |

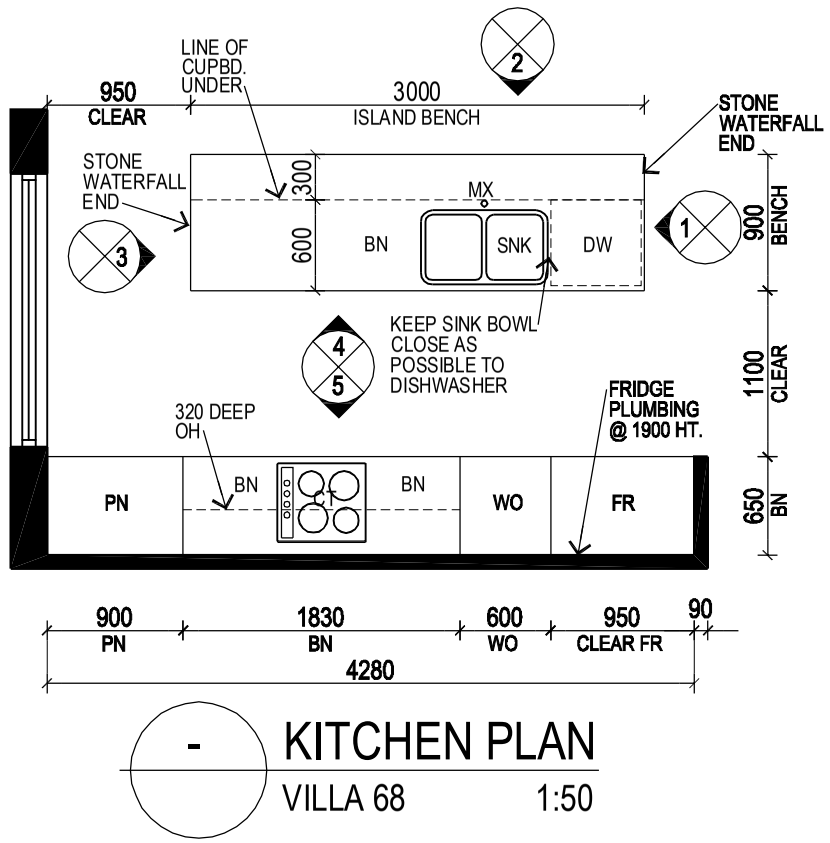



## - KITCHEN PLAN
VILLA 68 1:50

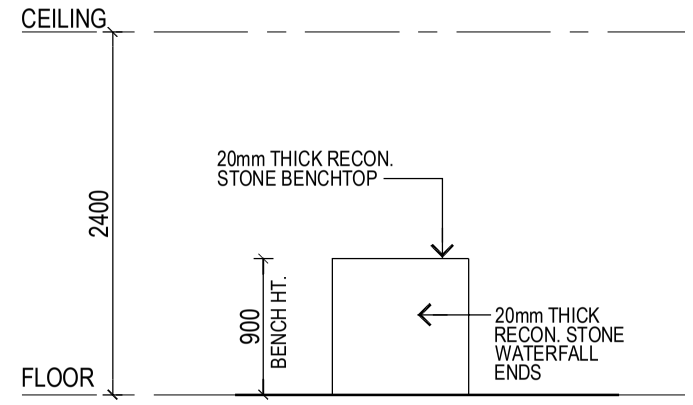



## - ELEVATION 1
KITCHEN - V68 1:50

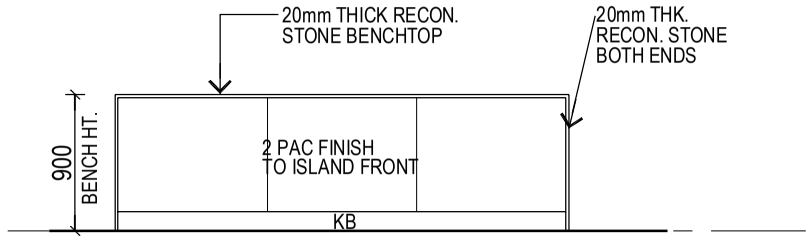



## - ELEVATION 2
KITCHEN - V68 1:50

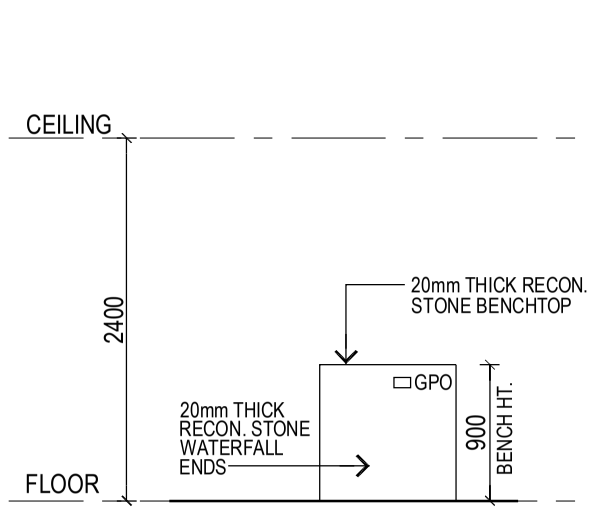


## - ELEVATION 3
KITCHEN - V68 1:50

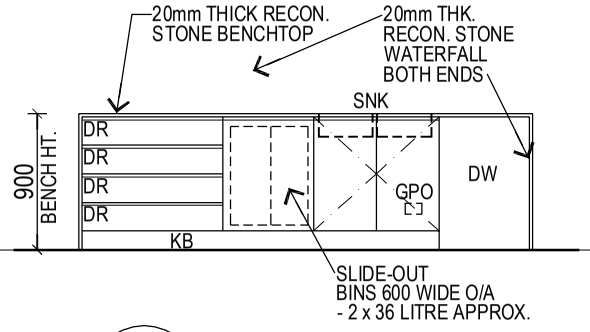


## - ELEVATION 4
KITCHEN - V68 1:50

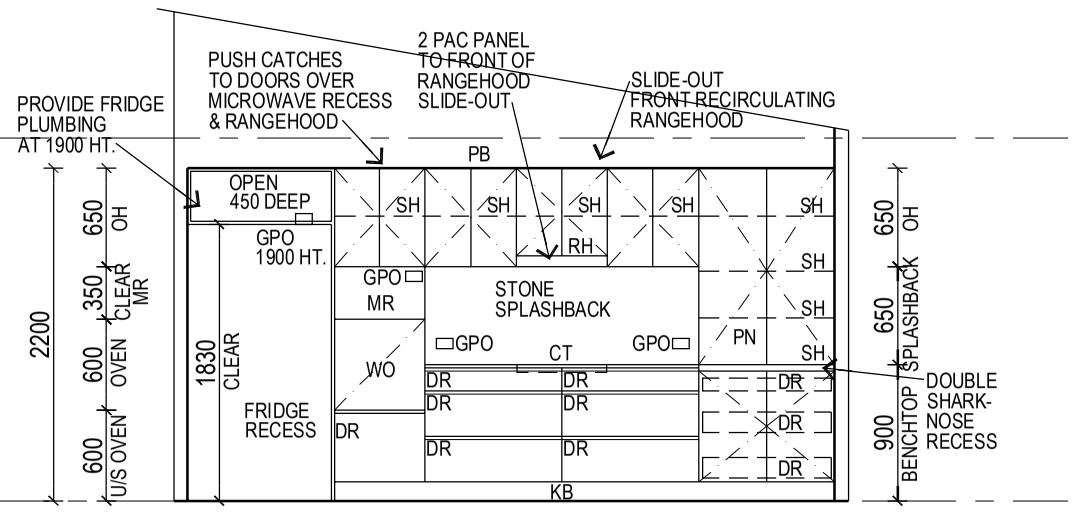


## - ELEVATION 5
KITCHEN - V68 1:50

| ISSUE | DATE | DESCRIPTION |
|---|---|---|
| A | 01/02/26 | ISSUED FOR CONSTRUCTION |


© COPYRIGHT NOTICE
Copyright of this drawing and design is held permanently by Carma Building Group Pty Ltd. Unauthorised use of this drawing and / or design, or any variation thereof, will trigger immediate legal proceedings.



carma building group
Suite 2 / 199 Gympie Tce, Noosaville Q 456
T 07 5447 1250 F 07 5470 2586
E admin@carmabuildinggroup.com.au


PROJECT
VILLAS 68 & 69
LAGUNA ESTATE
13 LAKE WEYBA DRIVE
NOOSAVILLE

CLIENT
LAGUNA RETIREMENT ESTATE

DRAWING TITLE
VILLA 68 - KITCHEN DETAILS

| SCALE | @ ORIGINAL SIZ |
|---|---|
| 1:50 | A3 |
| DATE | DRAW |
| SEPTEMBER 2025 | MW |


DRAWING STATUS
FOR CONSTRUCTION

| DRAWING NO. | ISSU |
|---|---|
| LRV068 WD-10 | A |


## INTERIOR ELEVATIONS ABBREVIATIONS & LEGEND

| | |
|---|---|
| AP | APPLIANCE CUPBD. ROLLER SHUTTER |
| AR | ARCHITRAVE |
| BH | BULKHEAD |
| BN | BENCHTOP |
| BR | BROOM CUPBOARD |
| BSP | BATH SPOUT |
| BTH | BATH TUB |
| CD | CLOTHES DRYER |
| CO | CORNICE |
| CT | COOKTOP |
| DR | DRAWER |
| DV | DUCTED VACUUM INLET |
| DW | DISHWASHER |
| FR | FRIDGE RECESS |
| FT | FEATURE TILE |
| FW | FLOOR WASTE |
| GR | GRAB RAIL |
| GPO | GENERAL POWER OUTLET (DOUBLE) |
| KB | KICKBOARD |
| L | LINEN CUPBOARD |
| LAM | PLASTIC LAMINATE FINISH |
| MIR | MIRROR |
| MR | MICROWAVE RECESS |
| MXR | MIXER TAP |
| OH | OVERHEAD CUPBOARD |
| PB | PLASTERBOARD BULKHEAD |
| PL | PLASTERBOARD FINISH |
| PN | PANTRY |
| RBH | ROBE HOOK |
| RH | RANGEHOOD |
| SB | SHOWER BASKET |
| SCR | SHOWER SCREEN |
| SH | SHELF / SHELVES |
| SHR | SHOWER |
| SK | SKIRTING BOARD |
| SNK | SINK |
| SP | SPLASHBACK |
| SR | SHOWER ROSE |
| SRD | SLIDING ROBE DOORS |
| SSH | SHOWER SHELF |
| T | LAUNDRY TUB |
| TBS | TOILET BRUSH SET |
| TRG | TOWEL RING |
| TRH | TOILET ROLL HOLDER |
| TS | TOILET SUITE |
| TWL | TOWEL RAIL |
| VAN | VANITY BENCH |
| VB | VANITY BASIN |
| WM | WASHING MACHINE SPACE |
| WMT | WASHING MACHINE TAPS |
| WO | WALL OVEN |
| WR | WINE RACKS |
| WT | WALL TILES |

## - LAUNDRY
VILLA 68 1:50

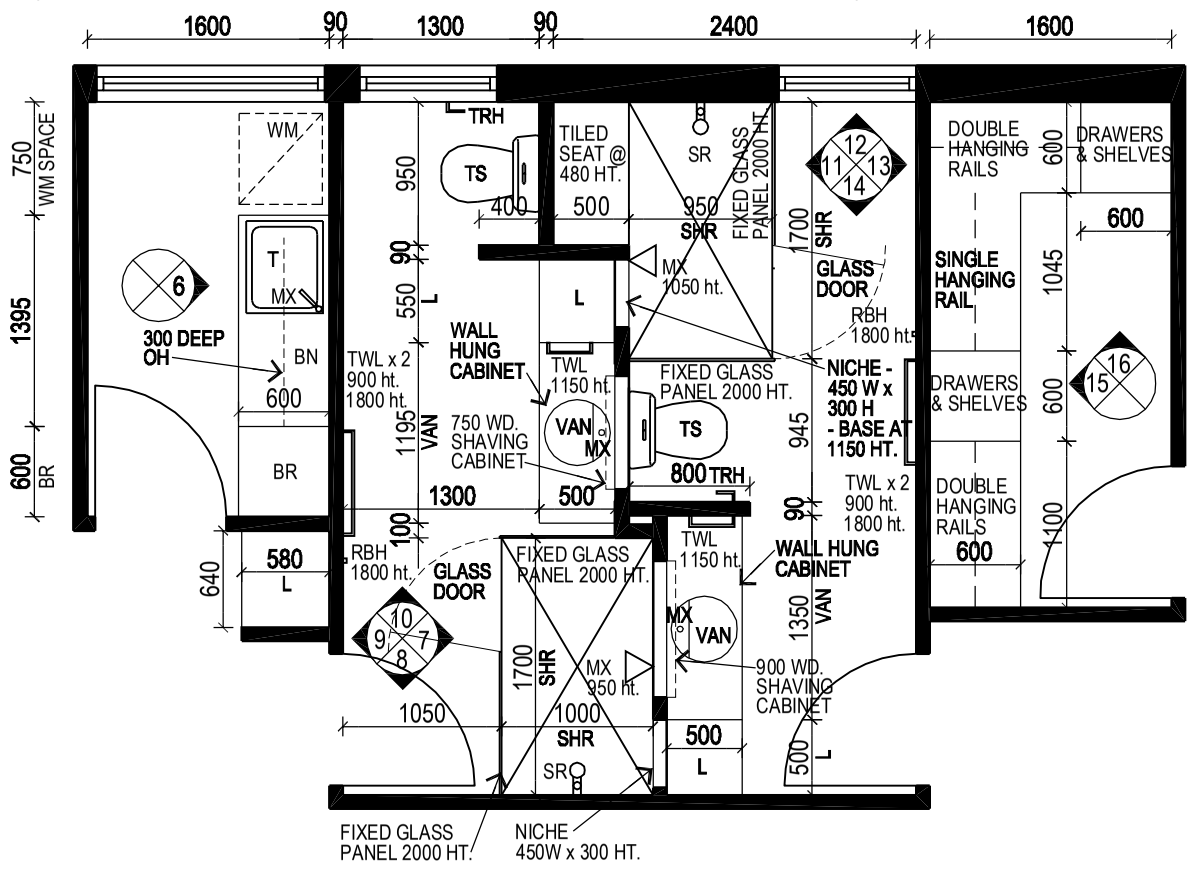



## - BED 1 W.I.ROBE
VILLA 68 1:50

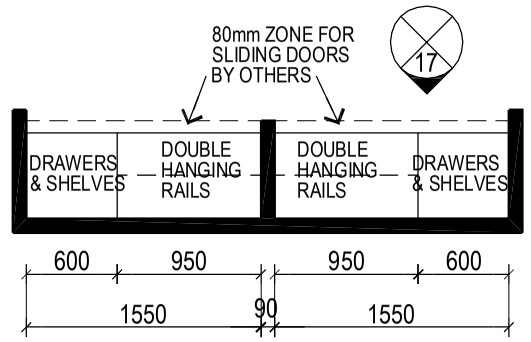



## - BED 2 ROBE
VILLA 68 1:50

## - BATHROOM
VILLA 68 1:50


## - ENSUITE
VILLA 68 1:50

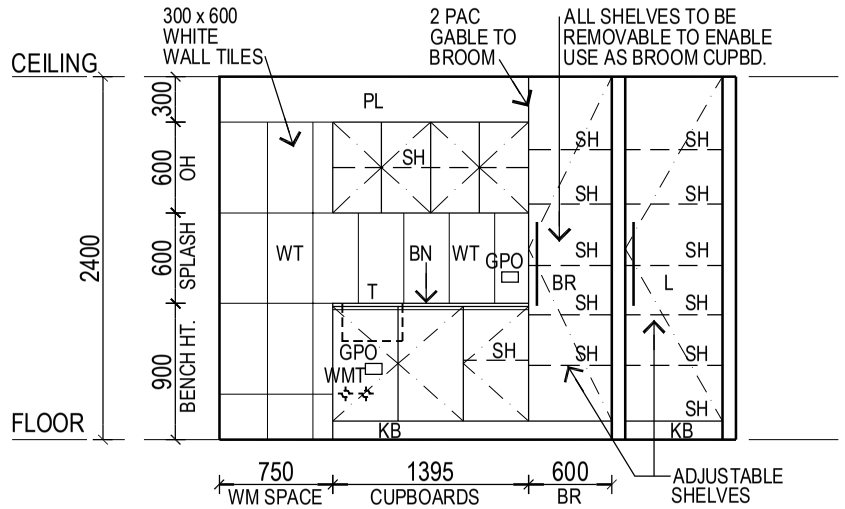



## - ELEVATION 6
LAUNDRY - V68 1:50

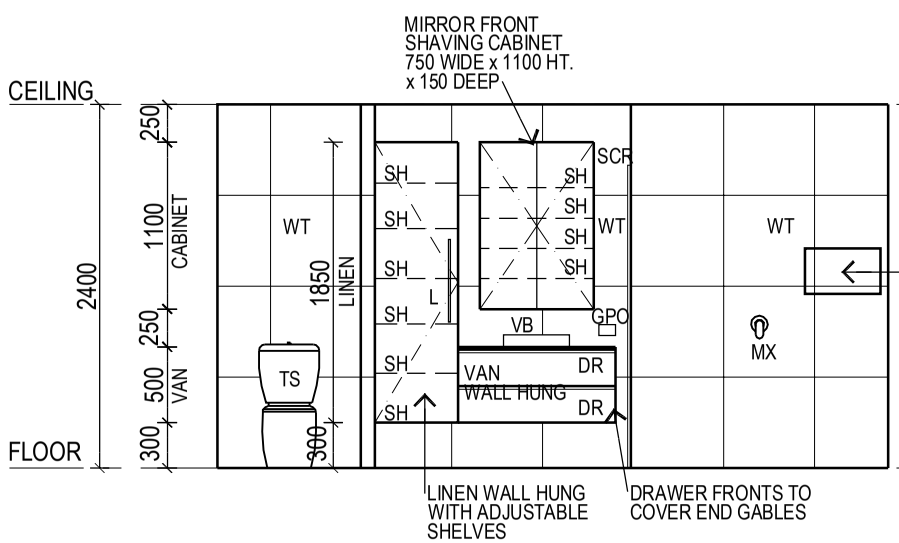



## - ELEVATION 7
BATHROOM - V68 1:50

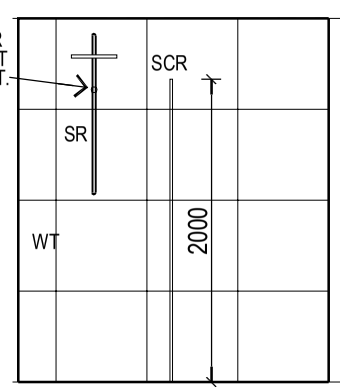


## - ELEVATION 8
BATHROOM - V68 1:50

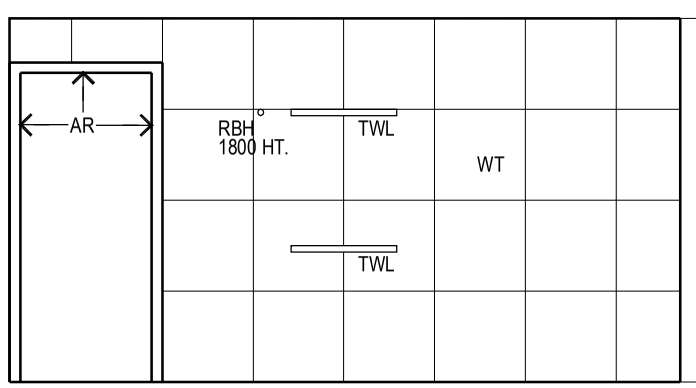


## - ELEVATION 9
BATHROOM - V68 1:50

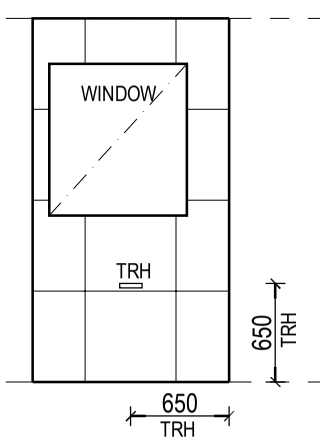


## - ELEVATION 10
BATHROOM - V68 1:50

| ISSUE | DATE | DESCRIPTION |
|---|---|---|
| A | 01/02/26 | ISSUED FOR CONSTRUCTION |


© COPYRIGHT NOTICE
Copyright of this drawing and design is held permanently by Carma Building Group Pty Ltd. Unauthorised use of this drawing and / or design, or any variation thereof, will trigger immediate legal proceedings.



carma building group
Suite 2 / 199 Gympie Tce, Noosaville Q 45(
T 07 5447 1250 F 07 5470 2586
E admin@carmabuildinggroup.com.au


PROJECT
VILLAS 68 & 69
LAGUNA ESTATE
13 LAKE WEYBA DRIVE
NOOSAVILLE

CLIENT
LAGUNA RETIREMENT ESTATE

DRAWING TITLE
VILLA 68 - LAUNDRY, BATHROOM, ENSUITE & ROBE DETAILS

SCALE @ ORIGINAL SIZ
1:50 A3


DATE DRAW
SEPTEMBER 2025 MW

DRAWING STATUS
FOR CONSTRUCTION

DRAWING NO. ISSU
LRV068 WD-11 A

## INTERIOR ELEVATIONS ABBREVIATIONS & LEGEND


| | |
|---|---|
| AP | APPLIANCE CUPBD. ROLLER SHUTTER |
| AR | ARCHITRAVE |
| BH | BULKHEAD |
| BN | BENCHTOP |
| BR | BROOM CUPBOARD |
| BSP | BATH SPOUT |
| BTH | BATH TUB |
| CD | CLOTHES DRYER |
| CO | CORNICE |
| CT | COOKTOP |
| DR | DRAWER |
| DV | DUCTED VACUUM INLET |
| DW | DISHWASHER |
| FR | FRIDGE RECESS |
| FT | FEATURE TILE |
| FW | FLOOR WASTE |
| GR | GRAB RAIL |
| GPO | GENERAL POWER OUTLET (DOUBLE) |
| KB | KICKBOARD |
| L | LINEN CUPBOARD |
| LAM | PLASTIC LAMINATE FINISH |
| MIR | MIRROR |
| MR | MICROWAVE RECESS |
| MXR | MIXER TAP |
| OH | OVERHEAD CUPBOARD |
| PB | PLASTERBOARD BULKHEAD |
| PL | PLASTERBOARD FINISH |
| PN | PANTRY |
| RBH | ROBE HOOK |
| RH | RANGEHOOD |
| SB | SHOWER BASKET |
| SCR | SHOWER SCREEN |
| SH | SHELF / SHELVES |
| SHR | SHOWER |
| SK | SKIRTING BOARD |
| SNK | SINK |
| SP | SPLASHBACK |
| SR | SHOWER ROSE |
| SRD | SLIDING ROBE DOORS |
| SSH | SHOWER SHELF |
| T | LAUNDRY TUB |
| TBS | TOILET BRUSH SET |
| TRG | TOWEL RING |
| TRH | TOILET ROLL HOLDER |
| TS | TOILET SUITE |
| TWL | TOWEL RAIL |
| VAN | VANITY BENCH |
| VB | VANITY BASIN |
| WM | WASHING MACHINE SPACE |
| WMT | WASHING MACHINE TAPS |
| WO | WALL OVEN |
| WR | WINE RACKS |
| WT | WALL TILES |

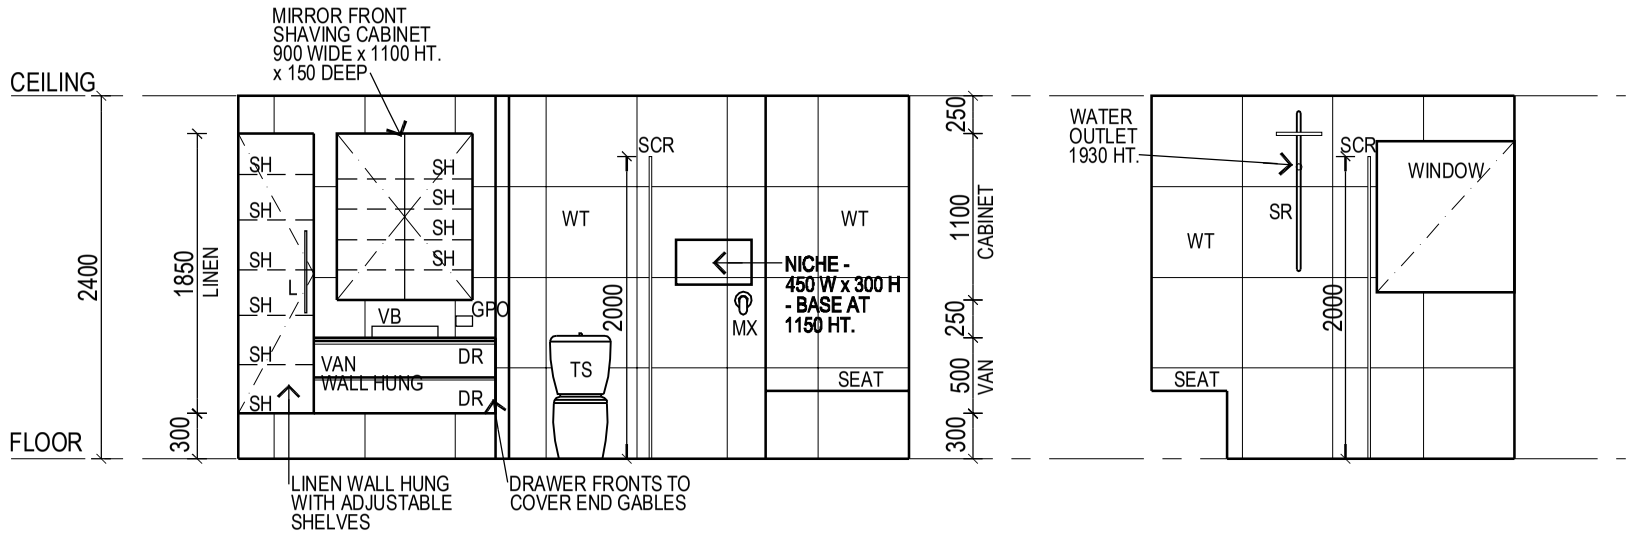


- ELEVATION 11
ENSUITE - V68 1:50





- ELEVATION 12
ENSUITE - V68 1:50

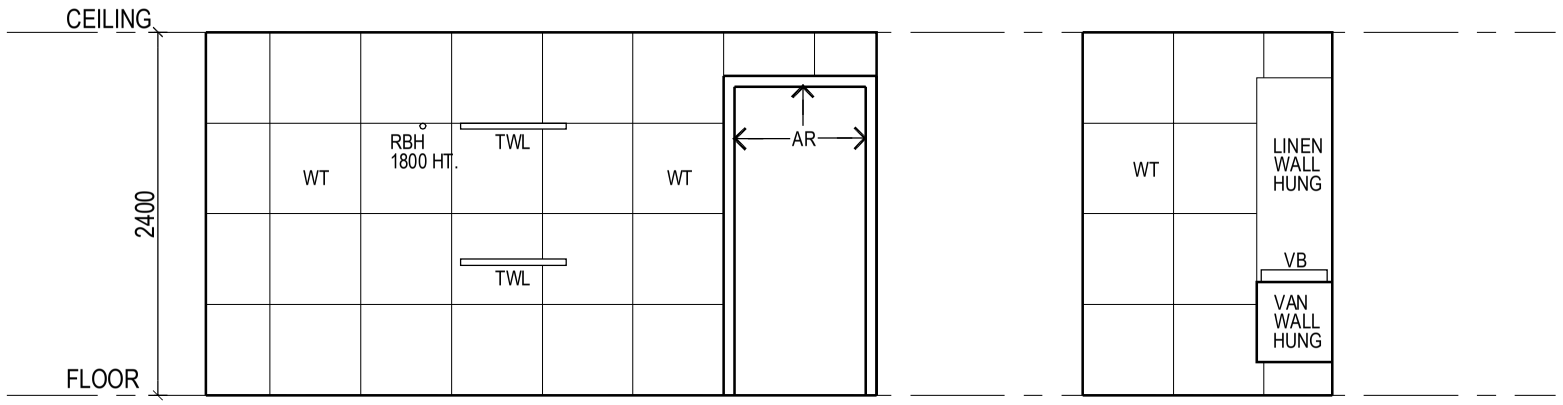


- ELEVATION 13
ENSUITE - V68 1:50

- ELEVATION 14
ENSUITE - V68 1:50

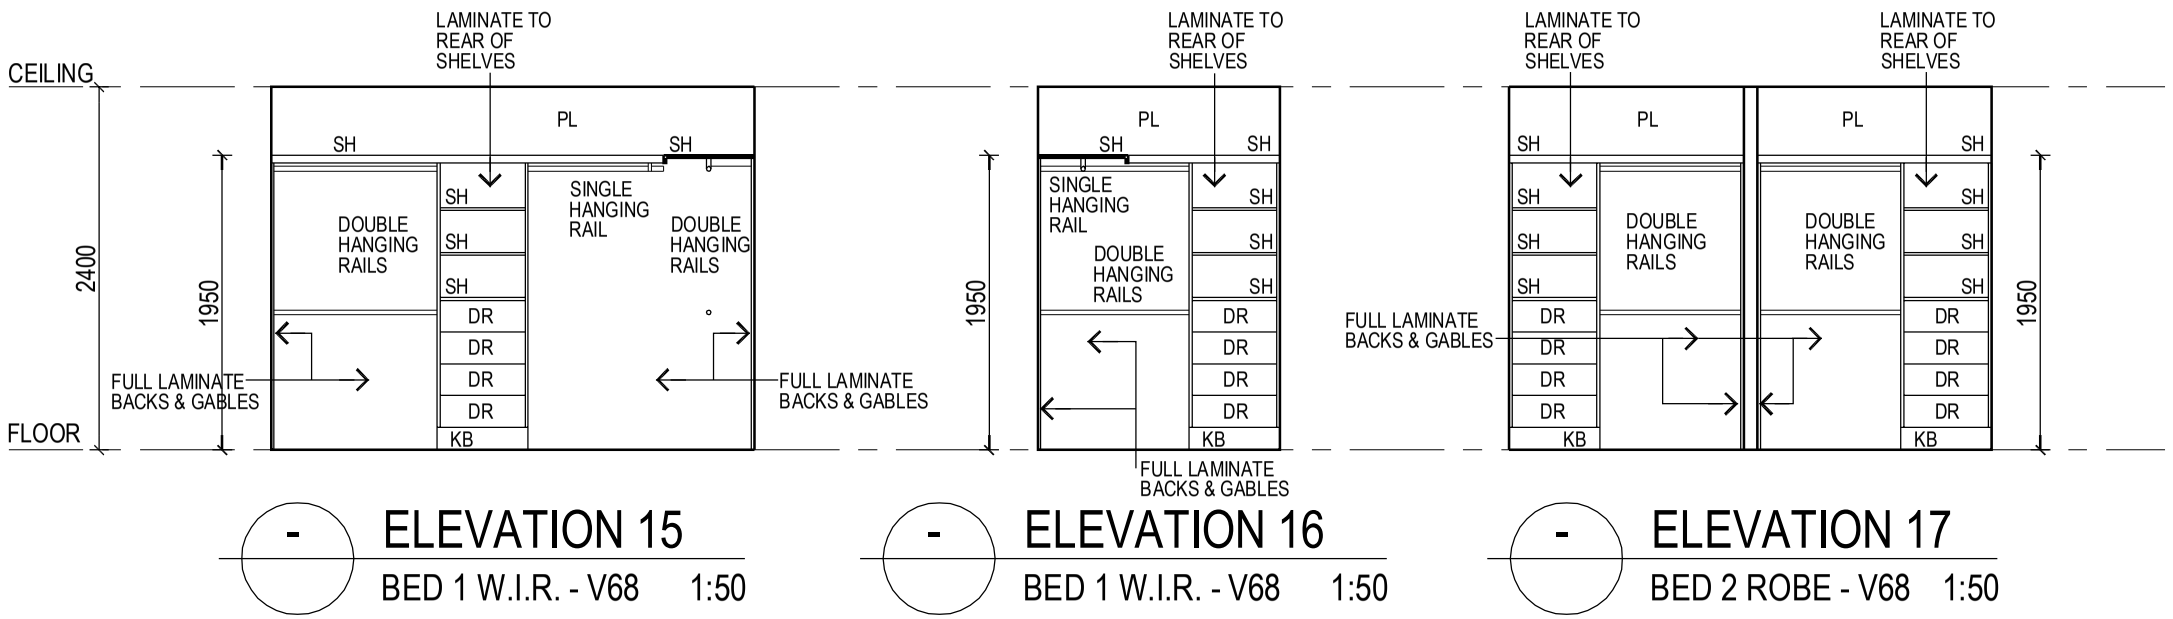


- ELEVATION 15
BED 1 W.I.R. - V68 1:50

- ELEVATION 16
BED 1 W.I.R. - V68 1:50

- ELEVATION 17
BED 2 ROBE - V68 1:50

| ISSUE | DATE | DESCRIPTION |
|---|---|---|
| A | 01/02/26 | ISSUED FOR CONSTRUCTION |


© COPYRIGHT NOTICE
Copyright of this drawing and design is held permanently by Carma Building Group Pty Ltd. Unauthorised use of this drawing and / or design, or any variation thereof, will trigger immediate legal proceedings.



carma building group
Suite 2 / 199 Gympie Tce, Noosaville Q 45
T 07 5447 1250 F 07 5470 2586
E admin@carmabuildinggroup.com.au


PROJECT
VILLAS 68 & 69
LAGUNA ESTATE
13 LAKE WEYBA DRIVE
NOOSAVILLE

CLIENT
LAGUNA RETIREMENT ESTATE

DRAWING TITLE
VILLA 68 - LAUNDRY, BATHROOM, ENSUITE & ROBE DETAILS

SCALE @ ORIGINAL SIZ
1:50 A3


DATE DRAW
SEPTEMBER 2025 MW

DRAWING STATUS
FOR CONSTRUCTION


DRAWING NO. ISSU
LRV068 WD-12 A

## INTERIOR ELEVATIONS ABBREVIATIONS & LEGEND


| | |
|---|---|
| AP | APPLIANCE CUPBD. ROLLER SHUTTER |
| AR | ARCHITRAVE |
| BH | BULKHEAD |
| BN | BENCHTOP |
| BR | BROOM CUPBOARD |
| BSP | BATH SPOUT |
| BTH | BATH TUB |
| CD | CLOTHES DRYER |
| CO | CORNICE |
| CT | COOKTOP |
| DR | DRAWER |
| DV | DUCTED VACUUM INLET |
| DW | DISHWASHER |
| FR | FRIDGE RECESS |
| FT | FEATURE TILE |
| FW | FLOOR WASTE |
| GR | GRAB RAIL |
| GPO | GENERAL POWER OUTLET (DOUBLE) |
| KB | KICKBOARD |
| L | LINEN CUPBOARD |
| LAM | PLASTIC LAMINATE FINISH |
| MIR | MIRROR |
| MR | MICROWAVE RECESS |
| MXR | MIXER TAP |
| OH | OVERHEAD CUPBOARD |
| PB | PLASTERBOARD BULKHEAD |
| PL | PLASTERBOARD FINISH |
| PN | PANTRY |
| RBH | ROBE HOOK |
| RH | RANGEHOOD |
| SB | SHOWER BASKET |
| SCR | SHOWER SCREEN |
| SH | SHELF / SHELVES |
| SHR | SHOWER |
| SK | SKIRTING BOARD |
| SNK | SINK |
| SP | SPLASHBACK |
| SR | SHOWER ROSE |
| SRD | SLIDING ROBE DOORS |
| SSH | SHOWER SHELF |
| T | LAUNDRY TUB |
| TBS | TOILET BRUSH SET |
| TRG | TOWEL RING |
| TRH | TOILET ROLL HOLDER |
| TS | TOILET SUITE |
| TWL | TOWEL RAIL |
| VAN | VANITY BENCH |
| VB | VANITY BASIN |
| WM | WASHING MACHINE SPACE |
| WMT | WASHING MACHINE TAPS |
| WO | WALL OVEN |
| WR | WINE RACKS |
| WT | WALL TILES |

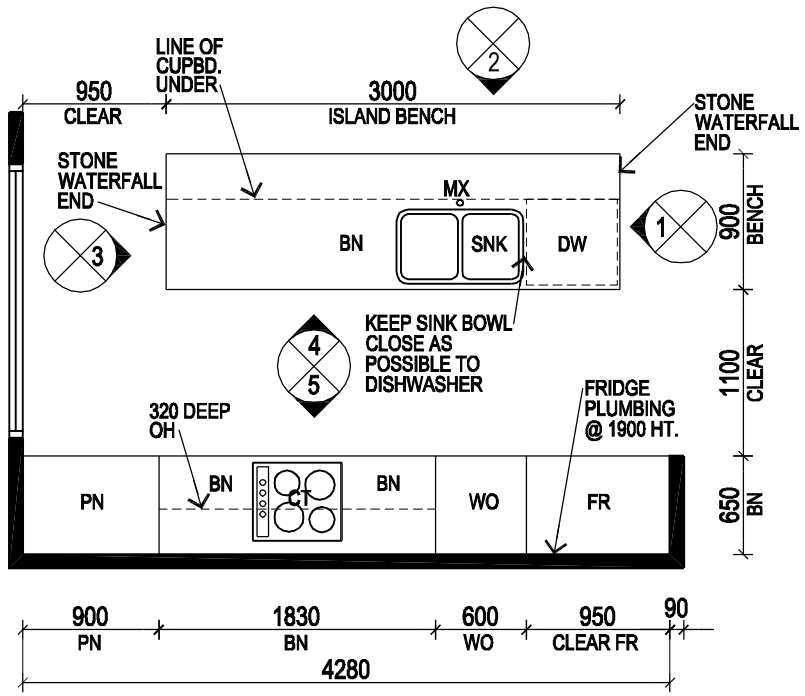



## - KITCHEN PLAN
VILLA 69 1:50

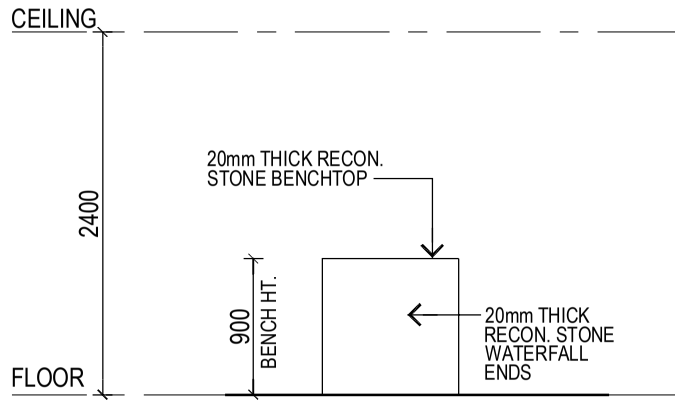



## - ELEVATION 1
KITCHEN - V69 1:50

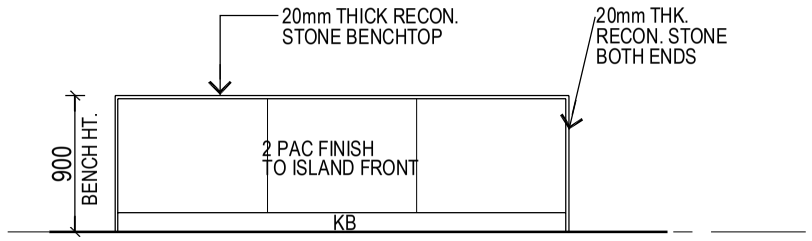



## - ELEVATION 2
KITCHEN - V69 1:50

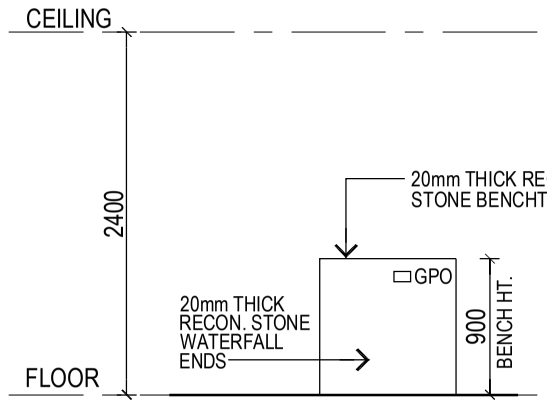


## - ELEVATION 3
KITCHEN - V69 1:50

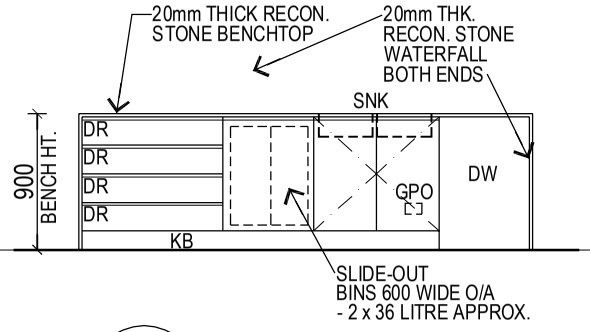


## - ELEVATION 4
KITCHEN - V69 1:50

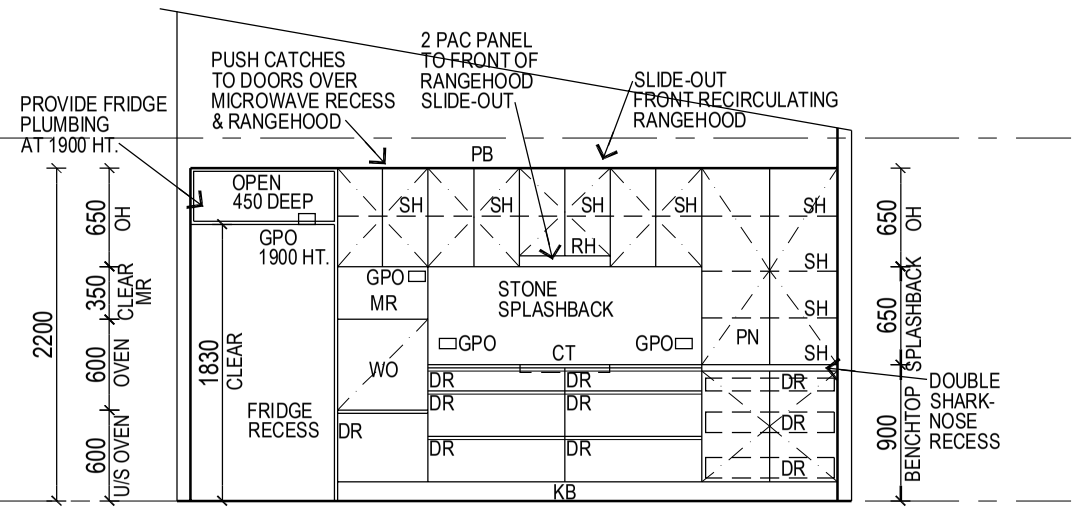


## - ELEVATION 5
KITCHEN - V69 1:50


© COPYRIGHT NOTICE
Copyright of this drawing and design is held permanently by Carma Building Group Pty Ltd. Unauthorised use of this drawing and / or design, or any variation thereof, will trigger immediate legal proceedings.


| ISSUE | DATE | DESCRIPTION |
|---|---|---|
| A | 01/02/26 | ISSUED FOR CONSTRUCTION |


carma building group
Suite 2 / 199 Gympie Tce, Noosaville Q 456
T 07 5447 1250 F 07 5470 2586
E admin@carmabuildinggroup.com.au


PROJECT
VILLAS 68 & 69
LAGUNA ESTATE
13 LAKE WEYBA DRIVE
NOOSAVILLE

CLIENT
LAGUNA RETIREMENT ESTATE

DRAWING TITLE
VILLA 69 - KITCHEN DETAILS


| SCALE | @ ORIGINAL SIZ |
|---|---|
| 1:50 | A3 |
| DATE | DRAW |
| SEPTEMBER 2025 | MW |

DRAWING STATUS
FOR CONSTRUCTION


| DRAWING NO. | ISSU |
|---|---|
| LRV068 WD-13 | A |

## INTERIOR ELEVATIONS ABBREVIATIONS & LEGEND

| | |
|---|---|
| AP | APPLIANCE CUPBD. ROLLER SHUTTER |
| AR | ARCHITRAVE |
| BH | BULKHEAD |
| BN | BENCHTOP |
| BR | BROOM CUPBOARD |
| BSP | BATH SPOUT |
| BTH | BATH TUB |
| CD | CLOTHES DRYER |
| CO | CORNICE |
| CT | COOKTOP |
| DR | DRAWER |
| DV | DUCTED VACUUM INLET |
| DW | DISHWASHER |
| FR | FRIDGE RECESS |
| FT | FEATURE TILE |
| FW | FLOOR WASTE |
| GR | GRAB RAIL |
| GPO | GENERAL POWER OUTLET (DOUBLE) |
| KB | KICKBOARD |
| L | LINEN CUPBOARD |
| LAM | PLASTIC LAMINATE FINISH |
| MIR | MIRROR |
| MR | MICROWAVE RECESS |
| MXR | MIXER TAP |
| OH | OVERHEAD CUPBOARD |
| PB | PLASTERBOARD BULKHEAD |
| PL | PLASTERBOARD FINISH |
| PN | PANTRY |
| RBH | ROBE HOOK |
| RH | RANGEHOOD |
| SB | SHOWER BASKET |
| SCR | SHOWER SCREEN |
| SH | SHELF / SHELVES |
| SHR | SHOWER |
| SK | SKIRTING BOARD |
| SNK | SINK |
| SP | SPLASHBACK |
| SR | SHOWER ROSE |
| SRD | SLIDING ROBE DOORS |
| SSH | SHOWER SHELF |
| T | LAUNDRY TUB |
| TBS | TOILET BRUSH SET |
| TRG | TOWEL RING |
| TRH | TOILET ROLL HOLDER |
| TS | TOILET SUITE |
| TWL | TOWEL RAIL |
| VAN | VANITY BENCH |
| VB | VANITY BASIN |
| WM | WASHING MACHINE SPACE |
| WMT | WASHING MACHINE TAPS |
| WO | WALL OVEN |
| WR | WINE RACKS |
| WT | WALL TILES |

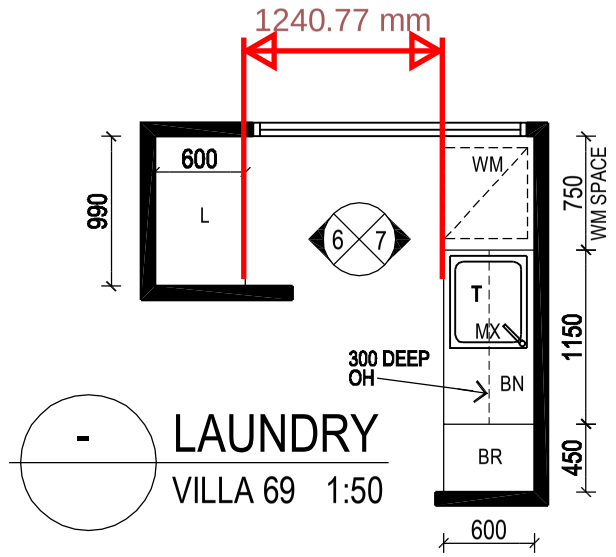



## - LAUNDRY
VILLA 69 1:50

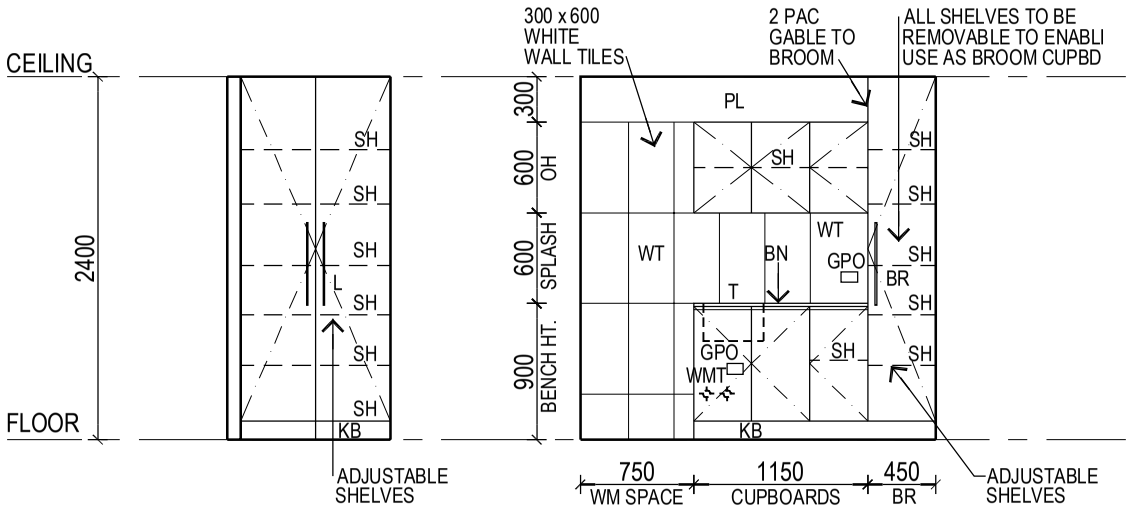


## - ELEVATION 6
LAUNDRY - V69 1:50





## - ELEVATION 7
LAUNDRY - V69 1:50

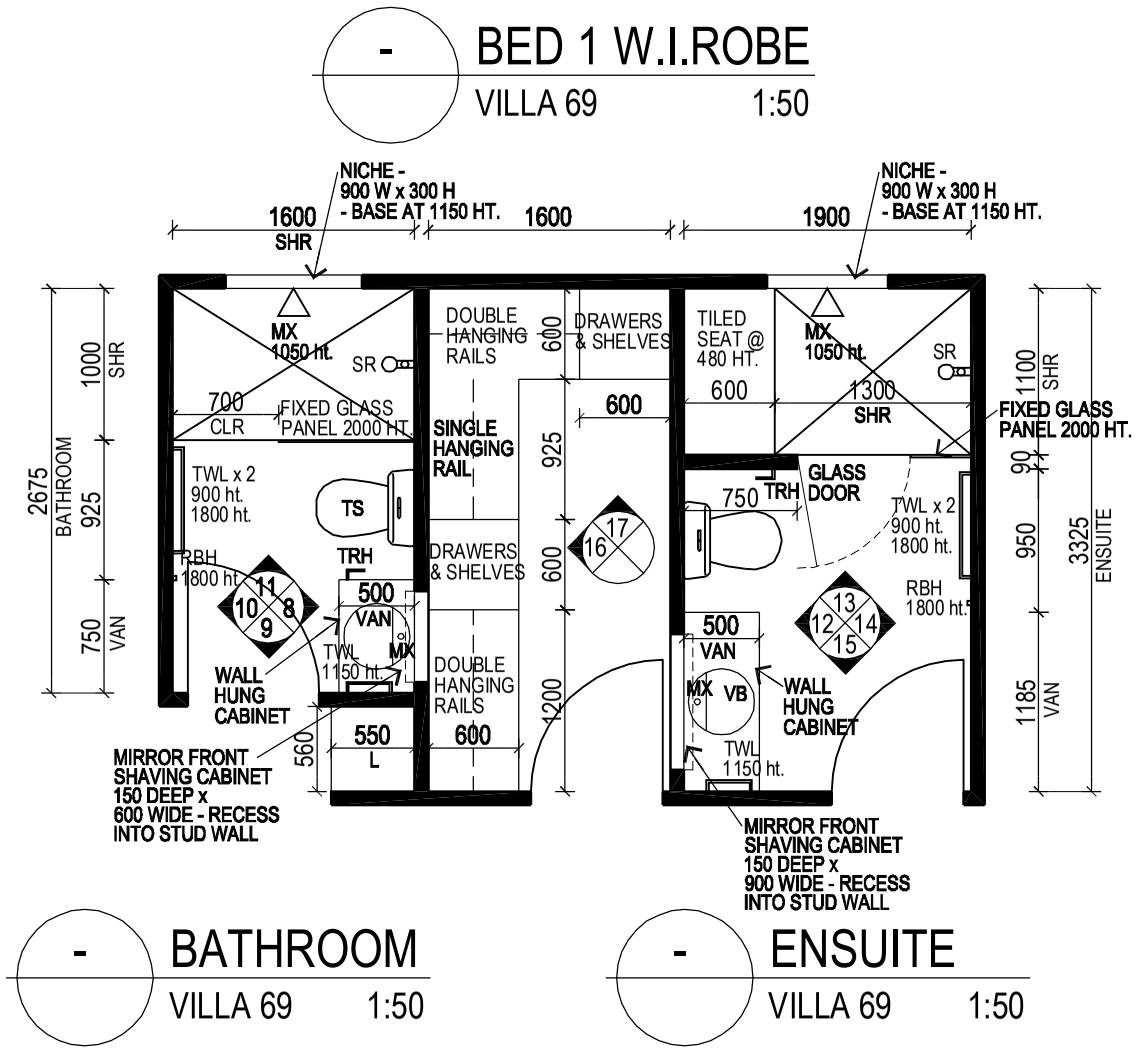



## - BED 1 W.I.ROBE
VILLA 69 1:50

## - BATHROOM
VILLA 69 1:50


## - ENSUITE
VILLA 69 1:50

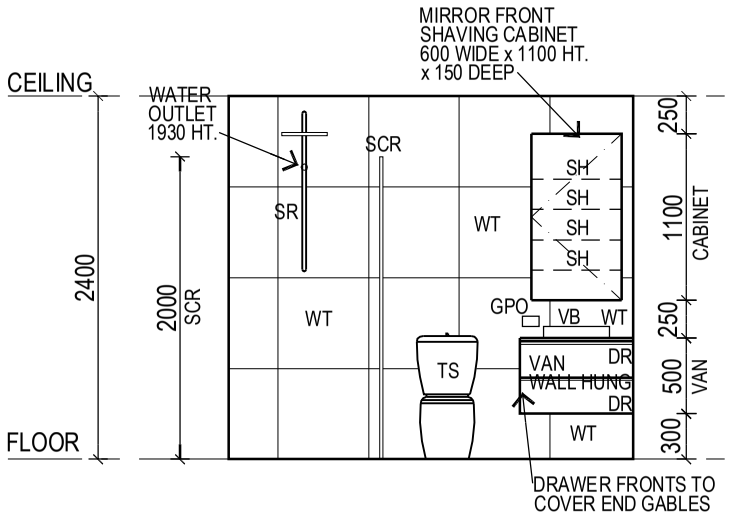



## - ELEVATION 8
BATHROOM - V69 1:50

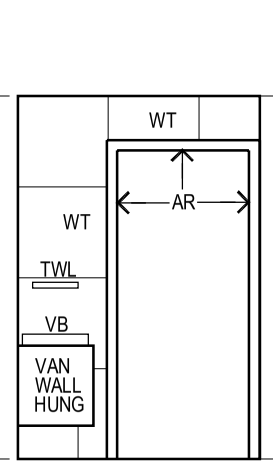


## - ELEVATION 9
BATHROOM - V69 1:50

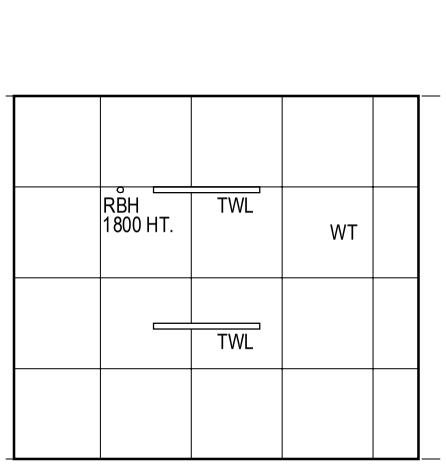


## - ELEVATION 10
BATHROOM - V69 1:50

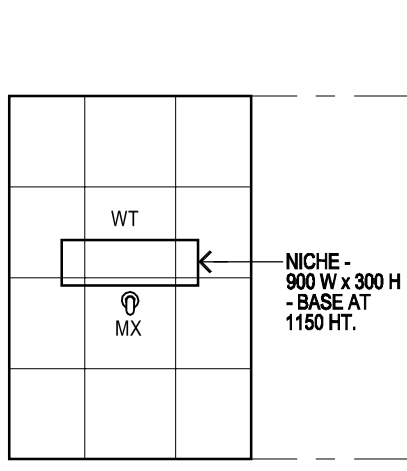


## - ELEVATION 11
BATHROOM - V69 1:50

| ISSUE | DATE | DESCRIPTION |
|---|---|---|
| A | 01/02/26 | ISSUED FOR CONSTRUCTION |

© COPYRIGHT NOTICE
Copyright of this drawing and design is held permanently by Carma Building Group Pty Ltd. Unauthorised use of this drawing and / or design, or any variation thereof, will trigger immediate legal proceedings.

carma building group
Suite 2 / 199 Gympie Tce, Noosaville Q 45
T 07 5447 1250 F 07 5470 2586
E admin@carmabuildinggroup.com.au

PROJECT
VILLAS 68 & 69
LAGUNA ESTATE
13 LAKE WEYBA DRIVE
NOOSAVILLE

CLIENT
LAGUNA RETIREMENT ESTATE

DRAWING TITLE
VILLA 69 - LAUNDRY, BATHROOM, ENSUITE & ROBE DETAILS

SCALE @ ORIGINAL SIZ
1:50 A3


DATE DRAW
SEPTEMBER 2025 MW

DRAWING STATUS
FOR CONSTRUCTION

DRAWING NO. ISSU
LRV068 WD-14 A

## INTERIOR ELEVATIONS ABBREVIATIONS & LEGEND

| | |
|---|---|
| AP | APPLIANCE CUPBD. ROLLER SHUTTER |
| AR | ARCHITRAVE |
| BH | BULKHEAD |
| BN | BENCHTOP |
| BR | BROOM CUPBOARD |
| BSP | BATH SPOUT |
| BTH | BATH TUB |
| CD | CLOTHES DRYER |
| CO | CORNICE |
| CT | COOKTOP |
| DR | DRAWER |
| DV | DUCTED VACUUM INLET |
| DW | DISHWASHER |
| FR | FRIDGE RECESS |
| FT | FEATURE TILE |
| FW | FLOOR WASTE |
| GR | GRAB RAIL |
| GPO | GENERAL POWER OUTLET (DOUBLE) |
| KB | KICKBOARD |
| L | LINEN CUPBOARD |
| LAM | PLASTIC LAMINATE FINISH |
| MIR | MIRROR |
| MR | MICROWAVE RECESS |
| MXR | MIXER TAP |
| OH | OVERHEAD CUPBOARD |
| PB | PLASTERBOARD BULKHEAD |
| PL | PLASTERBOARD FINISH |
| PN | PANTRY |
| RBH | ROBE HOOK |
| RH | RANGEHOOD |
| SB | SHOWER BASKET |
| SCR | SHOWER SCREEN |
| SH | SHELF / SHELVES |
| SHR | SHOWER |
| SK | SKIRTING BOARD |
| SNK | SINK |
| SP | SPLASHBACK |
| SR | SHOWER ROSE |
| SRD | SLIDING ROBE DOORS |
| SSH | SHOWER SHELF |
| T | LAUNDRY TUB |
| TBS | TOILET BRUSH SET |
| TRG | TOWEL RING |
| TRH | TOILET ROLL HOLDER |
| TS | TOILET SUITE |
| TWL | TOWEL RAIL |
| VAN | VANITY BENCH |
| VB | VANITY BASIN |
| WM | WASHING MACHINE SPACE |
| WMT | WASHING MACHINE TAPS |
| WO | WALL OVEN |
| WR | WINE RACKS |
| WT | WALL TILES |

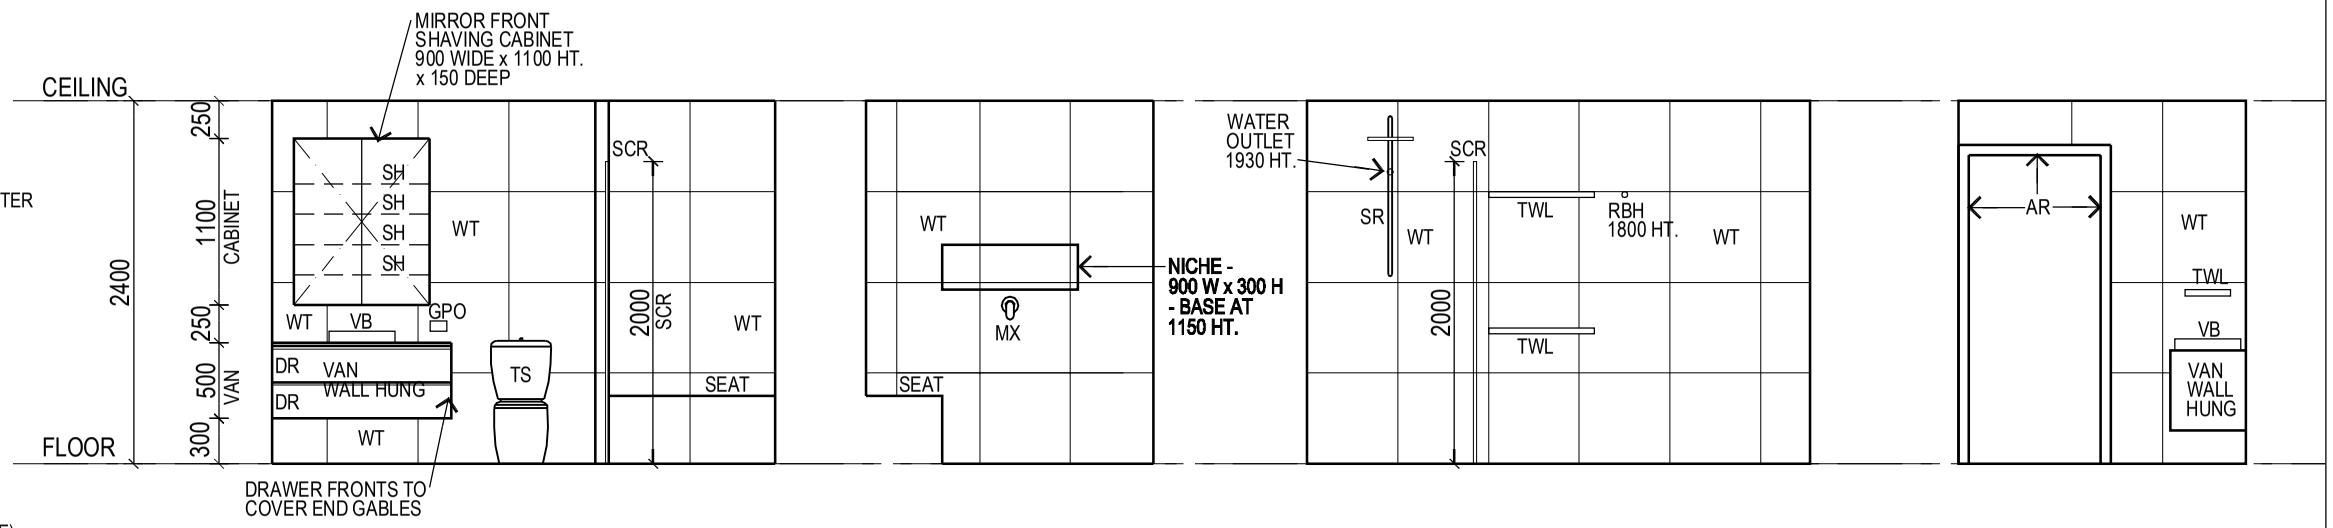



- ELEVATION 12
ENSUITE - V69 1:50


- ELEVATION 13
ENSUITE - V69 1:50

- ELEVATION 14
ENSUITE - V69 1:50

- ELEVATION 15
ENSUITE - V69 1:50

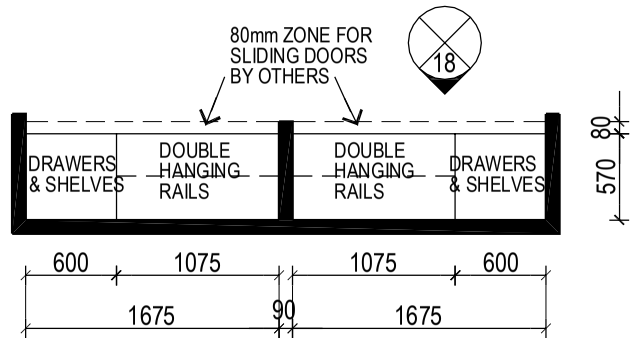


- BED 2 ROBE
VILLA 69 1:50

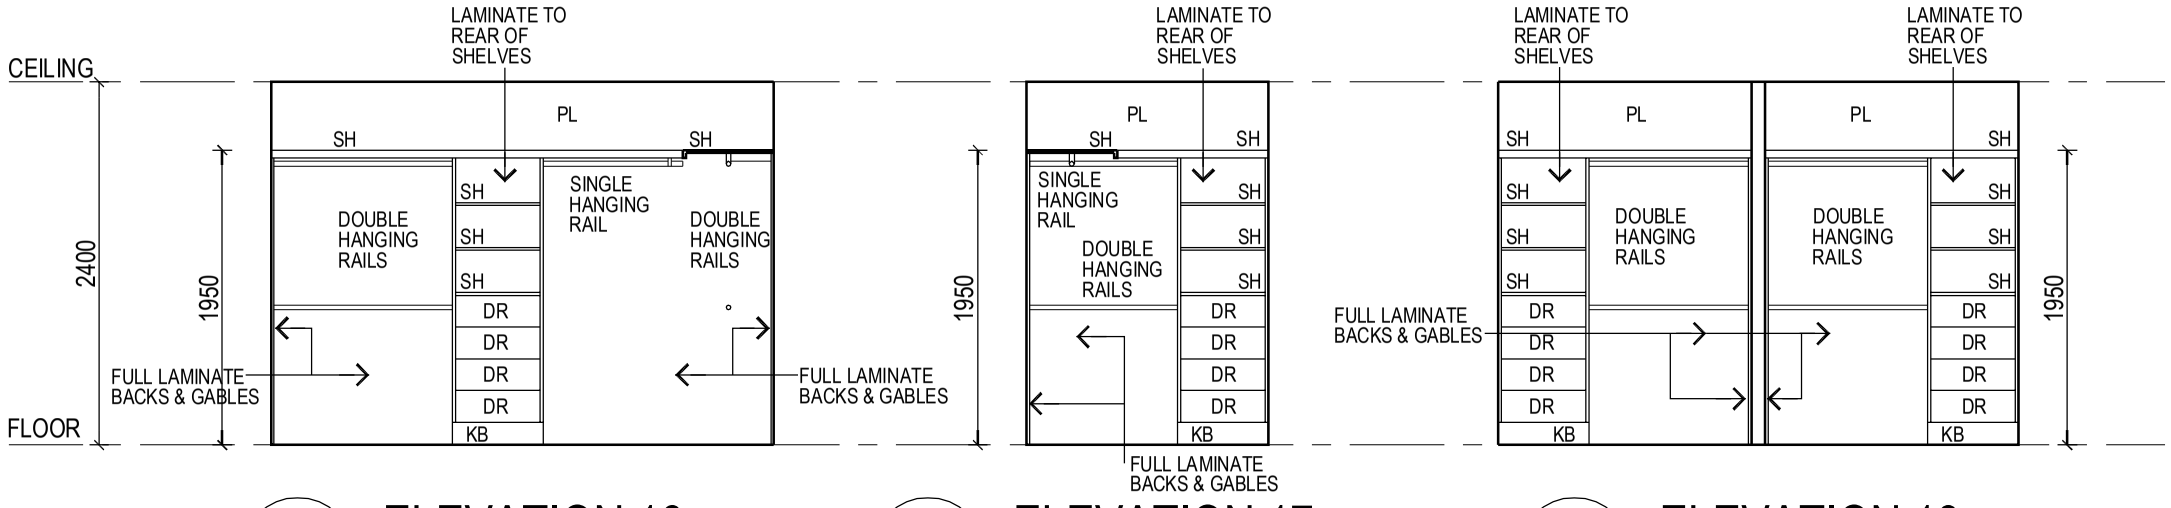


- ELEVATION 16
BED 1 W.I.R. - V69 1:50

- ELEVATION 17
BED 1 W.I.R. - V69 1:50

- ELEVATION 18
BED 2 ROBE - V69 1:50

| ISSUE | DATE | DESCRIPTION |
|---|---|---|
| A | 01/02/26 | ISSUED FOR CONSTRUCTION |


© COPYRIGHT NOTICE
Copyright of this drawing and design is held permanently by Carma Building Group Pty Ltd. Unauthorised use of this drawing and / or design, or any variation thereof, will trigger immediate legal proceedings.



carma building group
Suite 2 / 199 Gympie Tce, Noosaville Q 45(
T 07 5447 1250 F 07 5470 2586
E admin@carmabuildinggroup.com.au


PROJECT
VILLAS 68 & 69
LAGUNA ESTATE
13 LAKE WEYBA DRIVE
NOOSAVILLE

CLIENT
LAGUNA RETIREMENT ESTATE


DRAWING TITLE
VILLA 69 - LAUNDRY, BATHROOM, ENSUITE & ROBE DETAILS

SCALE @ ORIGINAL SIZ
1:50 A3

DATE DRAW
SEPTEMBER 2025 MW

DRAWING STATUS
FOR CONSTRUCTION

DRAWING NO. ISSU
LRV068 WD-15 A

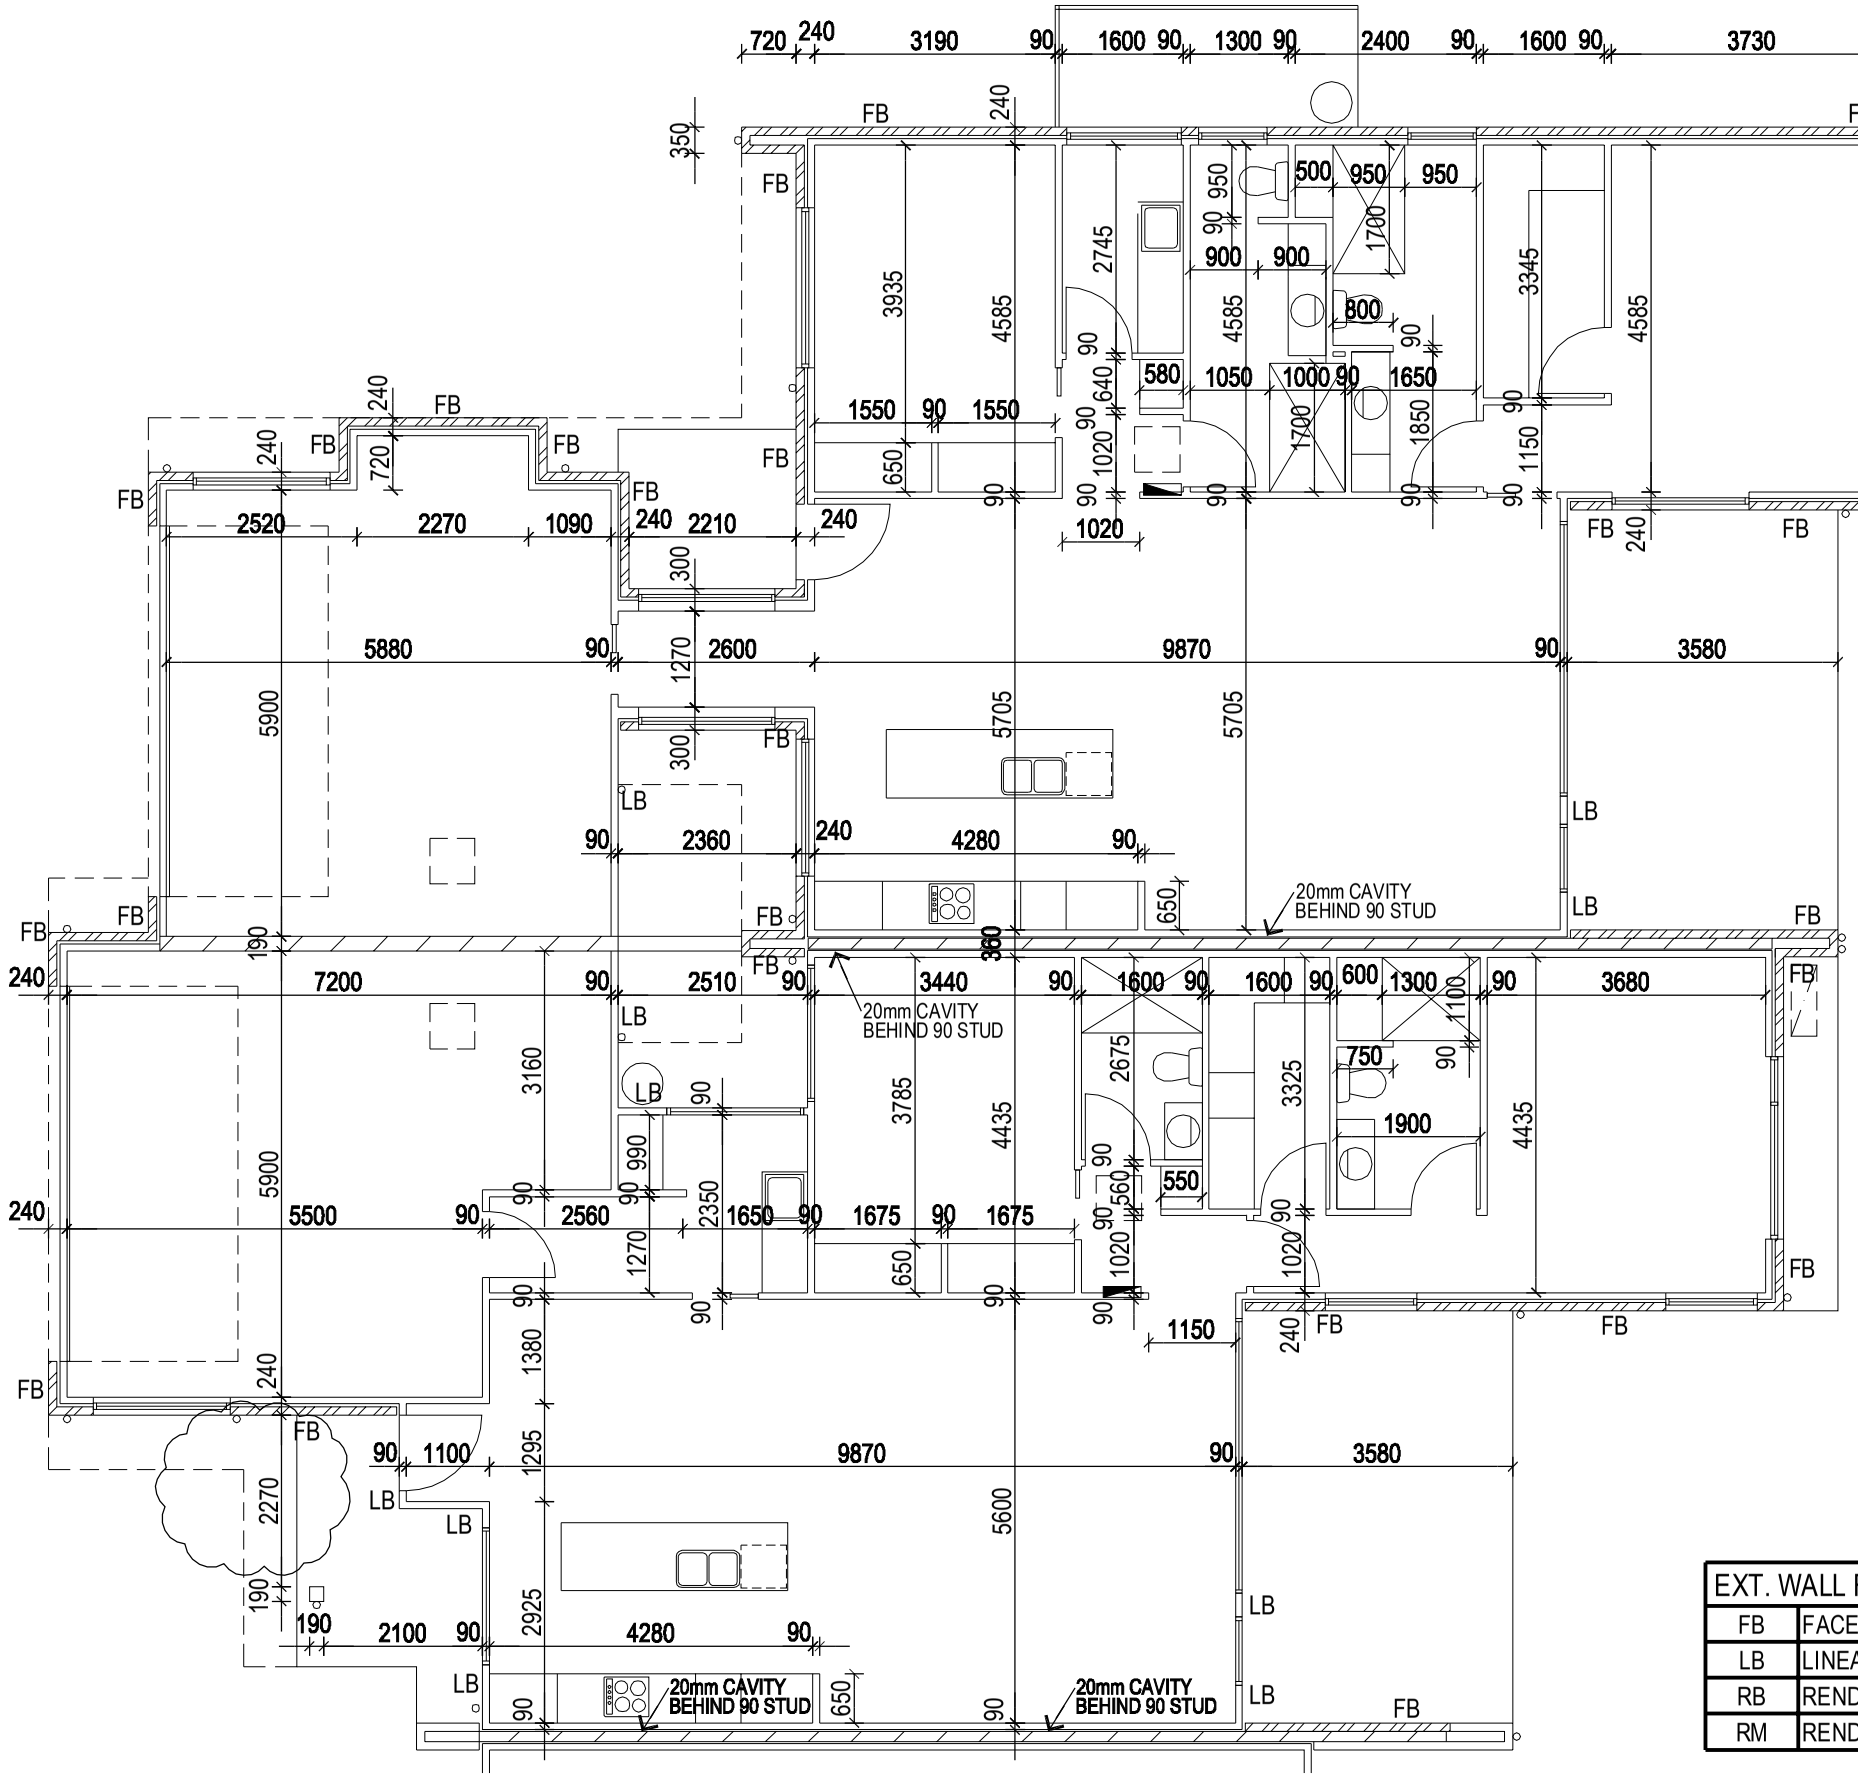


| EXT. WALL FINISHES LEGEND | |
|---|---|
| FB | FACE BRICKWORK |
| LB | LINEA-BOARD CLADDING |
| RB | RENDERED BLUEBOARD |
| RM | RENDERED MASONRY |

| ISSUE | DATE | DESCRIPTION |
|---|---|---|
| A | 01/09/25 | ISSUED FOR APPROVALS |
| B | 06/01/26 | VILLA 69 ENSUITE SHOWER SIZE |
| C | 02/03/26 | VILLA 68 150mm WIDER |
| D | 03/03/26 | VILLA 69 FRONT PORCH POST SETOUT |

© COPYRIGHT NOTICE
Copyright of this drawing and design is held permanently by Carma Building Group Pty Ltd. Unauthorised use of this drawing and / or design, or any variation thereof, will trigger immediate legal proceedings.

carma building group
Suite 2 / 199 Gympie Tce, Noosaville Q 456
T 07 5447 1250 F 07 5470 2586
E admin@carmabuildinggroup.com.au

PROJECT
VILLAS 68 & 69
LAGUNA ESTATE
13 LAKE WEYBA DRIVE
NOOSAVILLE

CLIENT
LAGUNA RETIREMENT ESTATE

DRAWING TITLE
FLOOR PLAN DIMENSIONED & EXTERNAL WALL FINISHES

SCALE @ ORIGINAL SIZ
1:100 A3

DATE DRAW
AUGUST 2025 MW

DRAWING STATUS
FOR CONSTRUCTION

DRAWING NO. ISSU
LRV068 WD-20 D