


Note: This drawing is an artistic interpretation of the general appearance of the design. It is not meant to be an exact rendition.	BUNNINGS warehouse	This is an original design and must not be released or copied unless applicable fee has been paid or job order placed.	Date Created: 11 September 2026 IHC: Philip Bowler



Note: This drawing is an artistic interpretation of the general appearance of the design. It is not meant to be an exact rendition.	BUNNINGS warehouse	This is an original design and must not be released or copied unless applicable fee has been paid or job order placed.	Date Created: 11 September 2026 IHC: Philip Bowler



Note: This drawing is an artistic interpretation of the general appearance of the design. It is not meant to be an exact rendition.	BUNNINGS warehouse	This is an original design and must not be released or copied unless applicable fee has been paid or job order placed.	Date Created: 11 September 2026 IHC: Philip Bowler

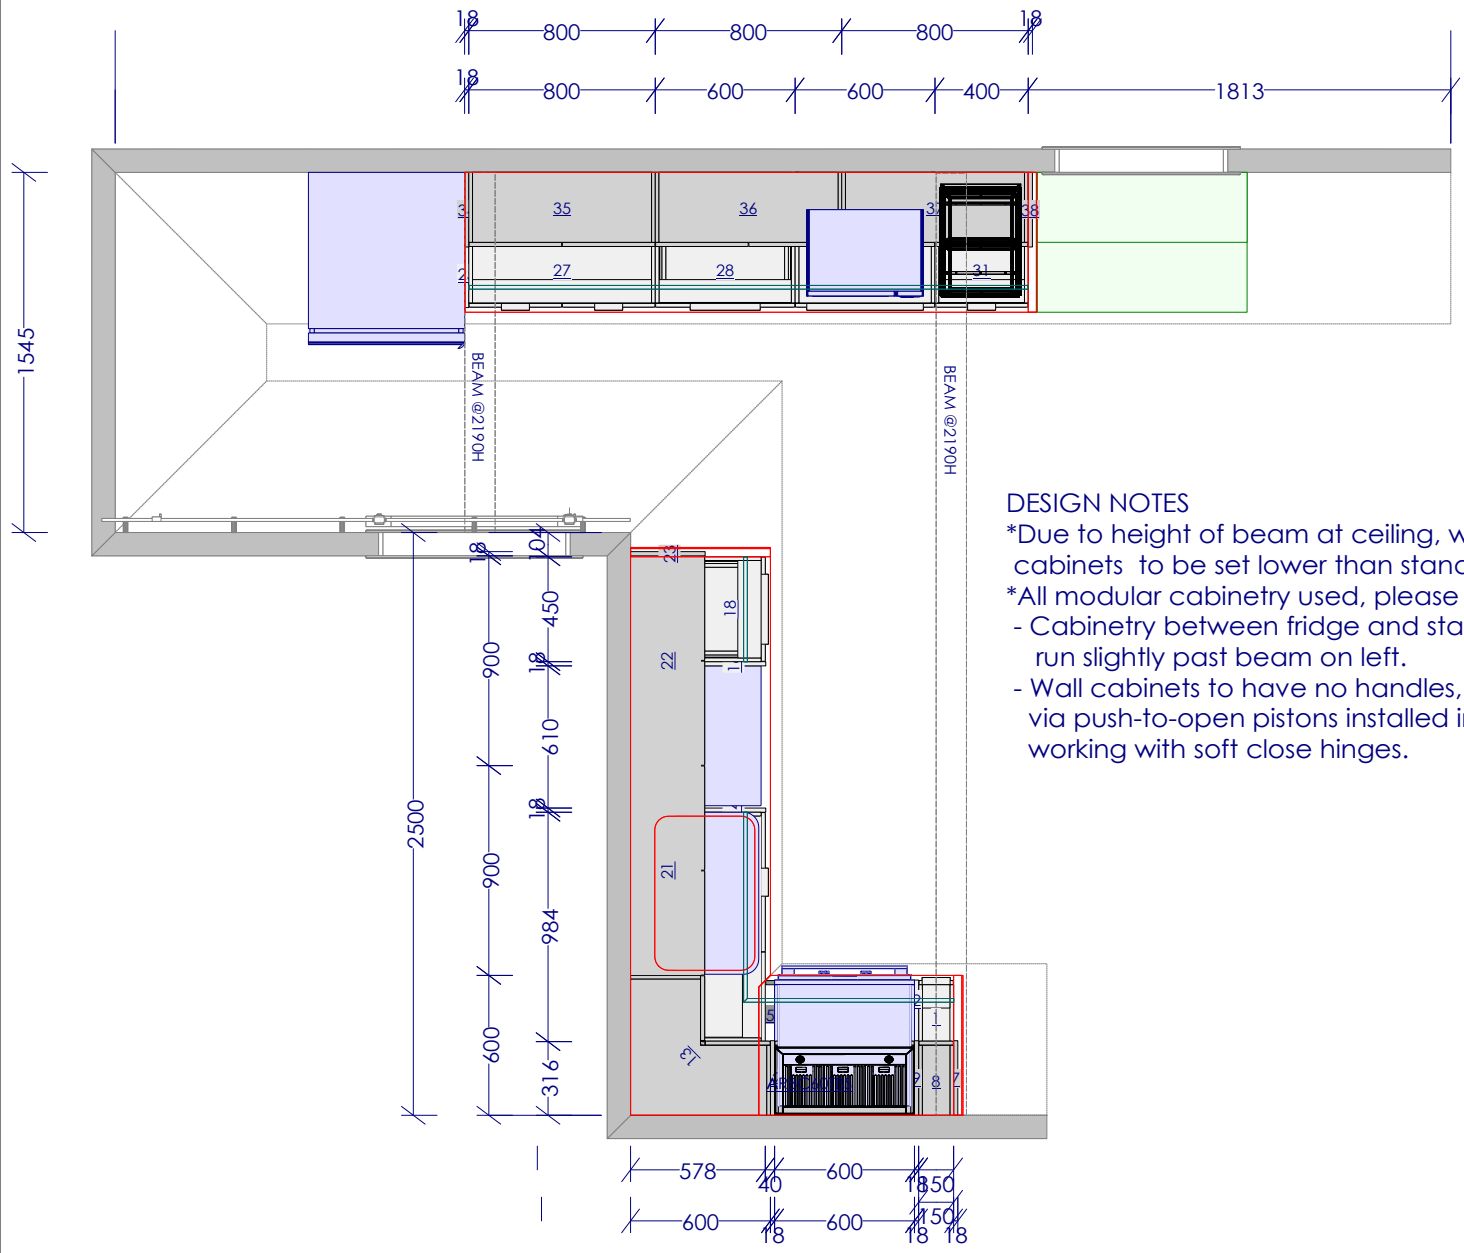

DESIGN NOTES

*Due to height of beam at ceiling, wall cabinets to be set lower than standard.


*All modular cabinetry used, please note

- Cabinetry between fridge and stairs may run slightly past beam on left.
- Wall cabinets to have no handles, operate via push-to-open pistons installed in cabinet, working with soft close hinges.

Legend

1: 150mm Base Cabinet
2: Wall End Panel- Macaroon
3: 600mm Oven Cabinet
5: Filler Panel (Base)- Macaroon
7: Wall End Panel- Macaroon
8: 150mm Wall Cabinet
9: Wall End Panel- Macaroon
10: Med Slideout Rangehood Cabinet 600mm
12: Wall End Panel- Macaroon
13: 600mm Corner Wall Cabinet
14: Base End Panel- Macaroon
16: Base End Panel- Macaroon
17: 1000mm Blind Corner Base Cabinet
18: 450mm 4 Drawer Base Cabinet
21: 900mm Wall Cabinet
22: 900mm Wall Cabinet
23: Wall End Panel- Macaroon
25: Base End Panel- Macaroon
27: 800mm Base Cabinet
28: 600mm 2 Drawer Base Cabinet
29: Underbench Microwave Cabinet
31: 400mm Base Cabinet
34: Wall End Panel- Macaroon
35: 800mm Wall Cabinet
36: 800mm Wall Cabinet
37: 800mm Wall Cabinet
38: Wall End Panel- Macaroon

All dimensions _size designations given are subject to verification on job site and adjustment to fit job conditions.	BUNNINGS warehouse	This is an original design and must not be released or copied unless applicable fee has been paid or job order placed.	Designed: 9/2/2026 Printed: 9/11/2026
Geraldine Wheaton 95 Orient Dr Kitchen V2		All	Drawing #: 1 | No Scale.

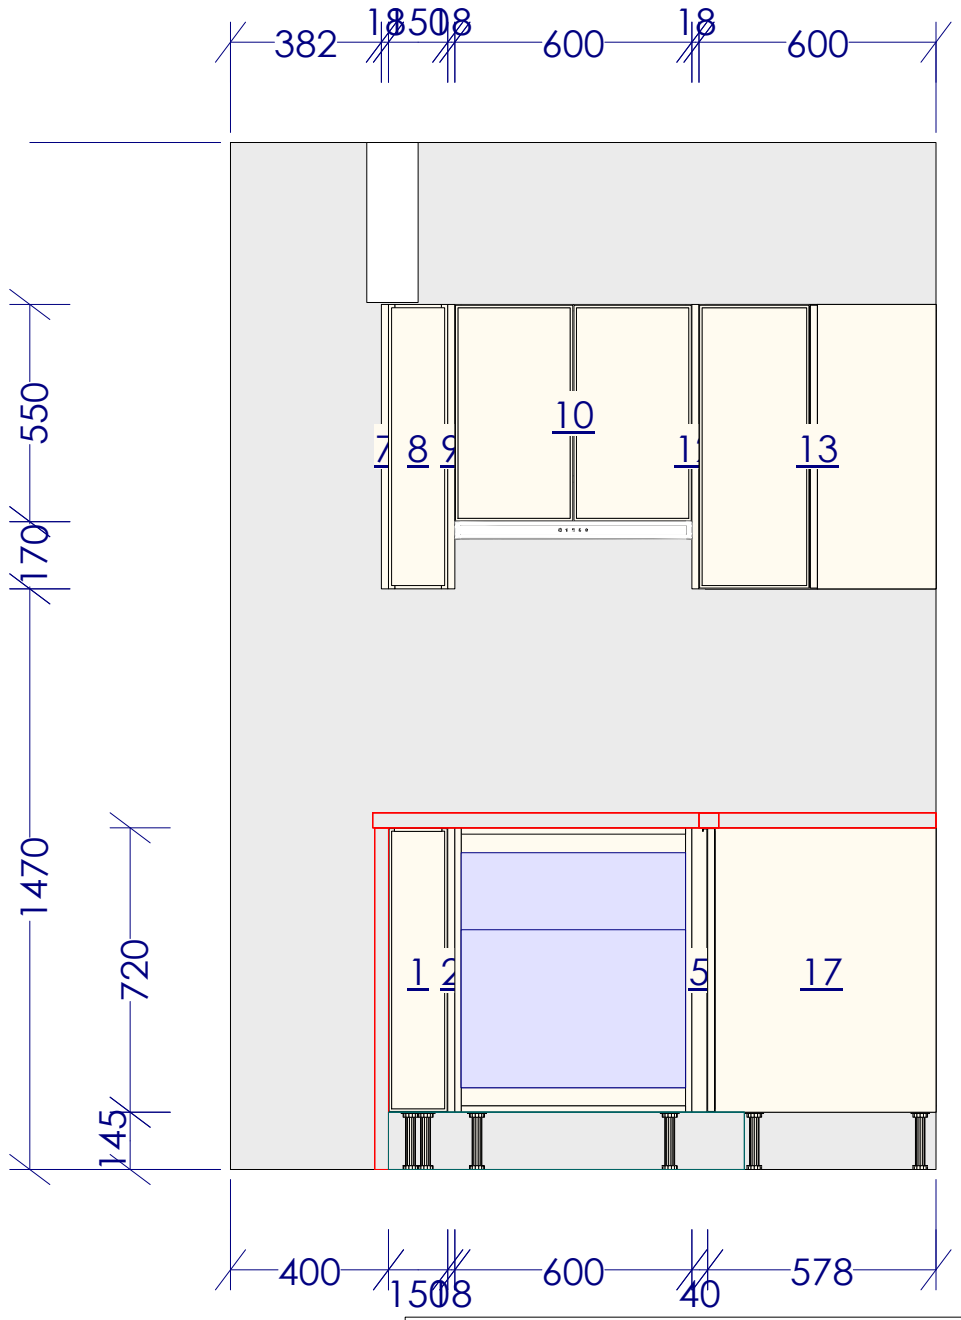


Legend
1: 150mm Base Cabinet
2: Wall End Panel- Macaroon
3: 600mm Oven Cabinet
5: Filler Panel (Base)- Macaroon
7: Wall End Panel- Macaroon
8: 150mm Wall Cabinet
9: Wall End Panel- Macaroon
10: Med Slideout Rangehood Cabinet 600mm
11: ARBC60TBS
12: Wall End Panel- Macaroon
13: 600mm Corner Wall Cabinet
17: 1000mm Blind Corner Base Cabinet

INSTALLER NOTES
5: Filler panel to be cut as needed.

All dimensions _size designations given are subject to verification on job site and adjustment to fit job conditions.	BUNNINGS warehouse	This is an original design and must not be released or copied unless applicable fee has been paid or job order placed.	Designed: 9/2/2026 Printed: 9/11/2026

Geraldine Wheaton 95 Orient Dr Kitchen V2	El 1	Drawing #: 1	No Scale.

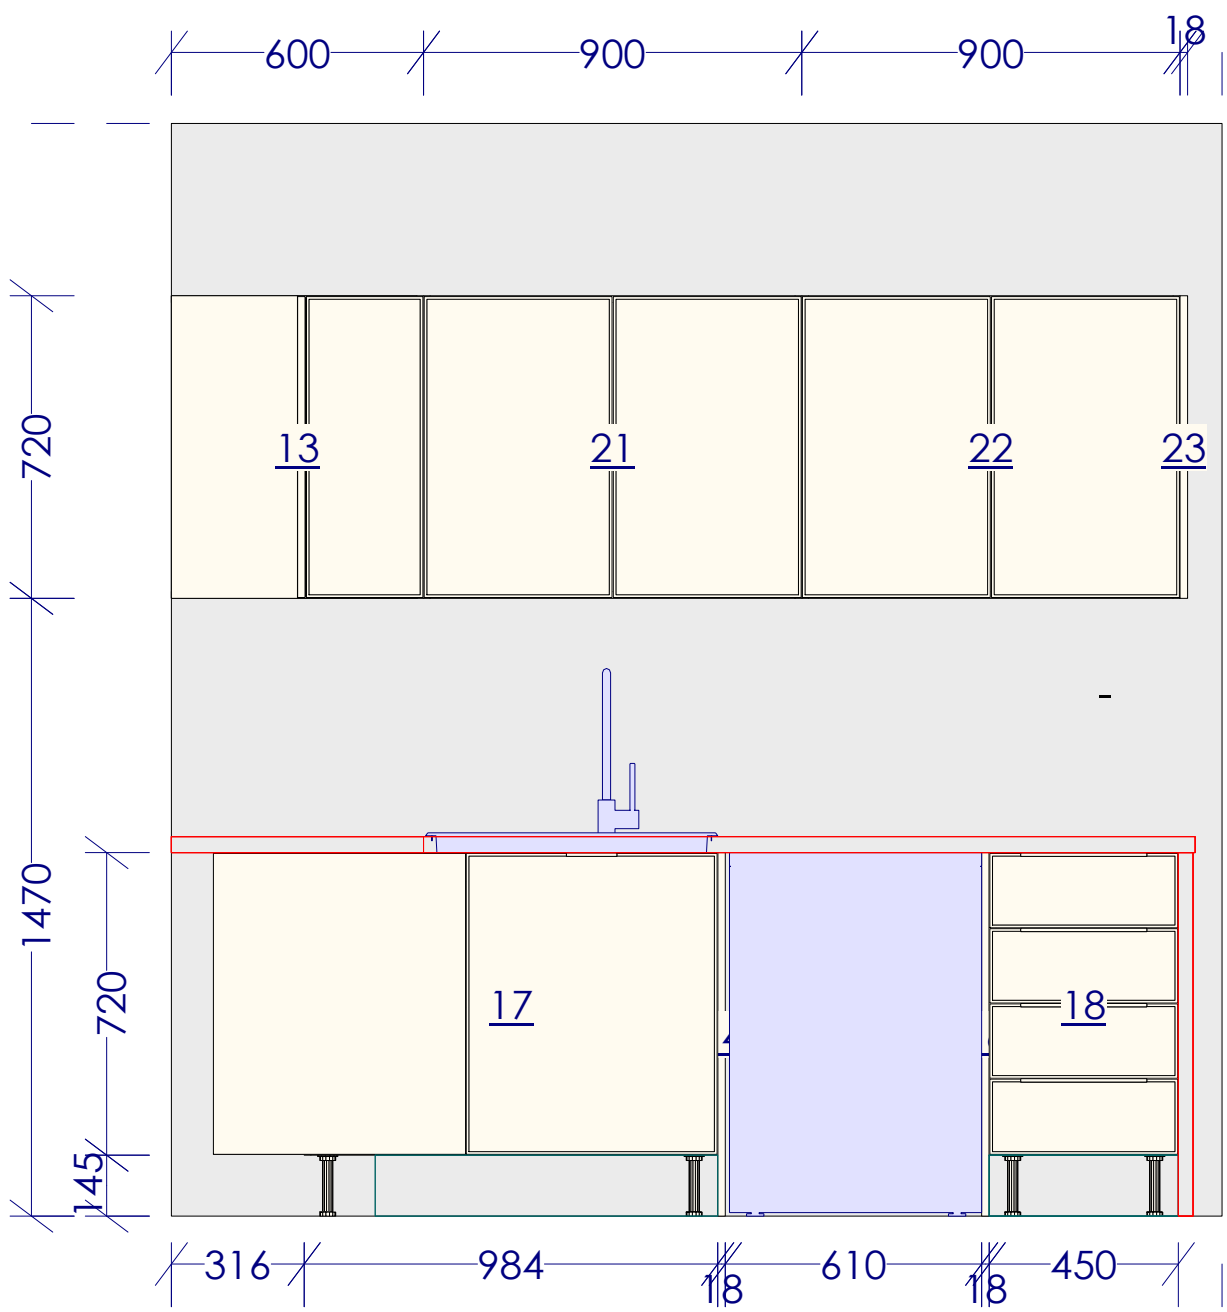

Legend

13: 600mm Corner Wall Cabinet
14: Base End Panel- Macaroon
16: Base End Panel- Macaroon
17: 1000mm Blind Corner Base Cabinet
18: 450mm 4 Drawer Base Cabinet
21: 900mm Wall Cabinet
22: 900mm Wall Cabinet
23: Wall End Panel- Macaroon

INSTALLER NOTES


17: Blind corner cabinet (600mm door) to be set off corner as needed, to give extra depth for door to open across front of oven.


All dimensions _size designations given are subject to verification on job site and adjustment to fit job conditions.

This is an original design and must not be released or copied unless applicable fee has been paid or job order placed.

Designed: 9/2/2026
Printed: 9/11/2026

Geraldine Wheaton 95 Orient Dr Kitchen V2	El 2	Drawing #: 1	No Scale.

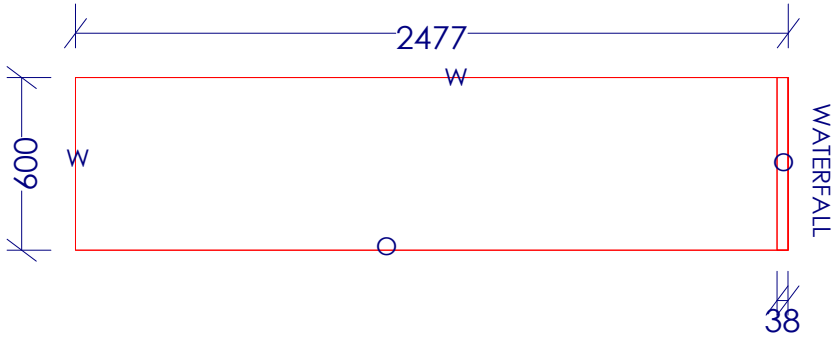

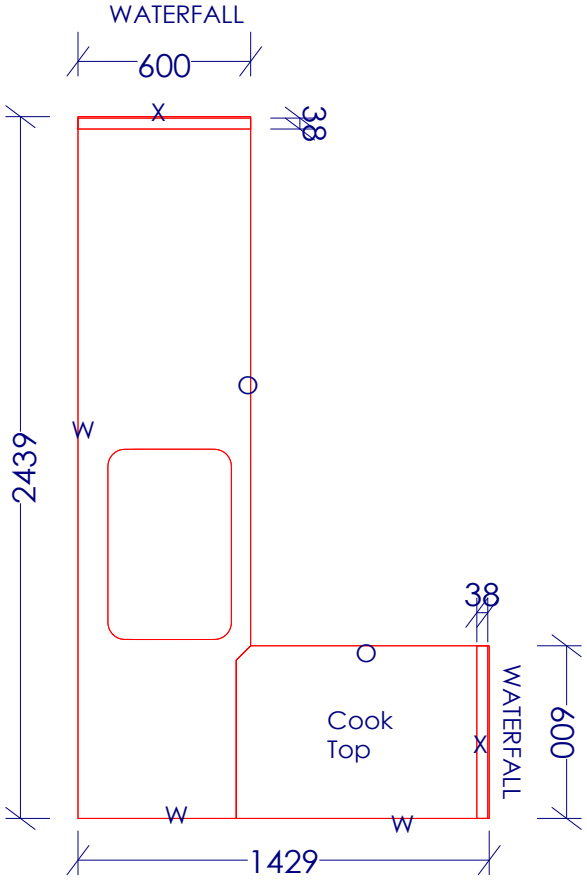

THINK Benchtops (DIY only).
Product supplied to specified sizes, with masons mitre joins in corners. Cutouts (e.g. sink, tap, cooktop) to be completed onsite by cabinetry installer.
Where waterfall end specified, benchtop lengths take into account 40mm overhang, to overlap vertical sections by around 2mm.

Colour:Bianco
Profile: 38mm square edge

VERSION: 1
IHC: Philip Bowler

All dimensions _size designations given are subject to verification on job site and adjustment to fit job conditions.	BUNNINGS warehouse	This is an original design and must not be released or copied unless applicable fee has been paid or job order placed.	Designed: 9/2/2026 Printed: 9/11/2026

Geraldine Wheaton 95 Orient Dr Kitchen V2	Countertops	Drawing #: 1	No Scale.