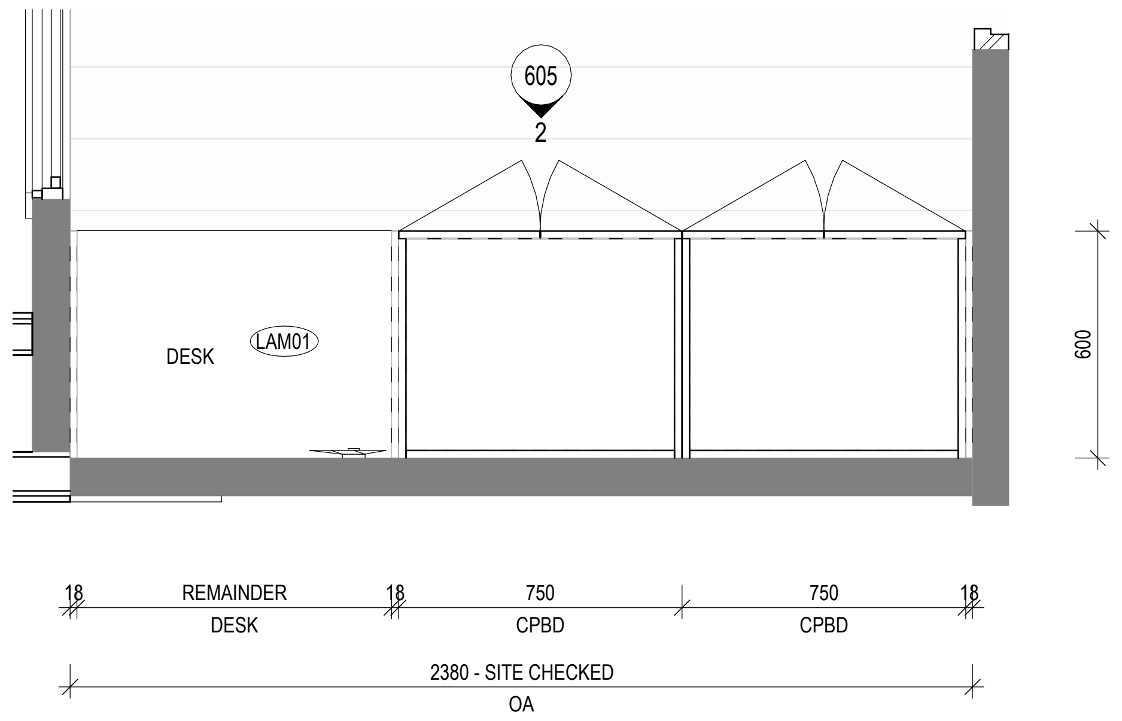

1
203
J07 (MIRRORED) - PLAYROOM JOINERY
1 : 20

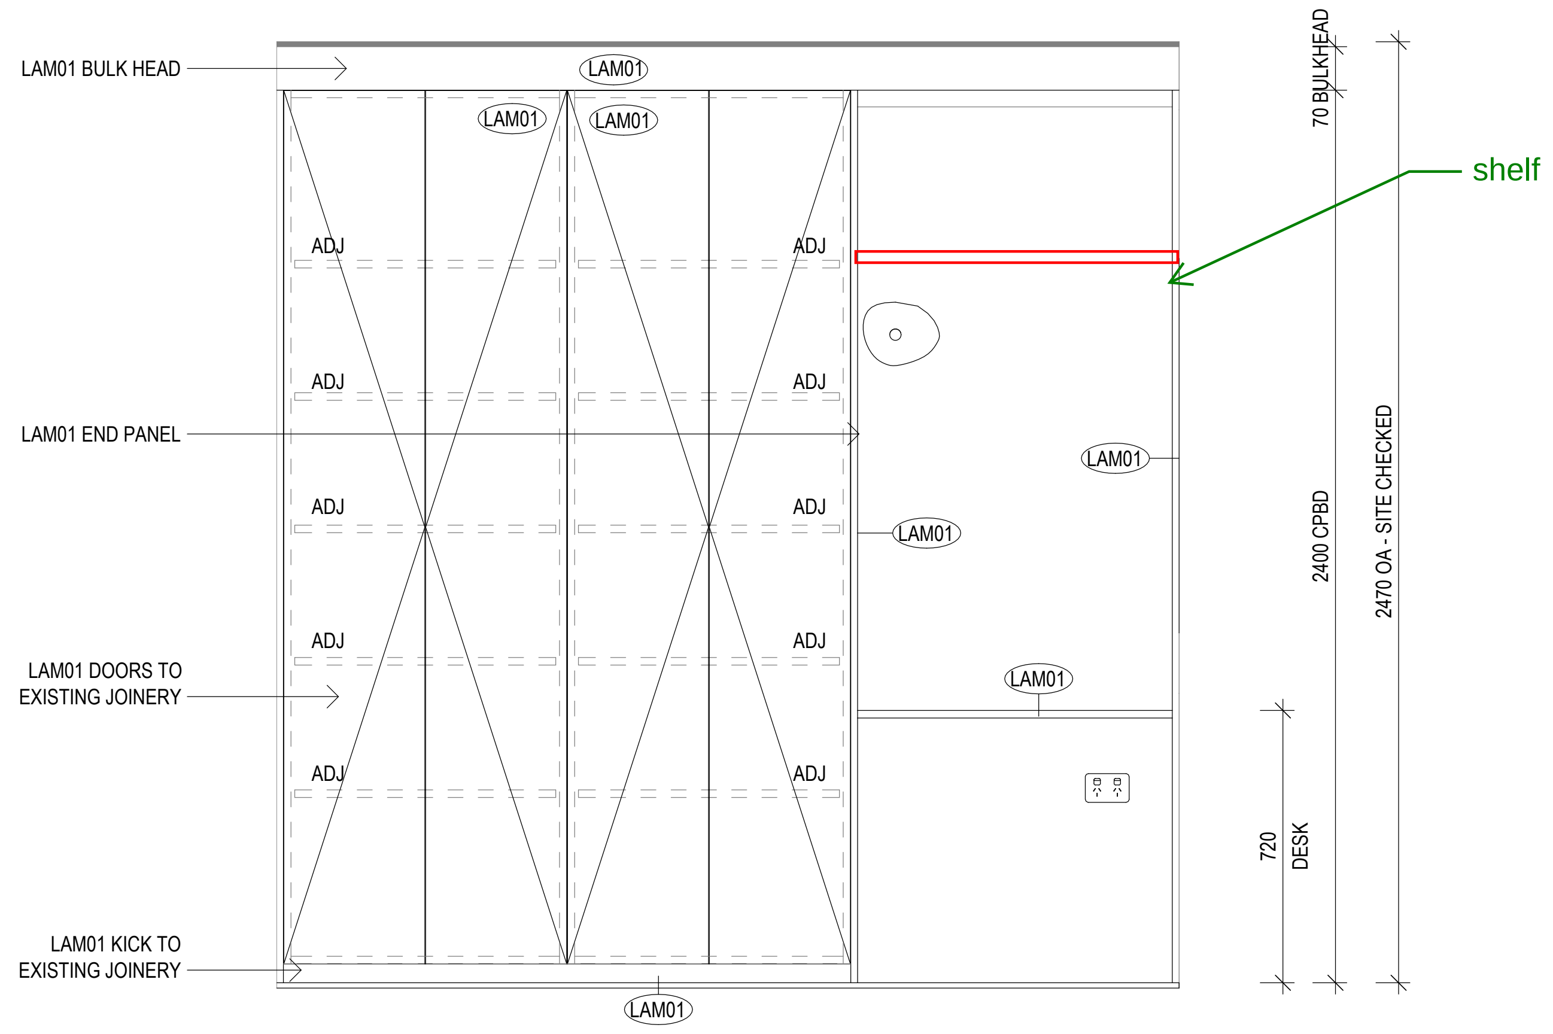

2
104
J07 (MIRRORED) - PLAYROOM JOINERY - ELEVATION
1 : 20

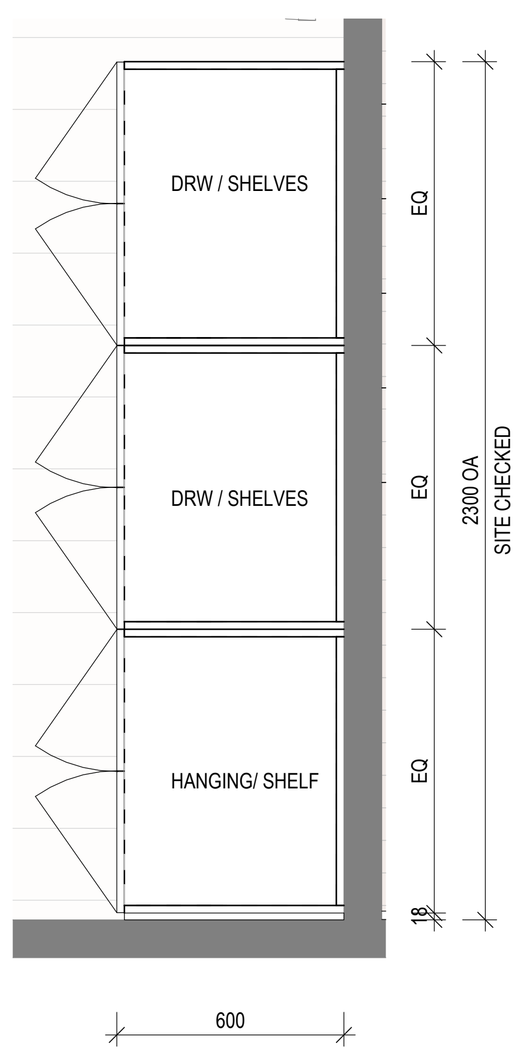

3
203
J09 - BED 1
1 : 20

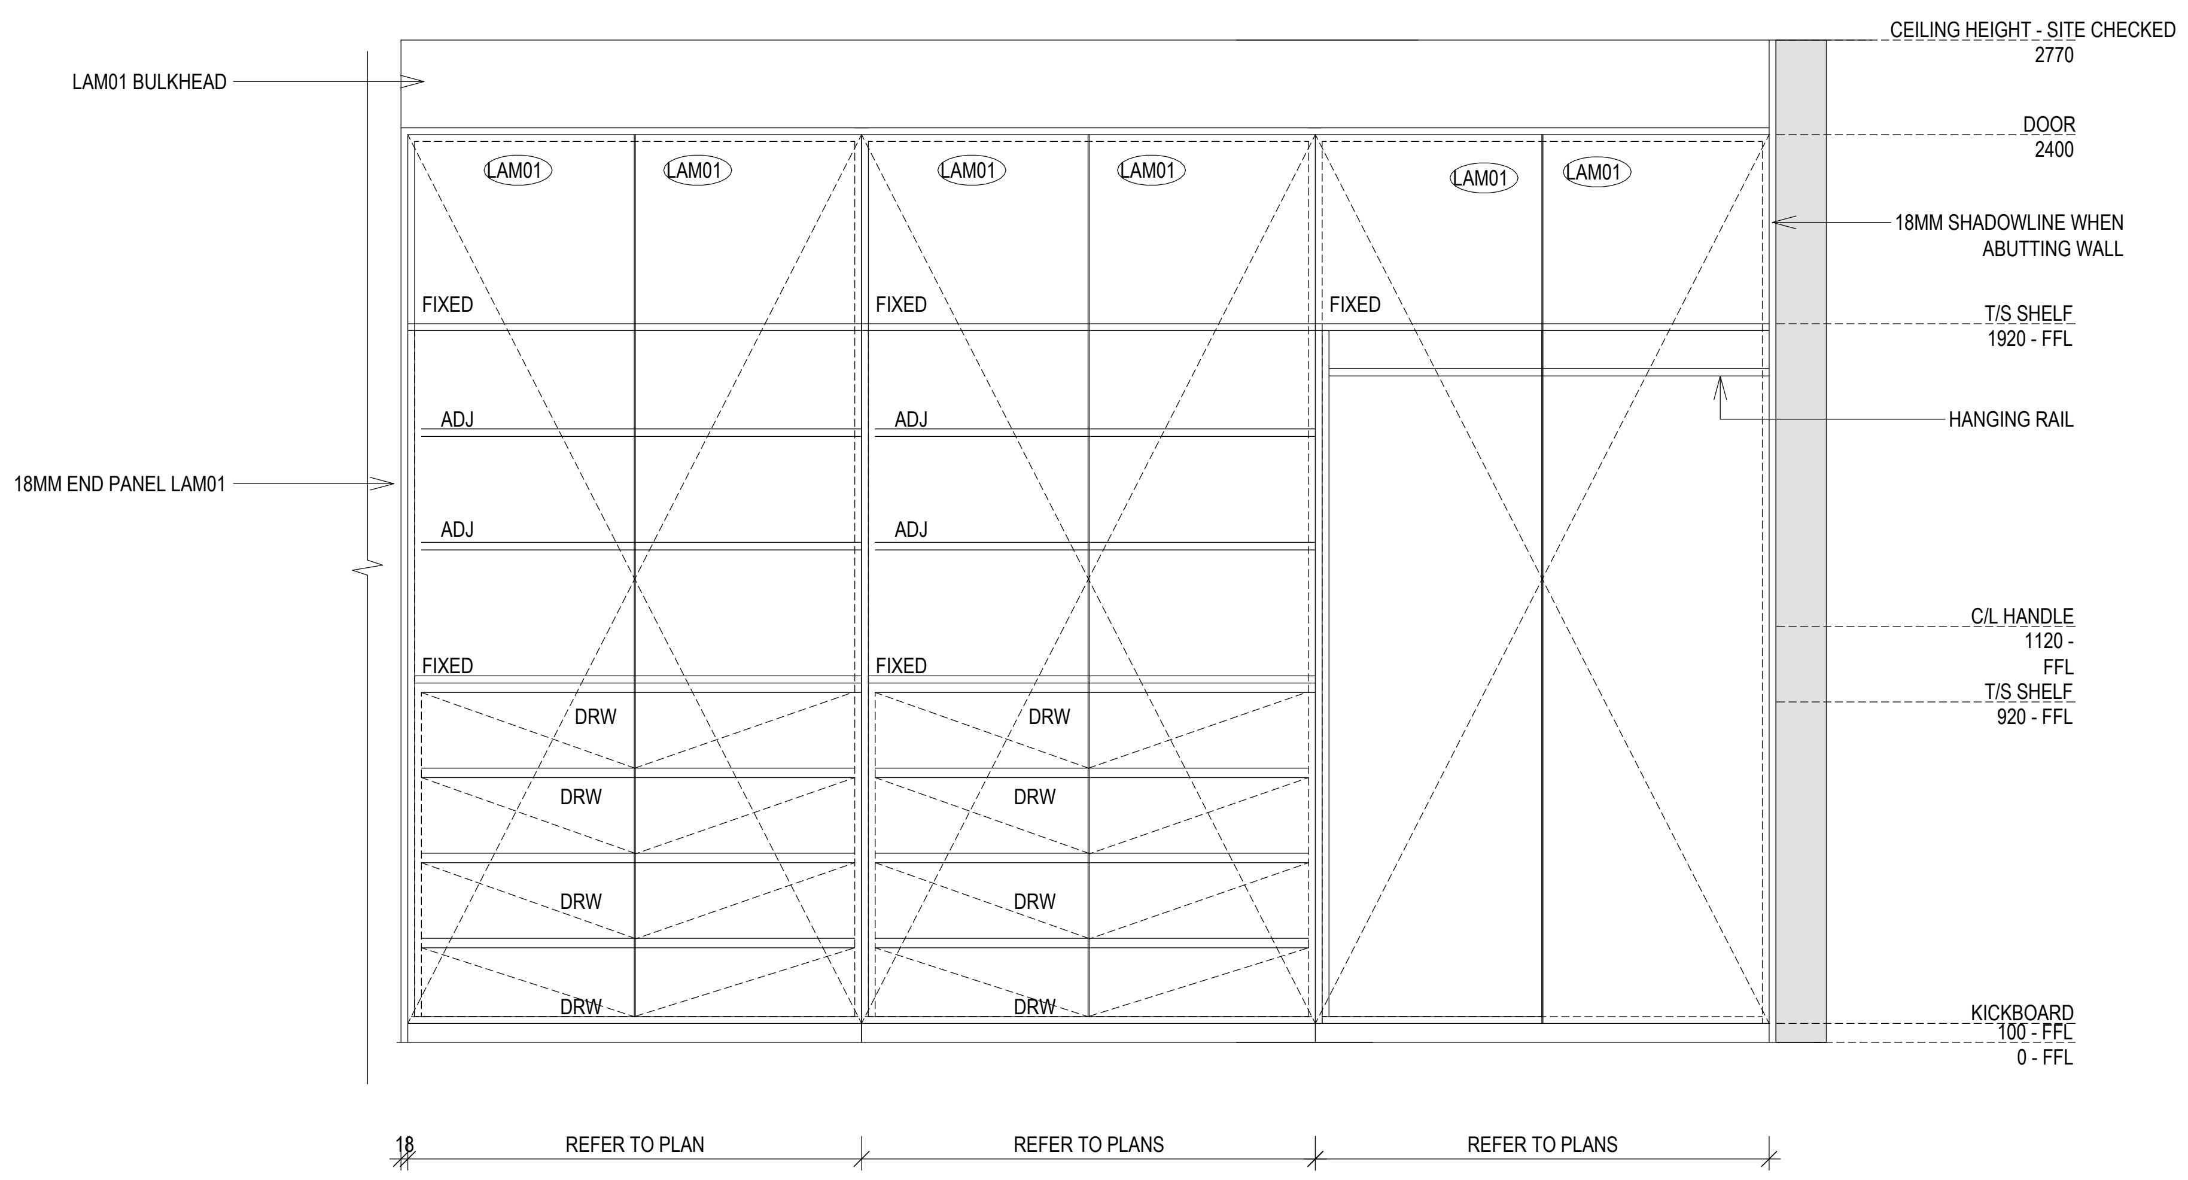

4
J09 - 2 CUPBOARD ROBE - ELEVATION
1 : 20

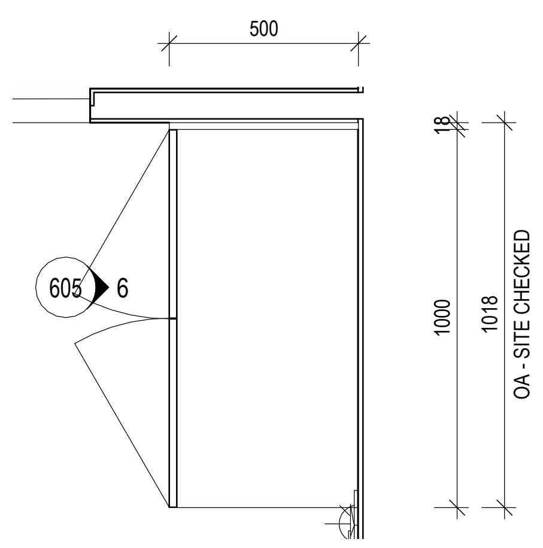

5
203
J12 -MASTER STORAGE
1 : 20

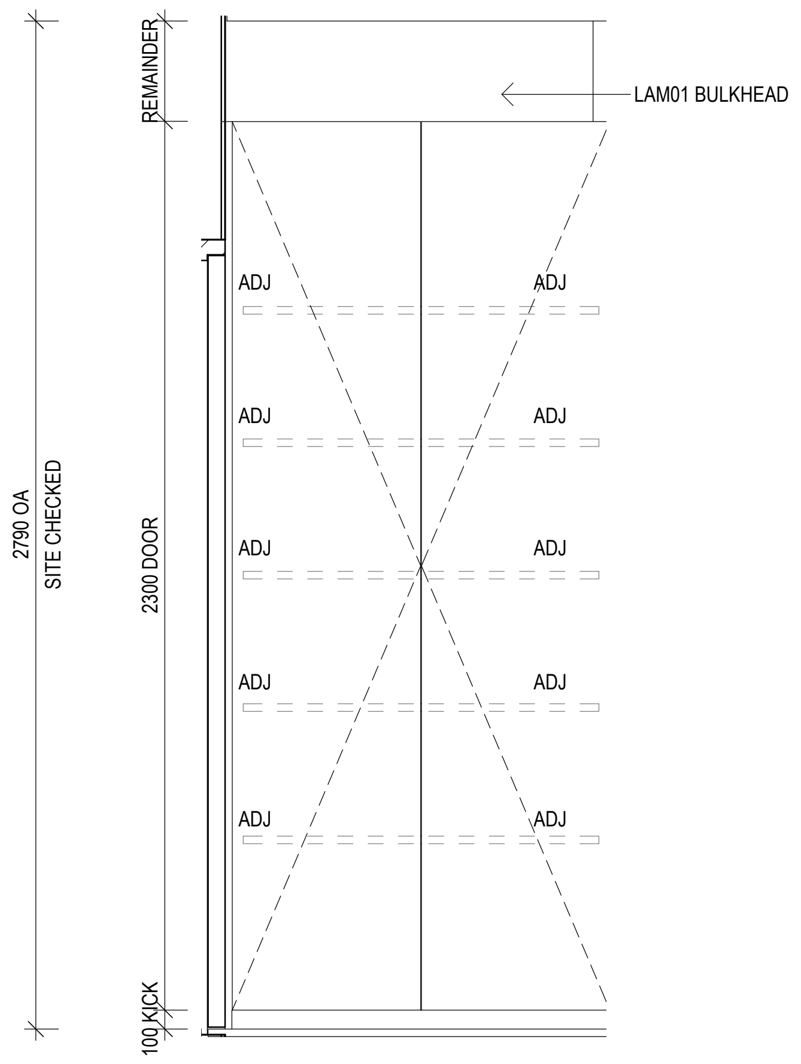

6
104
J12 - ELEVATION
1 : 20

28/09/2026 2:01:48 PM
C:\Users\KatherineB\OneDrive - nettletontribe\38 Howard\Revit\Concstruction\38 HOWARD_PROPOSED_ARCH (1).rvt

Client

Client Logo

Issue	Description	Date
A	JOINERY ISSUE 2	28-09-2026

Builder and/or subcontractors shall verify all project dimensions before commencing on-site work or off-site fabrication. Figured dimensions shall take precedence over scaled dimensions. This drawing is copyright and cannot be reproduced in whole or in part or by any medium without the written permission of Katherine Blackham.

Builder

Builders Logo

Project Name
38 Howard Street
Project Address
38 Howard Street, Grange QLD

Key Plan
0 2000 5000

Drawing Title:
JOINERY

Checker: **KB**
Sheet Size: **A1**
Scale: **1:20**
Drawing Number: **2025-01_605**
Issue: **A**