
Entry J01 Plan 1 : 20

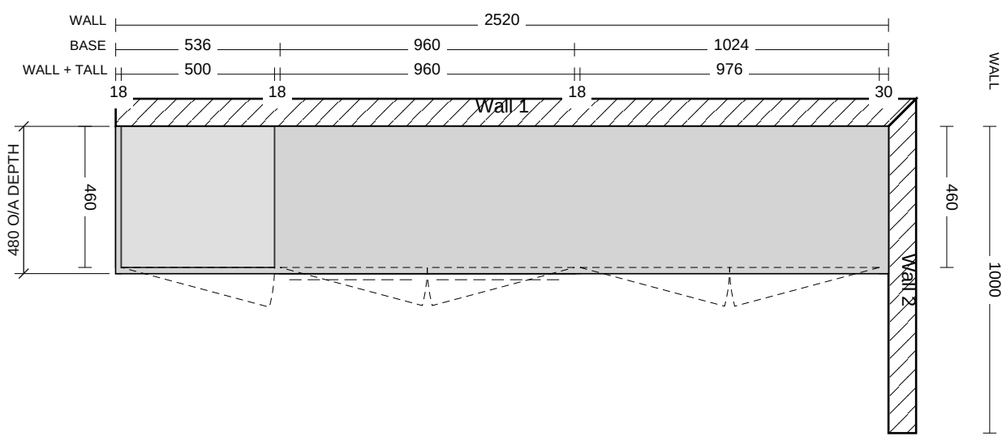

SPECIFICATIONS - Entry J01
RHK6581 Lee Smith

FRONTS + PANELS
Laminex 18mm ABS Grain - Elegant Oak
Panels: LX Abs Grain 18mm – Elegant Oak

HANDLES
Client supplied - undrilled

CARCASS
Internal: LX Colour 16mm – Paperbark


DRAWERS
Drawer box: DTC Dragon Pro - Whiteboard 16.5mm

HARDWARE
Hinges: Blum
Runners: DTC Dragon Pro – Silk White 400mm

Client Approved Signature : ..... Date : .....

Kitchens By Resident Hero 32 Gateway Drive Phone: 0754471077 mark@residenthero.com.au www.residenthero.com.au	RHK6581 Lee Smith	**Scale: 1 : 20**	**Sheet 1 of 3**
	Entry J01	Do not scale off this drawing.	Drawn By:
	38 Howard St, Grange QLD		Date: 02/11/26


Entry J01 Elevation Wall 1 1 : 20

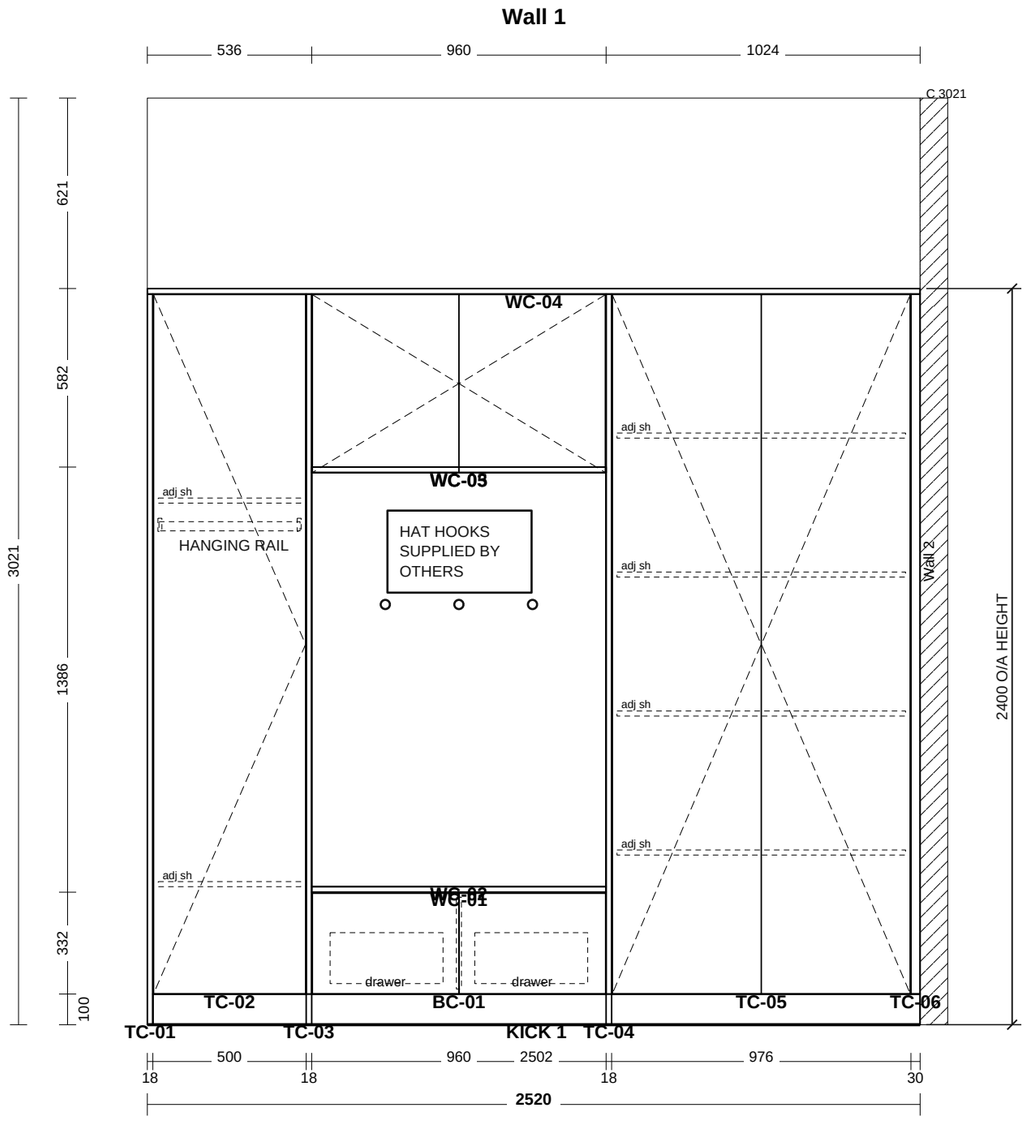


Client Approved Signature : ..... Date : .....

Kitchens By Resident Hero 32 Gateway Drive Phone: 0754471077 mark@residenthero.com.au www.residenthero.com.au	RHK6581 Lee Smith	**Scale: 1 : 20**	**Sheet 2 of 3**
	Entry J01	Do not scale off this drawing.	Drawn By:
	38 Howard St, Grange QLD		Date: 02/11/26

Entry J01 3D NTS

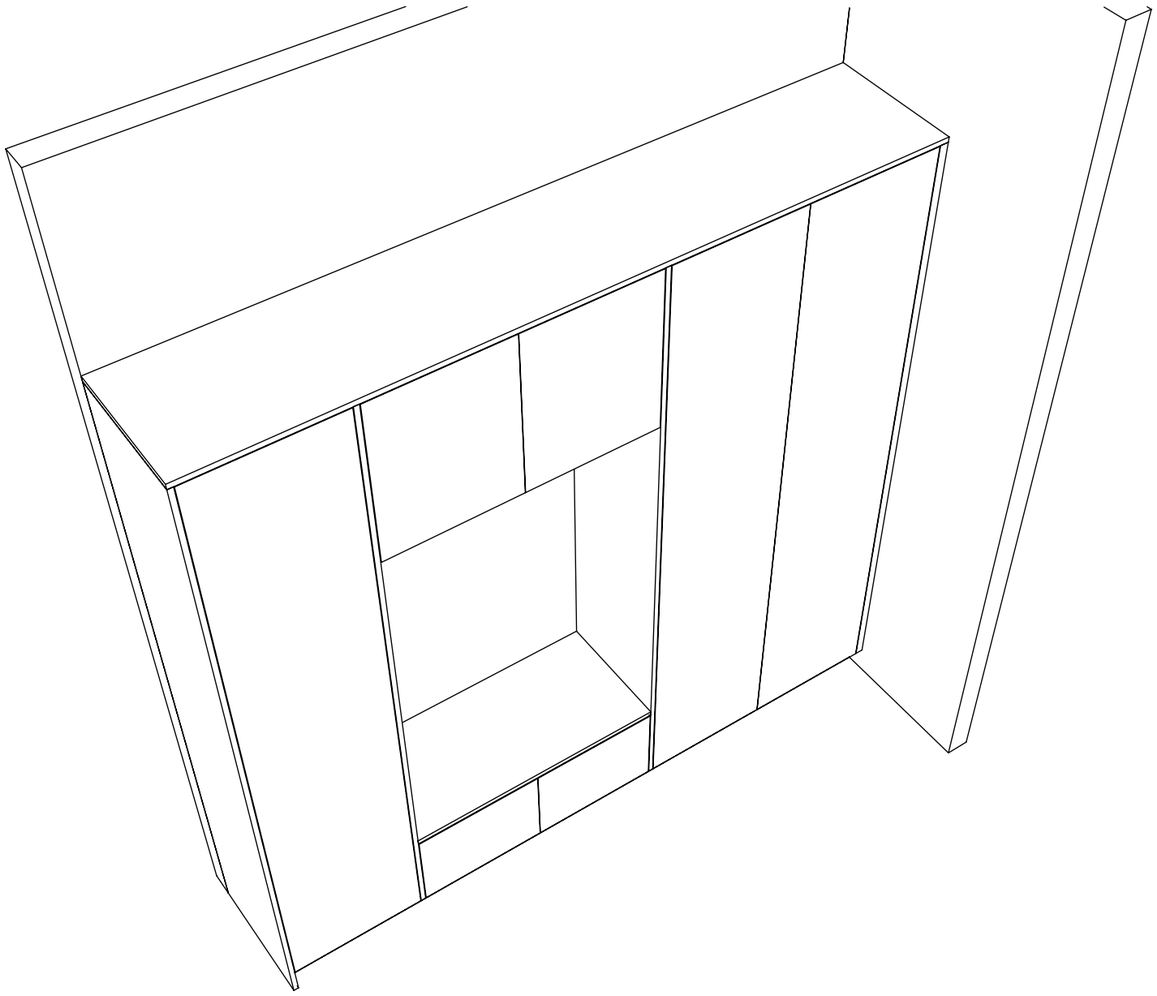


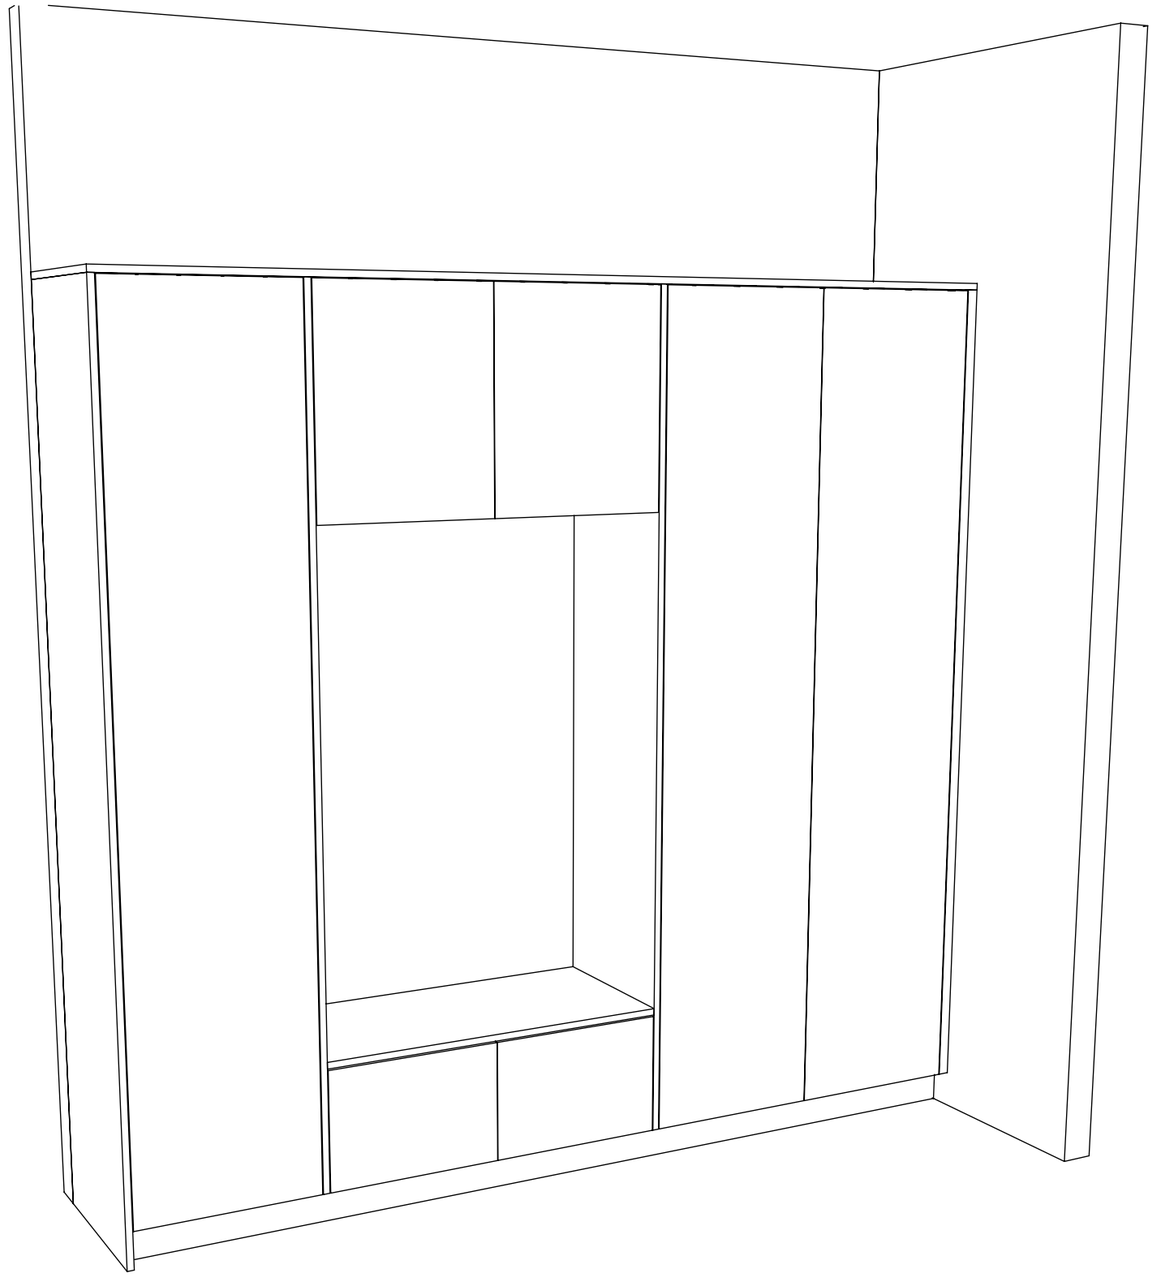

Client Approved Signature : ..... Date : .....

Kitchens By Resident Hero 32 Gateway Drive Phone: 0754471077 mark@residenthero.com.au www.residenthero.com.au	RHK6581 Lee Smith	**Scale: NTS**	**Sheet 3 of 3**
	Entry J01	Do not scale off this drawing.	Drawn By:
	38 Howard St, Grange QLD		Date: 02/11/26

Laundry J02 Plan 1 : 20

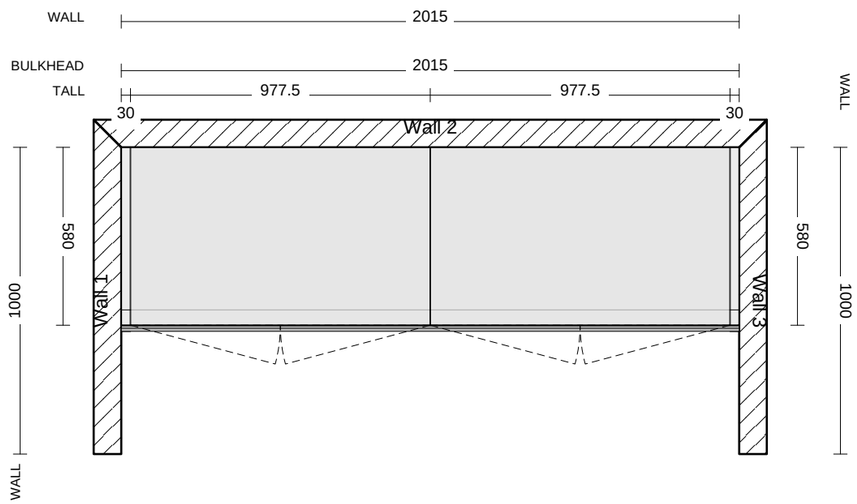

SPECIFICATIONS - Laundry J02
RHK6581 Lee Smith

FRONTS + PANELS
Laminex 18mm ABS Grain - Elegant Oak
Panels: LX Abs Grain 18mm – Elegant Oak

HANDLES
Client supplied - undrilled


CARCASS
Internal: Whiteboard 16.5mm

HARDWARE
Hinges: Blum

Client Approved Signature : ..... Date : .....

Kitchens By Resident Hero 32 Gateway Drive Phone: 0754471077 mark@residenthero.com.au www.residenthero.com.au	RHK6581 Lee Smith	**Scale: 1 : 20**	**Sheet 1 of 3**
	Laundry J02	Do not scale off this drawing.	Drawn By:
	38 Howard St, Grange QLD		Date: 02/11/26


Laundry J02 Elevation Wall 2 1 : 20

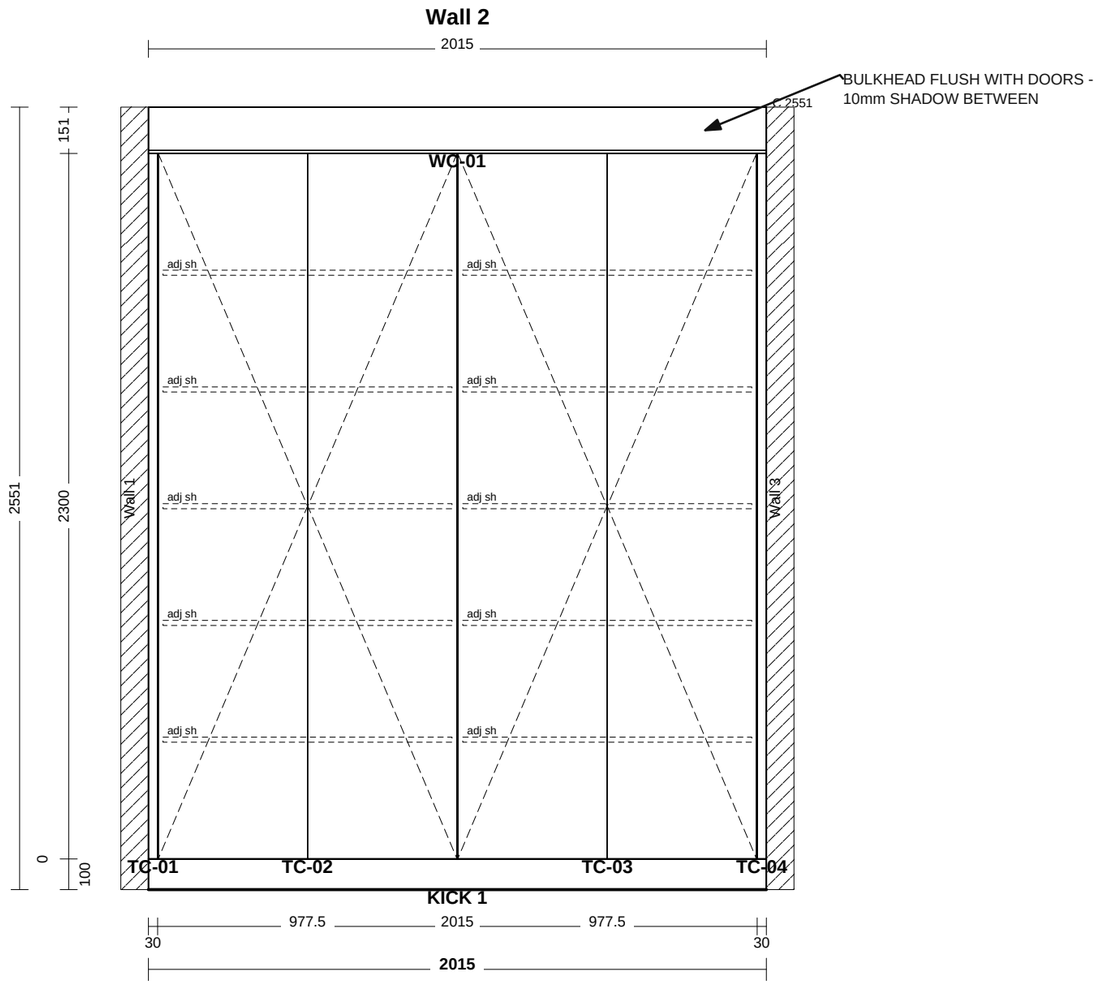


Client Approved Signature : ..... Date : .....

Kitchens By Resident Hero 32 Gateway Drive Phone: 0754471077 mark@residenthero.com.au www.residenthero.com.au	RHK6581 Lee Smith	**Scale: 1 : 20**	**Sheet 2 of 3**
	Laundry J02	Do not scale off this drawing.	Drawn By:
	38 Howard St, Grange QLD		Date: 02/11/26

Laundry J02 3D NTS

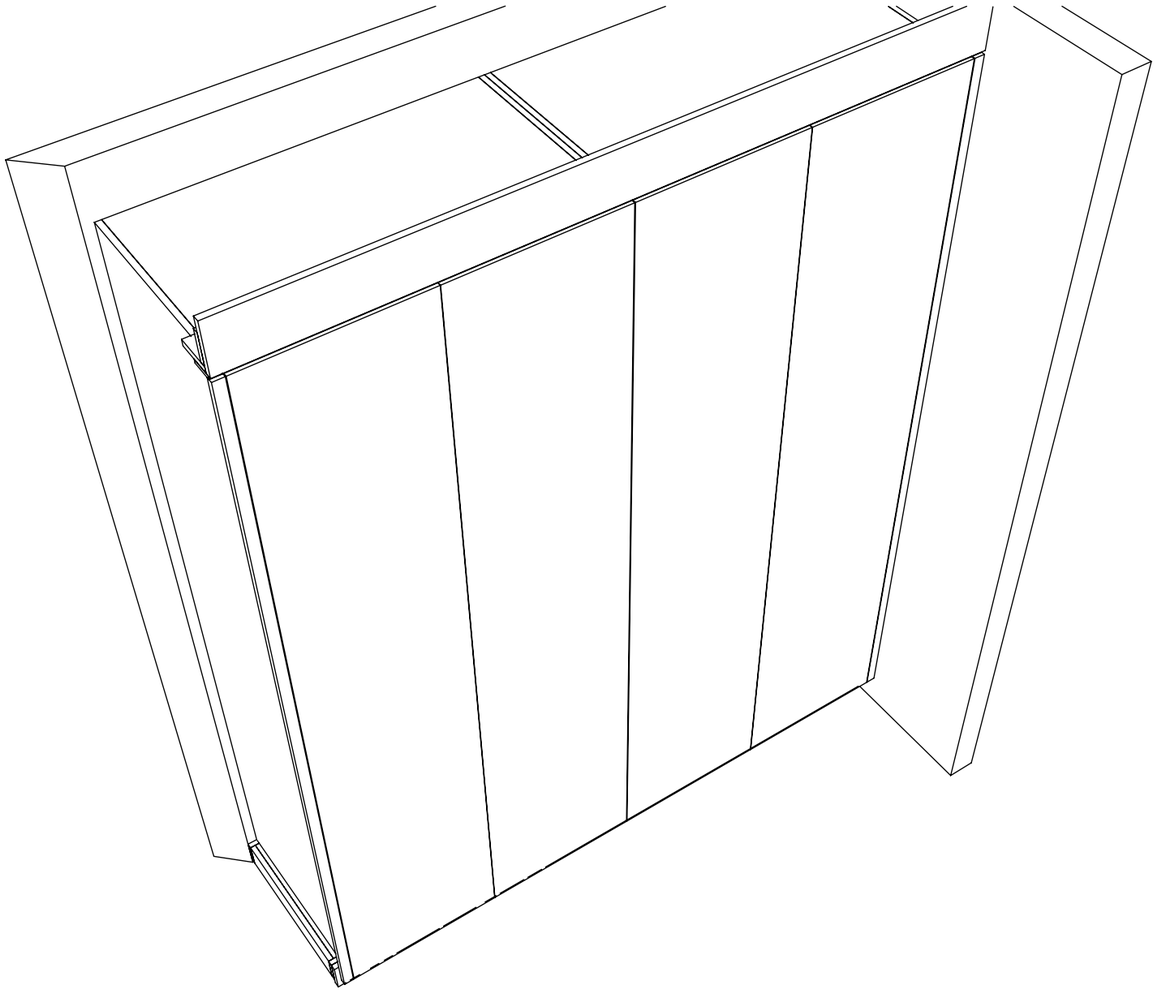


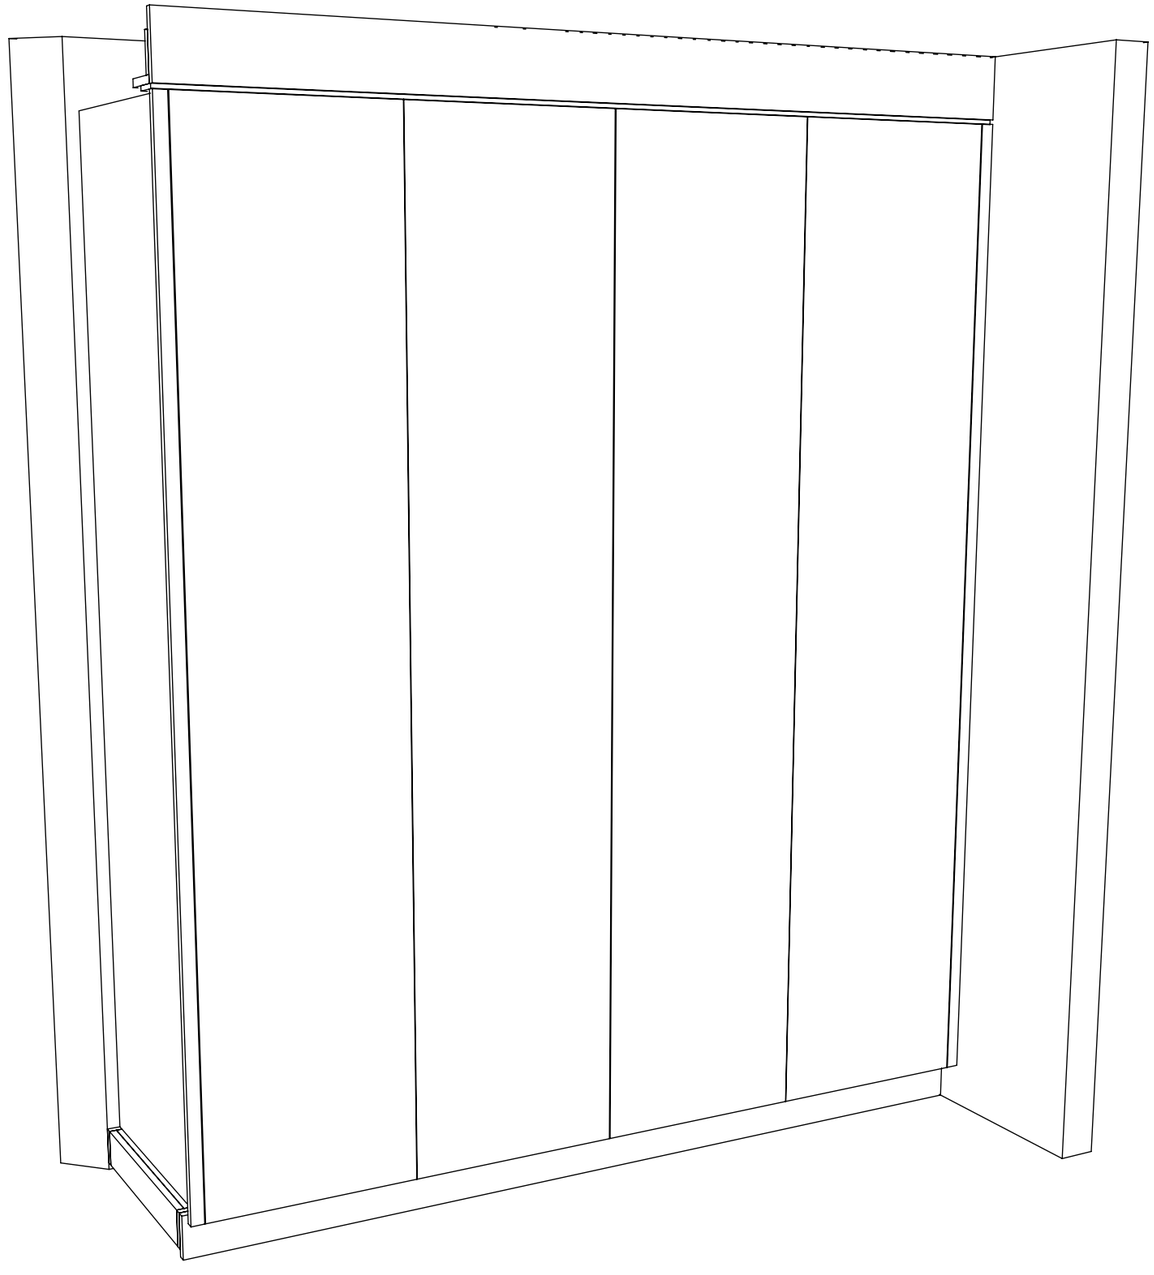

Client Approved Signature : ..... Date : .....

Kitchens By Resident Hero 32 Gateway Drive Phone: 0754471077 mark@residenthero.com.au www.residenthero.com.au	RHK6581 Lee Smith	**Scale: NTS**	**Sheet 3 of 3**
	Laundry J02	Do not scale off this drawing.	Drawn By:
	38 Howard St, Grange QLD		Date: 02/11/26

Laundry J03 Plan 1 : 20

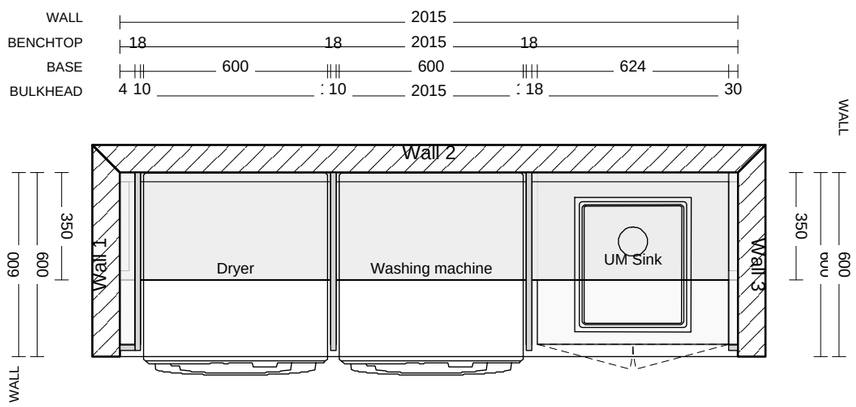

SPECIFICATIONS - Laundry J03
RHK6581 Lee Smith

BENCHTOP
By others

FRONTS + PANELS
Laminex 18mm ABS Grain - Elegant Oak
Panels: LX Abs Grain 18mm – Elegant Oak

HANDLES
Client supplied - undrilled

CARCASS
Internal: Whiteboard 16.5mm

DRAWERS
Drawer box: DTC Dragon Pro


HARDWARE
Hinges: Blum
Runners: DTC Dragon Pro – Silk White

SINK
U/Mount Sink

Client Approved Signature : ..... Date : .....

Kitchens By Resident Hero 32 Gateway Drive Phone: 0754471077 mark@residenthero.com.au www.residenthero.com.au	RHK6581 Lee Smith	**Scale: 1 : 20**	**Sheet 1 of 3**
	Laundry J03	Do not scale off this drawing.	Drawn By:
	38 Howard St, Grange QLD		Date: 02/11/26


Laundry J03 Elevation Wall 2 1 : 20

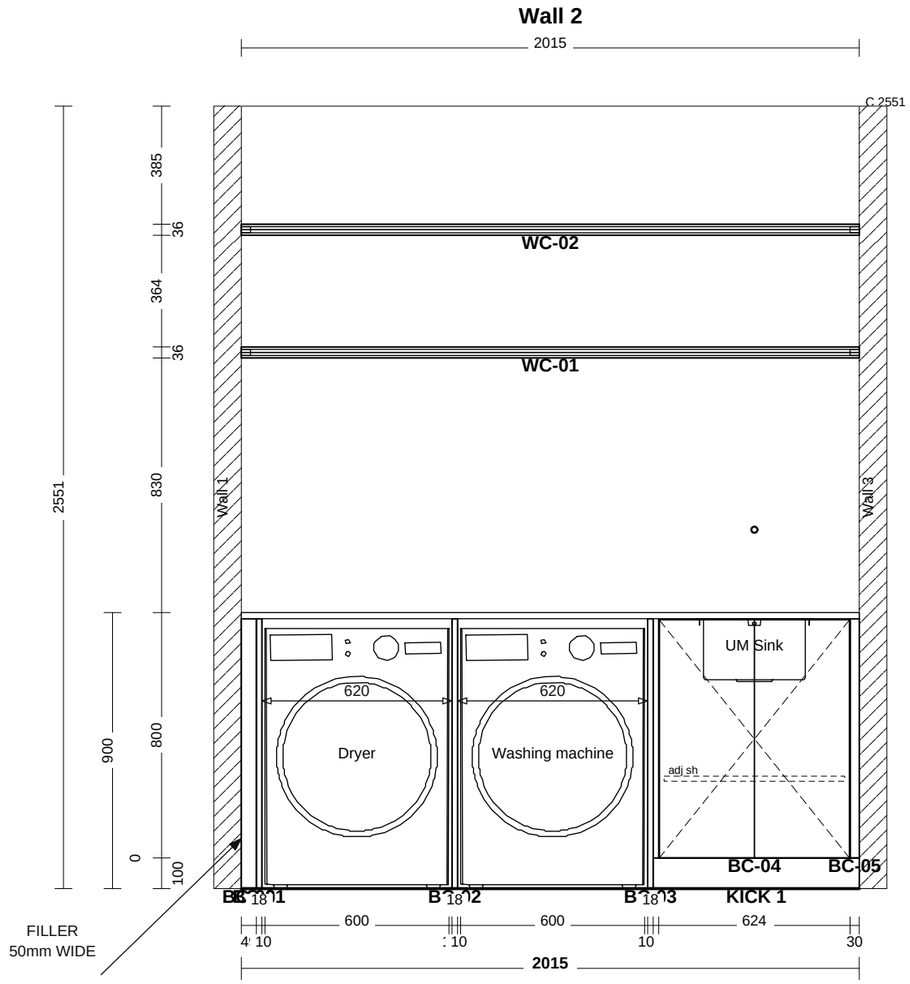


Client Approved Signature : ..... Date : .....

Kitchens By Resident Hero 32 Gateway Drive Phone: 0754471077 mark@residenthero.com.au www.residenthero.com.au	RHK6581 Lee Smith	**Scale: 1 : 20**	**Sheet 2 of 3**
	Laundry J03	Do not scale off this drawing.	Drawn By:
	38 Howard St, Grange QLD		Date: 02/11/26

Laundry J03 3D NTS

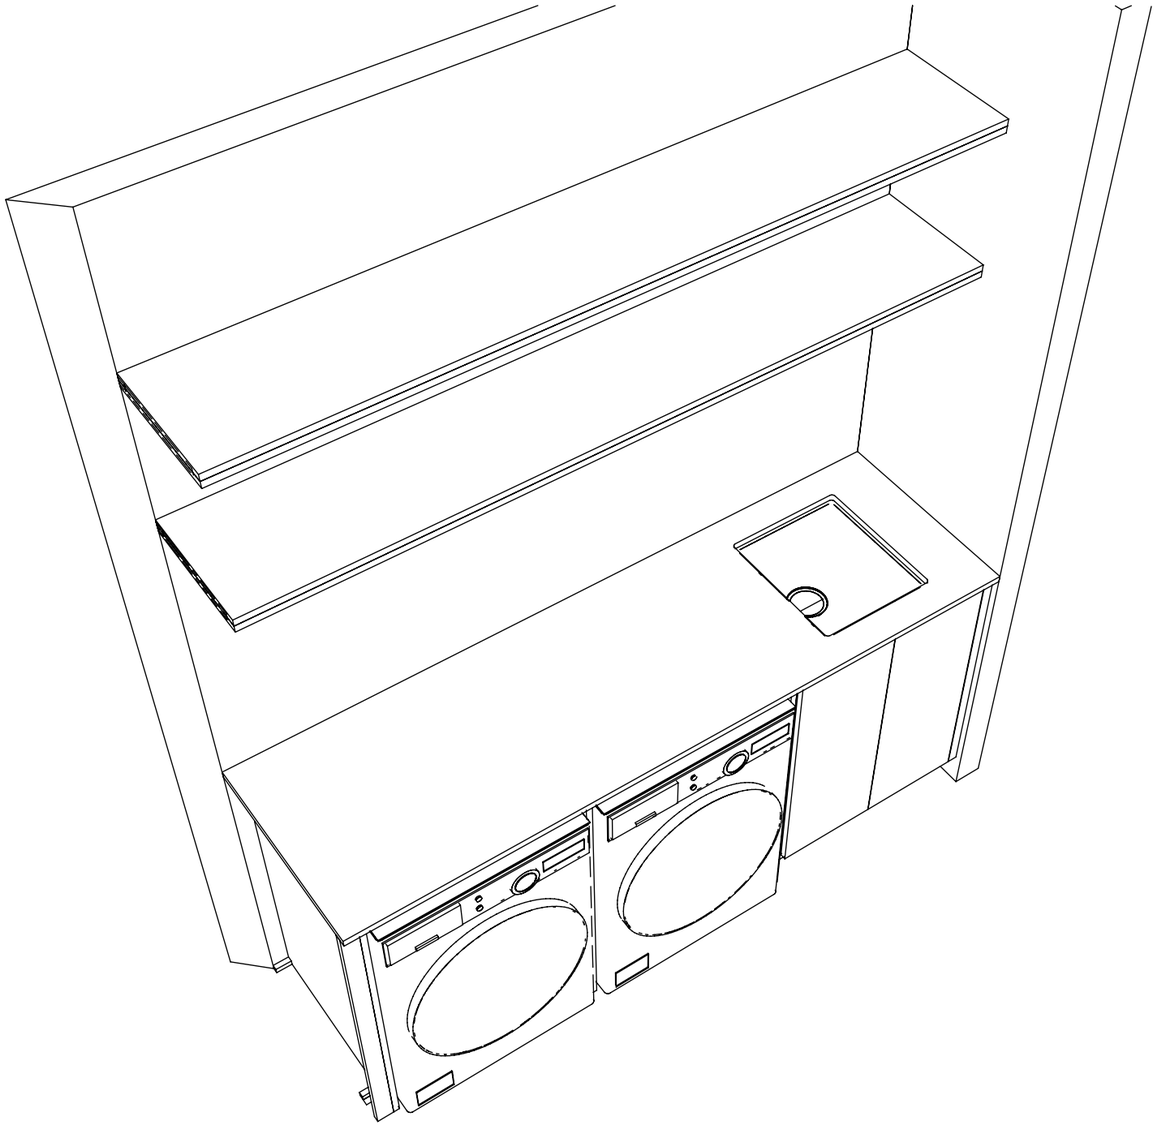

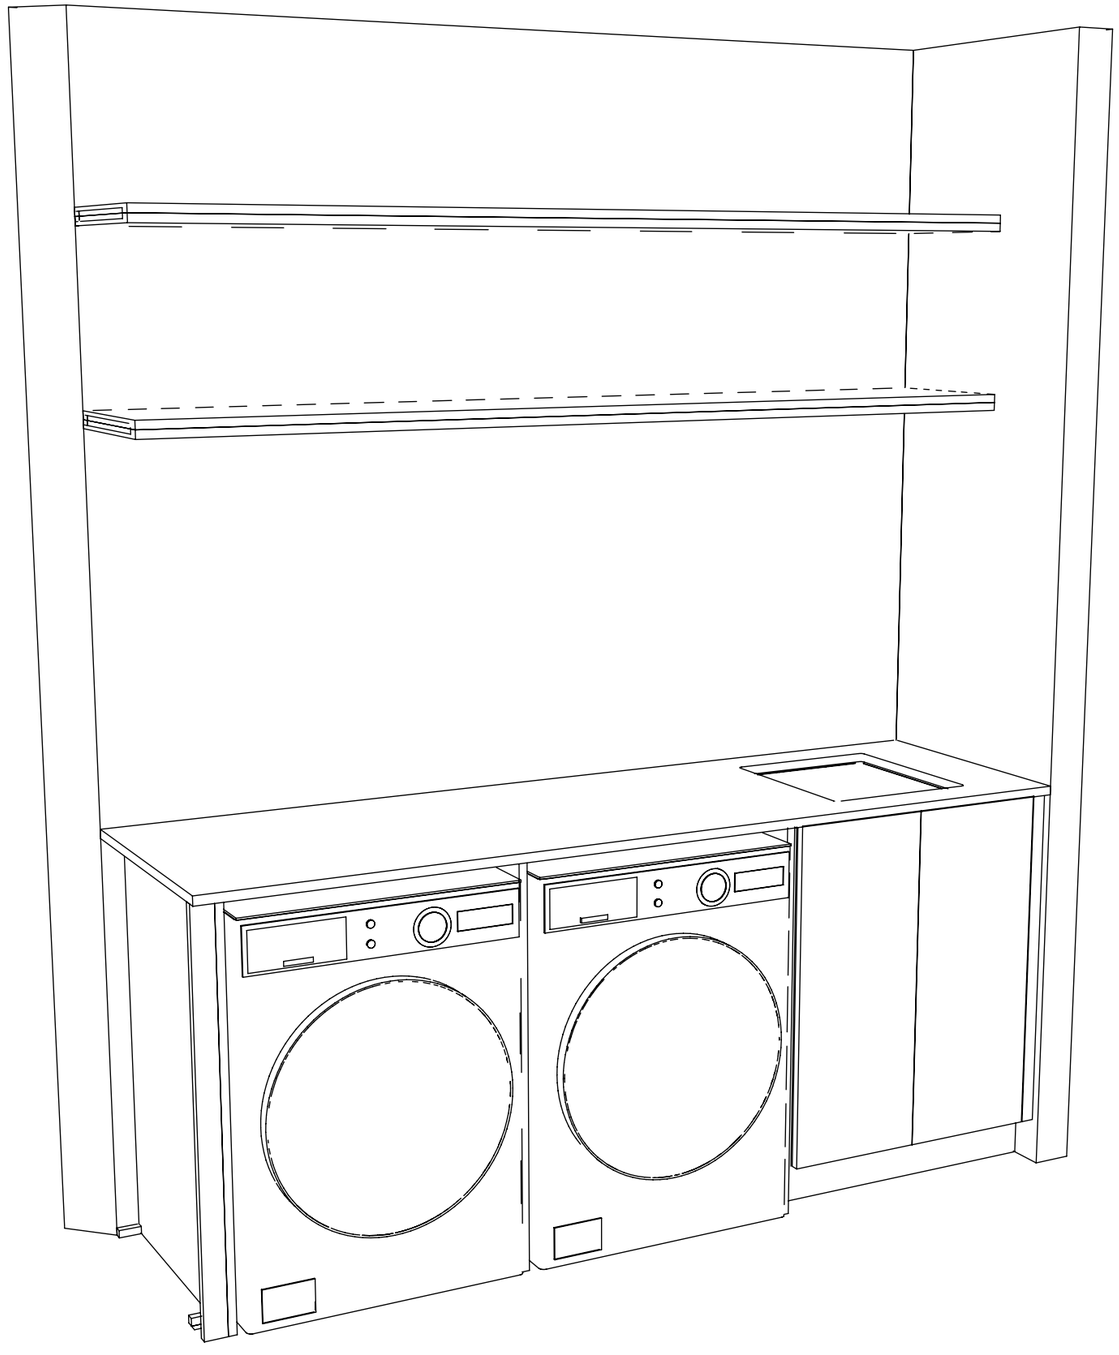

Client Approved Signature : ..... Date : .....

Kitchens By Resident Hero 32 Gateway Drive Phone: 0754471077 mark@residenthero.com.au www.residenthero.com.au	RHK6581 Lee Smith	**Scale: NTS**	**Sheet 3 of 3**
	Laundry J03	Do not scale off this drawing.	Drawn By:
	38 Howard St, Grange QLD		Date: 02/11/26

SPECIFICATIONS - Kitchen J05 + Butler's J04
RHK6581 Lee Smith

FRONTS + PANELS
Laminex 18mm ABS Grain - Elegant Oak
Panels: LX Abs Grain 18mm – Elegant Oak, Whiteboard 16.5mm

HANDLES
Linear sharknose strip 35

CARCASS
Internal: Whiteboard 16.5mm

DRAWERS
Drawer box: DTC Dragon Pro - Whiteboard 16.5mm

HARDWARE
Hinges: Blum
Runners: DTC Dragon Pro – Silk White 500mm
Bin: Nikpol Teramo 74L

APPLIANCES + SINKS - Kitchen J05 + Butler's J04
RHK6581 Lee Smith

SINK
Mondella double bowl U/M sink 760 (Bunnings 1056993)

TAPWARE
Yabby Sydney Round kitchen mixer - antique brass

OVENS
Miele H 2861 BP oven 60cm (black)
Miele H 7240 BM combi microwave (black)

COOKTOP
Miele KM 7373 FL induction cooktop 800 (surface mount)

BIN
Nikpol Teramo 74L


Client Approved Signature : ..... Date : .....

Kitchens By Resident Hero
32 Gateway Drive
Phone: 0754471077
mark@residenthero.com.au
www.residenthero.com.au

RHK6581 Lee Smith	**Scale: NTS**	**Sheet 1 of 9**
Kitchen J05 + Butler's J04	Do not scale off this drawing.	Drawn By:
38 Howard St, Grange QLD		Date: 02/11/26

Kitchen J05 + Butler's J04 Plan

1 : 20

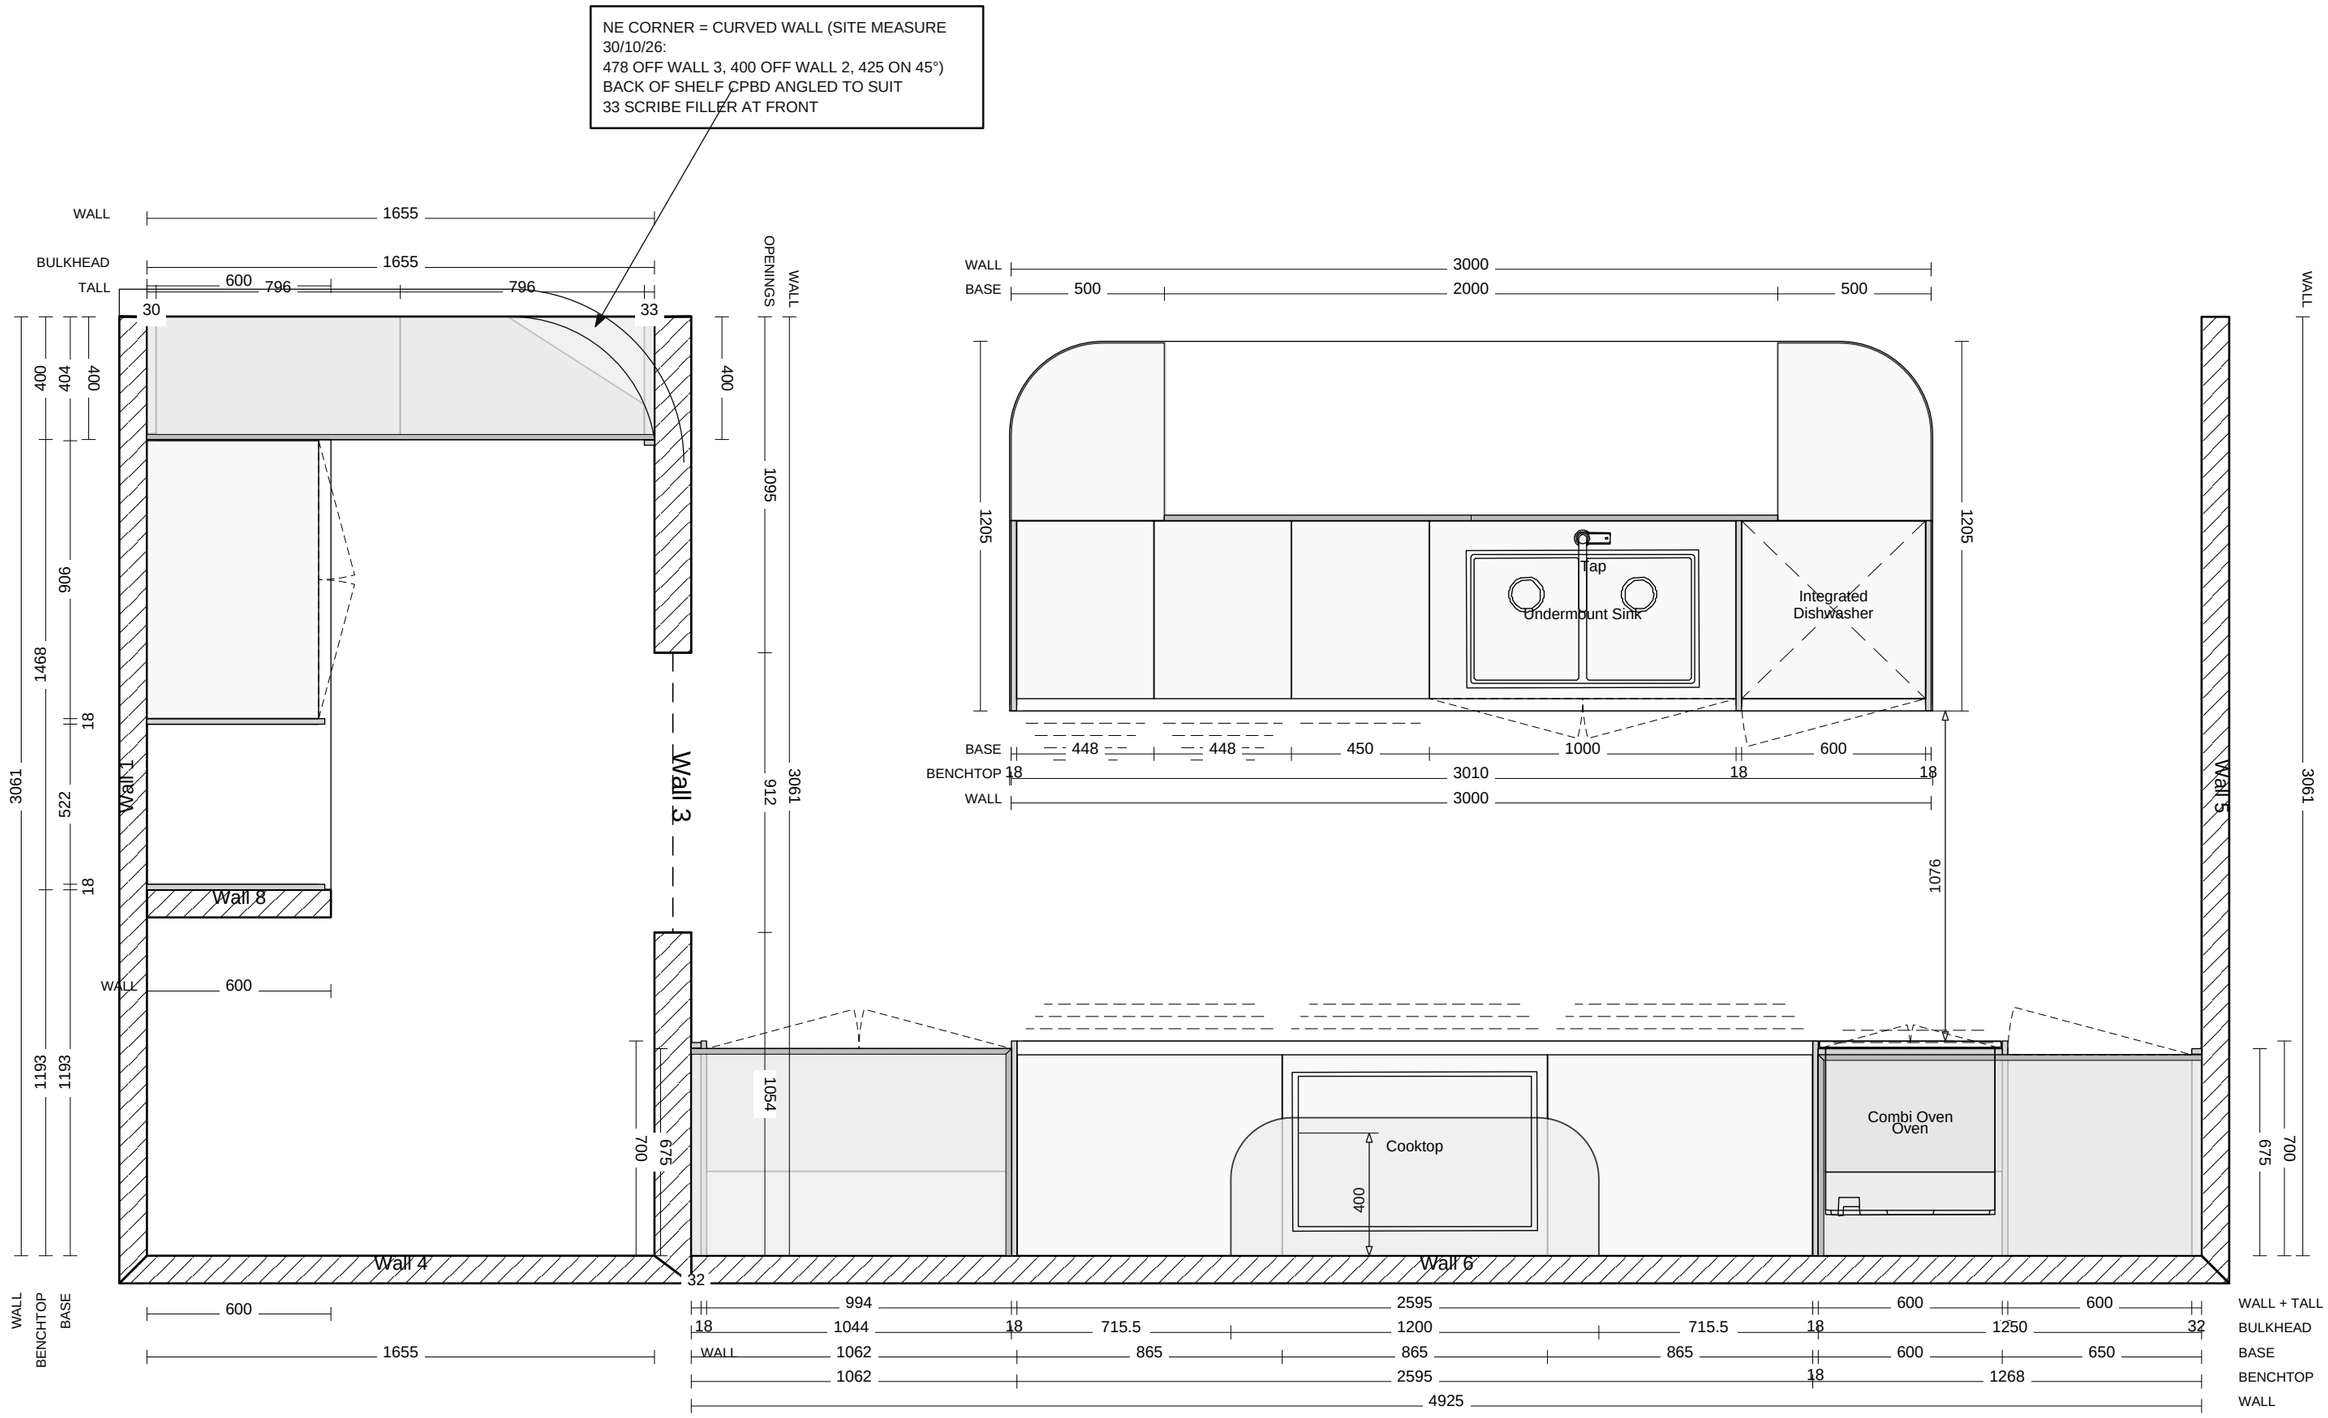


Client Approved Signature : ..... Date : .....

Kitchens By Resident Hero 32 Gateway Drive Phone: 0754471077 mark@residenthero.com.au www.residenthero.com.au	RHK6581 Lee Smith	**Scale: 1 : 20**	**Sheet 2 of 9**
	Kitchen J05 + Butler's J04	Do not scale off this drawing.	Drawn By:
	38 Howard St, Grange QLD		Date: 02/11/26

Kitchen J05 + Butler's J04 Elevation Wall 1

1 : 20

Wall 1

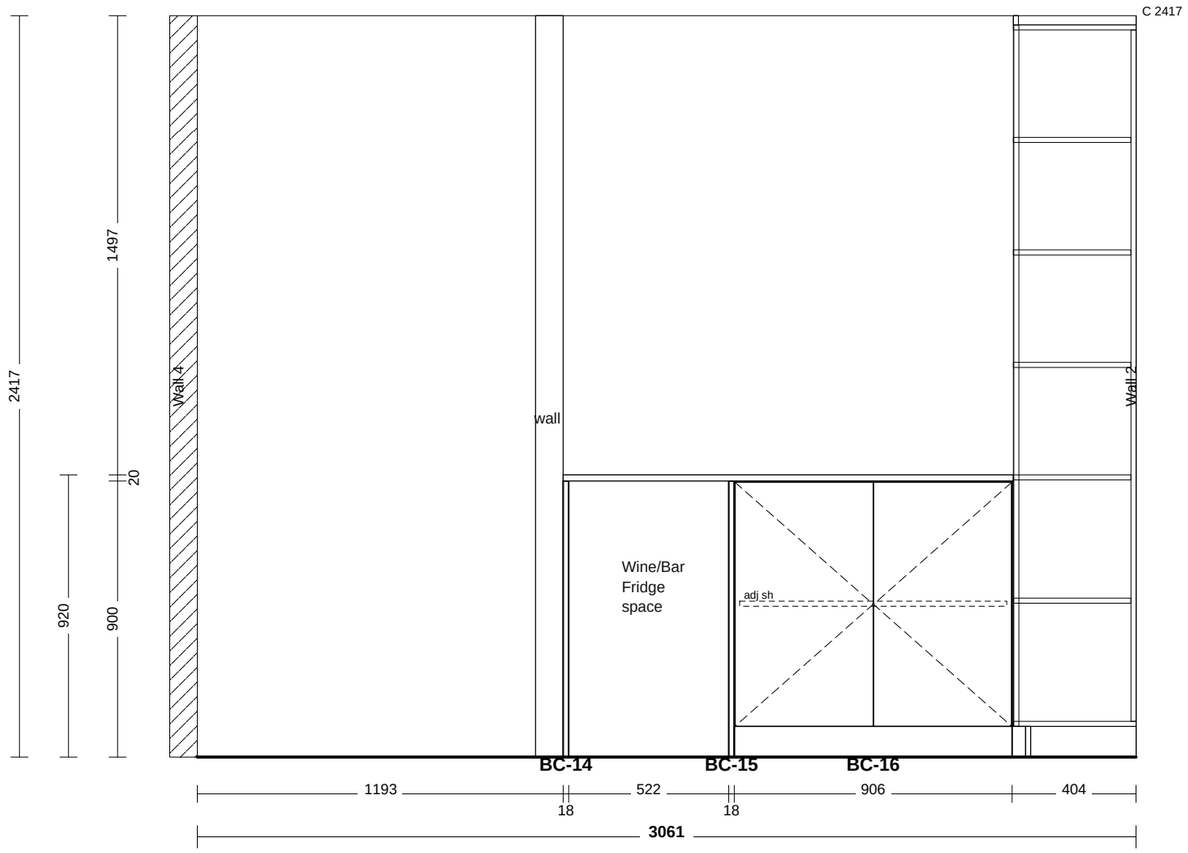


Client Approved Signature : ..... Date : .....

Kitchens By Resident Hero 32 Gateway Drive Phone: 0754471077 mark@residenthero.com.au www.residenthero.com.au	RHK6581 Lee Smith	**Scale: 1 : 20**	**Sheet 3 of 9**
	Kitchen J05 + Butler's J04	Do not scale off this drawing.	Drawn By:
	38 Howard St, Grange QLD		Date: 02/11/26

Kitchen J05 + Butler's J04 Elevation Wall 2

1 : 20

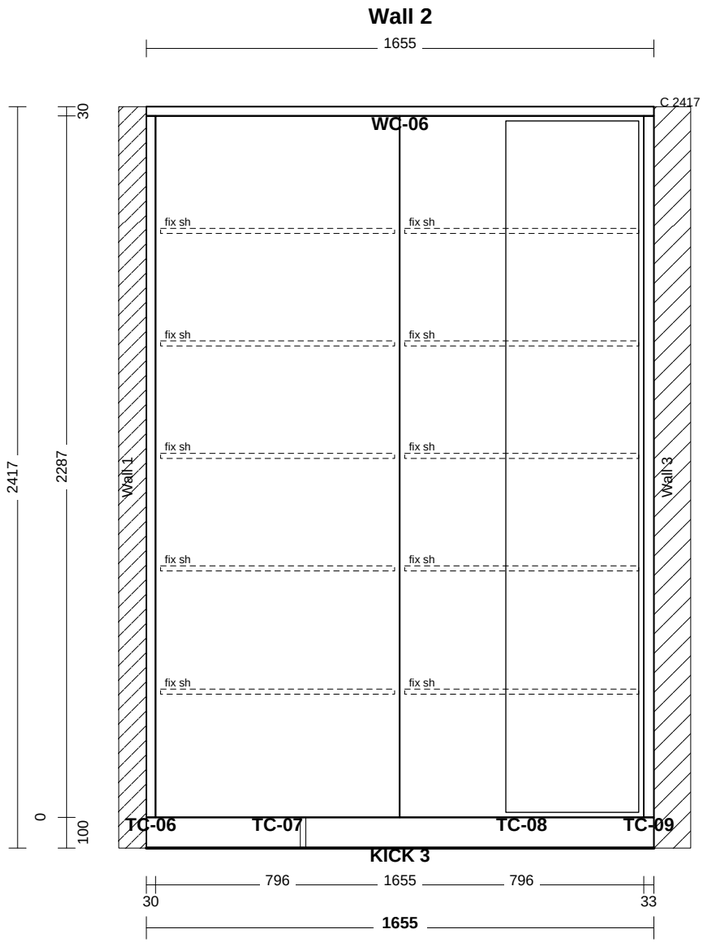


Client Approved Signature : ..... Date : .....

Kitchens By Resident Hero 32 Gateway Drive Phone: 0754471077 mark@residenthero.com.au www.residenthero.com.au	RHK6581 Lee Smith	**Scale: 1 : 20**	**Sheet 4 of 9**
	Kitchen J05 + Butler's J04	Do not scale off this drawing.	Drawn By:
	38 Howard St, Grange QLD		Date: 02/11/26

Kitchen J05 + Butler's J04 Elevation Wall 6

1 : 20

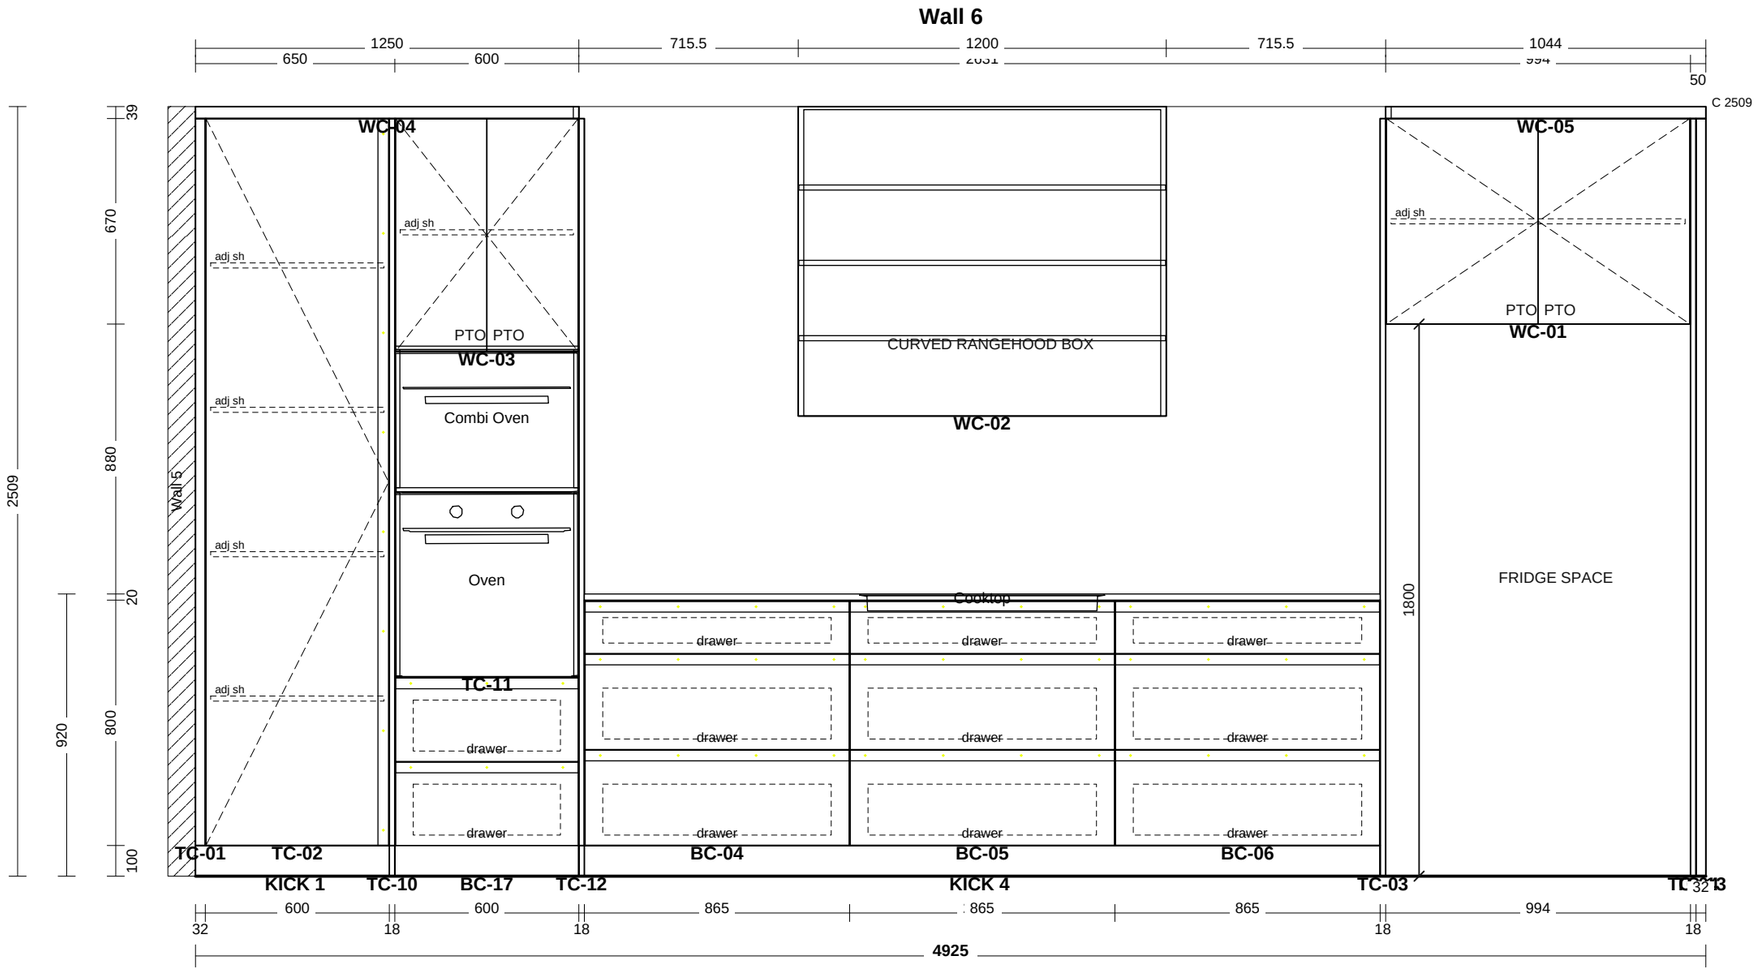


Client Approved Signature : ..... Date : .....

Kitchens By Resident Hero 32 Gateway Drive Phone: 0754471077 mark@residenthero.com.au www.residenthero.com.au	RHK6581 Lee Smith	**Scale: 1 : 20**	**Sheet 5 of 9**
	Kitchen J05 + Butler's J04	Do not scale off this drawing.	Drawn By:
	38 Howard St, Grange QLD		Date: 02/11/26

Kitchen J05 + Butler's J04 Elevation Wall 7


1 : 20

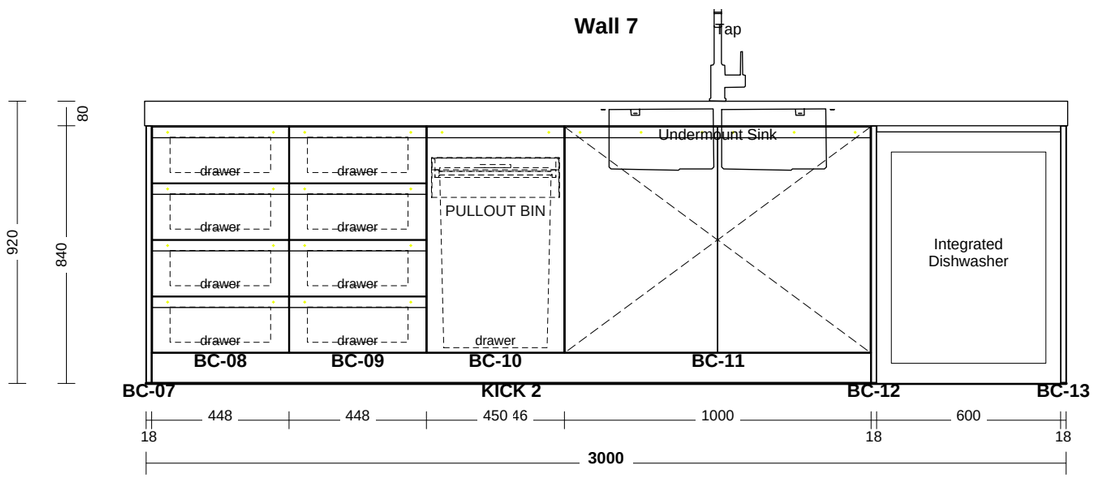


Client Approved Signature : ..... Date : .....

Kitchens By Resident Hero 32 Gateway Drive Phone: 0754471077 mark@residenthero.com.au www.residenthero.com.au	RHK6581 Lee Smith	**Scale: 1 : 20**	**Sheet 6 of 9**
	Kitchen J05 + Butler's J04	Do not scale off this drawing.	Drawn By:
	38 Howard St, Grange QLD		Date: 02/11/26

Kitchen J05 + Butler's J04 3D NTS

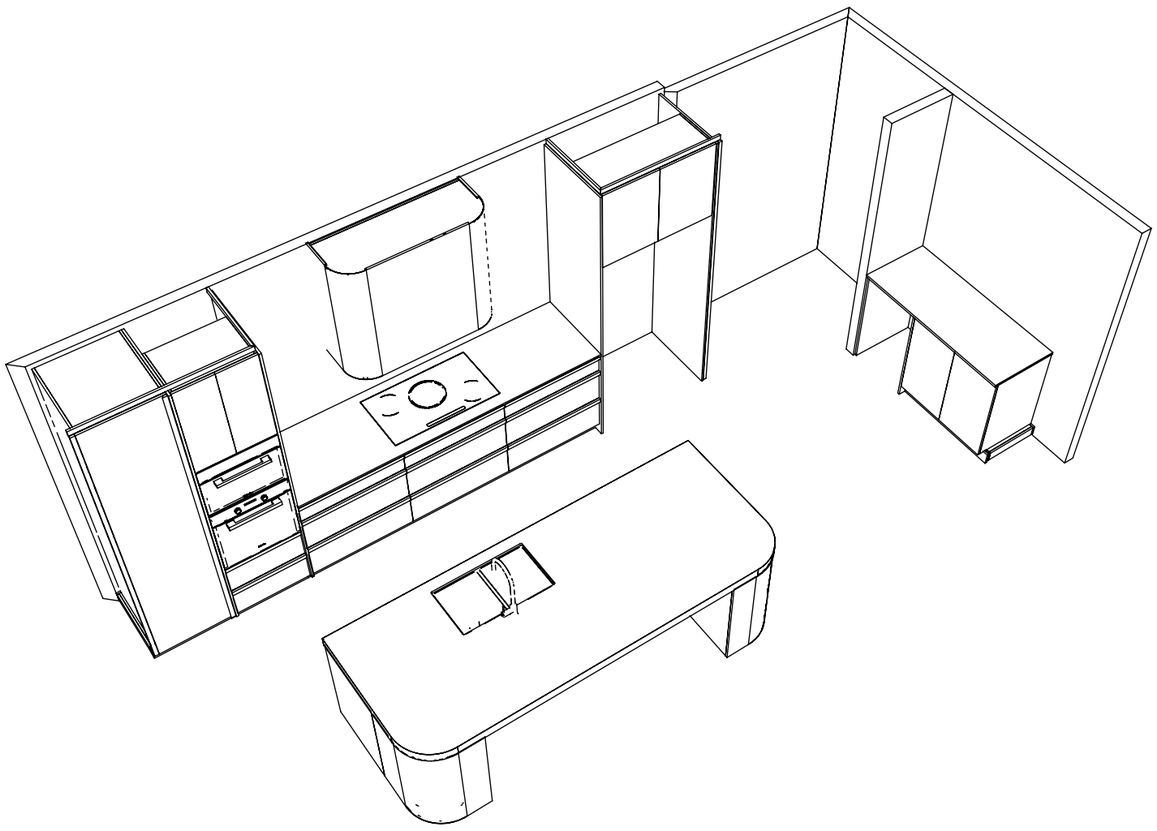


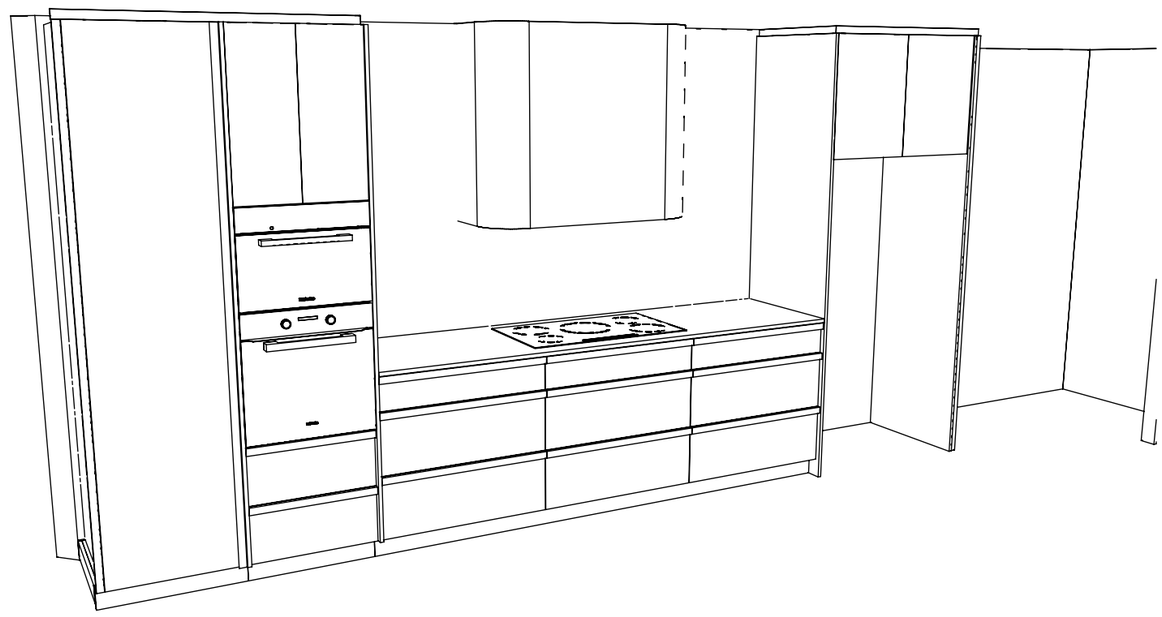

Client Approved Signature : ..... Date : .....

Kitchens By Resident Hero 32 Gateway Drive Phone: 0754471077 mark@residenthero.com.au www.residenthero.com.au	RHK6581 Lee Smith	**Scale: NTS**	**Sheet 7 of 9**
	Kitchen J05 + Butler's J04	Do not scale off this drawing.	Drawn By:
	38 Howard St, Grange QLD		Date: 02/11/26


Kitchen J05 + Butler's J04 3D NTS

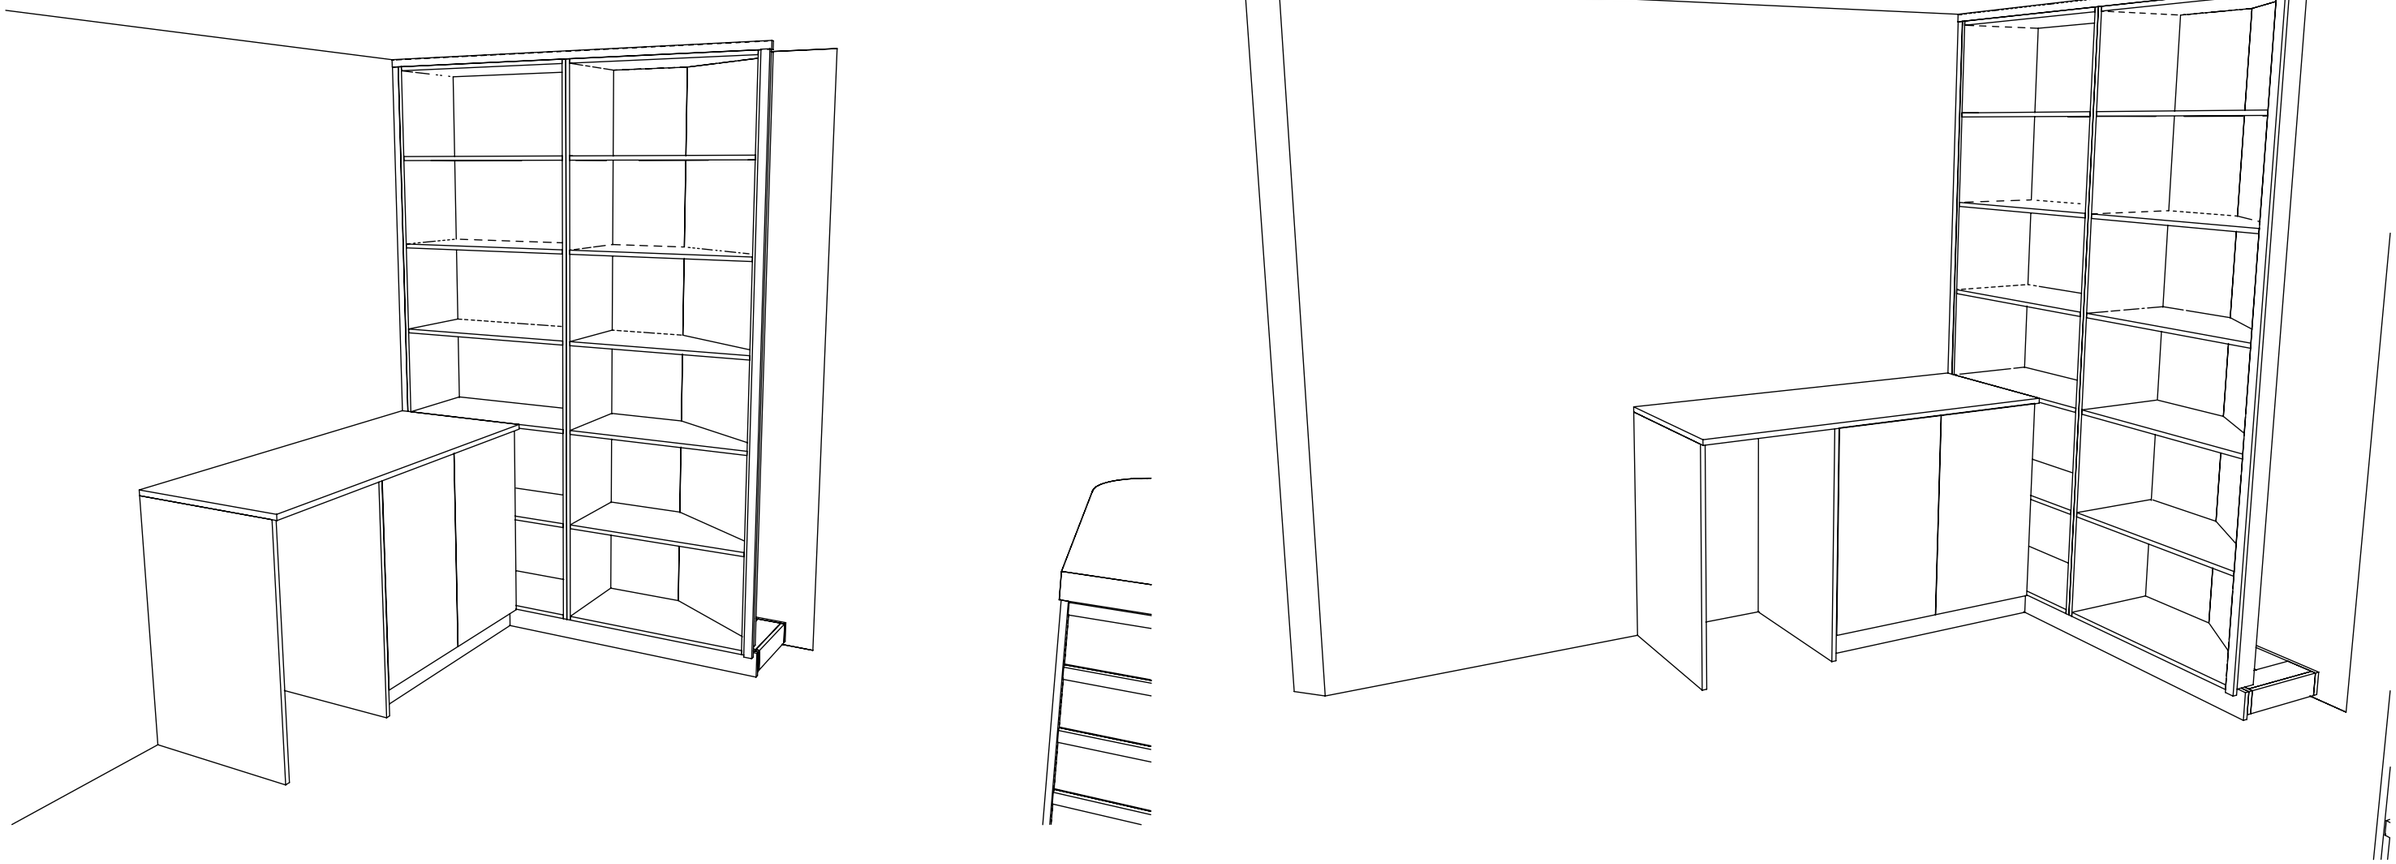


Client Approved Signature : ..... Date : .....

Kitchens By Resident Hero 32 Gateway Drive Phone: 0754471077 mark@residenthero.com.au www.residenthero.com.au	RHK6581 Lee Smith	**Scale: NTS**	**Sheet 8 of 9**
	Kitchen J05 + Butler's J04	Do not scale off this drawing.	Drawn By:
	38 Howard St, Grange QLD		Date: 02/11/26

Kitchen J05 + Butler's J04 3D NTS

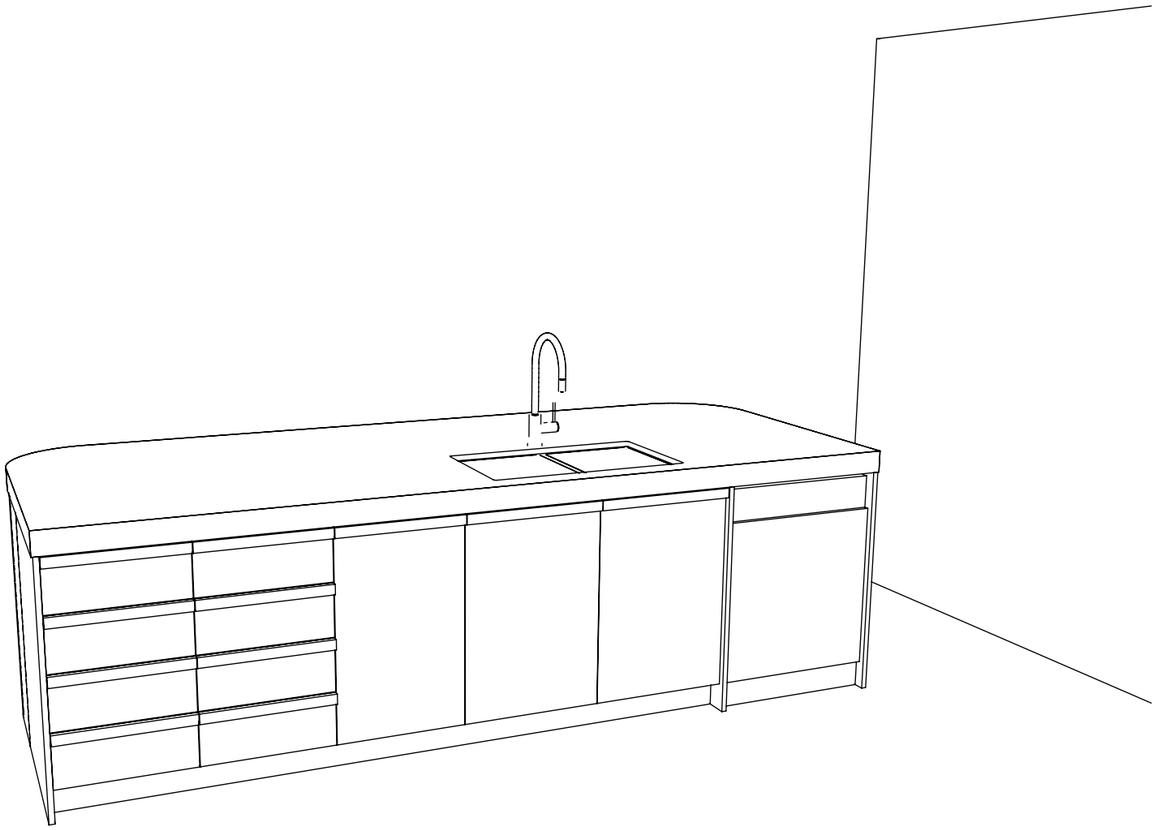


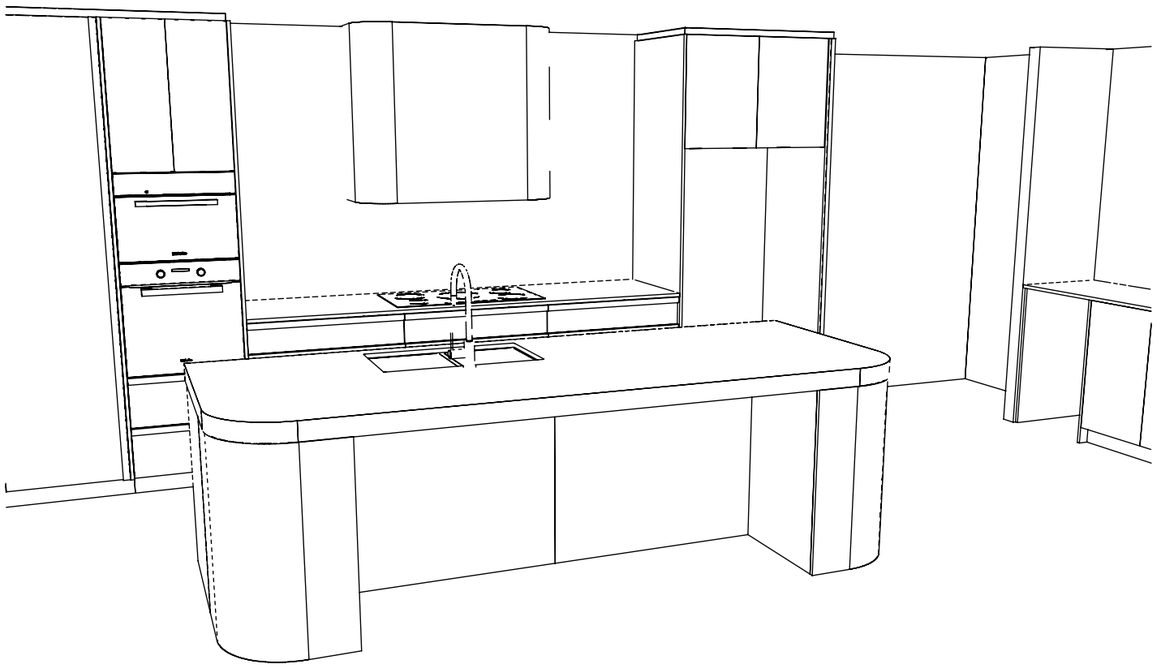

Client Approved Signature : ..... Date : .....

Kitchens By Resident Hero 32 Gateway Drive Phone: 0754471077 mark@residenthero.com.au www.residenthero.com.au	RHK6581 Lee Smith	**Scale: NTS**	**Sheet 9 of 9**
	Kitchen J05 + Butler's J04	Do not scale off this drawing.	Drawn By:
	38 Howard St, Grange QLD		Date: 02/11/26

Living J06 Plan 1 : 20

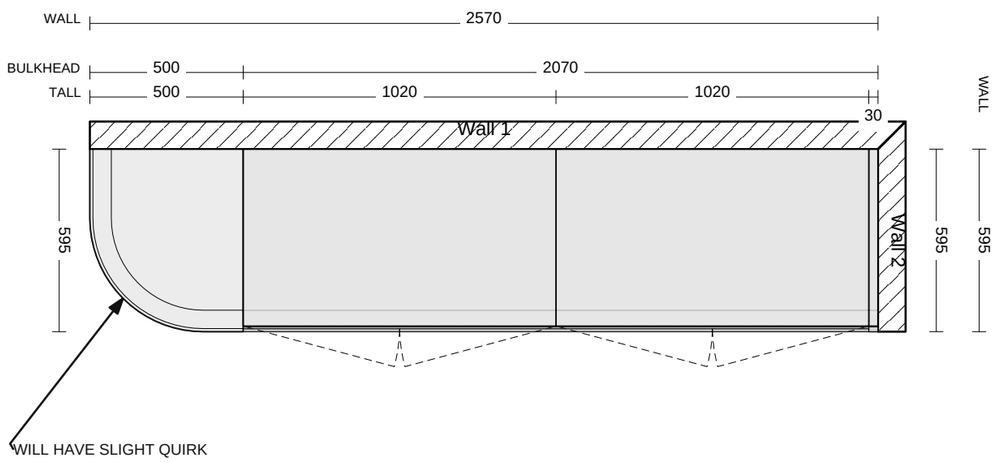

SPECIFICATIONS - Living J06
RHK6581 Lee Smith

FRONTS + PANELS
Laminex 16mm - Desert Dune 2595, Natural finish
Panels: LX Colour 16mm – Desert Dune

HANDLES
Client supplied - undrilled

CARCASS
Internal: Whiteboard 16.5mm


HARDWARE
Hinges: Blum

Client Approved Signature : ..... Date : .....

Kitchens By Resident Hero 32 Gateway Drive Phone: 0754471077 mark@residenthero.com.au www.residenthero.com.au	RHK6581 Lee Smith	**Scale: 1 : 20**	**Sheet 1 of 3**
	Living J06	Do not scale off this drawing.	Drawn By:
	38 Howard St, Grange QLD		Date: 02/11/26

Living J06 Elevation Wall 1


1 : 20

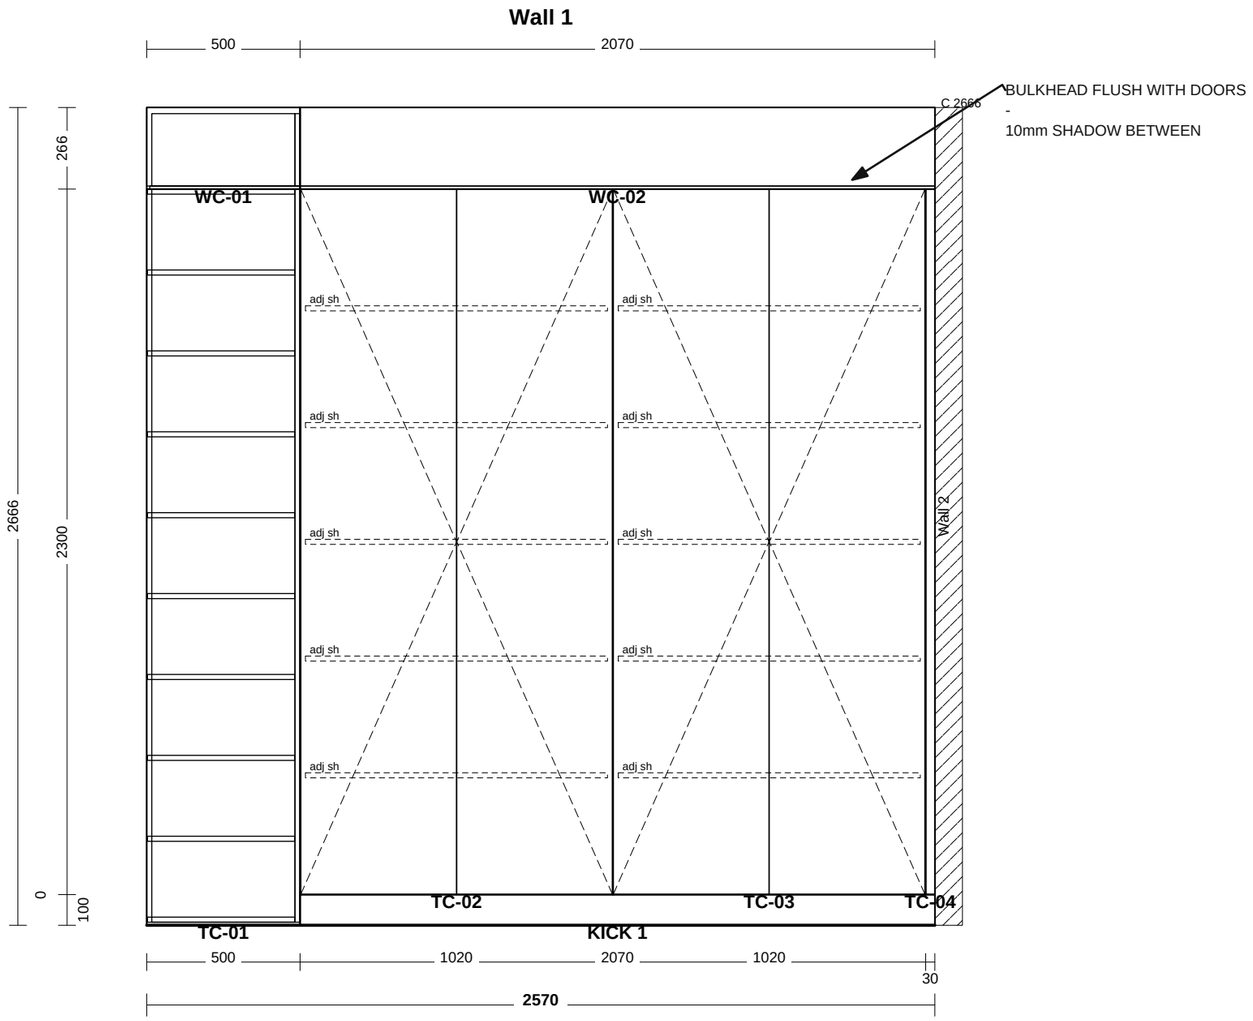


Client Approved Signature : ..... Date : .....

Kitchens By Resident Hero 32 Gateway Drive Phone: 0754471077 mark@residenthero.com.au www.residenthero.com.au	RHK6581 Lee Smith	**Scale: 1 : 20**	**Sheet 2 of 3**
	Living J06	Do not scale off this drawing.	Drawn By:
	38 Howard St, Grange QLD		Date: 02/11/26

Living J06 3D NTS

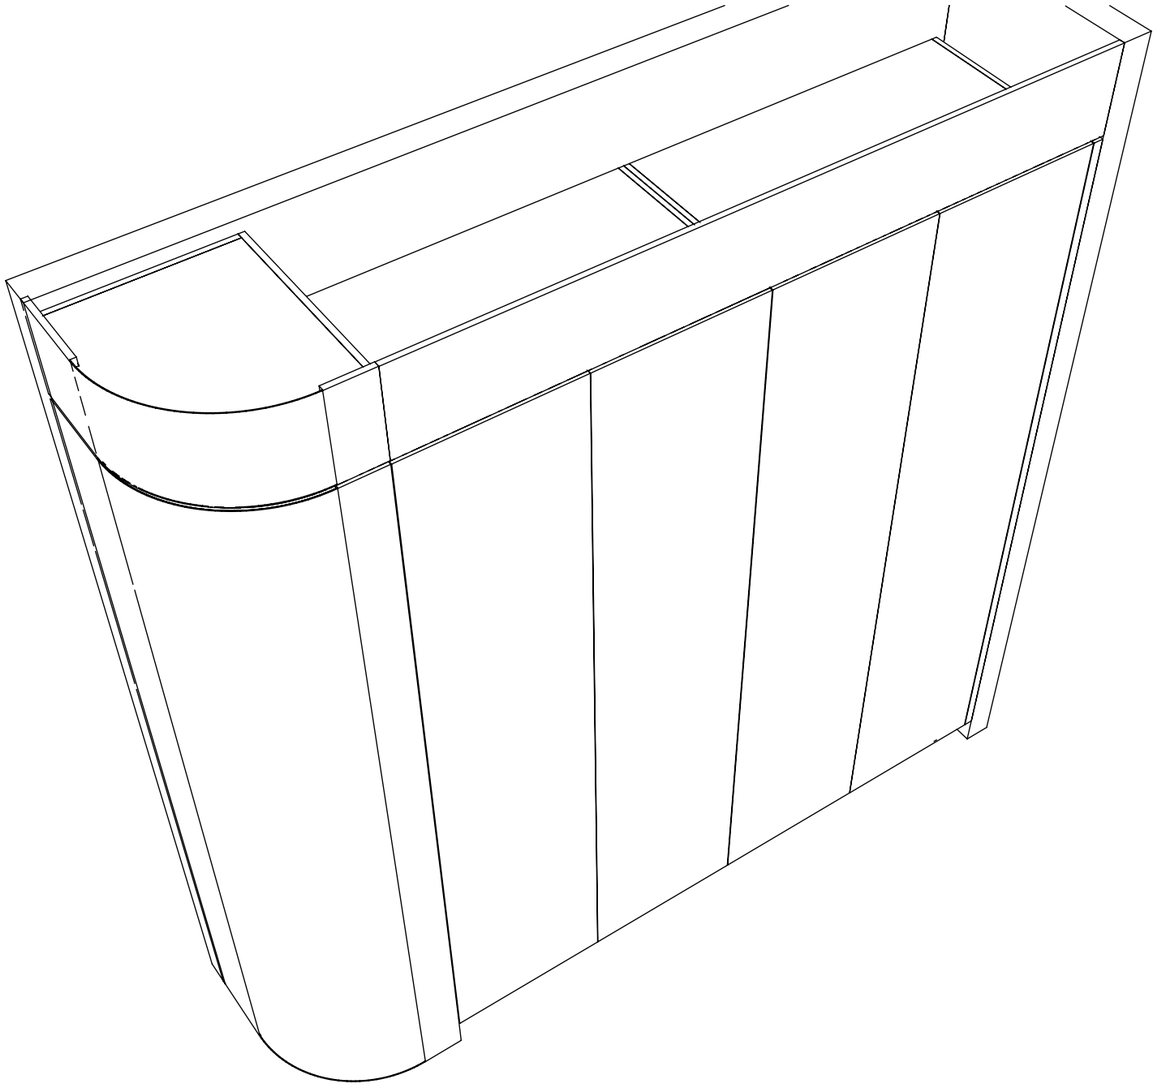


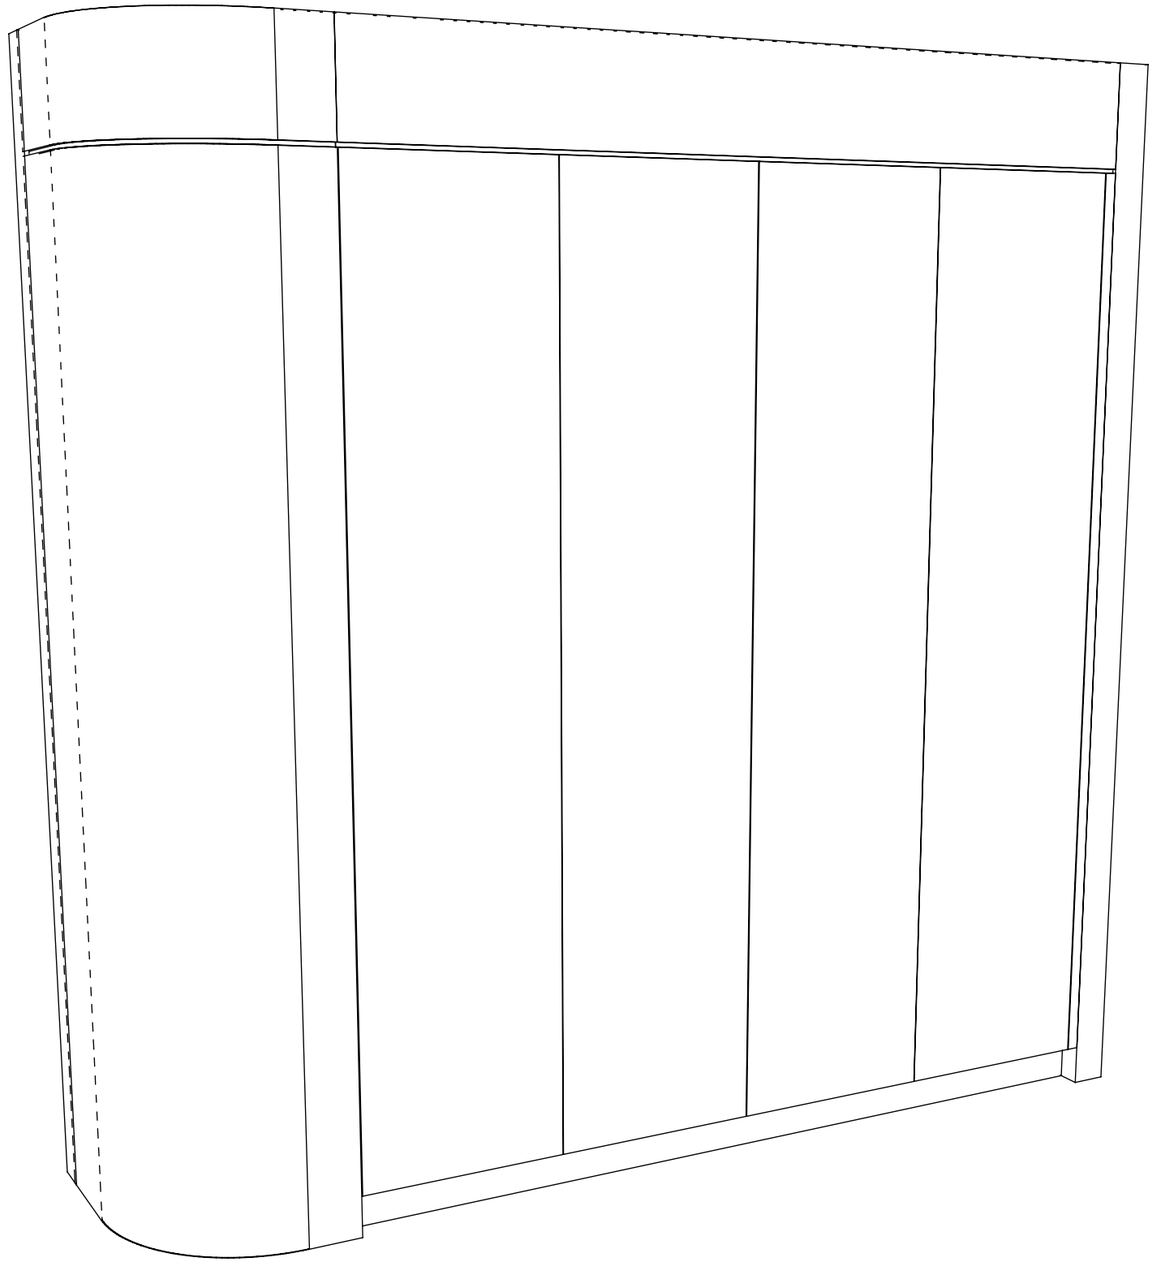

Client Approved Signature : ..... Date : .....

Kitchens By Resident Hero 32 Gateway Drive Phone: 0754471077 mark@residenthero.com.au www.residenthero.com.au	RHK6581 Lee Smith	**Scale: NTS**	**Sheet 3 of 3**
	Living J06	Do not scale off this drawing.	Drawn By:
	38 Howard St, Grange QLD		Date: 02/11/26

Play J07 Plan 1 : 20

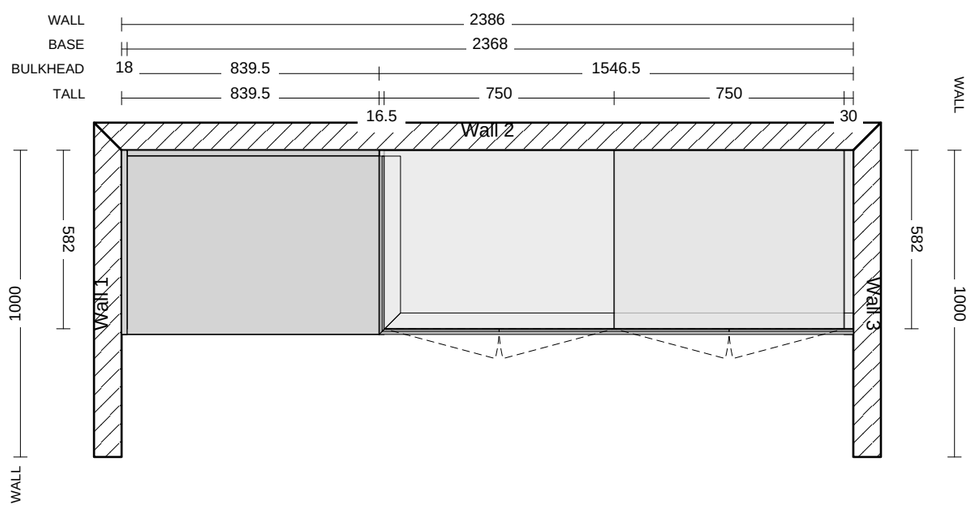

SPECIFICATIONS - Play J07
RHK6581 Lee Smith

FRONTS + PANELS
Laminex 16mm Colour - Sunbaked Natural
Panels: LX Colour 16mm – Sunbaked Natural
Desk top + side panel against wall:
Lx Elegant Oak 18mm

HANDLES
Client supplied - undrilled


CARCASS
Internal: Whiteboard 16.5mm

HARDWARE
Hinges: Blum

Client Approved Signature : ..... Date : .....

Kitchens By Resident Hero 32 Gateway Drive Phone: 0754471077 mark@residenthero.com.au www.residenthero.com.au	RHK6581 Lee Smith	**Scale: 1 : 20**	**Sheet 1 of 3**
	Play J07	Do not scale off this drawing.	Drawn By:
	38 Howard St, Grange QLD		Date: 02/11/26


Play J07 Elevation Wall 2 1 : 20

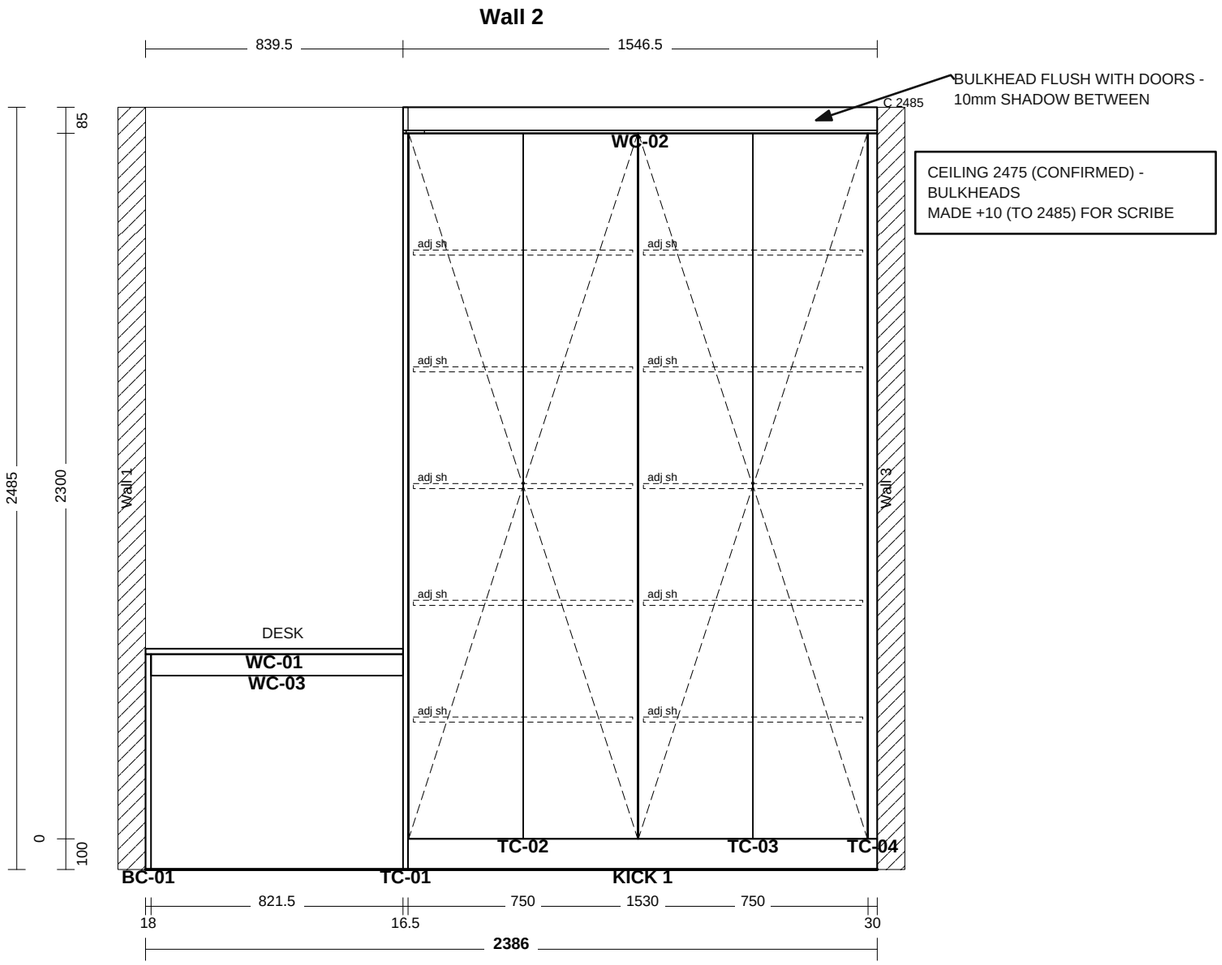


Client Approved Signature : ..... Date : .....

Kitchens By Resident Hero 32 Gateway Drive Phone: 0754471077 mark@residenthero.com.au www.residenthero.com.au	RHK6581 Lee Smith	**Scale: 1 : 20**	**Sheet 2 of 3**
	Play J07	Do not scale off this drawing.	Drawn By:
	38 Howard St, Grange QLD		Date: 02/11/26

Play J07 3D NTS

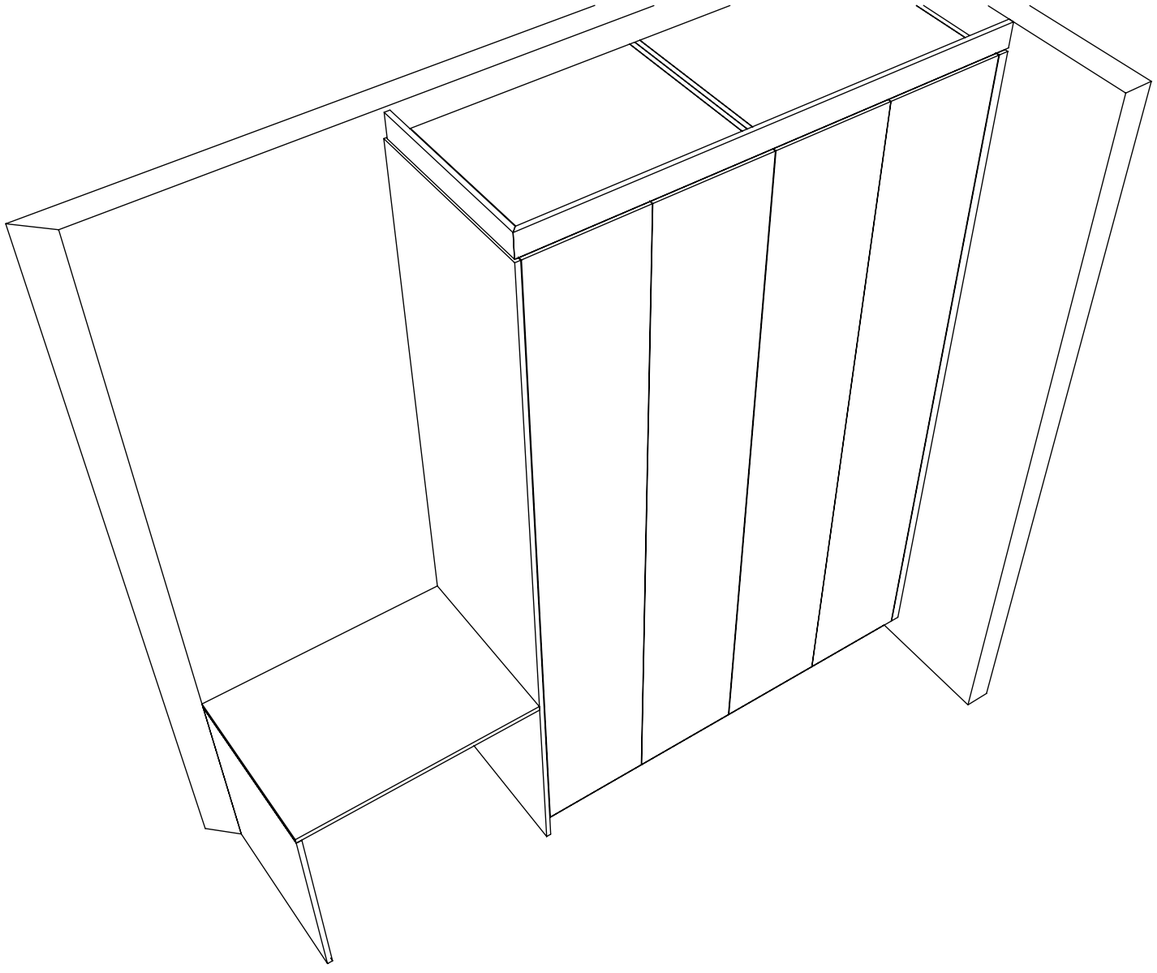


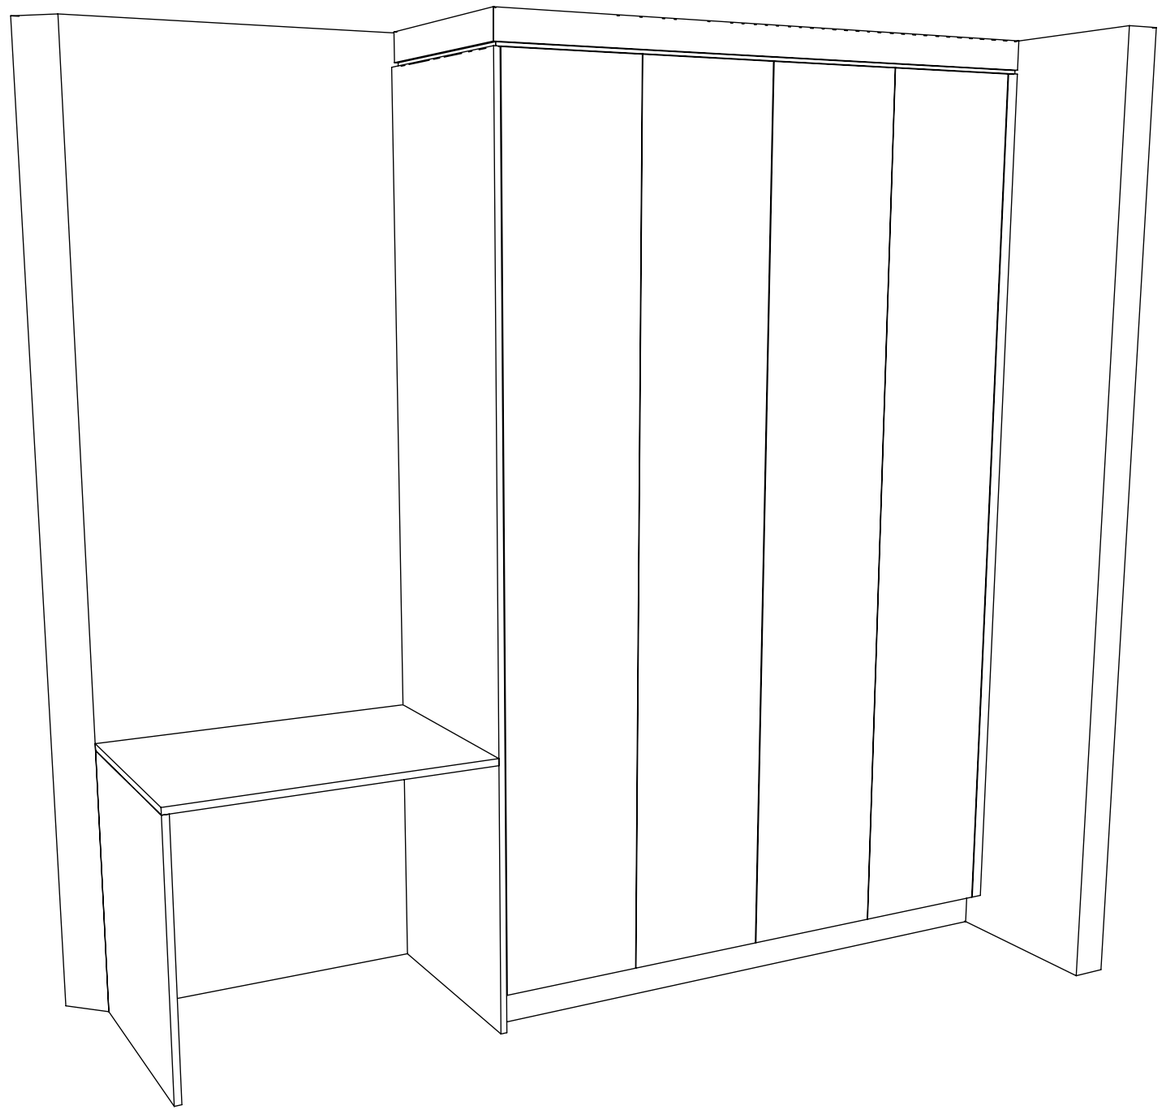

Client Approved Signature : ..... Date : .....

Kitchens By Resident Hero 32 Gateway Drive Phone: 0754471077 mark@residenthero.com.au www.residenthero.com.au	RHK6581 Lee Smith	**Scale: NTS**	**Sheet 3 of 3**
	Play J07	Do not scale off this drawing.	Drawn By:
	38 Howard St, Grange QLD		Date: 02/11/26

Play J07M Plan 1 : 20

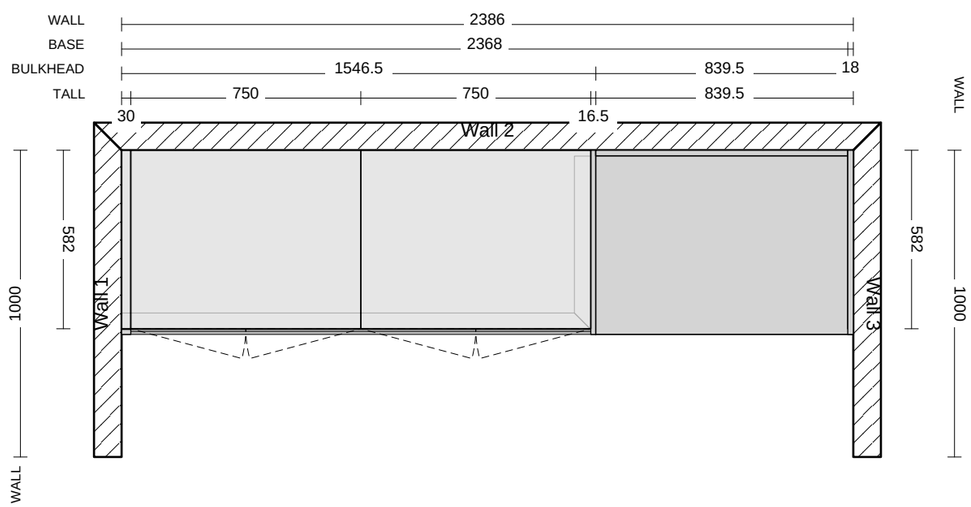

SPECIFICATIONS - Play J07M
RHK6581 Lee Smith

FRONTS + PANELS
Laminex 16mm Colour - Sunbaked Natural
Panels: LX Colour 16mm – Sunbaked Natural
Desk top + side panel against wall:
Lx Elegant Oak 18mm

HANDLES
Client supplied - undrilled


CARCASS
Internal: Whiteboard 16.5mm

HARDWARE
Hinges: Blum

Client Approved Signature : ..... Date : .....

Kitchens By Resident Hero 32 Gateway Drive Phone: 0754471077 mark@residenthero.com.au www.residenthero.com.au	RHK6581 Lee Smith	**Scale: 1 : 20**	**Sheet 1 of 3**
	Play J07M	Do not scale off this drawing.	Drawn By:
	38 Howard St, Grange QLD		Date: 02/11/26


Play J07M Elevation Wall 2 1 : 20

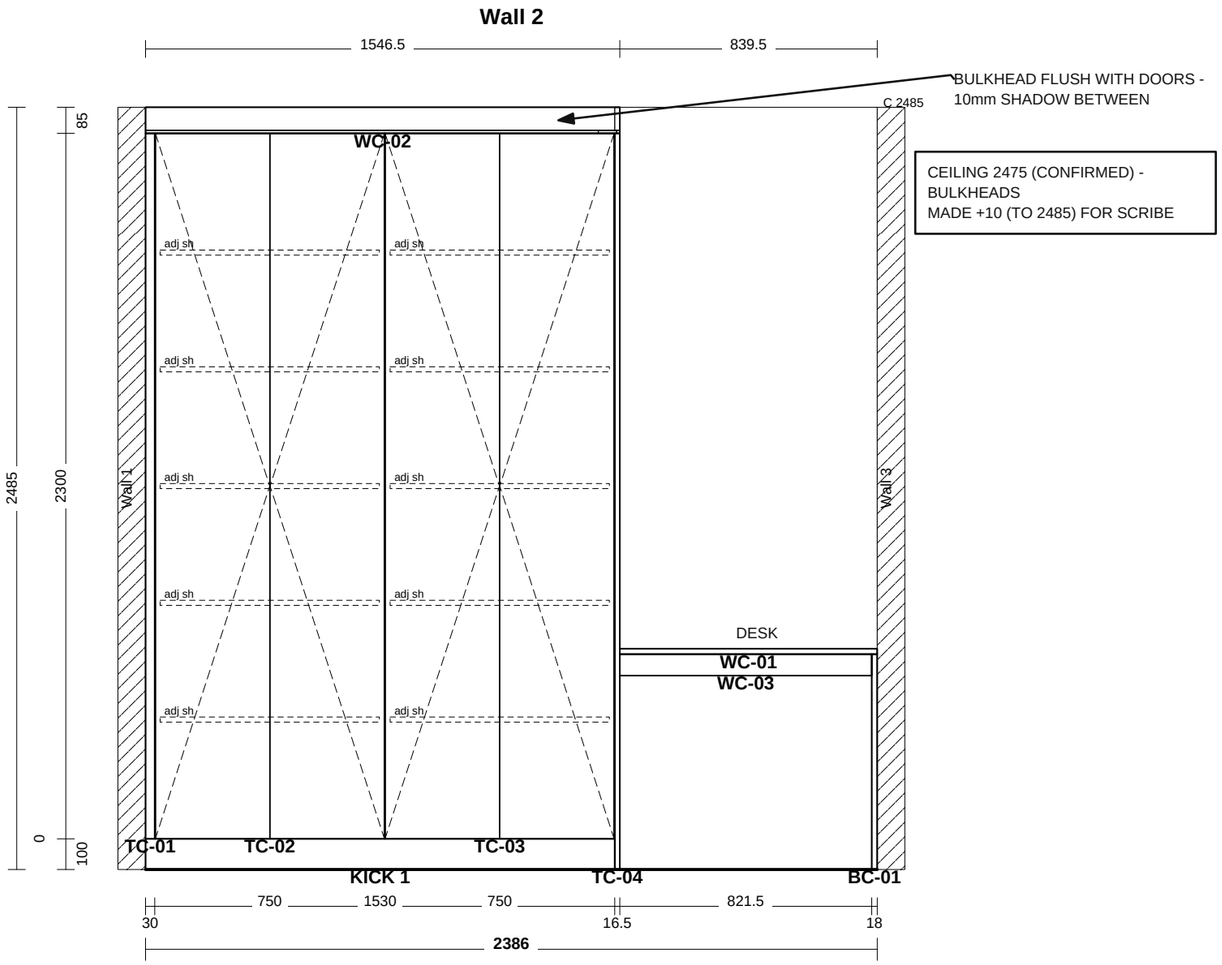


Client Approved Signature : ..... Date : .....

Kitchens By Resident Hero 32 Gateway Drive Phone: 0754471077 mark@residenthero.com.au www.residenthero.com.au	RHK6581 Lee Smith	**Scale: 1 : 20**	**Sheet 2 of 3**
	Play J07M	Do not scale off this drawing.	Drawn By:
	38 Howard St, Grange QLD		Date: 02/11/26

Play J07M 3D NTS

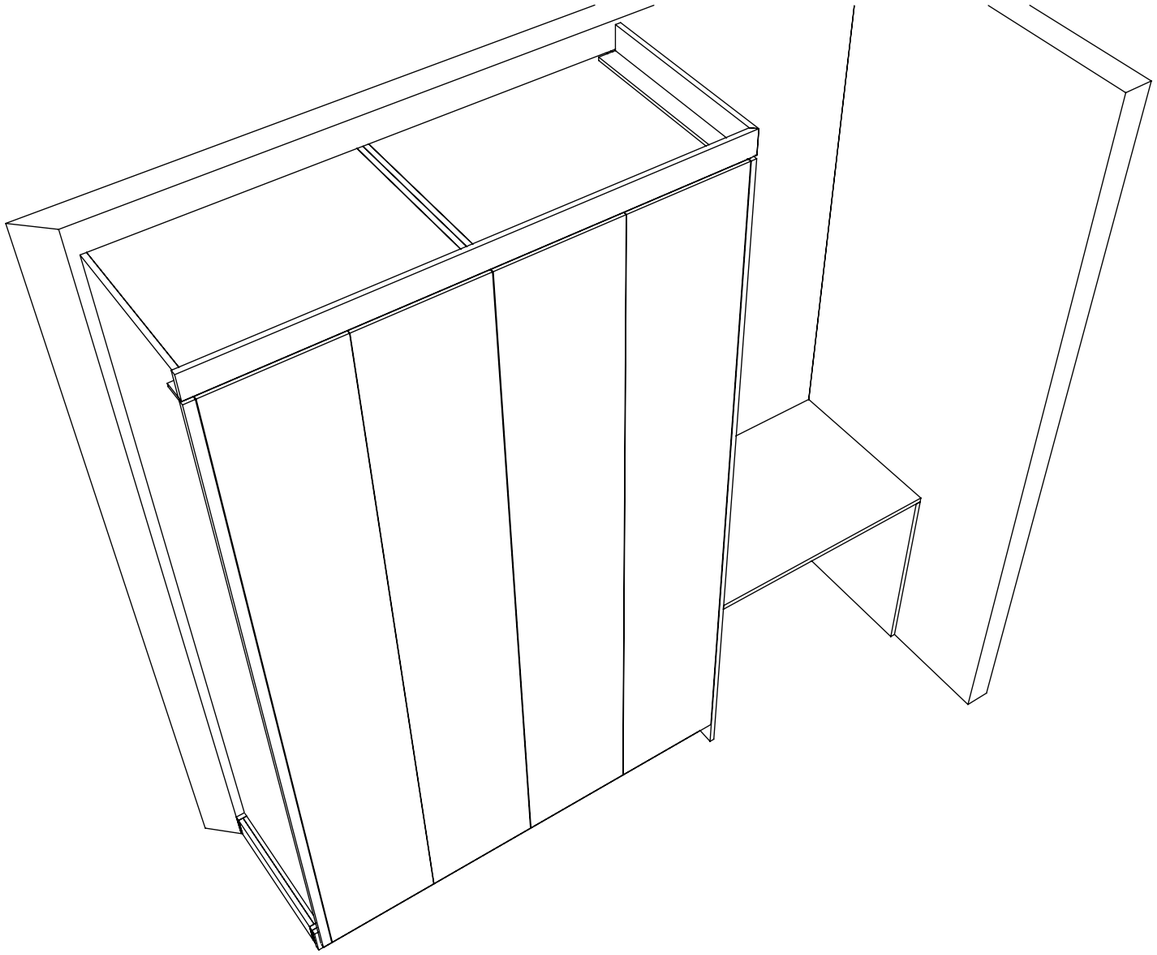


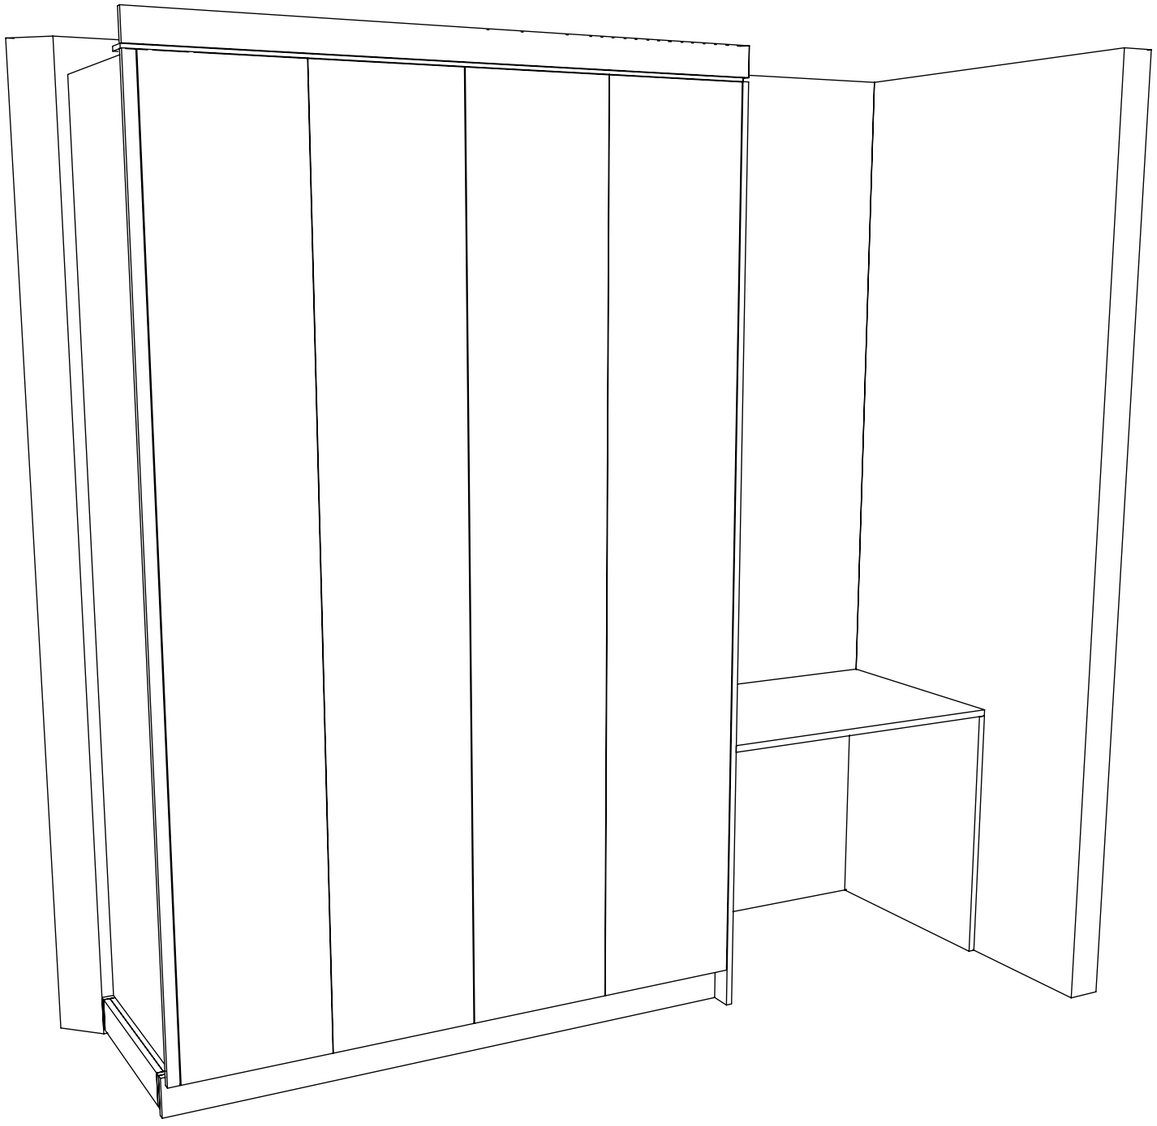

Client Approved Signature : ..... Date : .....

Kitchens By Resident Hero 32 Gateway Drive Phone: 0754471077 mark@residenthero.com.au www.residenthero.com.au	RHK6581 Lee Smith	**Scale: NTS**	**Sheet 3 of 3**
	Play J07M	Do not scale off this drawing.	Drawn By:
	38 Howard St, Grange QLD		Date: 02/11/26

Bed 2 J08 Plan 1 : 20

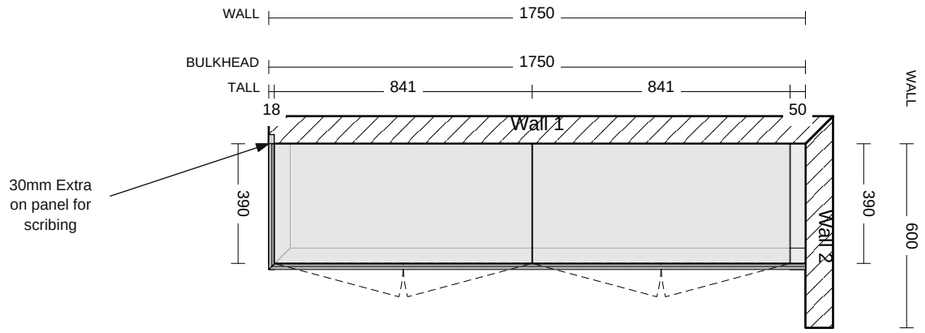

SPECIFICATIONS - Bed 2 J08
RHK6581 Lee Smith

FRONTS + PANELS
Laminex 18mm ABS Grain - Elegant Oak
Panels: LX Abs Grain 18mm – Elegant Oak

HANDLES
Client supplied - undrilled

CARCASS
Internal: Whiteboard 16.5mm


DRAWERS
Drawer box: DTC Dragon Pro

HARDWARE
Hinges: Blum
Runners: DTC Dragon Pro – Silk White

Client Approved Signature : ..... Date : .....

Kitchens By Resident Hero 32 Gateway Drive Phone: 0754471077 mark@residenthero.com.au www.residenthero.com.au	RHK6581 Lee Smith	**Scale: 1 : 20**	**Sheet 1 of 3**
	Bed 2 J08	Do not scale off this drawing.	Drawn By:
	38 Howard St, Grange QLD		Date: 02/11/26


Bed 2 J08 Elevation Wall 1 1 : 20

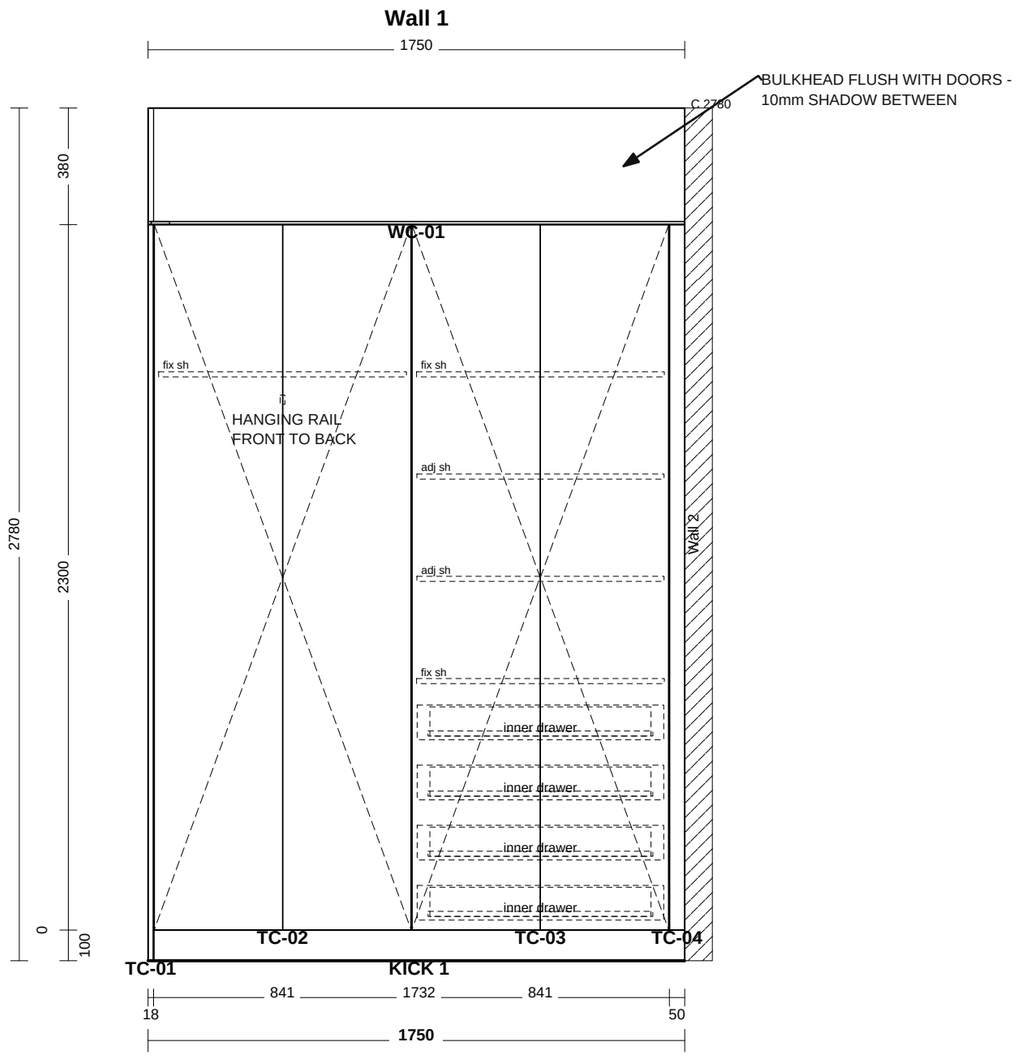


Client Approved Signature : ..... Date : .....

Kitchens By Resident Hero 32 Gateway Drive Phone: 0754471077 mark@residenthero.com.au www.residenthero.com.au	RHK6581 Lee Smith	**Scale: 1 : 20**	**Sheet 2 of 3**
	Bed 2 J08	Do not scale off this drawing.	Drawn By:
	38 Howard St, Grange QLD		Date: 02/11/26

Bed 2 J08 3D NTS

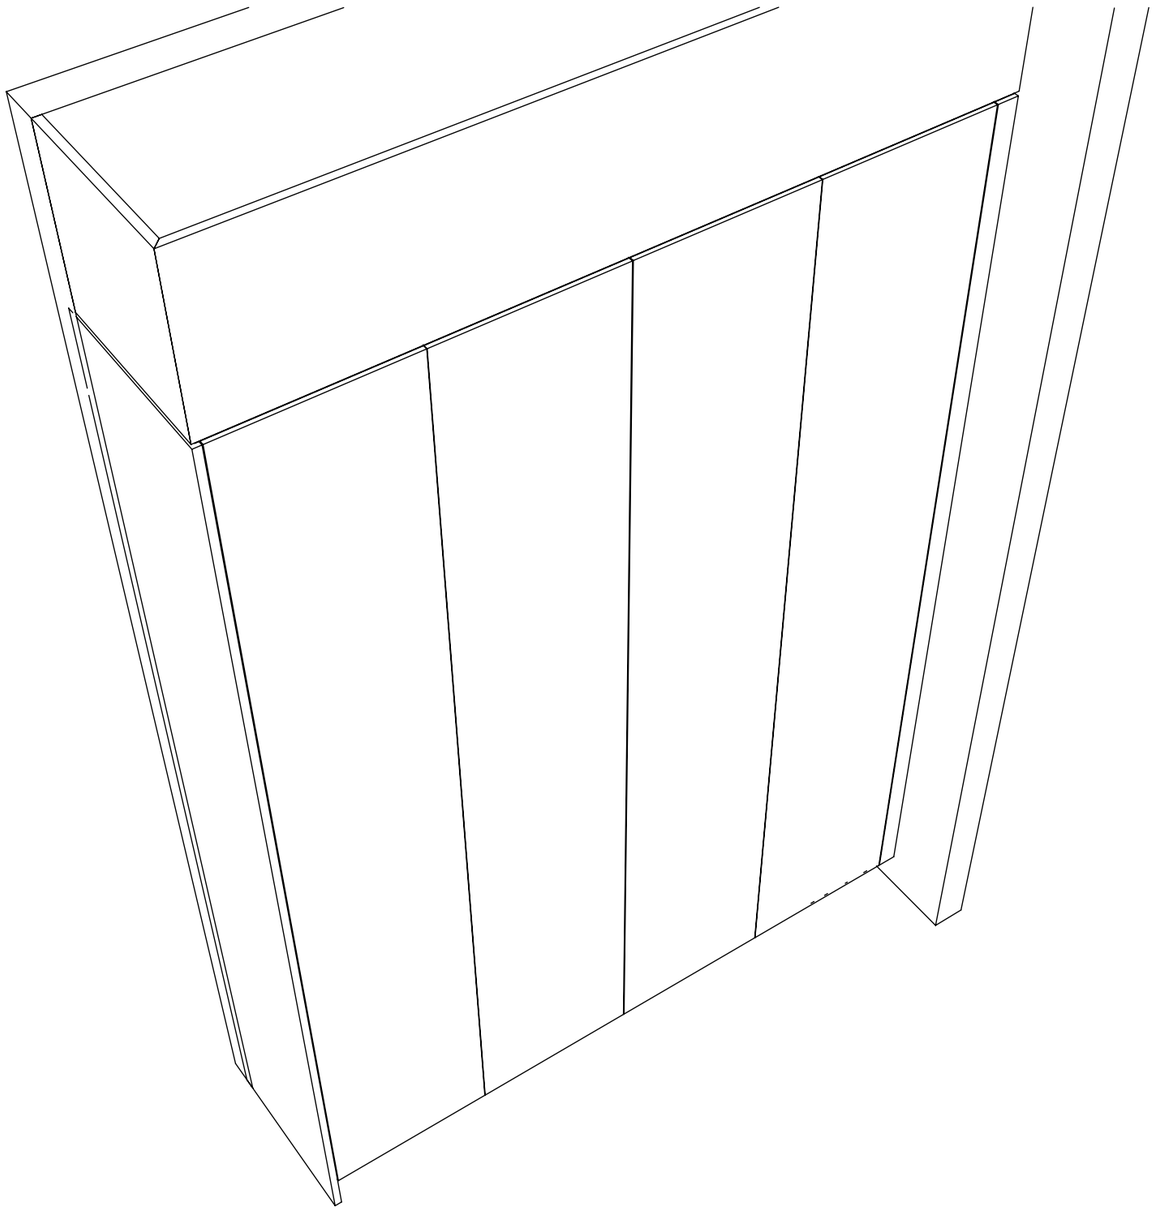


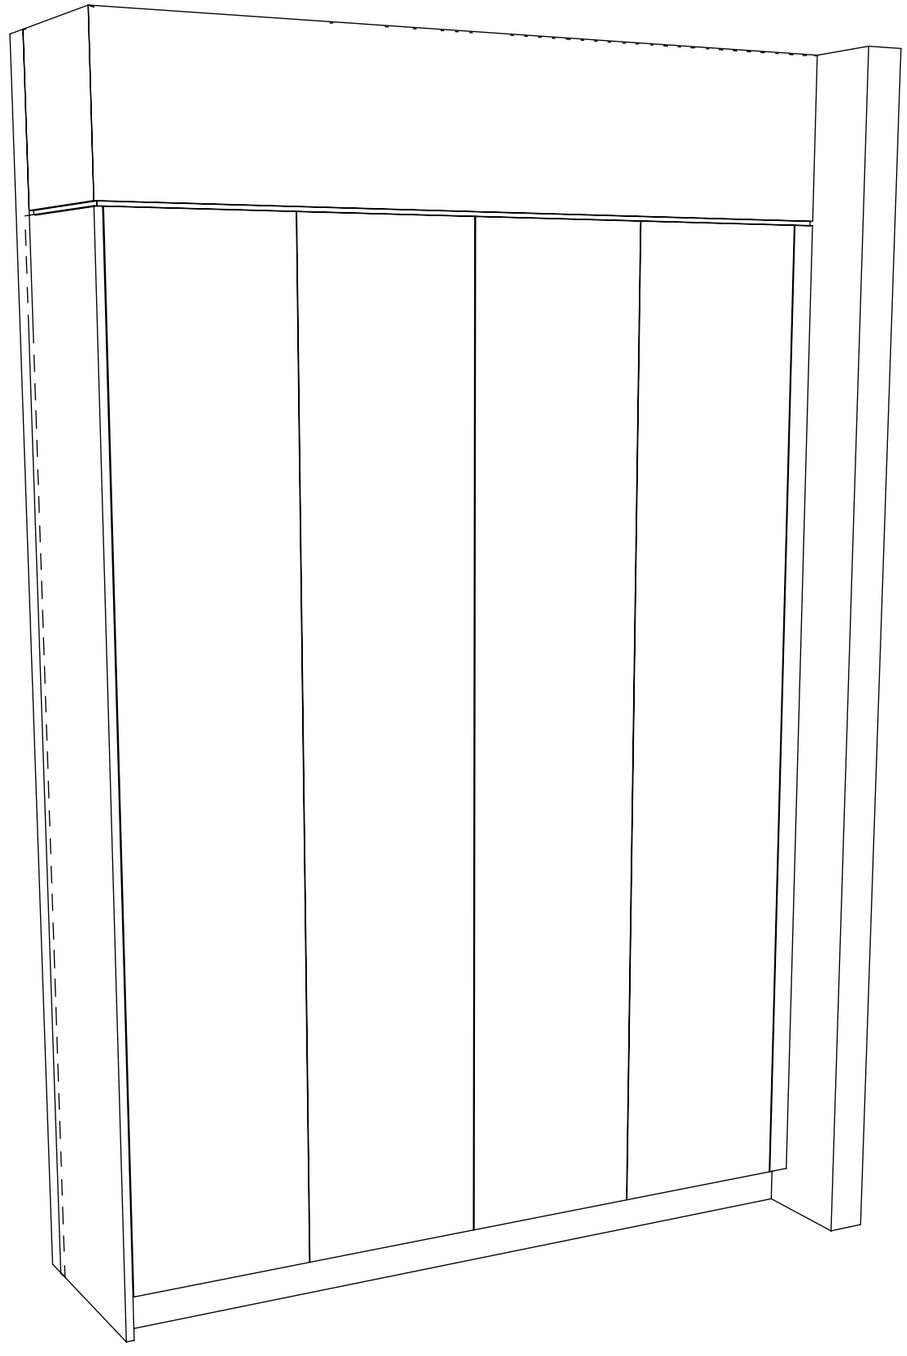

Client Approved Signature : ..... Date : .....

Kitchens By Resident Hero 32 Gateway Drive Phone: 0754471077 mark@residenthero.com.au www.residenthero.com.au	RHK6581 Lee Smith	**Scale: NTS**	**Sheet 3 of 3**
	Bed 2 J08	Do not scale off this drawing.	Drawn By:
	38 Howard St, Grange QLD		Date: 02/11/26

Bed 3 J08 Plan 1 : 20

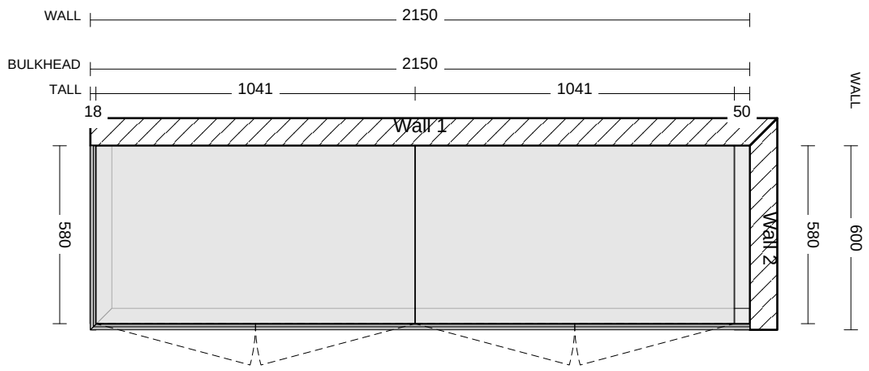

SPECIFICATIONS - Bed 3 J08
RHK6581 Lee Smith

FRONTS + PANELS
Laminex 18mm ABS Grain - Elegant Oak
Panels: LX Abs Grain 18mm – Elegant Oak

HANDLES
Client supplied - undrilled

CARCASS
Internal: Whiteboard 16.5mm

DRAWERS
Drawer box: DTC Dragon Pro


HARDWARE
Hinges: Blum
Runners: DTC Dragon Pro – Silk White

Client Approved Signature : ..... Date : .....

Kitchens By Resident Hero 32 Gateway Drive Phone: 0754471077 mark@residenthero.com.au www.residenthero.com.au	RHK6581 Lee Smith	**Scale: 1 : 20**	**Sheet 1 of 3**
	Bed 3 J08	Do not scale off this drawing.	Drawn By:
	38 Howard St, Grange QLD		Date: 02/11/26

Bed 3 J08 Elevation Wall 1


1 : 20

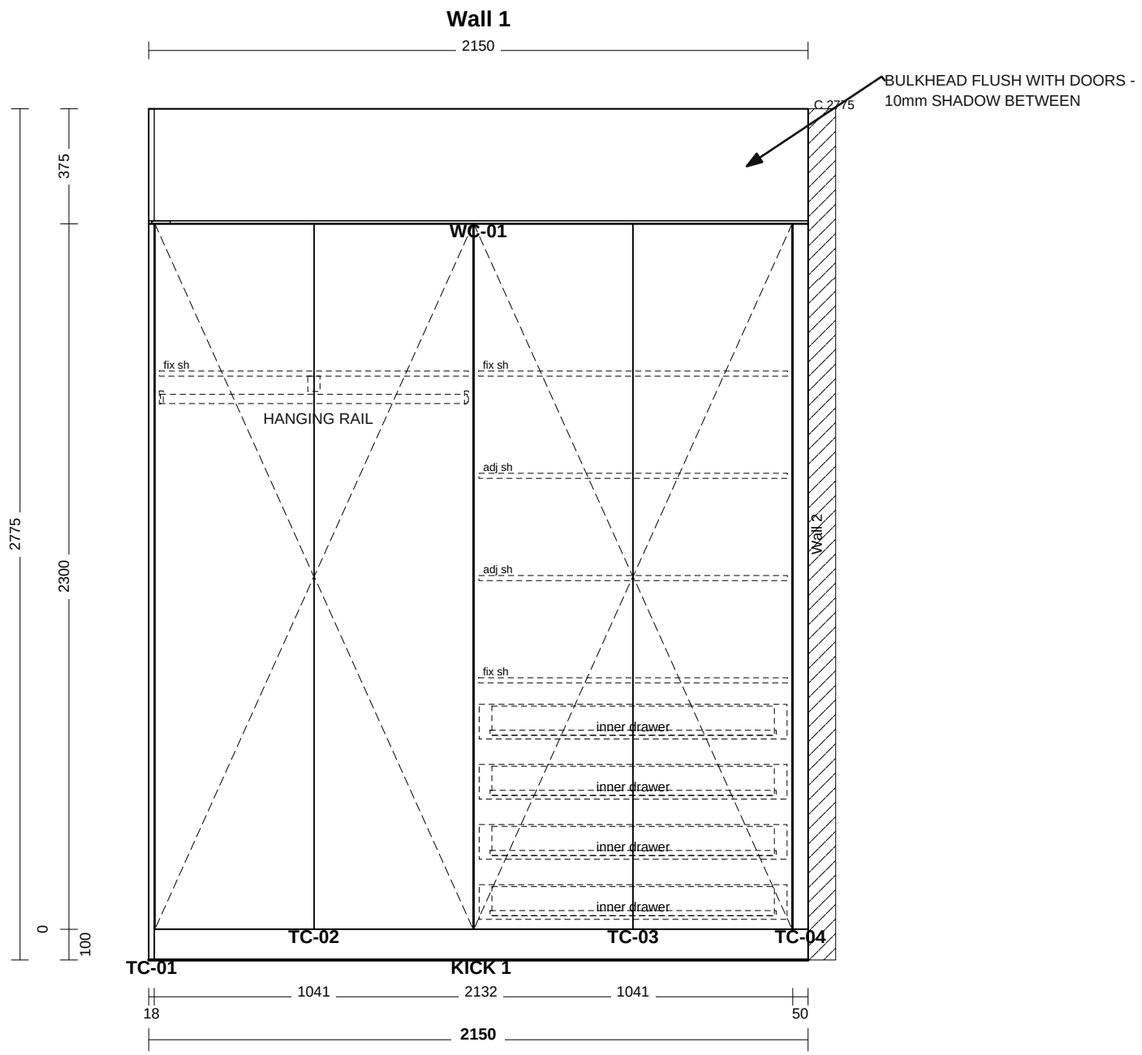


Client Approved Signature : ..... Date : .....

Kitchens By Resident Hero 32 Gateway Drive Phone: 0754471077 mark@residenthero.com.au www.residenthero.com.au	RHK6581 Lee Smith	**Scale: 1 : 20**	**Sheet 2 of 3**
	Bed 3 J08	Do not scale off this drawing.	Drawn By:
	38 Howard St, Grange QLD		Date: 02/11/26

Bed 3 J08 3D NTS

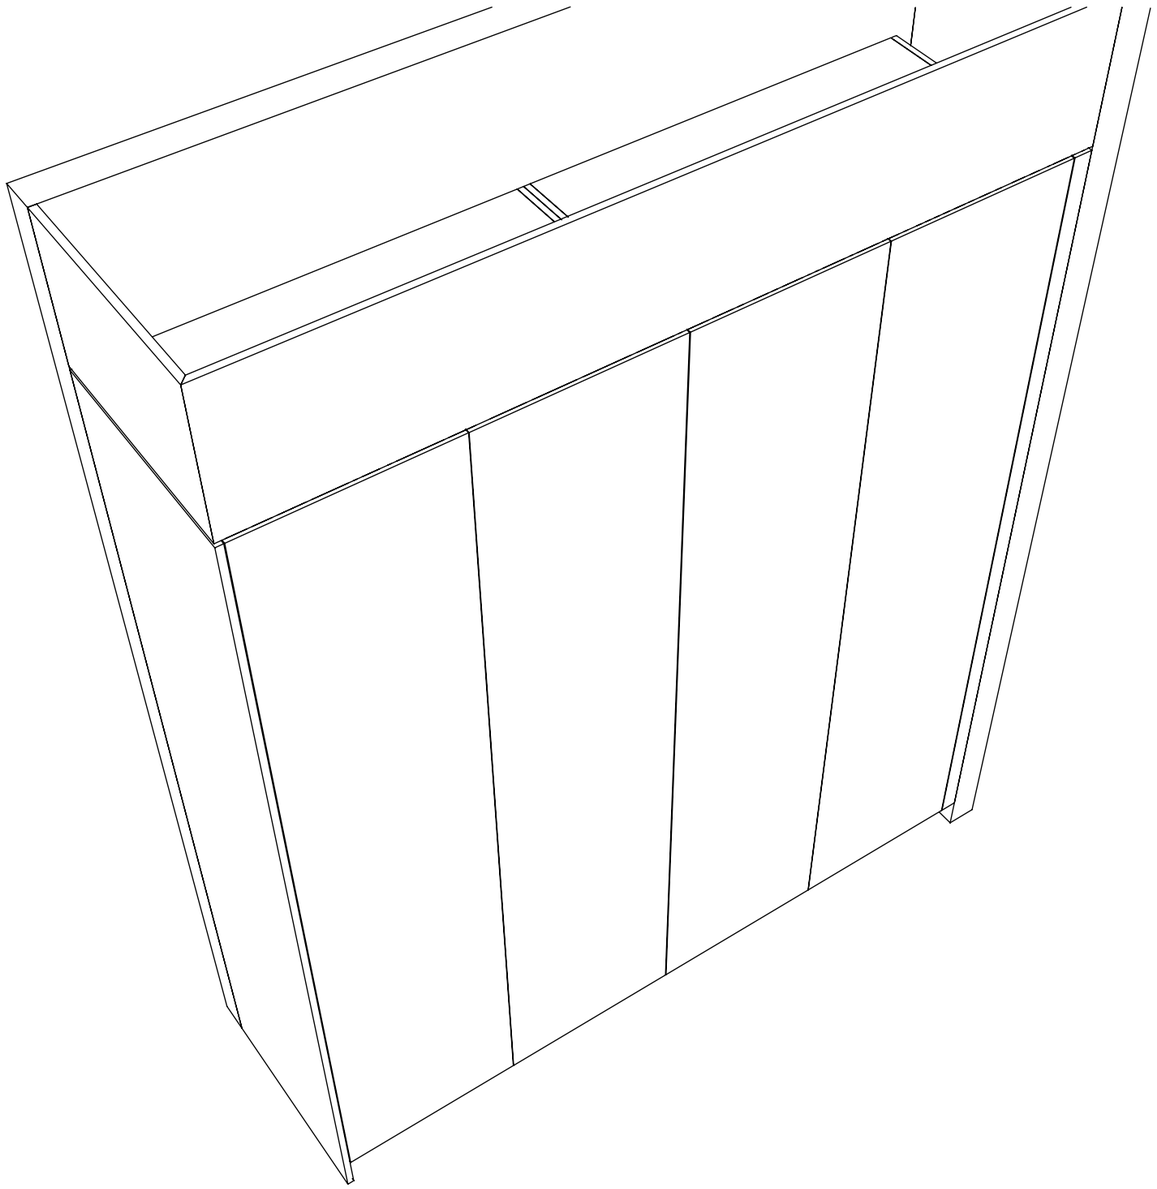


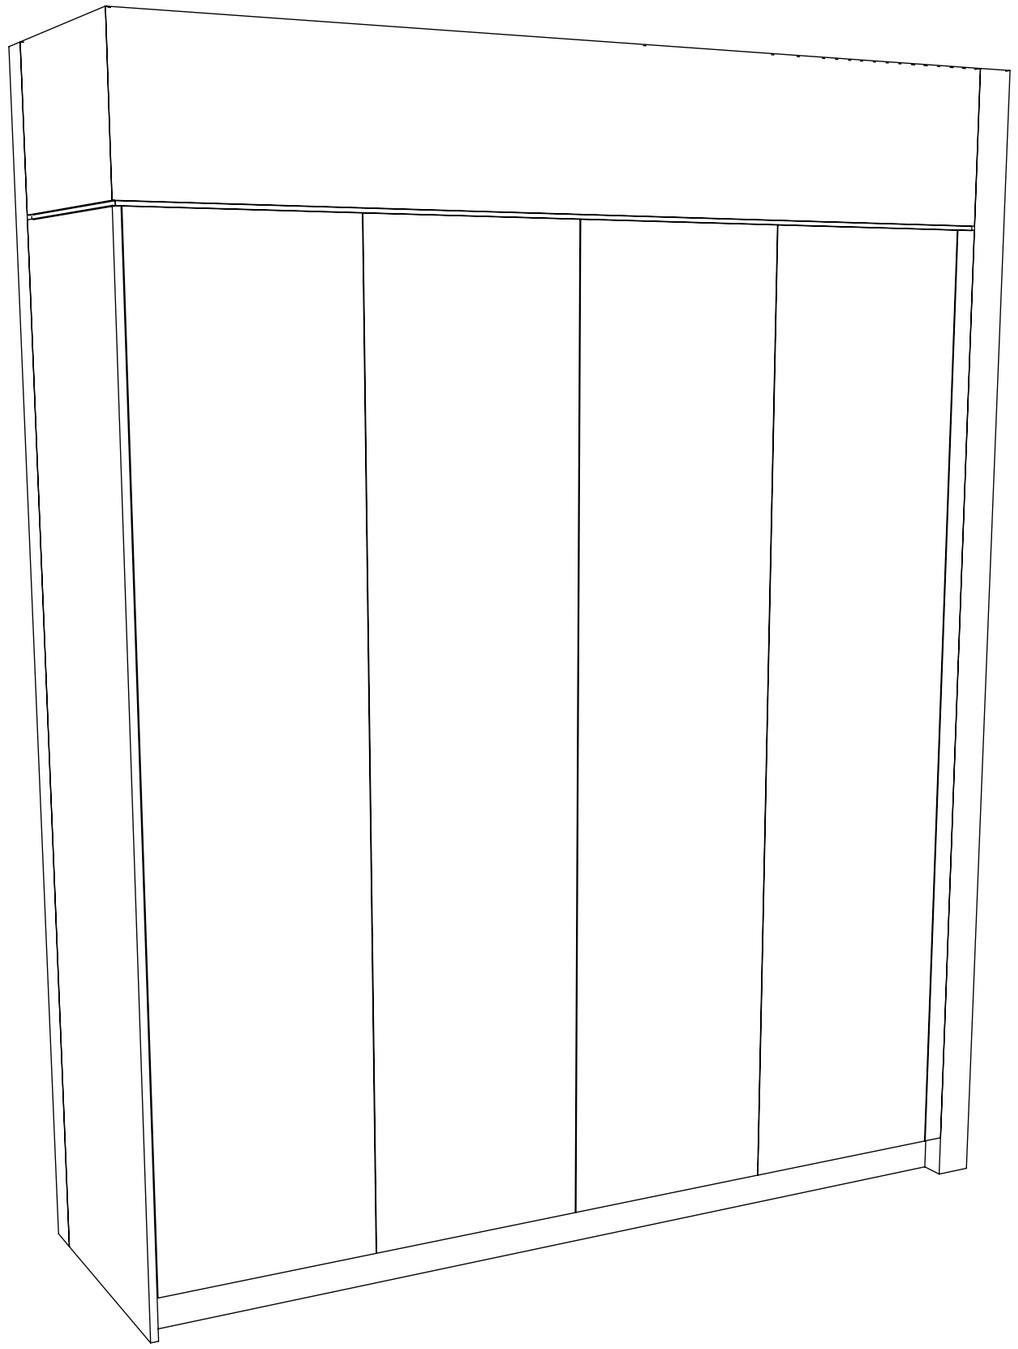

Client Approved Signature : ..... Date : .....

Kitchens By Resident Hero 32 Gateway Drive Phone: 0754471077 mark@residenthero.com.au www.residenthero.com.au	RHK6581 Lee Smith	**Scale: NTS**	**Sheet 3 of 3**
	Bed 3 J08	Do not scale off this drawing.	Drawn By:
	38 Howard St, Grange QLD		Date: 02/11/26

Bed 1 J09 Plan 1 : 20

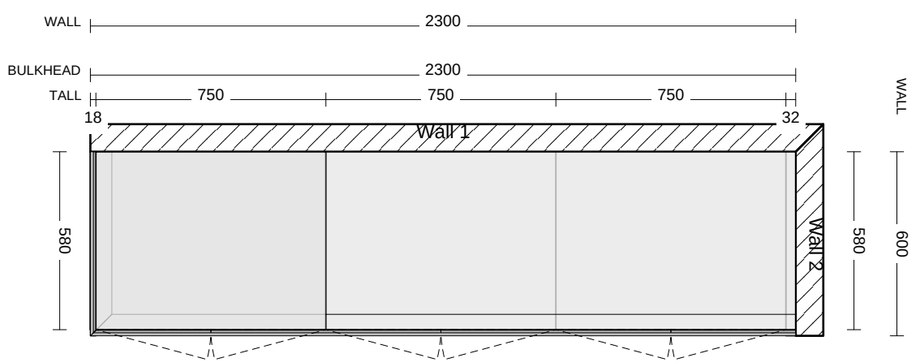

SPECIFICATIONS - Bed 1 J09
RHK6581 Lee Smith

FRONTS + PANELS
Laminex 18mm ABS Grain - Elegant Oak
Panels: LX Abs Grain 18mm – Elegant Oak

HANDLES
Client supplied - undrilled

CARCASS
Internal: Whiteboard 16.5mm


DRAWERS
Drawer box: DTC Dragon Pro

HARDWARE
Hinges: Blum
Runners: DTC Dragon Pro – Silk White

Client Approved Signature : ..... Date : .....

Kitchens By Resident Hero 32 Gateway Drive Phone: 0754471077 mark@residenthero.com.au www.residenthero.com.au	RHK6581 Lee Smith	**Scale: 1 : 20**	**Sheet 1 of 3**
	Bed 1 J09	Do not scale off this drawing.	Drawn By:
	38 Howard St, Grange QLD		Date: 02/11/26


Bed 1 J09 Elevation Wall 1 1 : 20

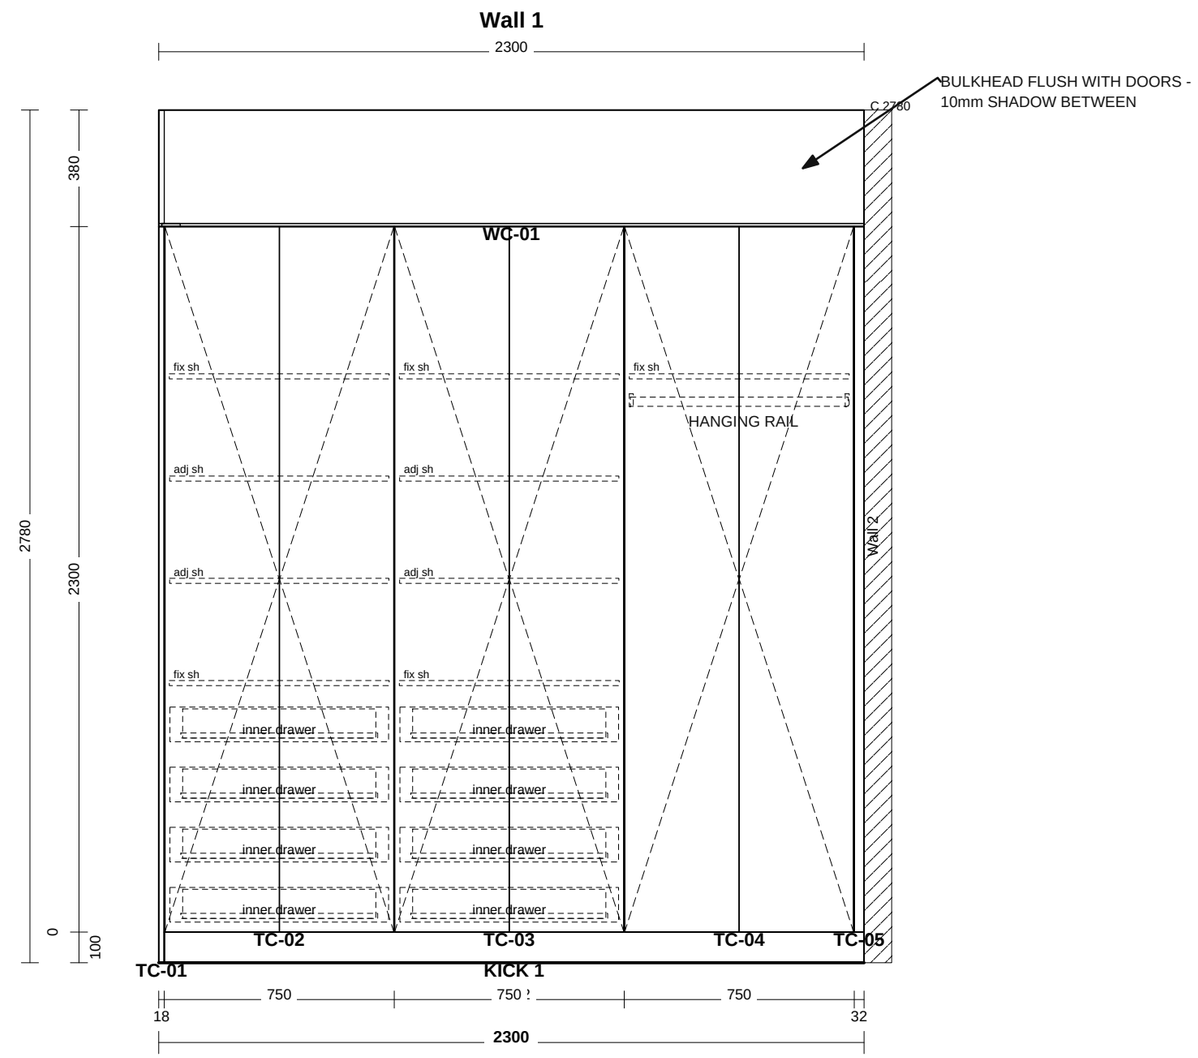


Client Approved Signature : ..... Date : .....

Kitchens By Resident Hero 32 Gateway Drive Phone: 0754471077 mark@residenthero.com.au www.residenthero.com.au	RHK6581 Lee Smith	**Scale: 1 : 20**	**Sheet 2 of 3**
	Bed 1 J09	Do not scale off this drawing.	Drawn By:
	38 Howard St, Grange QLD		Date: 02/11/26

Bed 1 J09 3D NTS

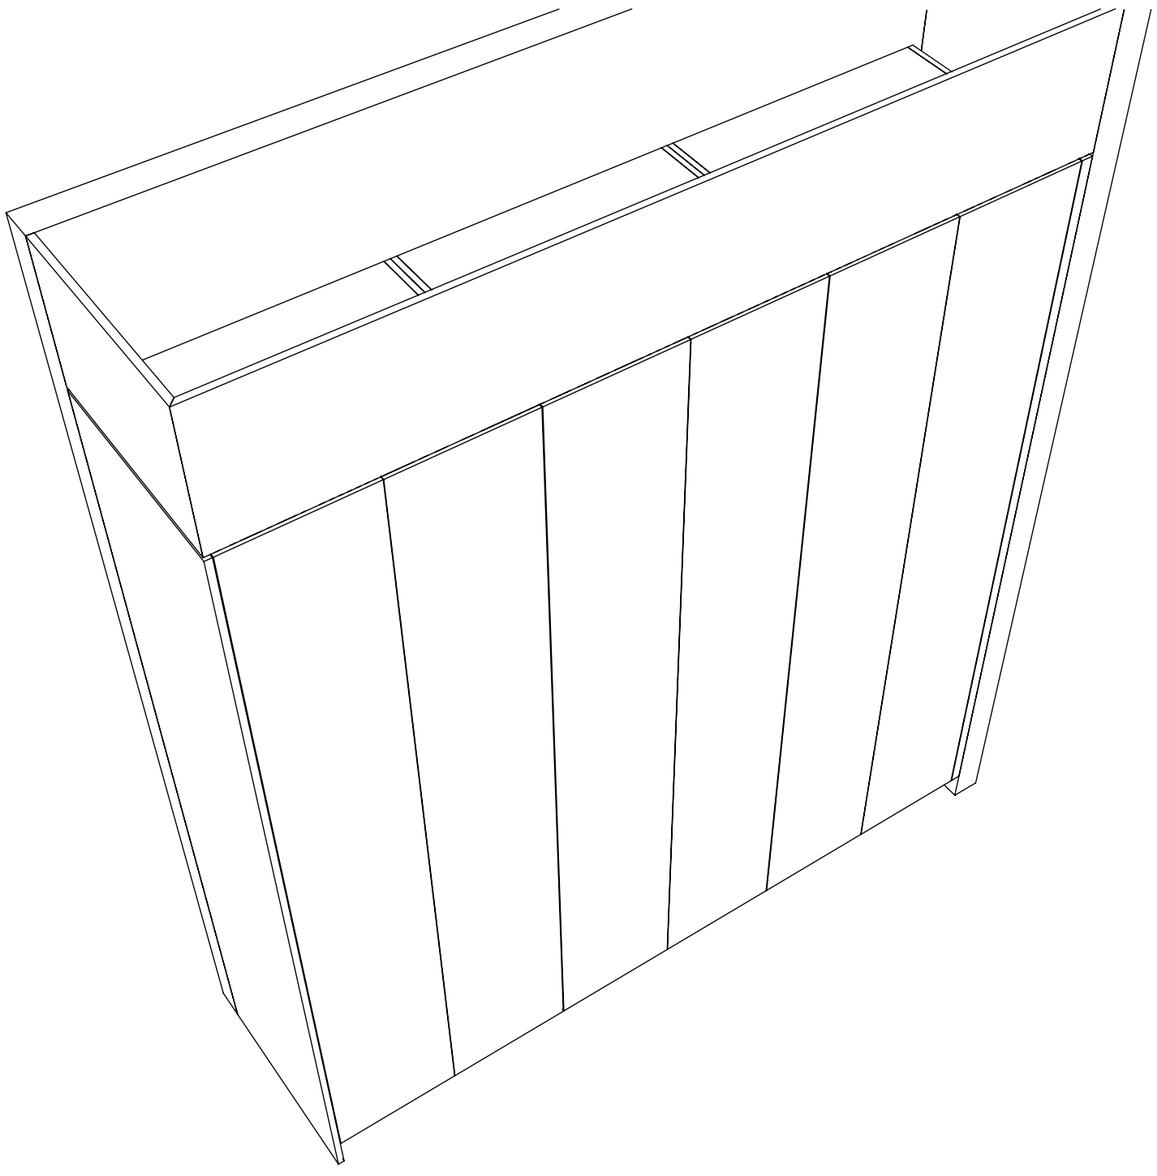


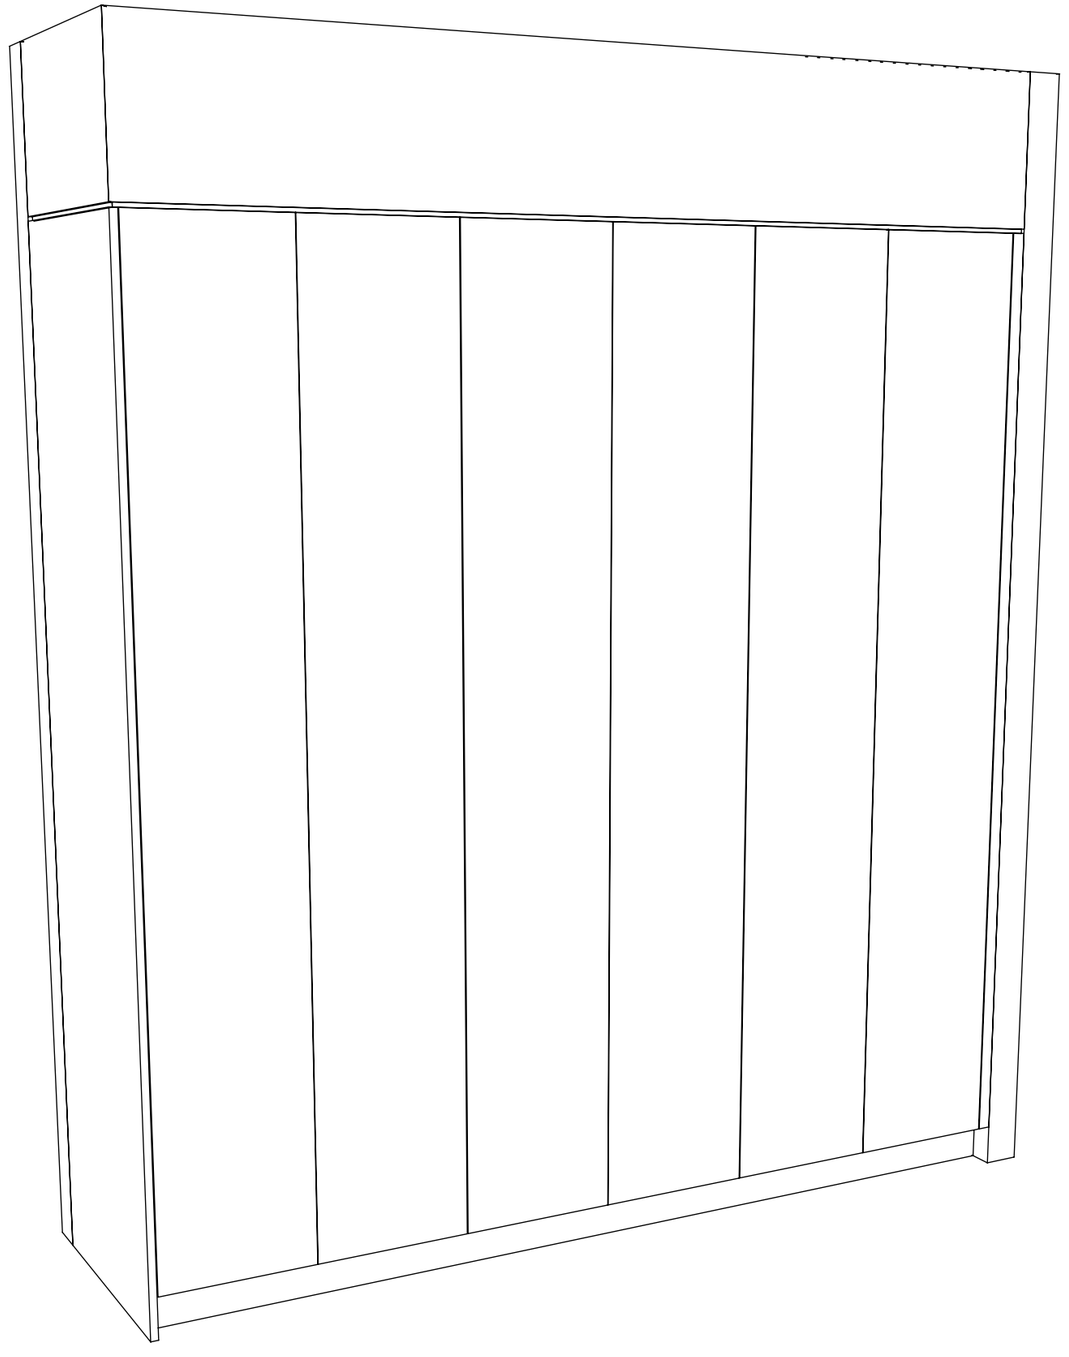

Client Approved Signature : ..... Date : .....

Kitchens By Resident Hero 32 Gateway Drive Phone: 0754471077 mark@residenthero.com.au www.residenthero.com.au	RHK6581 Lee Smith	**Scale: NTS**	**Sheet 3 of 3**
	Bed 1 J09	Do not scale off this drawing.	Drawn By:
	38 Howard St, Grange QLD		Date: 02/11/26

Storage J10 Plan 1 : 20

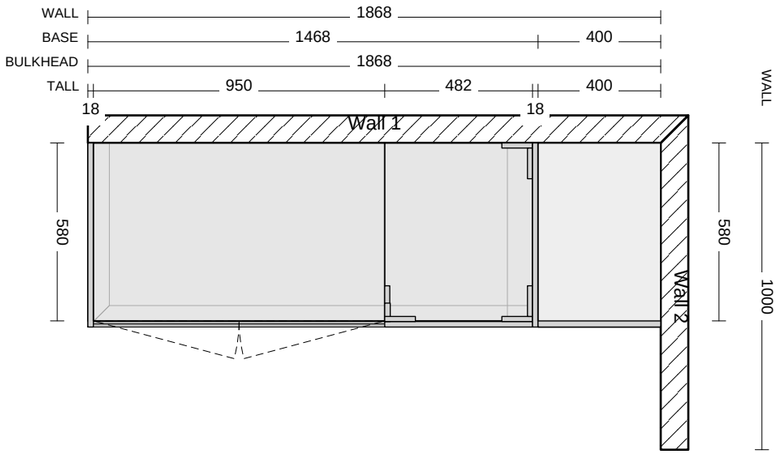

SPECIFICATIONS - Storage J10
RHK6581 Lee Smith

FRONTS + PANELS
Laminex 18mm ABS Grain - Elegant Oak
Panels: LX Abs Grain 18mm – Elegant Oak, Whiteboard 16.5mm

HANDLES
Client supplied - undrilled

CARCASS
Internal: Whiteboard 16.5mm


HARDWARE
Hinges: Blum

Client Approved Signature : ..... Date : .....

Kitchens By Resident Hero 32 Gateway Drive Phone: 0754471077 mark@residenthero.com.au www.residenthero.com.au	RHK6581 Lee Smith	**Scale: 1 : 20**	**Sheet 1 of 3**
	Storage J10	Do not scale off this drawing.	Drawn By:
	38 Howard St, Grange QLD		Date: 02/11/26

Storage J10 Elevation Wall 1


1 : 20

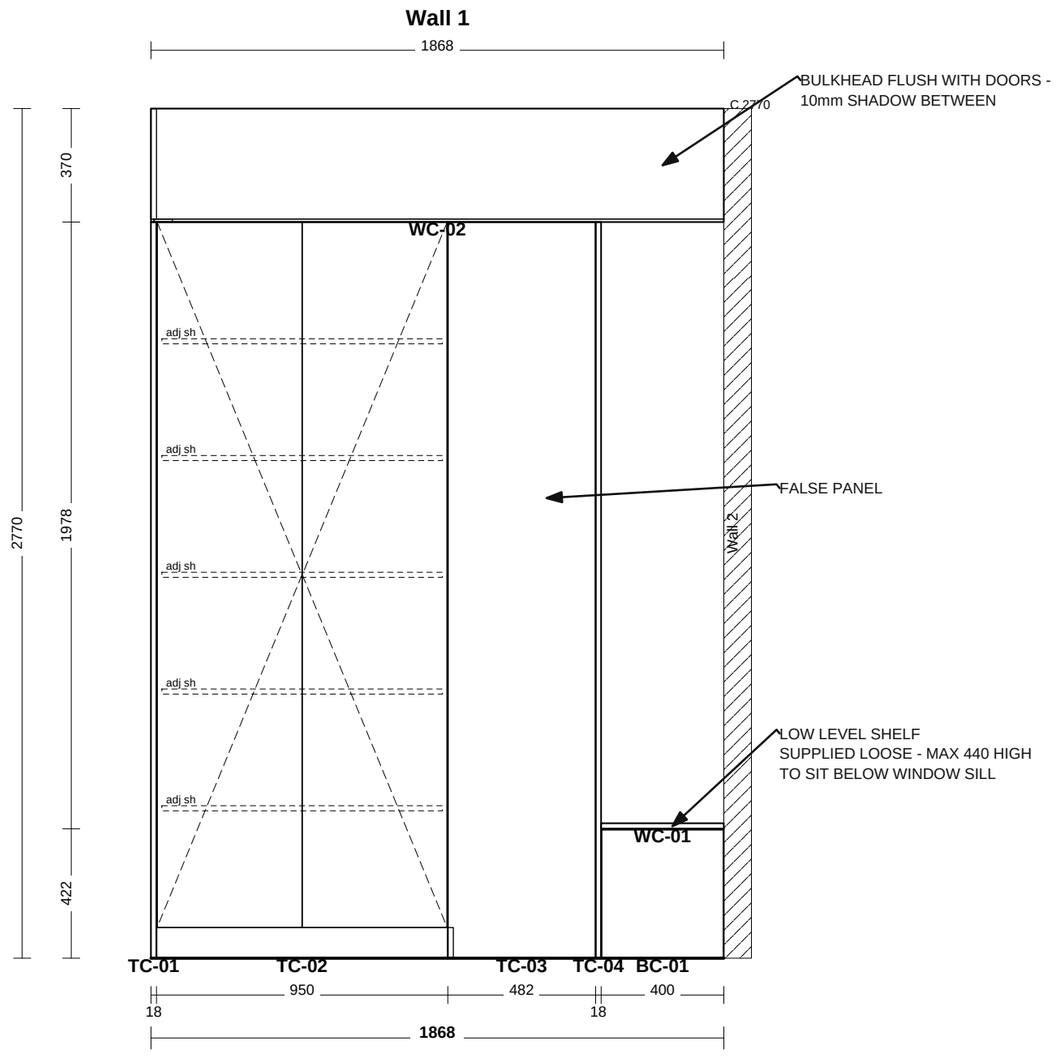


Client Approved Signature : ..... Date : .....

Kitchens By Resident Hero 32 Gateway Drive Phone: 0754471077 mark@residenthero.com.au www.residenthero.com.au	RHK6581 Lee Smith	**Scale: 1 : 20**	**Sheet 2 of 3**
	Storage J10	Do not scale off this drawing.	Drawn By:
	38 Howard St, Grange QLD		Date: 02/11/26

Storage J10 3D NTS

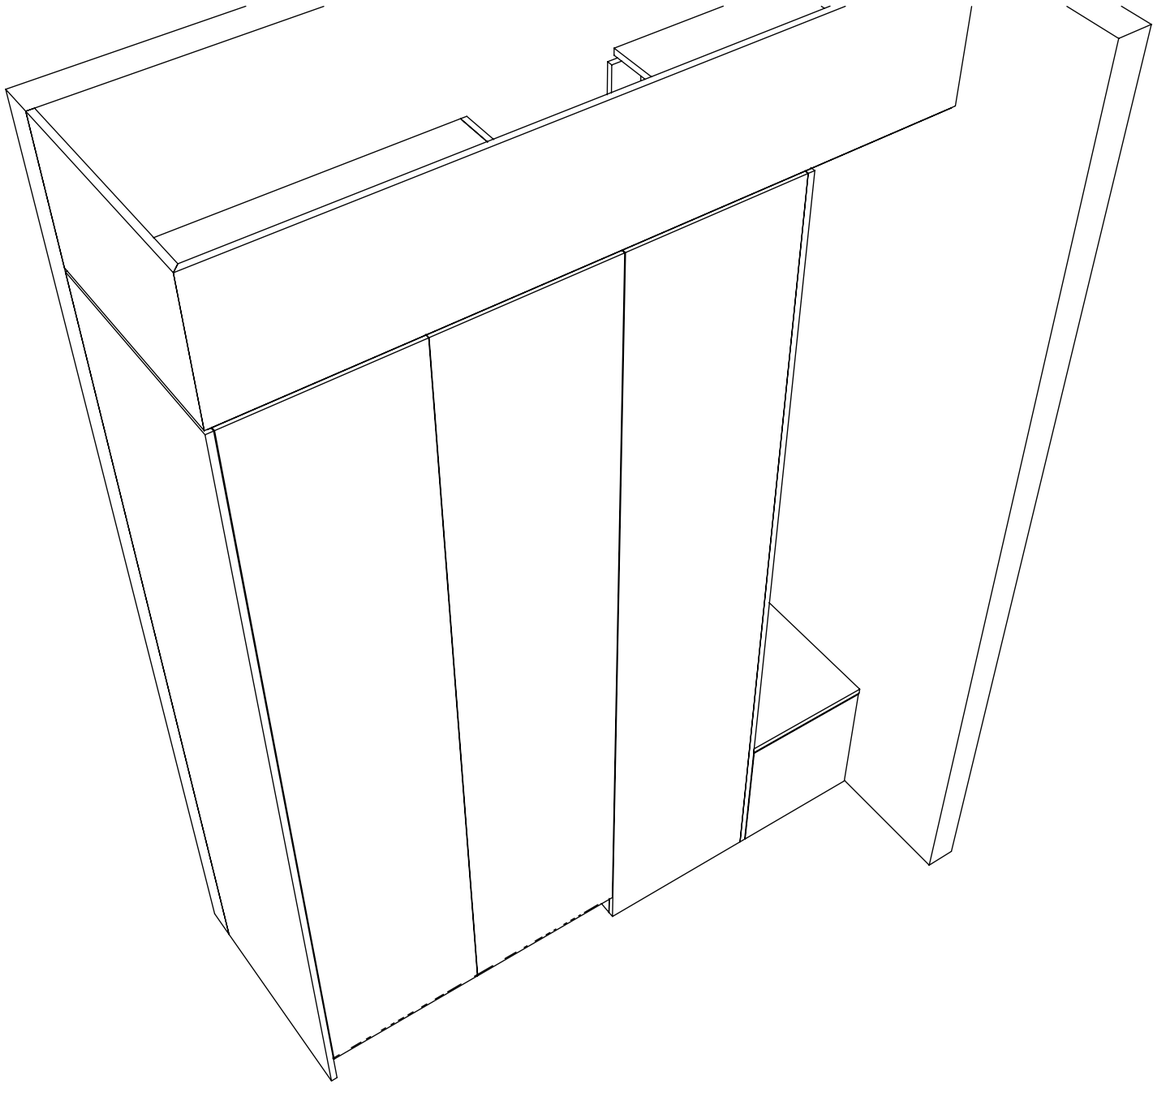


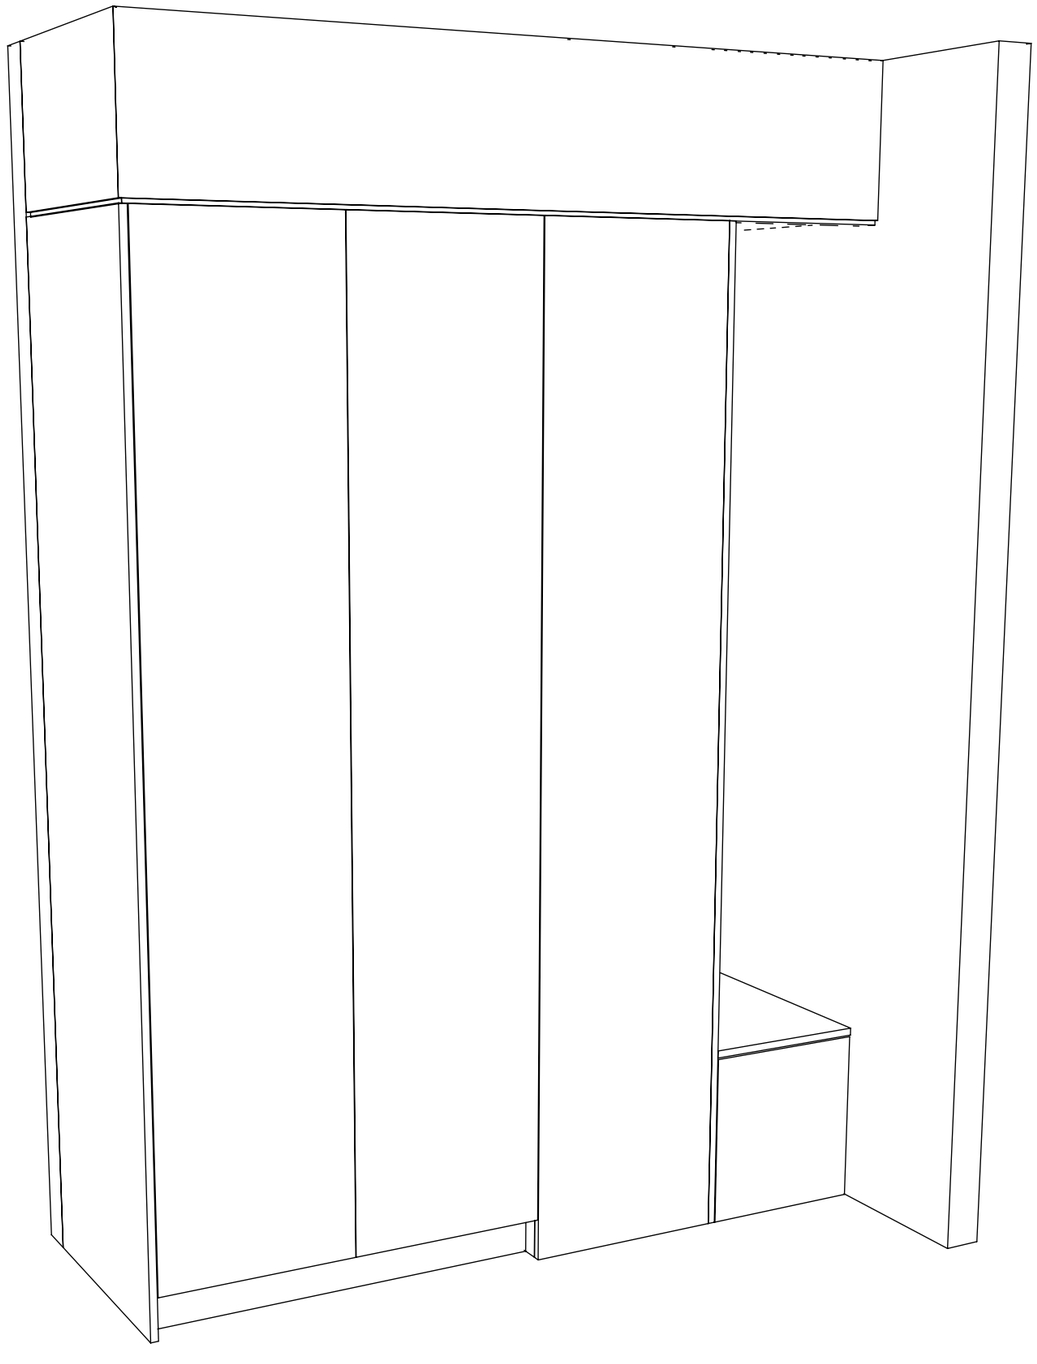

Client Approved Signature : ..... Date : .....

Kitchens By Resident Hero 32 Gateway Drive Phone: 0754471077 mark@residenthero.com.au www.residenthero.com.au	RHK6581 Lee Smith	**Scale: NTS**	**Sheet 3 of 3**
	Storage J10	Do not scale off this drawing.	Drawn By:
	38 Howard St, Grange QLD		Date: 02/11/26

WIR J11 Plan 1 : 20

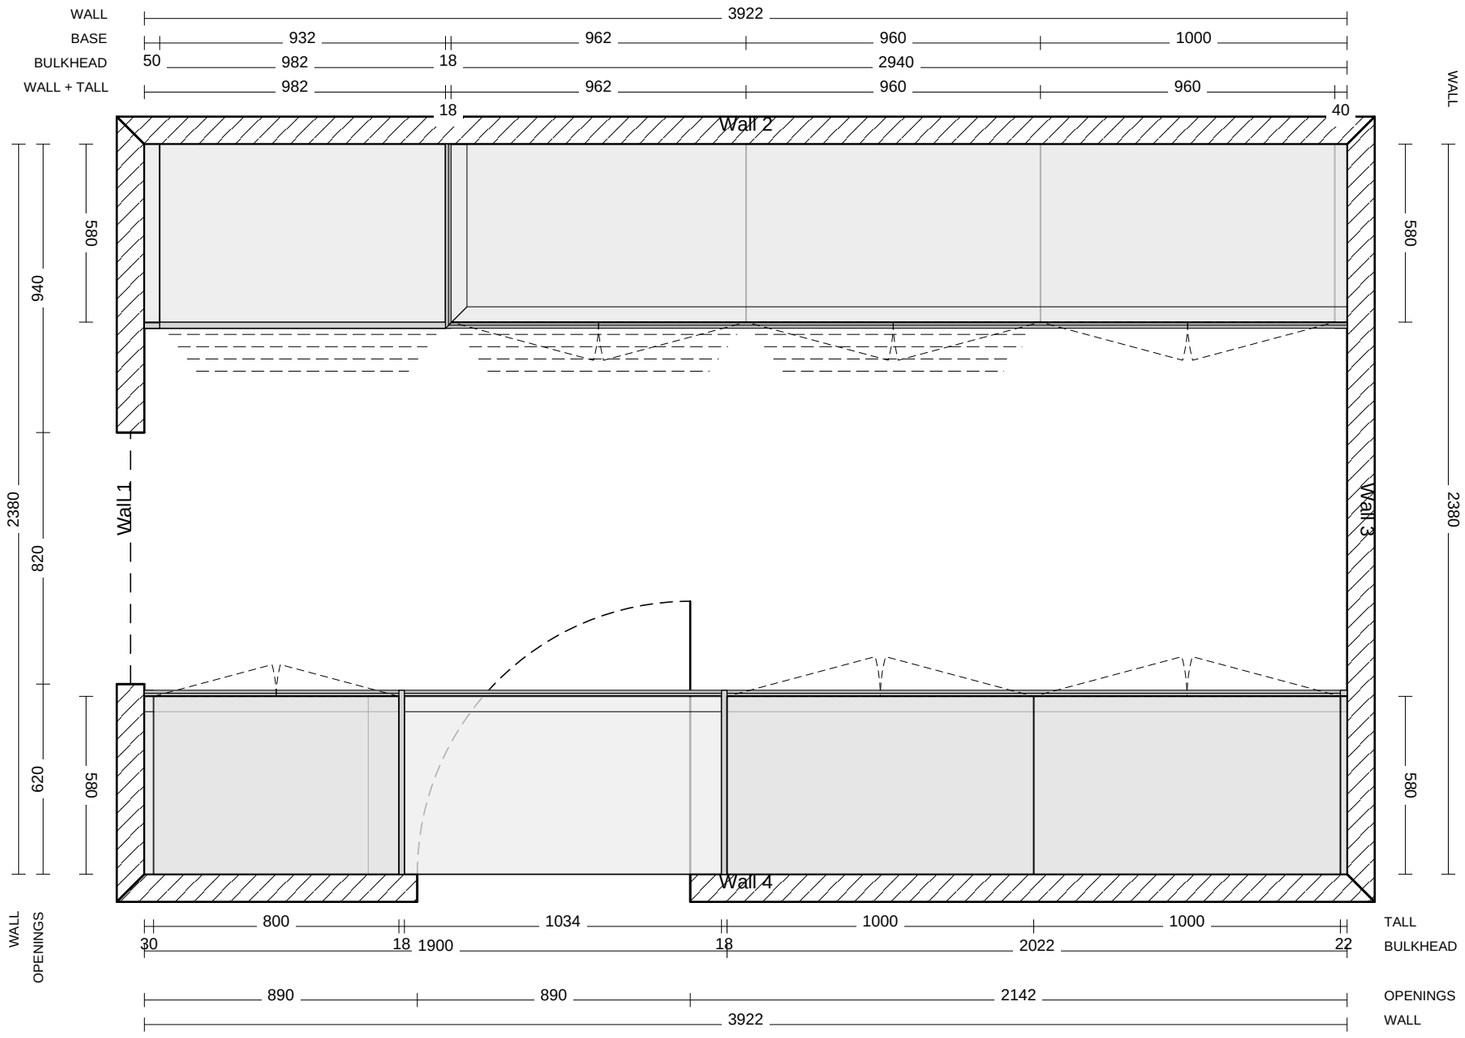

SPECIFICATIONS - WIR J11
RHK6581 Lee Smith

FRONTS + PANELS
Laminex 18mm ABS Grain - Elegant Oak
Panels: LX Abs Grain 18mm – Elegant Oak

HANDLES
Client supplied - undrilled

CARCASS
Internal: Whiteboard 16.5mm


DRAWERS
Drawer box: DTC Dragon Pro - Whiteboard 16.5mm

HARDWARE
Hinges: Blum
Runners: DTC Dragon Pro – Silk White 500mm

Client Approved Signature : ..... Date : .....

Kitchens By Resident Hero 32 Gateway Drive Phone: 0754471077 mark@residenthero.com.au www.residenthero.com.au	RHK6581 Lee Smith	**Scale: 1 : 20**	**Sheet 1 of 5**
	WIR J11	Do not scale off this drawing.	Drawn By:
	38 Howard St, Grange QLD		Date: 02/11/26


WIR J11 Elevation Wall 2 1 : 20

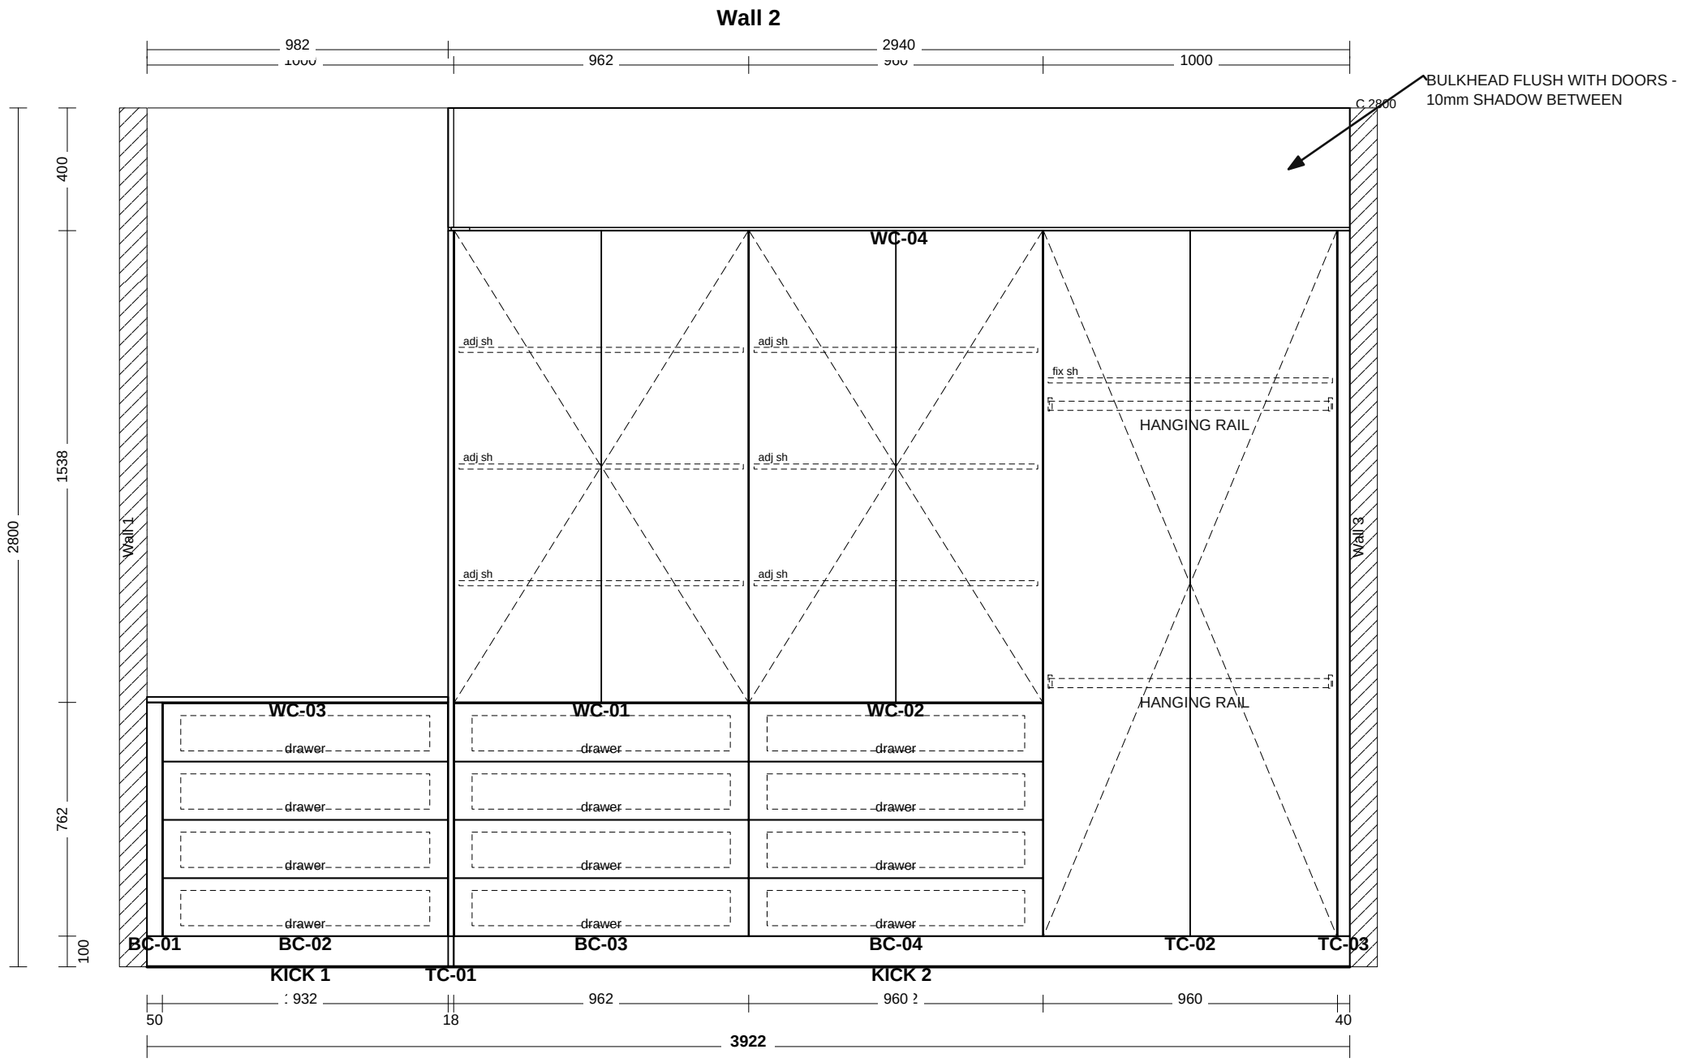

Client Approved Signature : ..... Date : .....

Kitchens By Resident Hero 32 Gateway Drive Phone: 0754471077 mark@residenthero.com.au www.residenthero.com.au	RHK6581 Lee Smith	**Scale: 1 : 20**	**Sheet 2 of 5**
	WIR J11	Do not scale off this drawing.	Drawn By:
	38 Howard St, Grange QLD		Date: 02/11/26


WIR J11 Elevation Wall 4 1 : 20

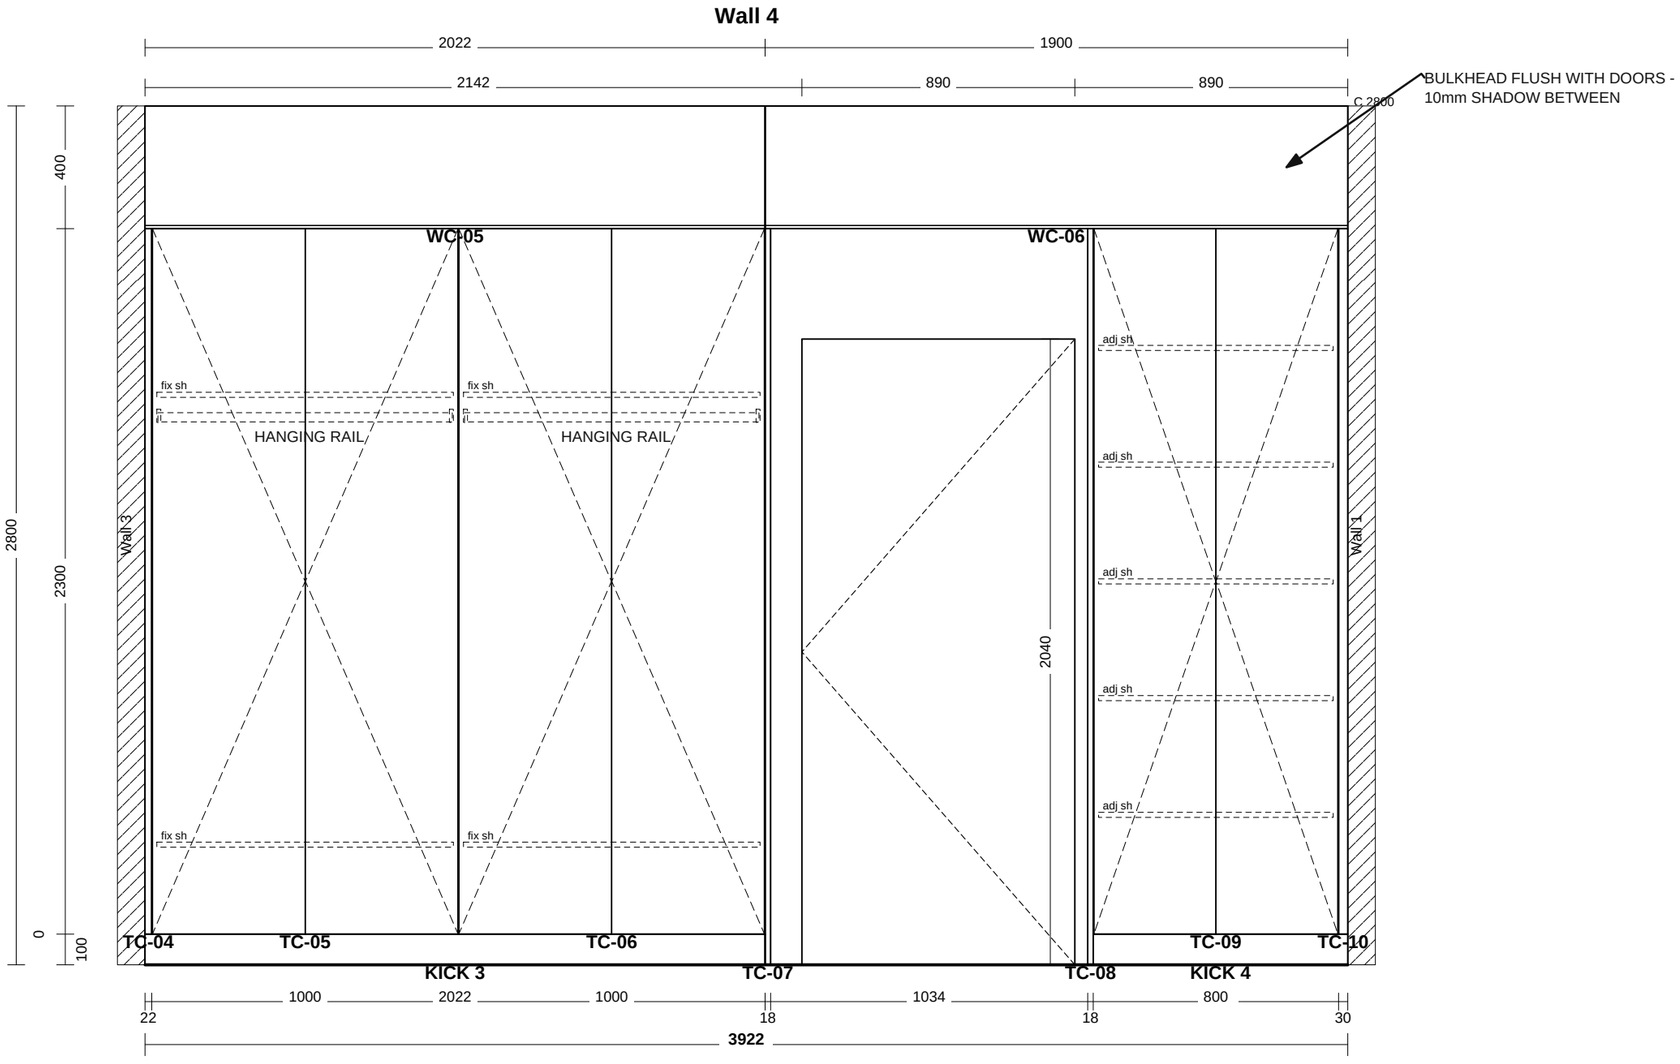


Client Approved Signature : ..... Date : .....

Kitchens By Resident Hero 32 Gateway Drive Phone: 0754471077 mark@residenthero.com.au www.residenthero.com.au	RHK6581 Lee Smith	**Scale: 1 : 20**	**Sheet 3 of 5**
	WIR J11	Do not scale off this drawing.	Drawn By:
	38 Howard St, Grange QLD		Date: 02/11/26

WIR J11 3D NTS

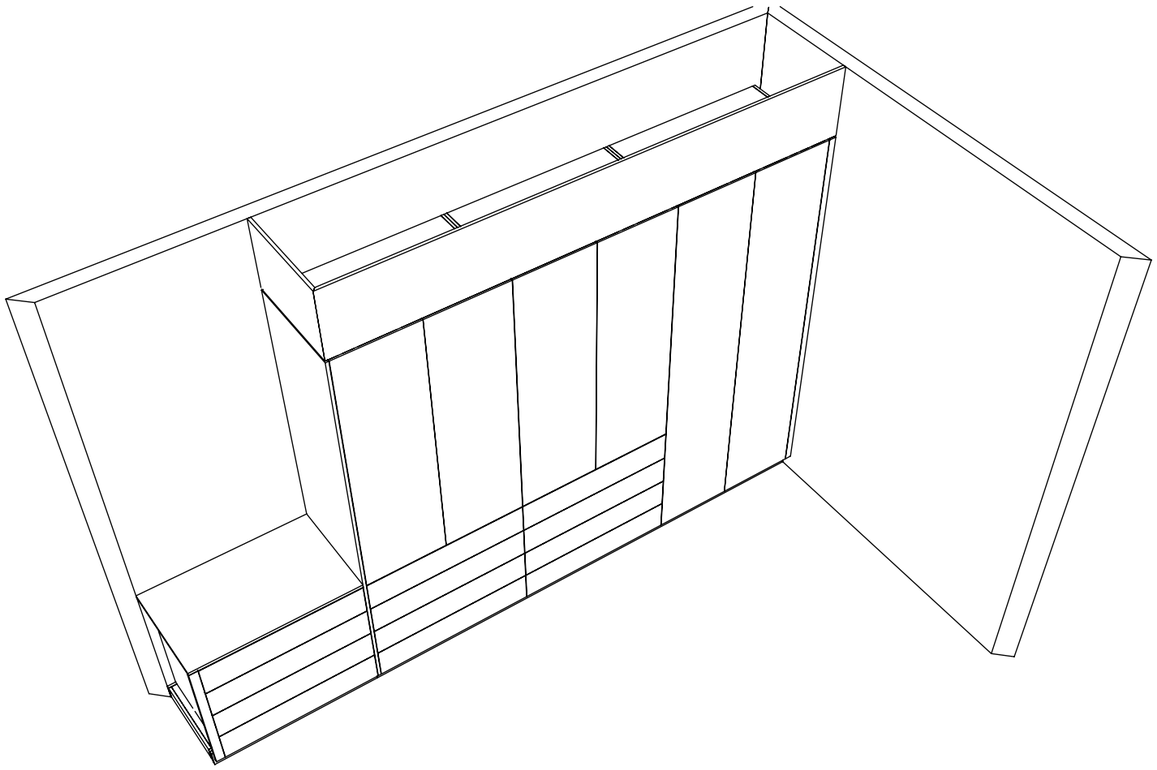


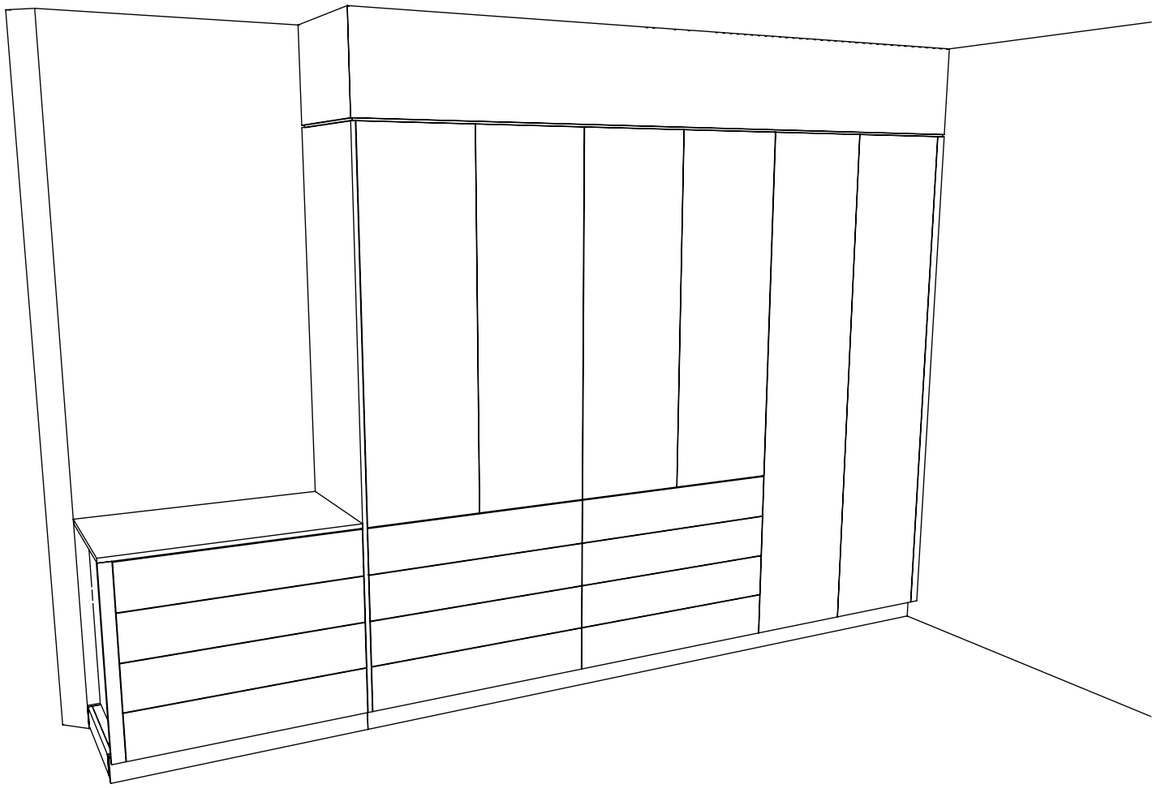

Client Approved Signature : ..... Date : .....

Kitchens By Resident Hero 32 Gateway Drive Phone: 0754471077 mark@residenthero.com.au www.residenthero.com.au	RHK6581 Lee Smith	**Scale: NTS**	**Sheet 4 of 5**
	WIR J11	Do not scale off this drawing.	Drawn By:
	38 Howard St, Grange QLD		Date: 02/11/26


WIR J11 3D NTS

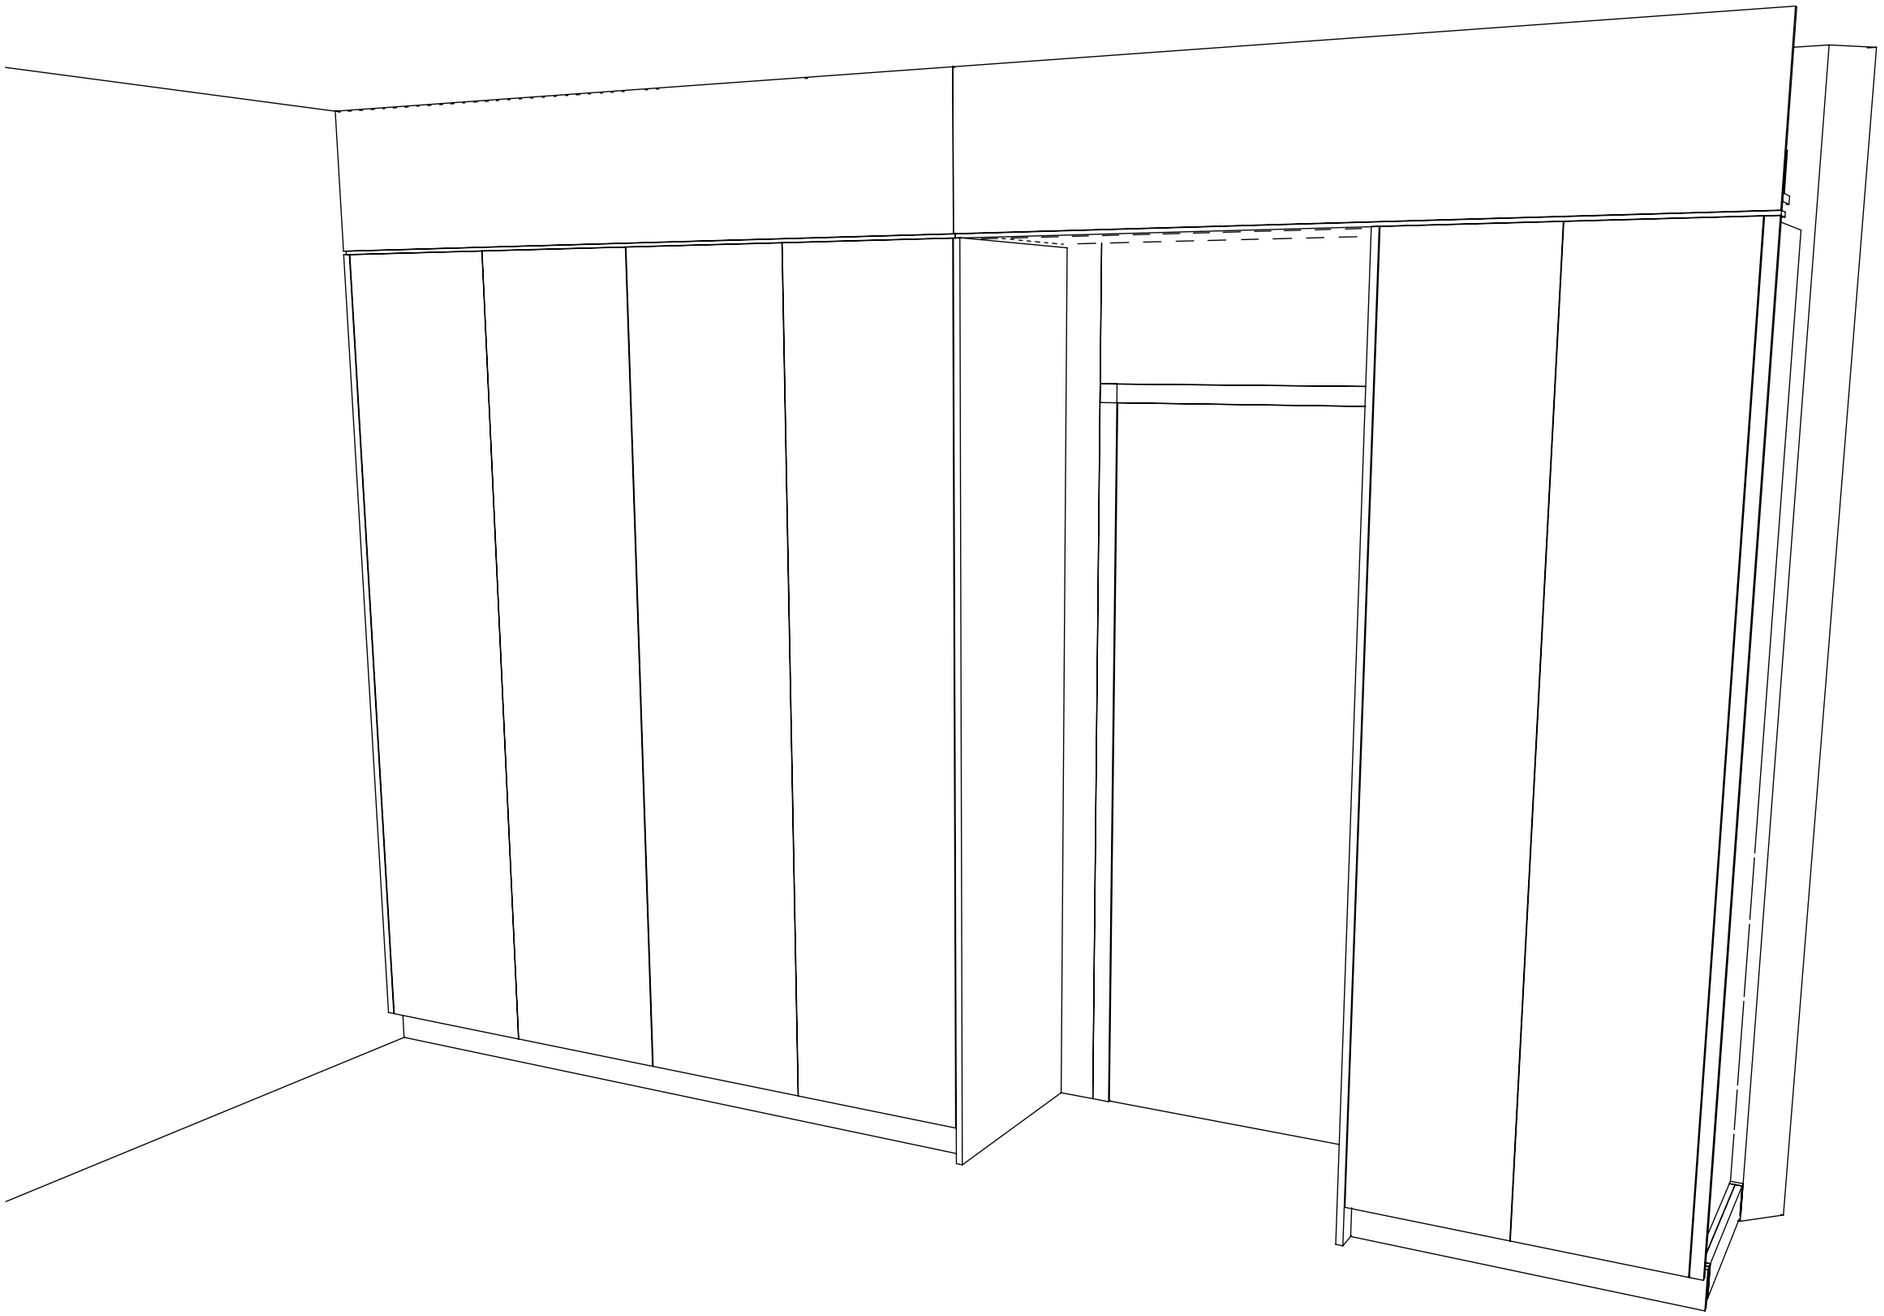

Client Approved Signature : ..... Date : .....

Kitchens By Resident Hero 32 Gateway Drive Phone: 0754471077 mark@residenthero.com.au www.residenthero.com.au	RHK6581 Lee Smith	**Scale: NTS**	**Sheet 5 of 5**
	WIR J11	Do not scale off this drawing.	Drawn By:
	38 Howard St, Grange QLD		Date: 02/11/26

Master Store J12 Plan 1 : 20

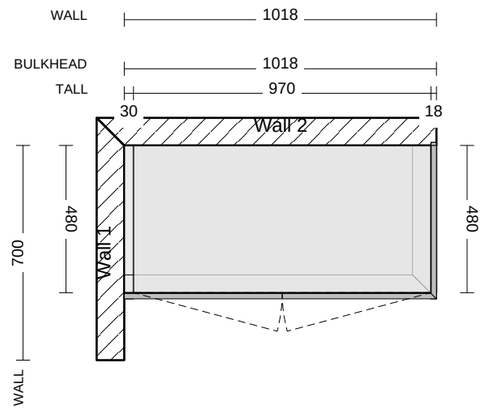

SPECIFICATIONS - Master Store J12
RHK6581 Lee Smith

FRONTS + PANELS
Laminex 18mm ABS Grain - Elegant Oak
Panels: LX Abs Grain 18mm – Elegant Oak

HANDLES
Client supplied - undrilled

CARCASS
Internal: Whiteboard 16.5mm


HARDWARE
Hinges: Blum

Client Approved Signature : ..... Date : .....

Kitchens By Resident Hero 32 Gateway Drive Phone: 0754471077 mark@residenthero.com.au www.residenthero.com.au	RHK6581 Lee Smith	**Scale: 1 : 20**	**Sheet 1 of 3**
	Master Store J12	Do not scale off this drawing.	Drawn By:
	38 Howard St, Grange QLD		Date: 02/11/26

Master Store J12 Elevation Wall 2


1 : 20

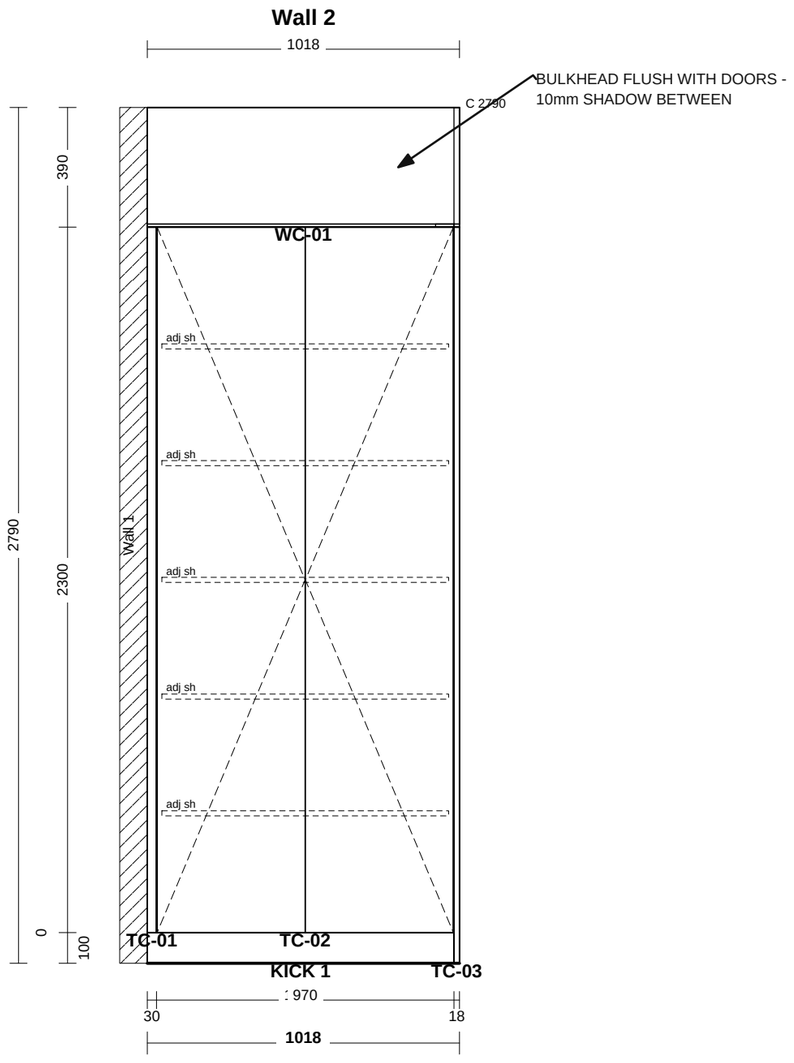


Client Approved Signature : ..... Date : .....

Kitchens By Resident Hero 32 Gateway Drive Phone: 0754471077 mark@residenthero.com.au www.residenthero.com.au	RHK6581 Lee Smith	**Scale: 1 : 20**	**Sheet 2 of 3**
	Master Store J12	Do not scale off this drawing.	Drawn By:
	38 Howard St, Grange QLD		Date: 02/11/26

Master Store J12 3D NTS

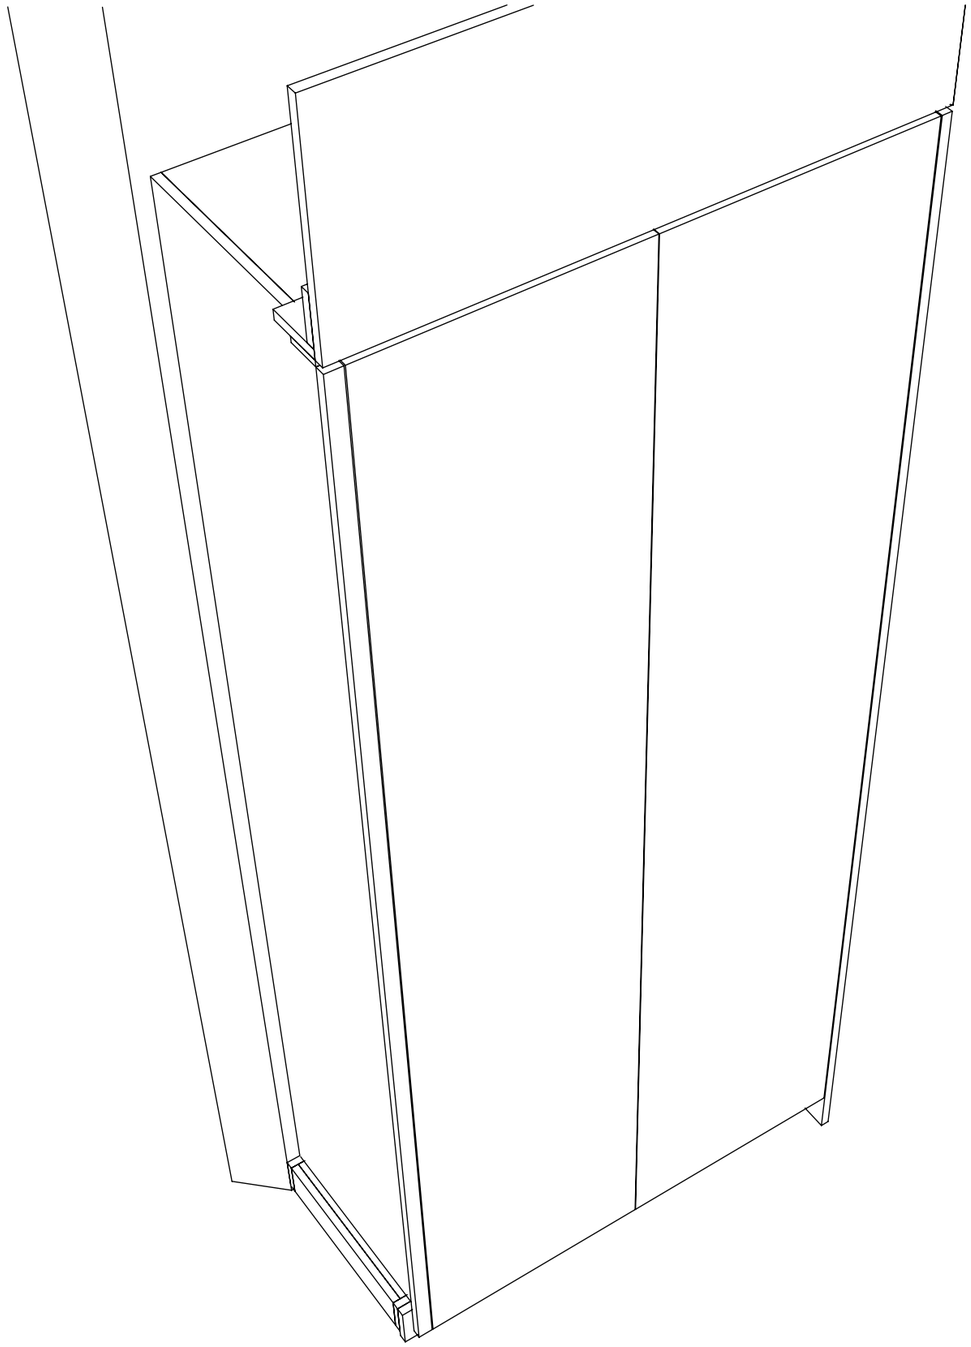

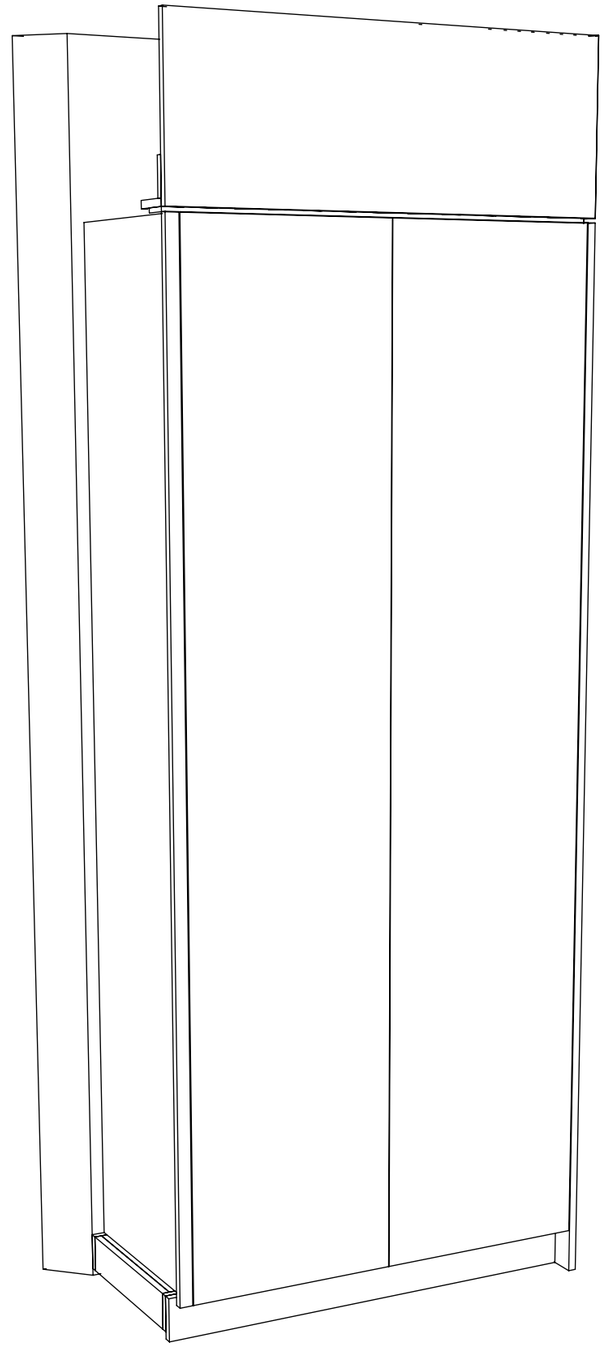

Client Approved Signature : ..... Date : .....

Kitchens By Resident Hero 32 Gateway Drive Phone: 0754471077 mark@residenthero.com.au www.residenthero.com.au	RHK6581 Lee Smith	**Scale: NTS**	**Sheet 3 of 3**
	Master Store J12	Do not scale off this drawing.	Drawn By:
	38 Howard St, Grange QLD		Date: 02/11/26