
Milross A109 - LIGHTING & SWITCHING

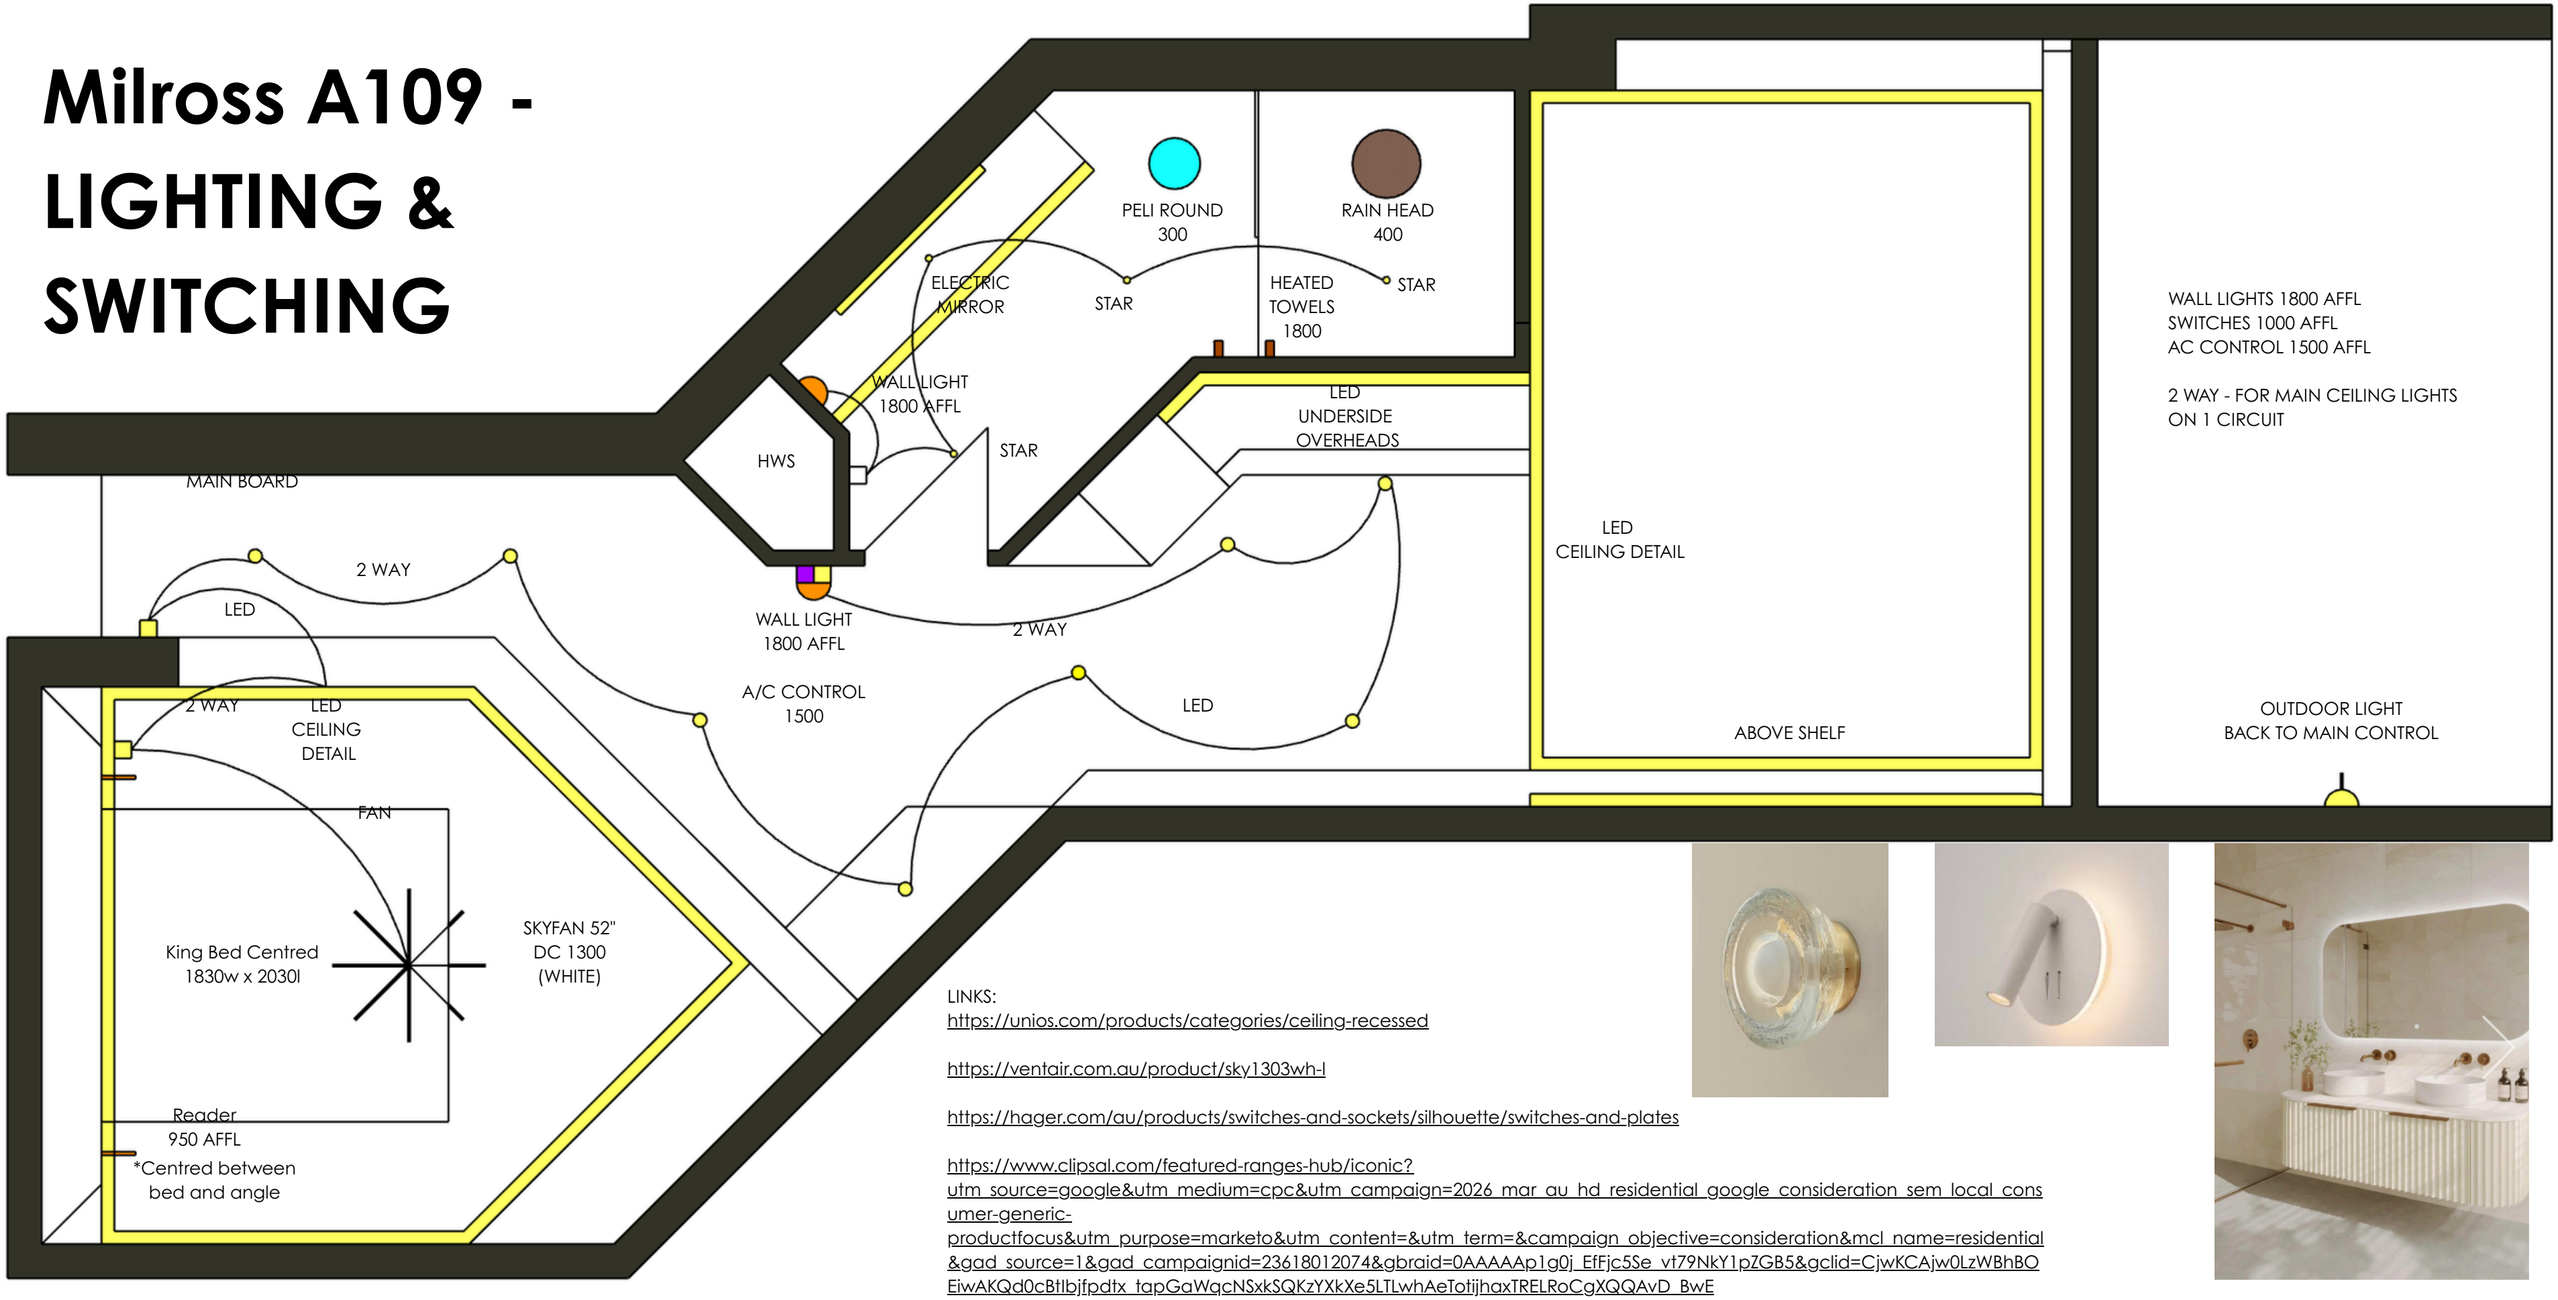

LINKS:
https://unios.com/products/categories/ceiling-recessed


https://ventair.com.au/product/sky1303wh-l

https://hager.com/au/products/switches-and-sockets/silhouette/switches-and-plates

https://www.clipsal.com/featured-ranges-hub/iconic?utm_source=google&utm_medium=cpc&utm_campaign=2026_mar_au_hd_residential_google_consideration_sem_local_consumer-generic-productfocus&utm_purpose=marketo&utm_content=&utm_term=&campaign_objective=consideration&mcl_name=residential&gad_source=1&gad_campaignid=23618012074&gbraid=0AAAAAp1g0j_EfFjc5Se_vt79NkY1pZGB5&gclid=CjwKCAjw0LzWBhBOEiwAKQd0cBtIbjfpdtx_tapGaWqcNSxkSQKzYXkXe5LTLwhAeTotijhaxTRELRoCgXQQAvD_BwE

Milross A109 - BATHROOM



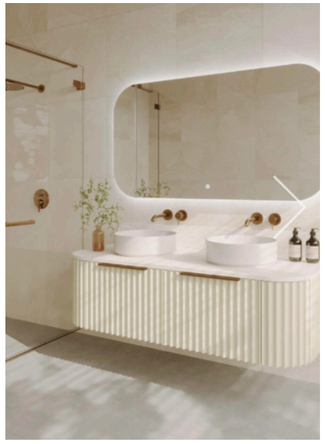

1800 AFFL

1550 AFFL


GPO + BREACH 1000 AFFL

GPO - 520 AFFL

WASTE - 450 AFFL

FFL

GPO's fit off to back
off cabinet
with curly cords
to drawers

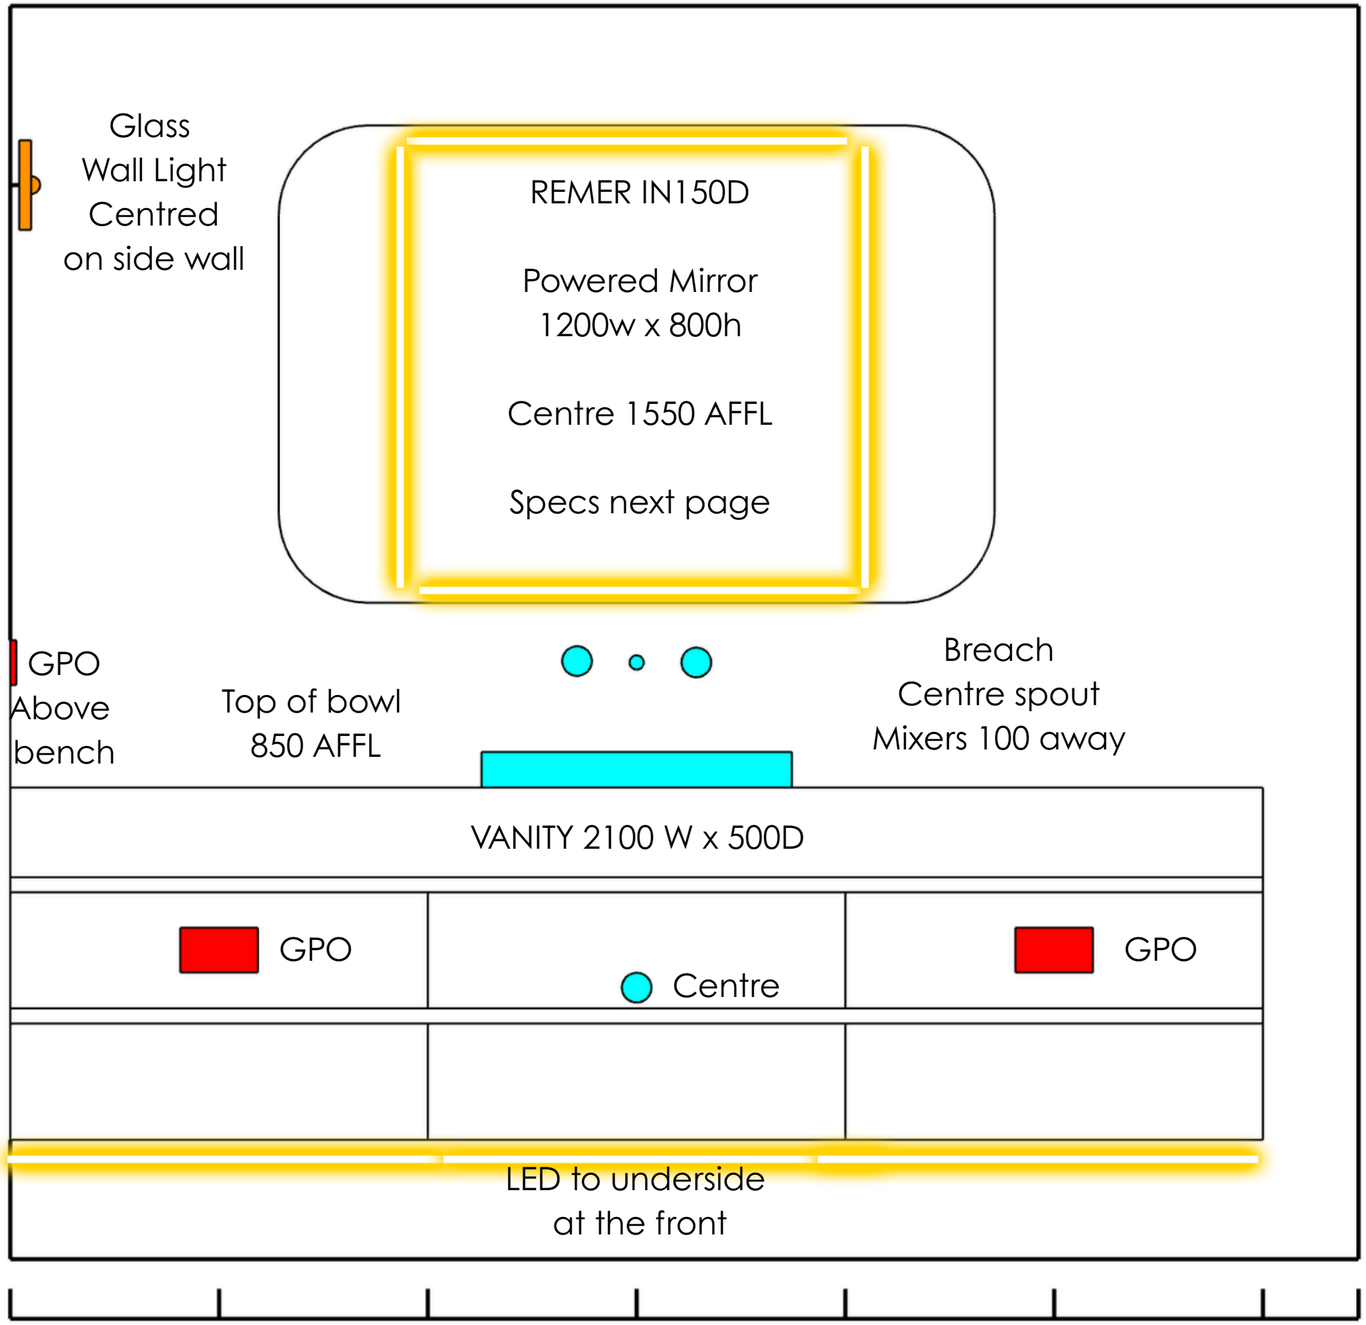


350 + 20
Villa, Tile and glue

1050 + 20
Centre

1750 + 20
Villa, Tile and glue

Milross A109 - LOUNGE

IMPORTANT: Lounge unit finishes directly under ceiling transition to kitchen dining

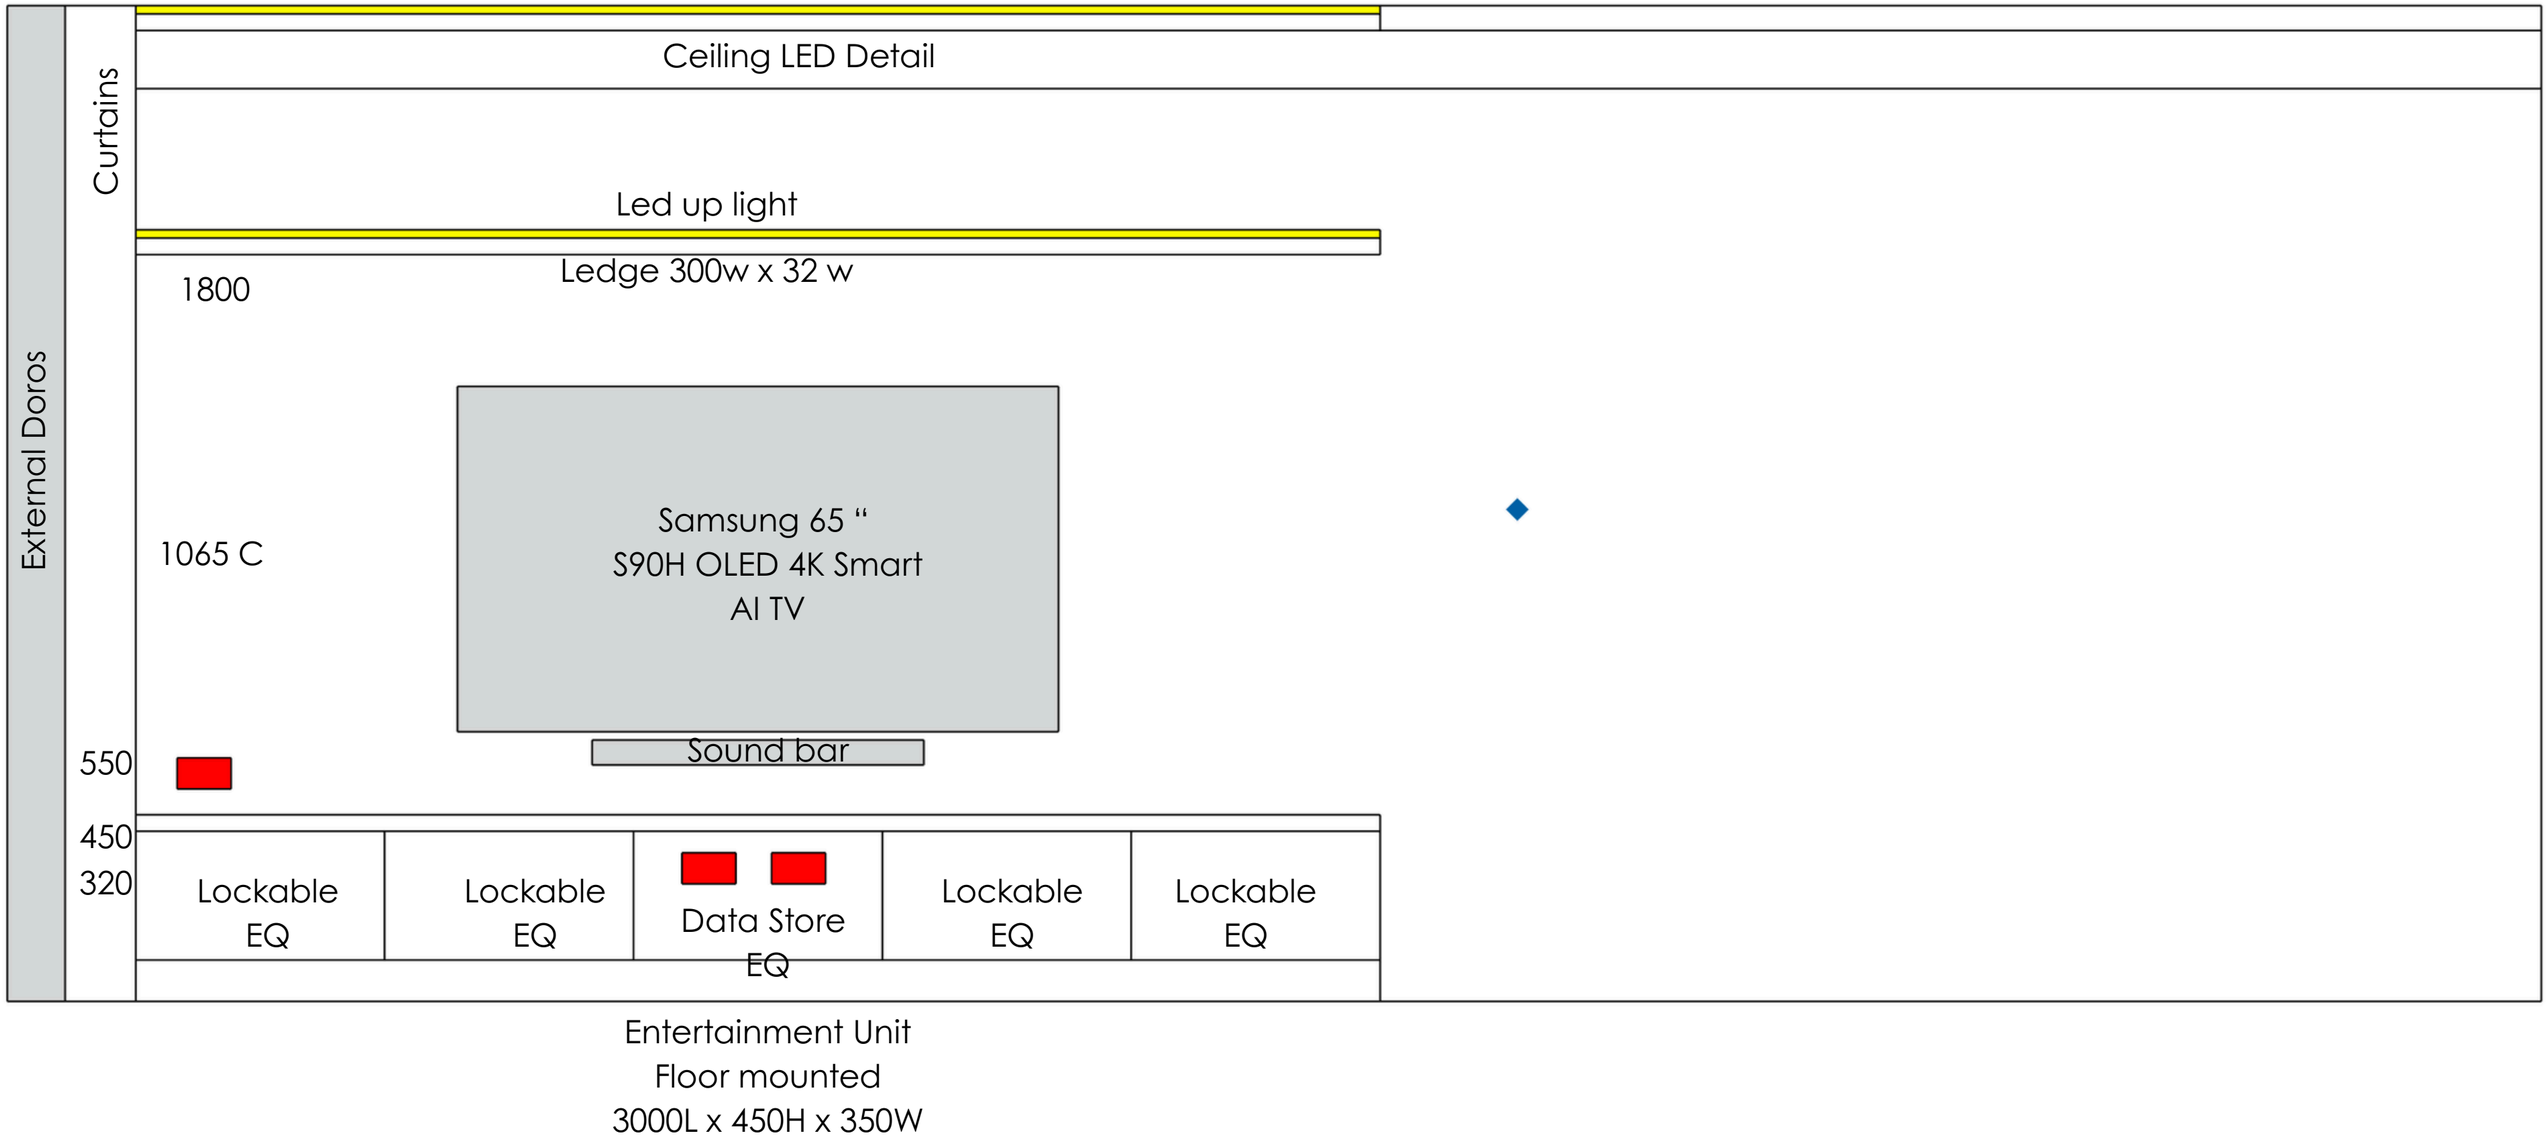


Milross A109 - LOUNGE




Entertainment Unit
Floor mounted
3000L x 450H x 350W


Milross A109 - KITCHEN

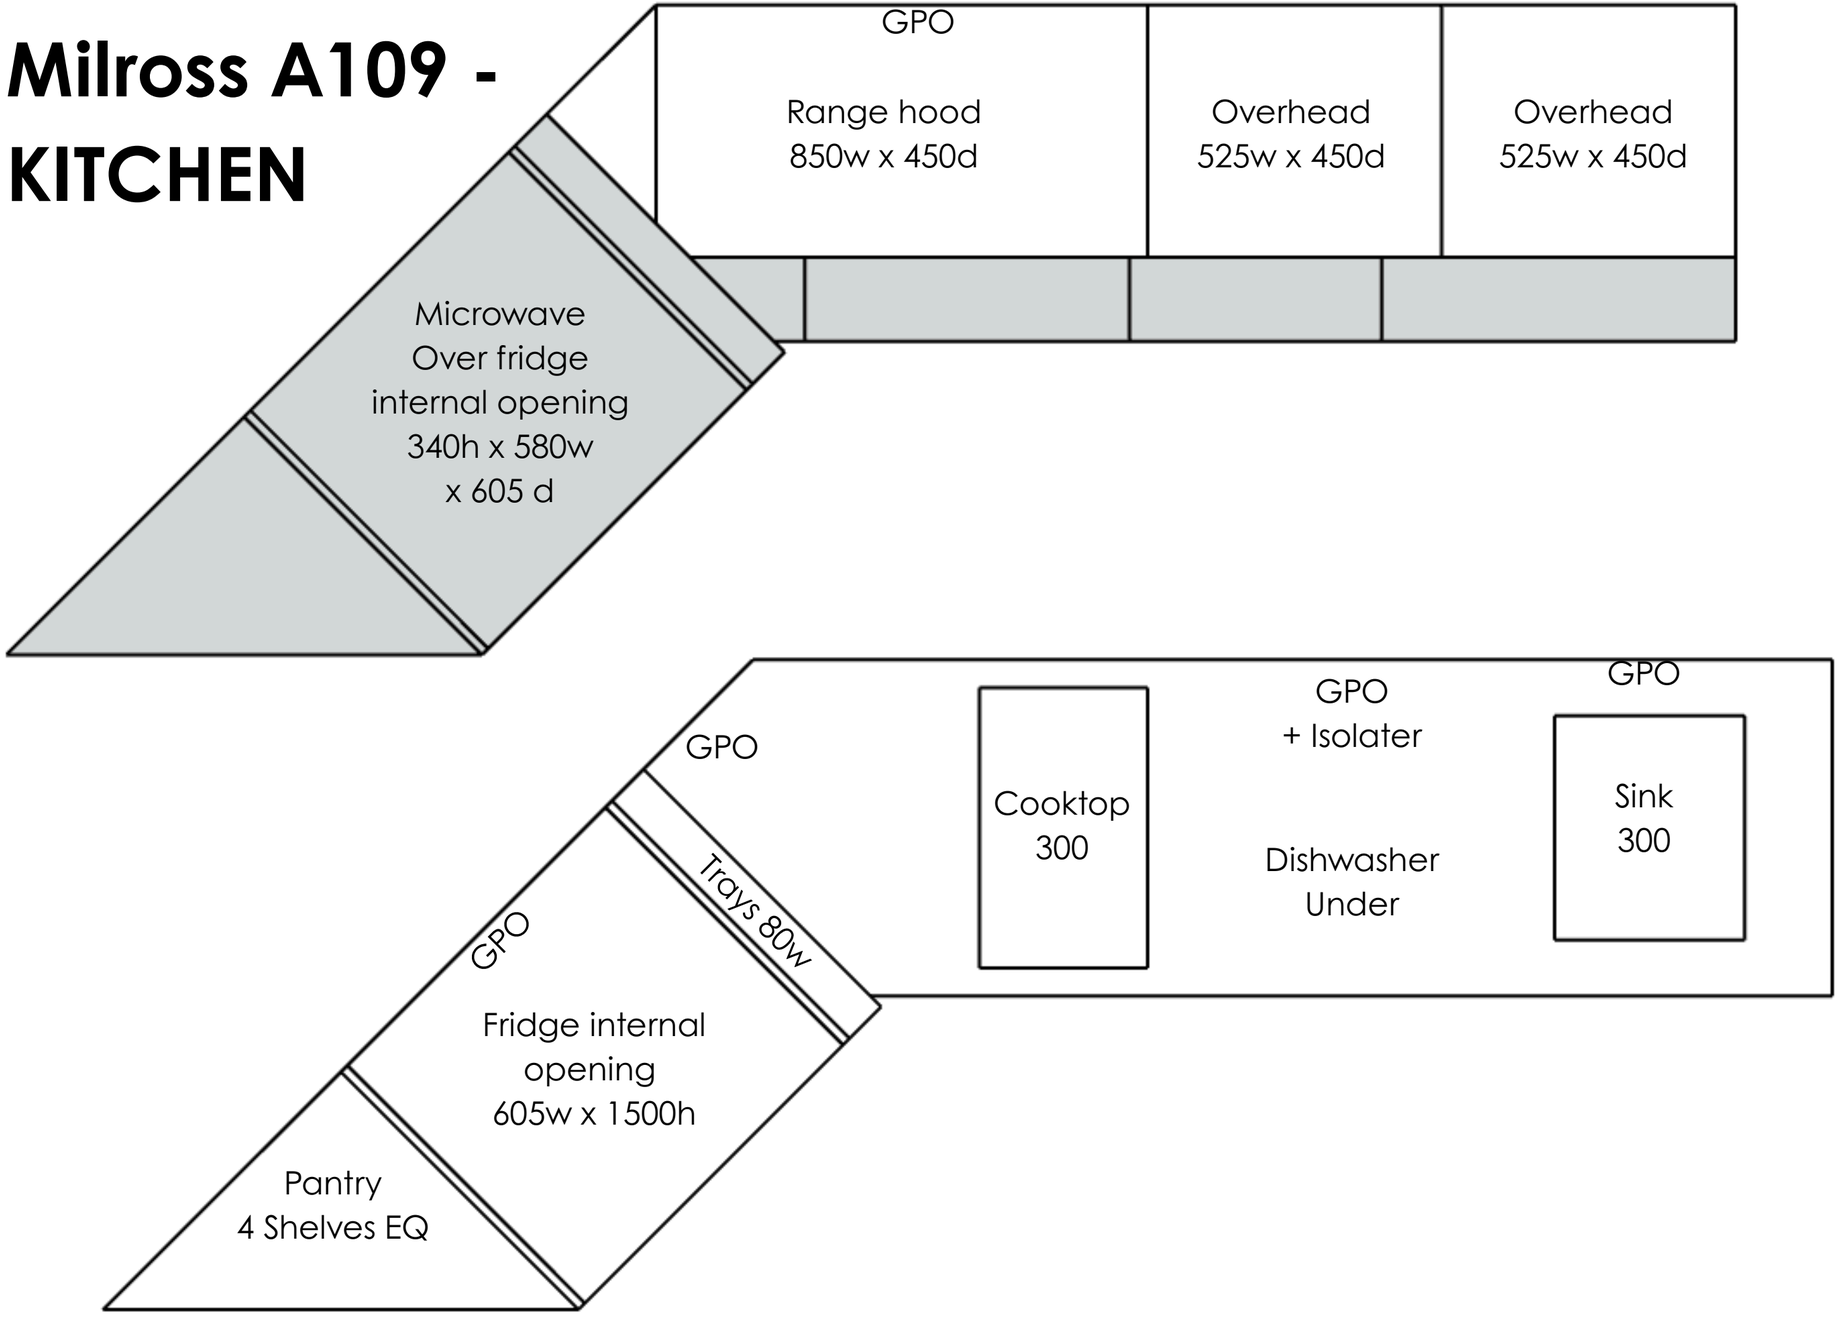

Milross A109 - KITCHEN

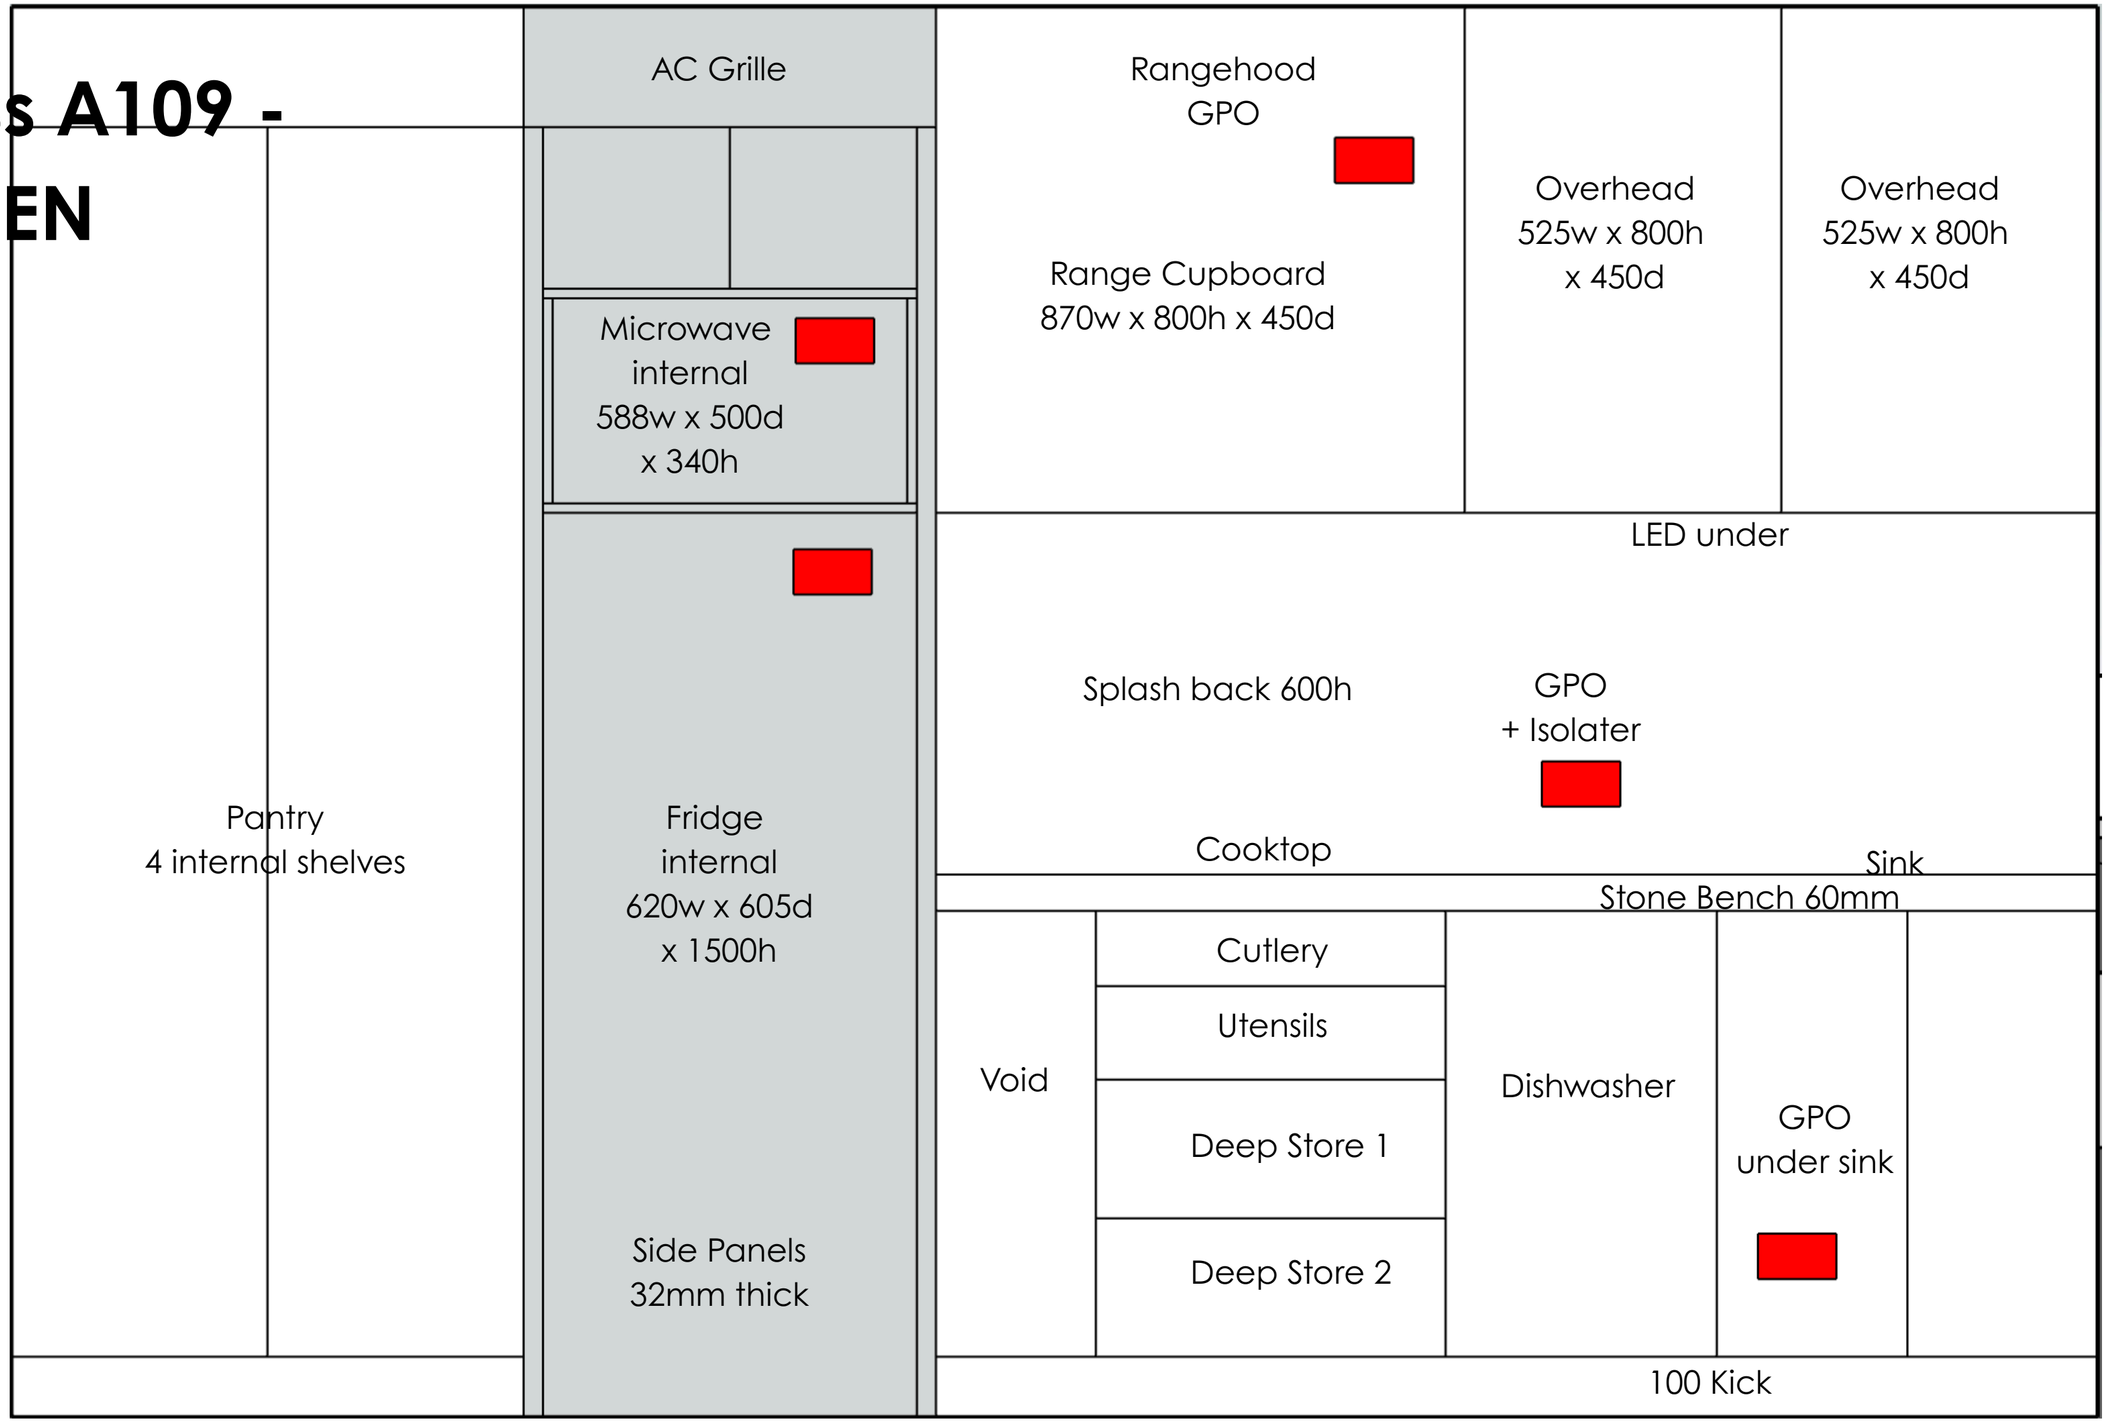

Milross A109 -
KITCHEN

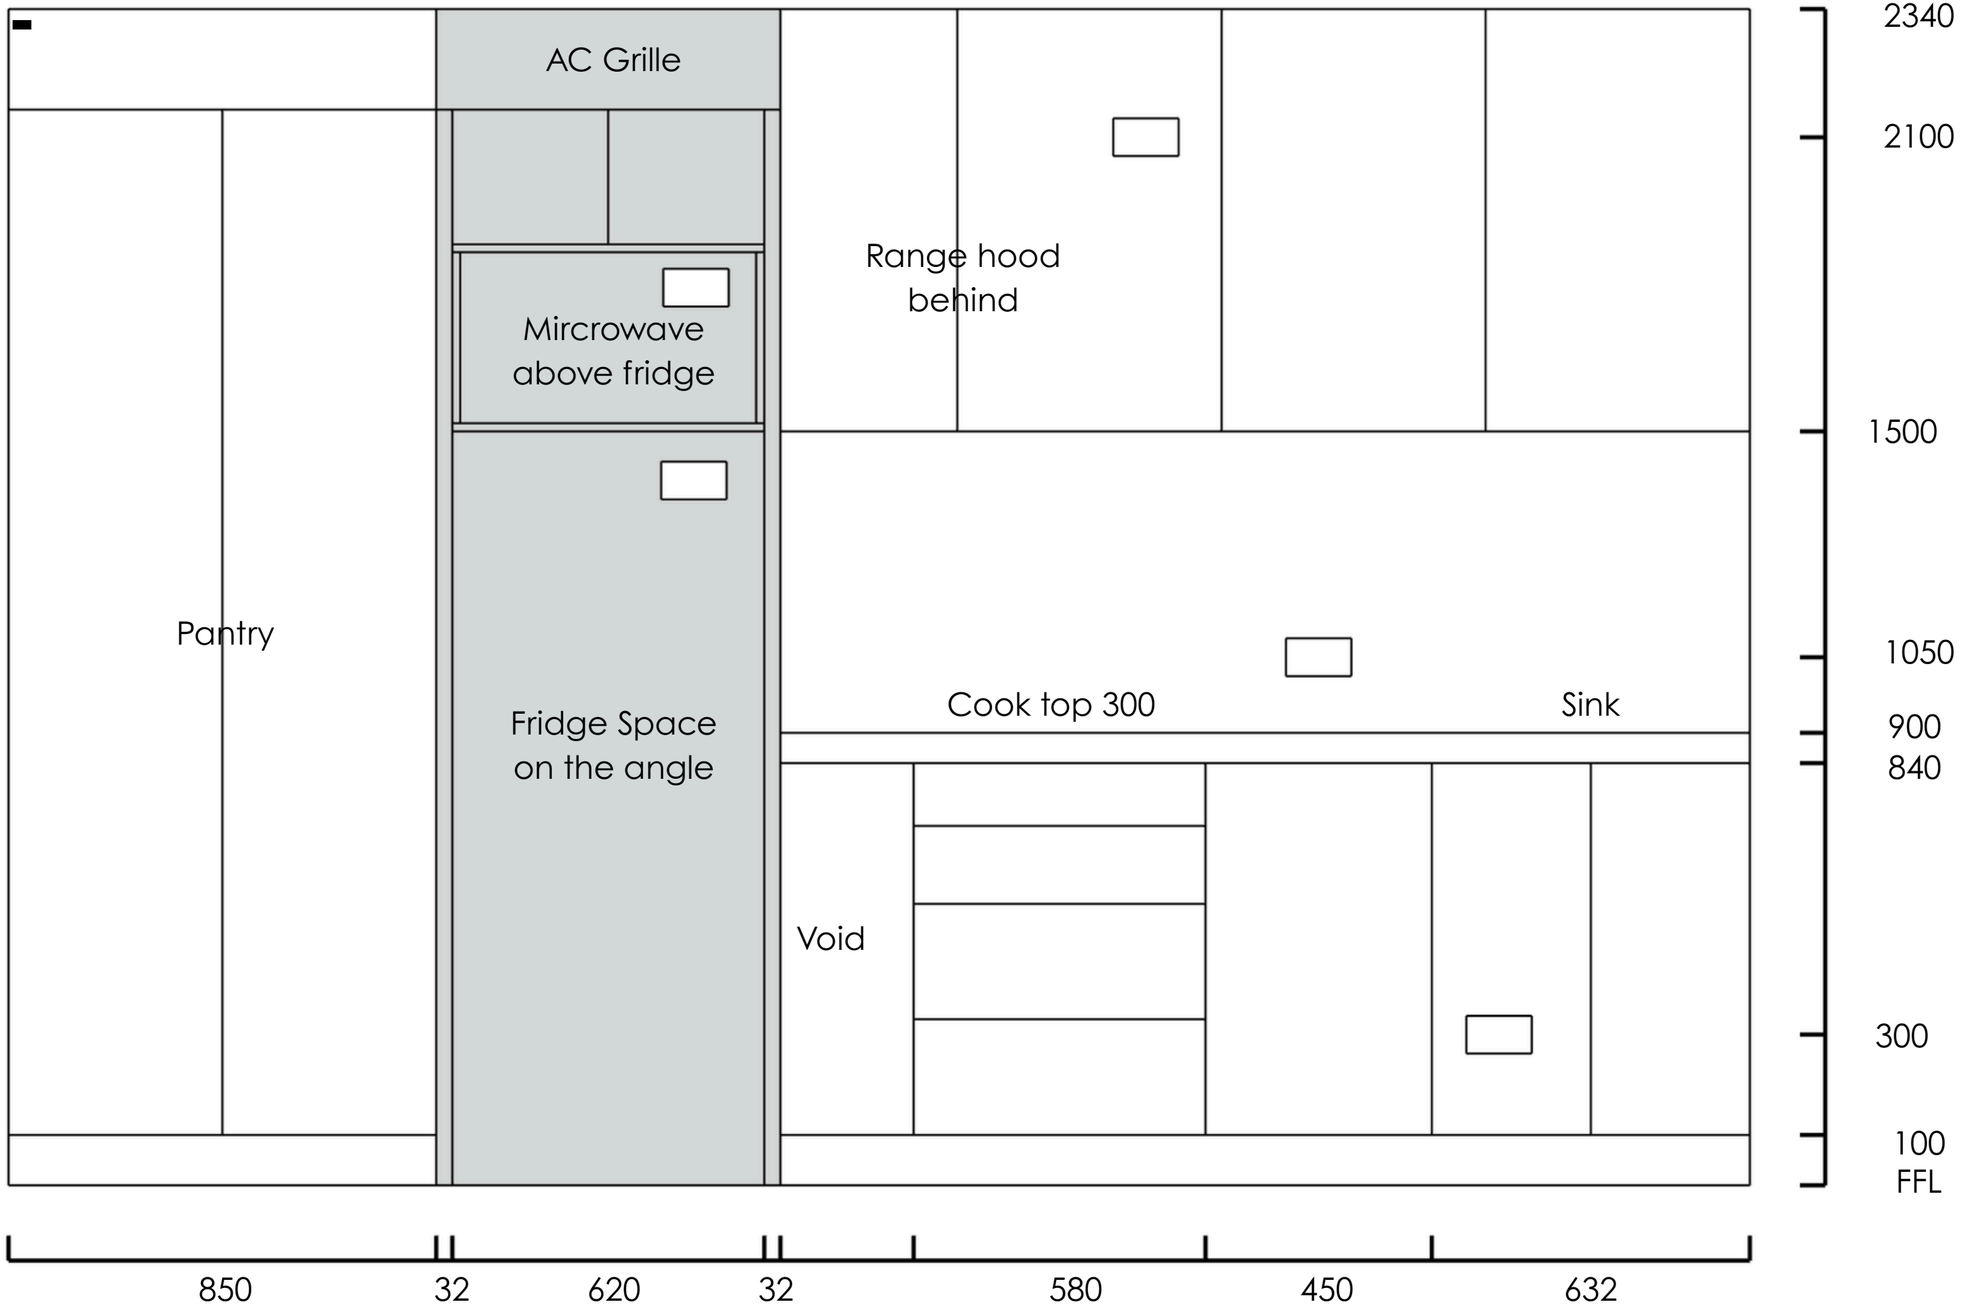

Milross A109 - KITCHEN


Bulkhead
200-250
for AC Grille



Milross A109 - ROBE



Back wall 1730

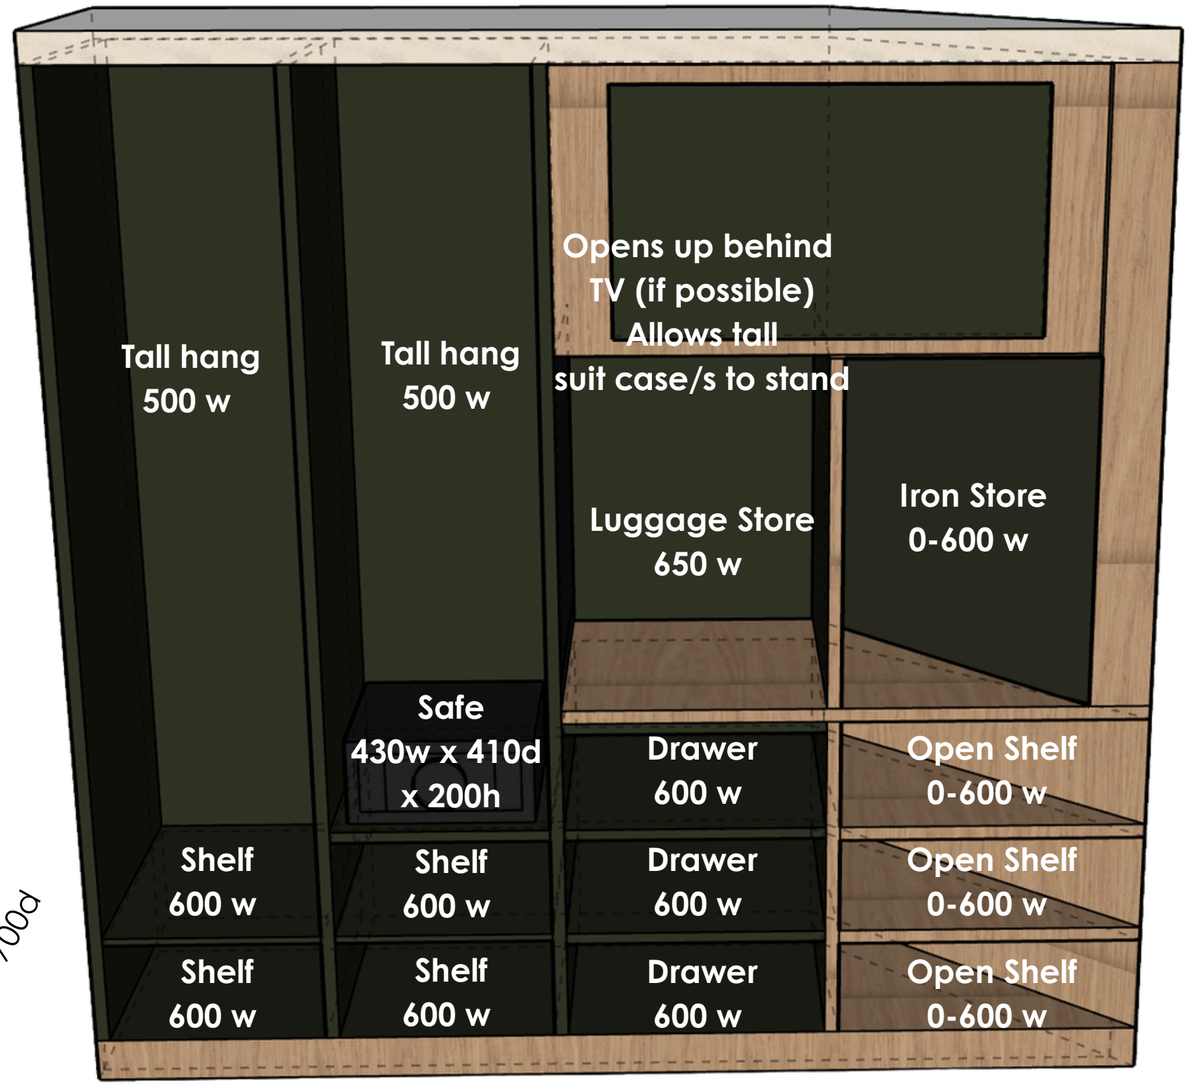

Robe 700d

front measurement 2430

Milross A109 - STUDY NOOK

Top stone height
= 750h

