
Bed 1 Robe + Study Plan

1 : 20

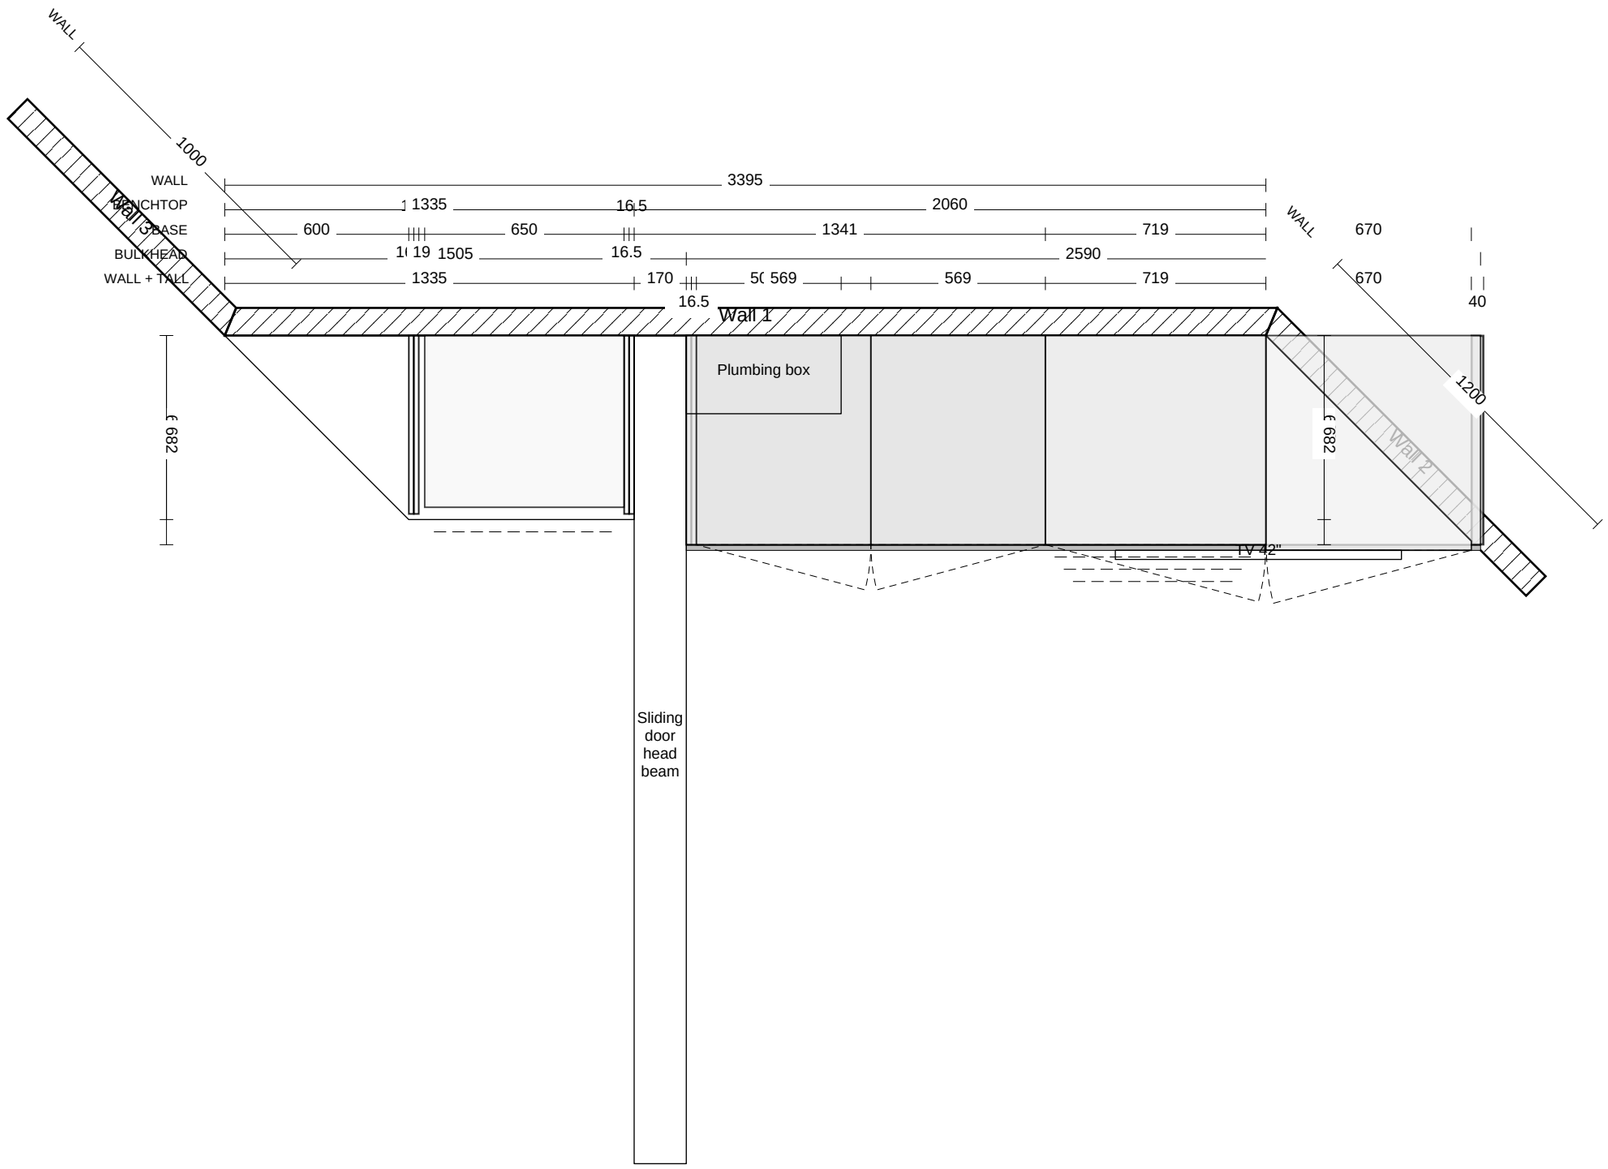

SPECIFICATIONS - Bed 1 Robe + Study
RHK6586 Greystone Constructions

BENCHTOP
-
Study desk 20mm stone, 45 deg waterfall end. Product + colour TBC

FRONTS + PANELS
Flat Grain — Polytec - Boston Oak Woodmatt
PT Woodmatt Boston Oak flat. 32 end panels (2 x 16.5 for now)
Kick: to match fronts

HANDLES
Push to open doors, finger pull drawers

CARCASS
Internal: Nikpol 16mm – Diamond Grey
External: PT Woodmatt 16mm – Boston Oak Woodmatt (BC-07)

HARDWARE
Hinges: Blum
Runners: DTC Dragon Pro 500mm


ACCESSORIES
30x15 oval hanging rails x 2. Safe by others

Client Approved Signature : ..... Date : .....

Kitchens By Resident Hero
32 Gateway Drive
Phone: 0754471077
mark@residenthero.com.au
www.residenthero.com.au

RHK6586 Greystone Constructions	**Scale: 1 : 20**	**Sheet 1 of 3**
Bed 1 Robe + Study	Do not scale off this drawing.	Drawn By:
		Date: 28/10/26


Bed 1 Robe + Study Elevation Wall 1 1 : 20

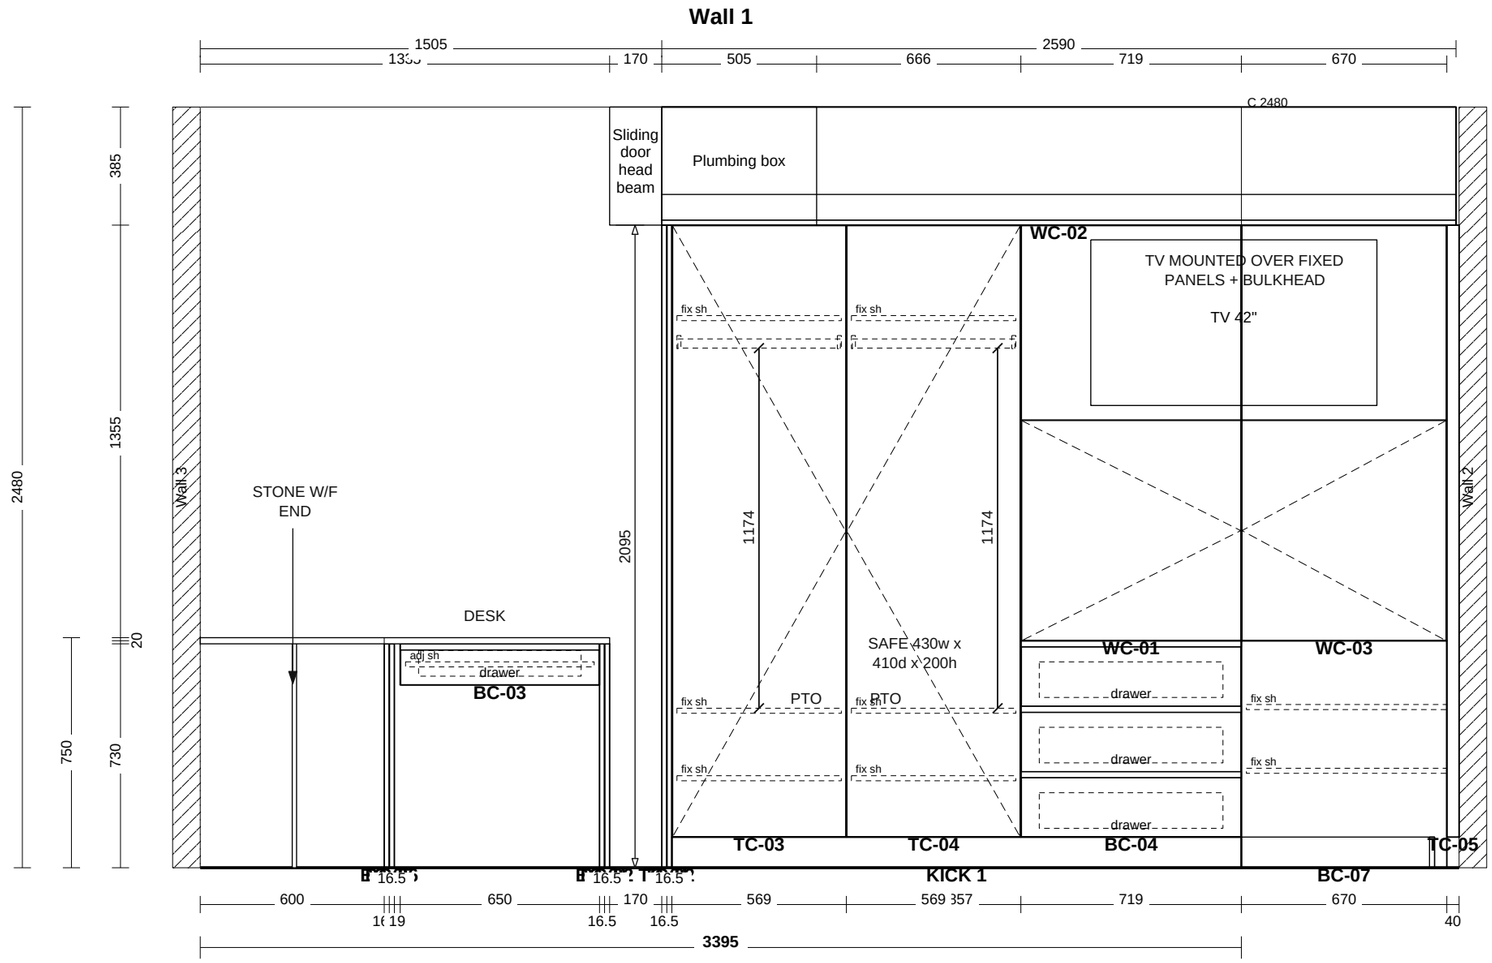


Client Approved Signature : ..... Date : .....

Kitchens By Resident Hero 32 Gateway Drive Phone: 0754471077 mark@residenthero.com.au www.residenthero.com.au	RHK6586 Greystone Constructions	**Scale: 1 : 20**	**Sheet 2 of 3**
	Bed 1 Robe + Study	Do not scale off this drawing.	Drawn By:
			Date: 28/10/26

Bed 1 Robe + Study 3D NTS

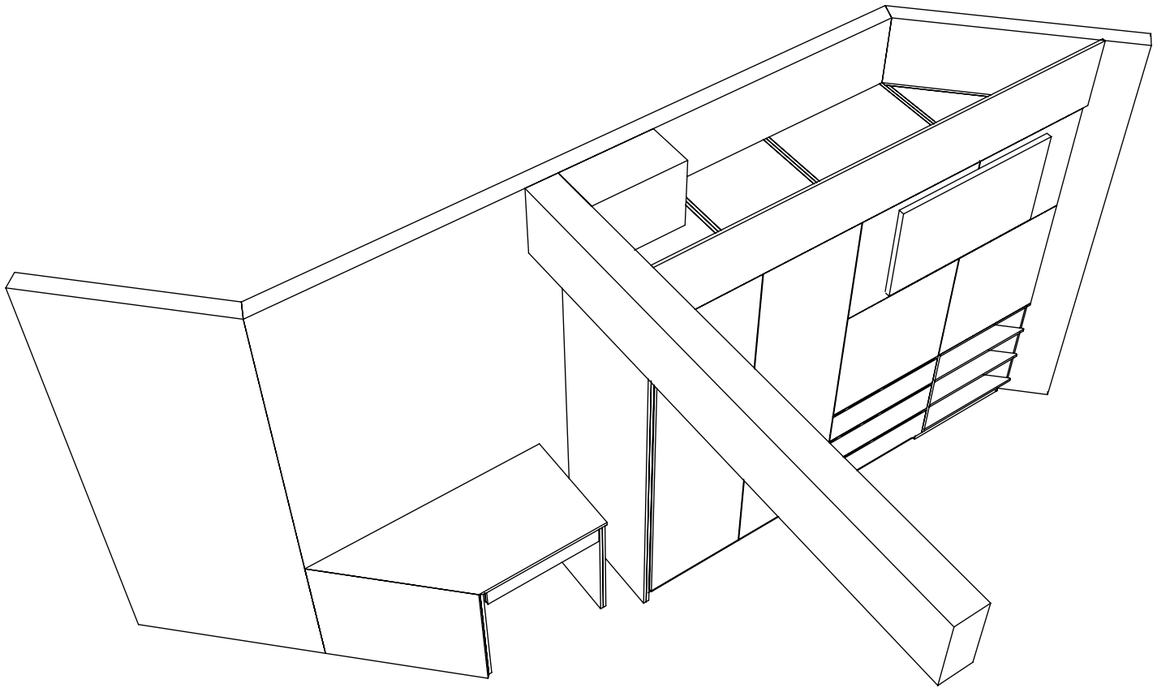

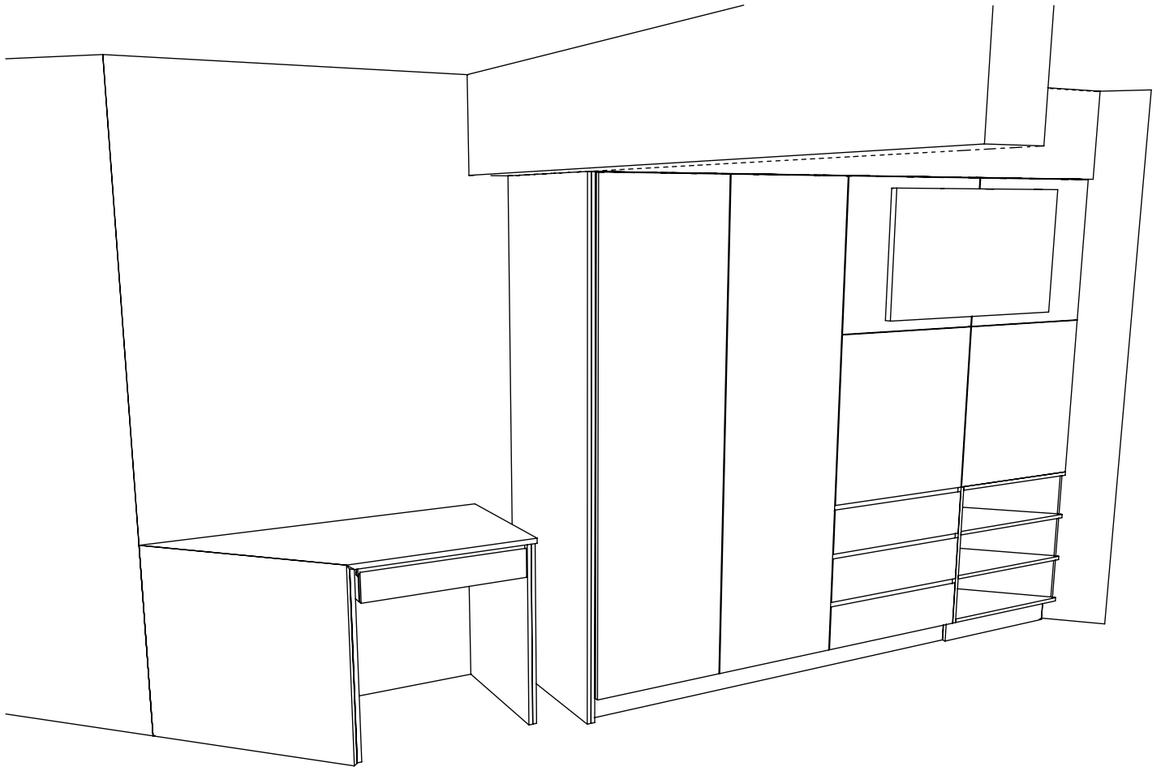


Client Approved Signature : ..... Date : .....

Kitchens By Resident Hero 32 Gateway Drive Phone: 0754471077 mark@residenthero.com.au www.residenthero.com.au	RHK6586 Greystone Constructions	**Scale: NTS**	**Sheet 3 of 3**
	Bed 1 Robe + Study	Do not scale off this drawing.	Drawn By:
			Date: 28/10/26

Lounge TV Unit Plan

1 : 20

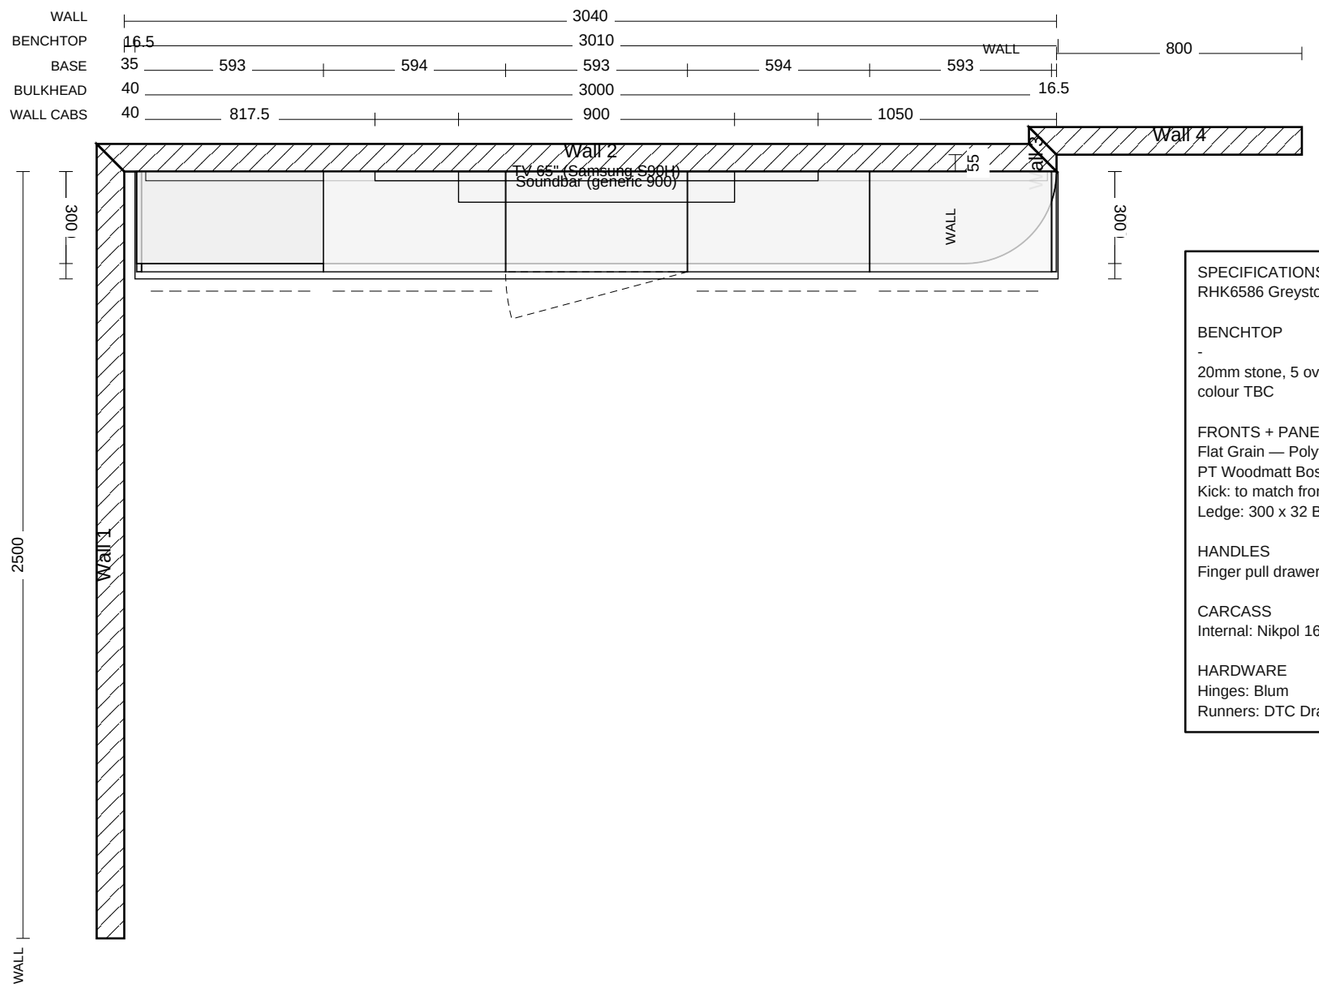

SPECIFICATIONS - Lounge TV Unit
RHK6586 Greystone Constructions

BENCHTOP
-
20mm stone, 5 overhang past fronts + end panels. Product + colour TBC

FRONTS + PANELS
Flat Grain — Polytec - Boston Oak Woodmatt
PT Woodmatt Boston Oak flat
Kick: to match fronts
Ledge: 300 x 32 Boston Oak, R300 RHS

HANDLES
Finger pull drawers, data store flap down. Locks on all fronts

CARCASS
Internal: Nikpol 16mm – Diamond Grey


HARDWARE
Hinges: Blum
Runners: DTC Dragon Pro 300mm

Client Approved Signature : ..... Date : .....

Kitchens By Resident Hero 32 Gateway Drive Phone: 0754471077 mark@residenthero.com.au www.residenthero.com.au	RHK6586 Greystone Constructions	**Scale: 1 : 20**	**Sheet 1 of 3**
	Lounge TV Unit	Do not scale off this drawing.	Drawn By:
			Date: 28/10/26

Lounge TV Unit Elevation Wall 2


1 : 20

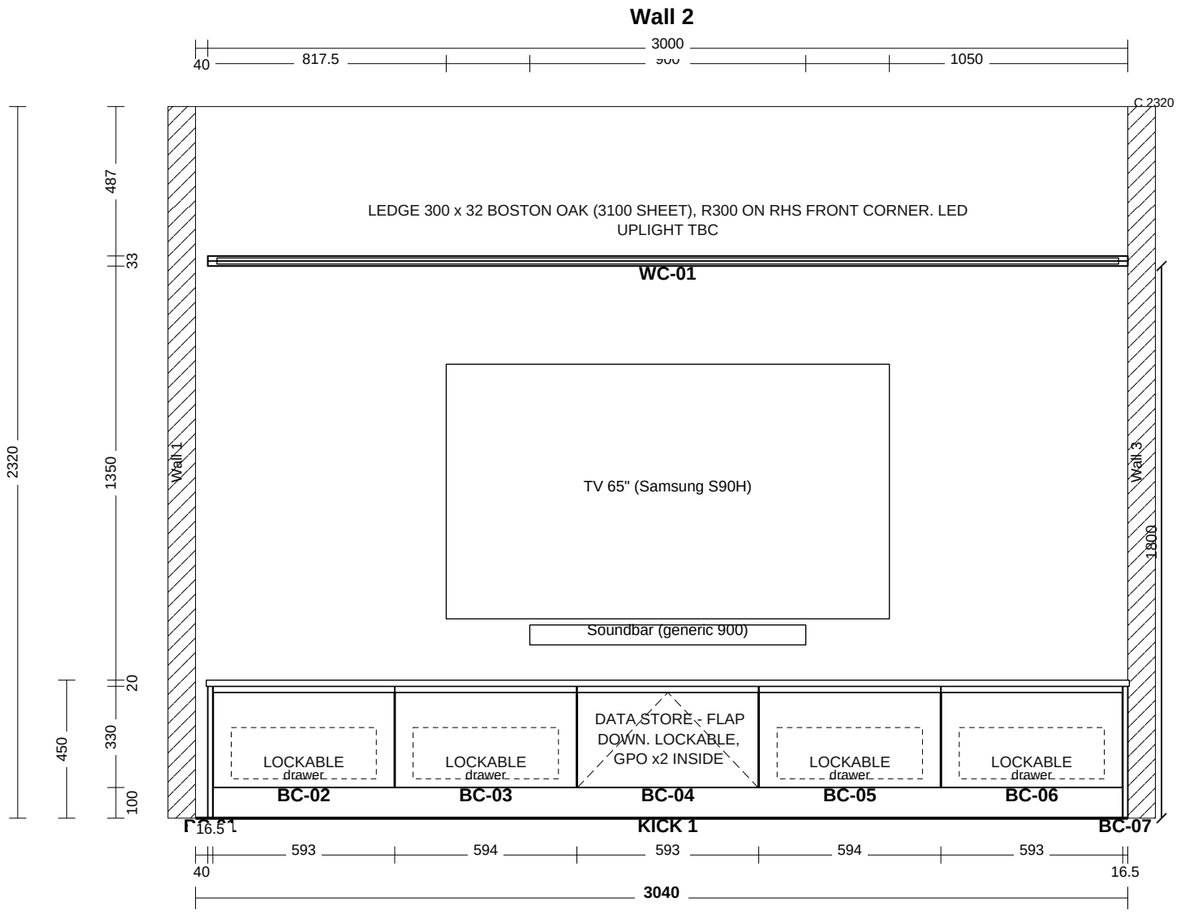


Client Approved Signature : ..... Date : .....

Kitchens By Resident Hero 32 Gateway Drive Phone: 0754471077 mark@residenthero.com.au www.residenthero.com.au	RHK6586 Greystone Constructions	**Scale: 1 : 20**	**Sheet 2 of 3**
	Lounge TV Unit	Do not scale off this drawing.	Drawn By:
			Date: 28/10/26

Lounge TV Unit 3D NTS

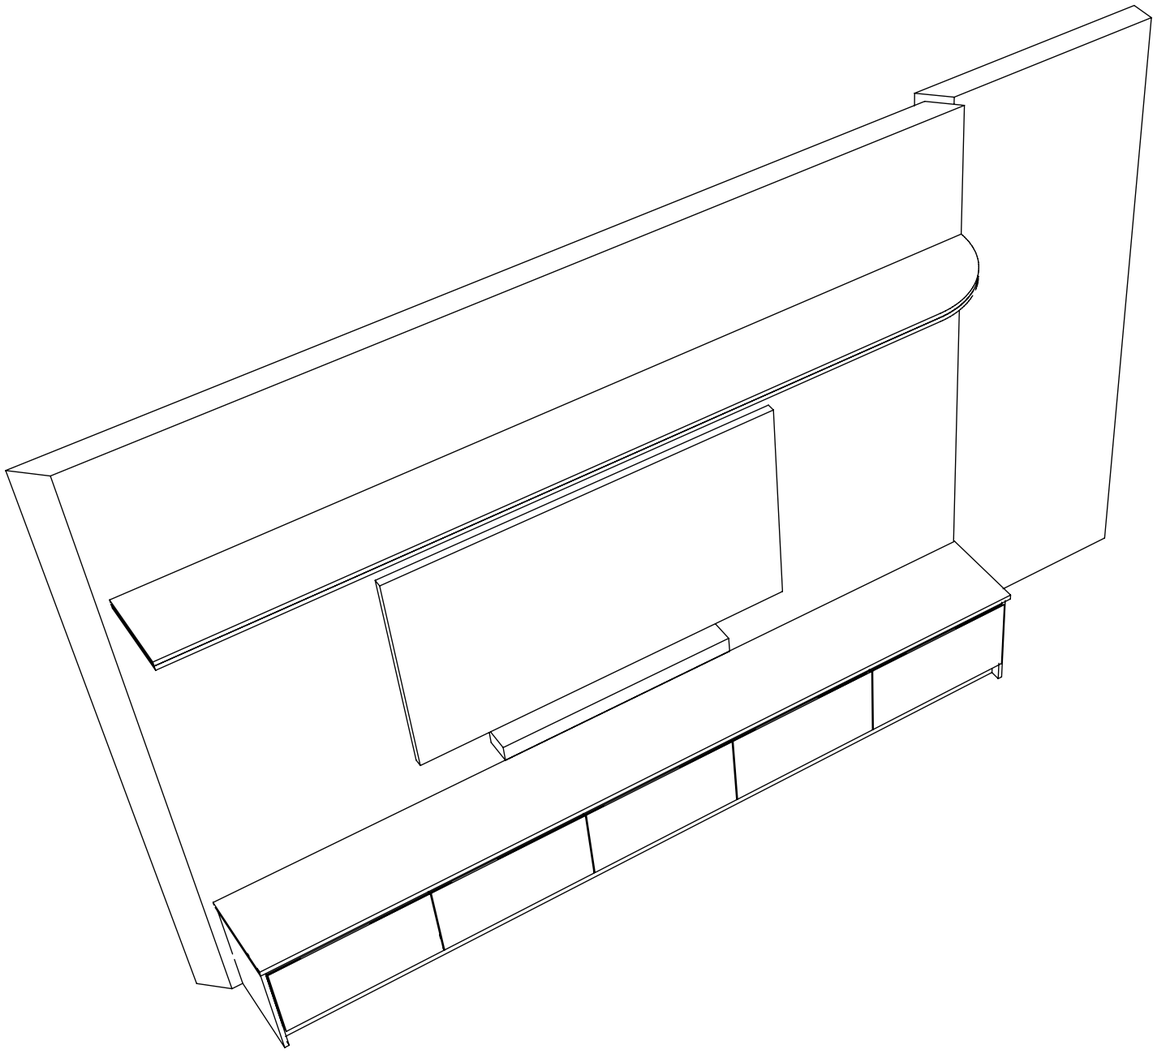


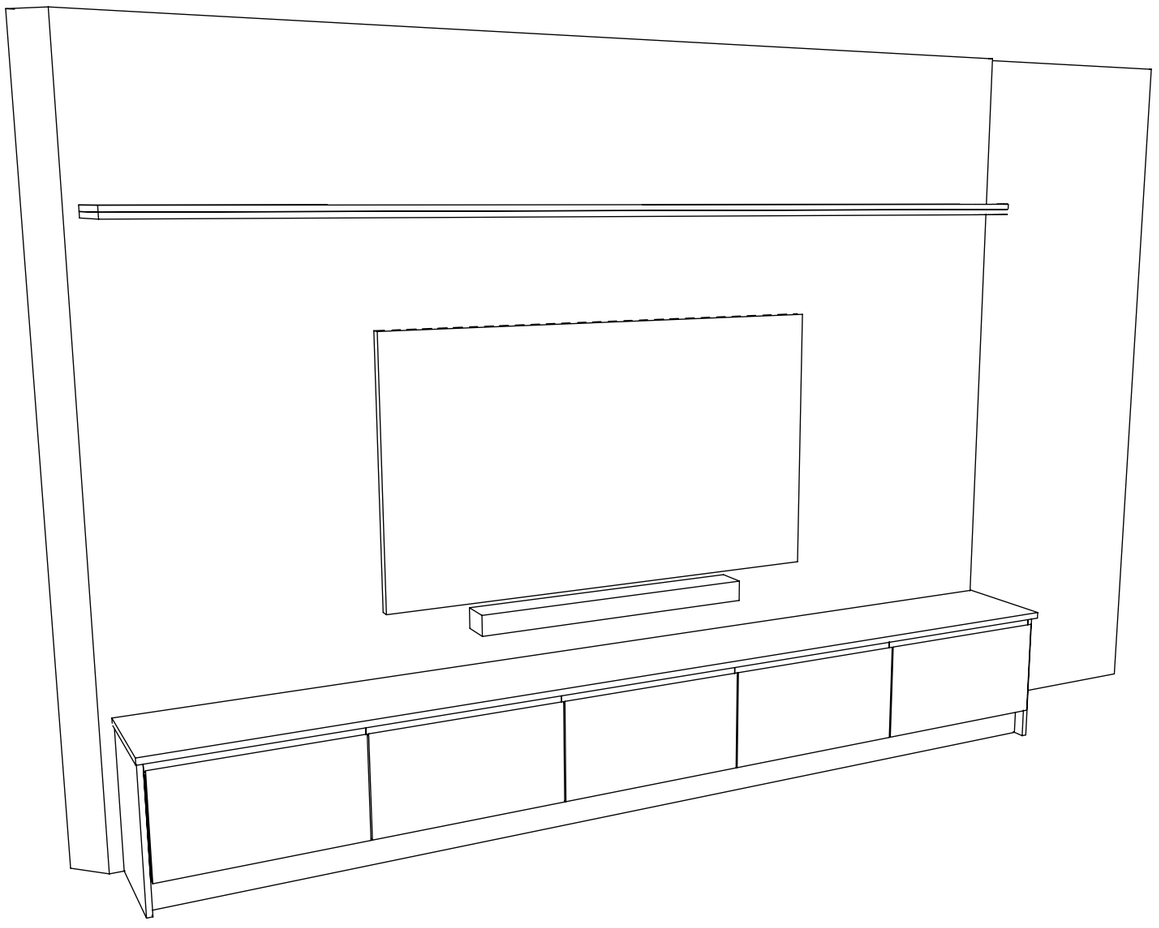

Client Approved Signature : ..... Date : .....

Kitchens By Resident Hero 32 Gateway Drive Phone: 0754471077 mark@residenthero.com.au www.residenthero.com.au	RHK6586 Greystone Constructions	**Scale: NTS**	**Sheet 3 of 3**
	Lounge TV Unit	Do not scale off this drawing.	Drawn By:
			Date: 28/10/26

Bathroom Vanity Plan 1 : 20

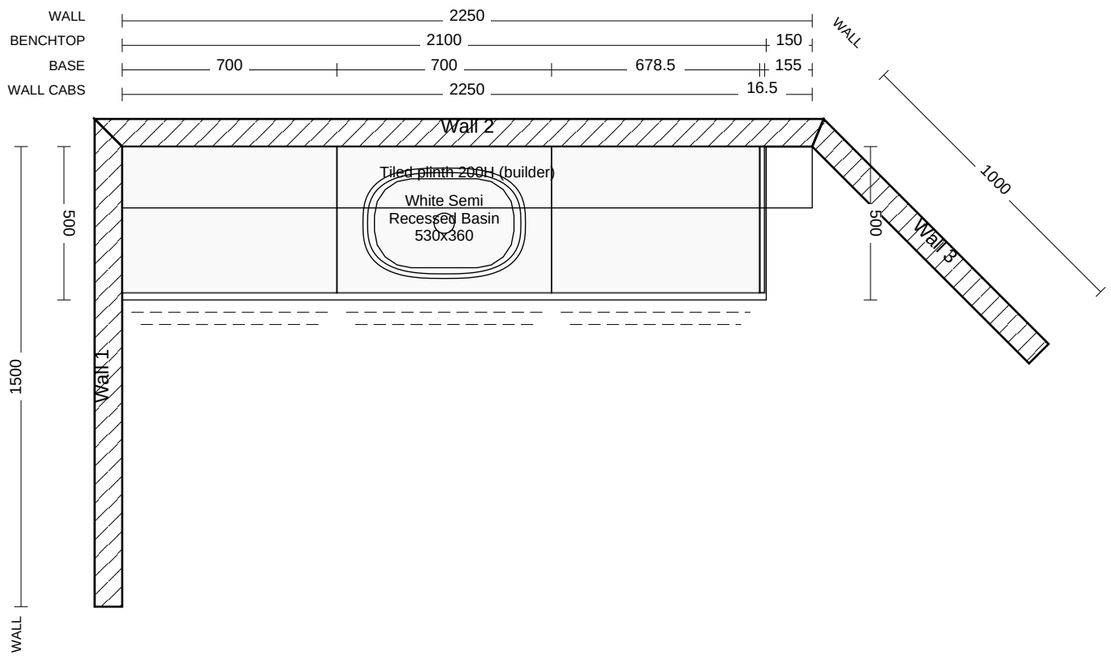

SPECIFICATIONS - Bathroom Vanity
RHK6586 Greystone Constructions

BENCHTOP
-
20mm stone + 150mm mitred apron (front + RH end), 785 top.
Product + colour TBC

FRONTS + PANELS
Flat Grain — Polytec - Boston Oak Woodmatt
PT Woodmatt Boston Oak flat

HANDLES
Finger pull drawers

BASIN
Semi-inset 530 x 360, wall spout + taps

CARCASS
Internal: Nikpol 16mm – Diamond Grey
Sits on 200H tiled plinth by builder


HARDWARE
Runners: DTC Dragon Pro 350mm / 400mm

Client Approved Signature : ..... Date : .....

Kitchens By Resident Hero
32 Gateway Drive
Phone: 0754471077
mark@residenthero.com.au
www.residenthero.com.au

RHK6586 Greystone Constructions	**Scale: 1 : 20**	**Sheet 1 of 3**
Bathroom Vanity	Do not scale off this drawing.	Drawn By:
		Date: 28/10/26


Bathroom Vanity Elevation Wall 2 1 : 20

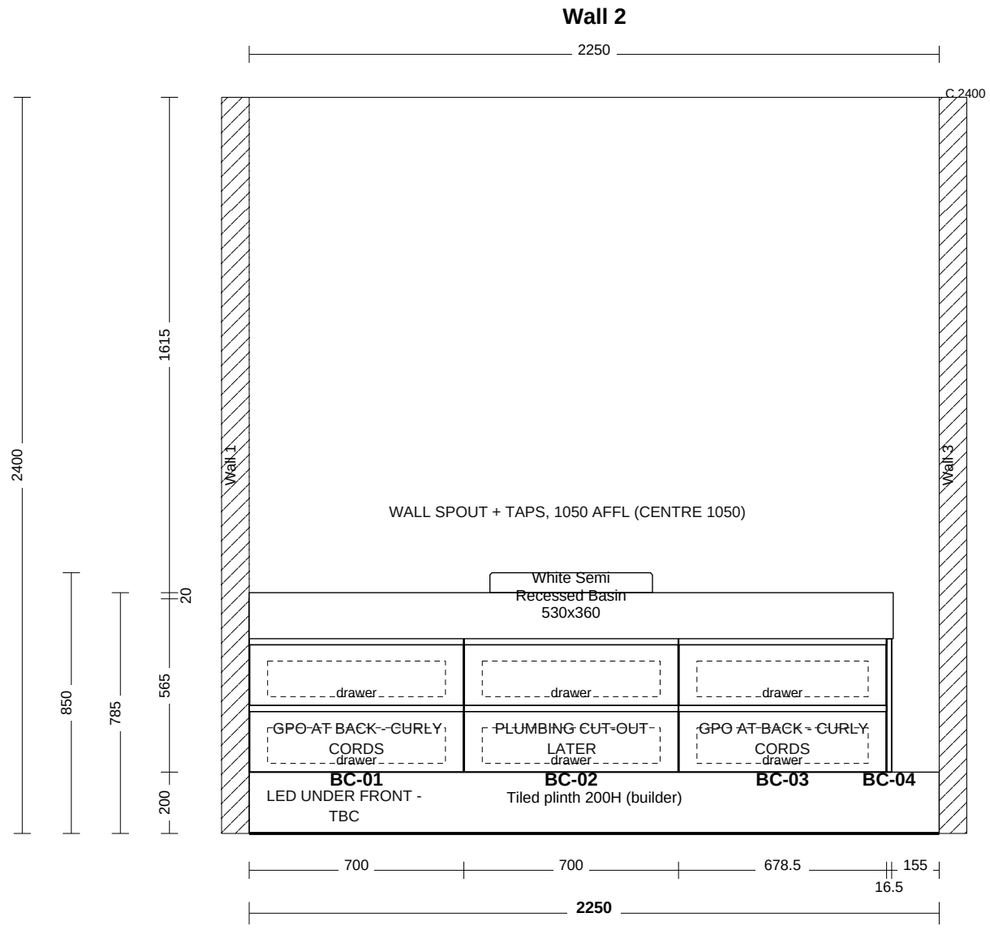


Client Approved Signature : ..... Date : .....

Kitchens By Resident Hero 32 Gateway Drive Phone: 0754471077 mark@residenthero.com.au www.residenthero.com.au	RHK6586 Greystone Constructions	**Scale: 1 : 20**	**Sheet 2 of 3**
	Bathroom Vanity	Do not scale off this drawing.	Drawn By:
			Date: 28/10/26

Bathroom Vanity 3D NTS

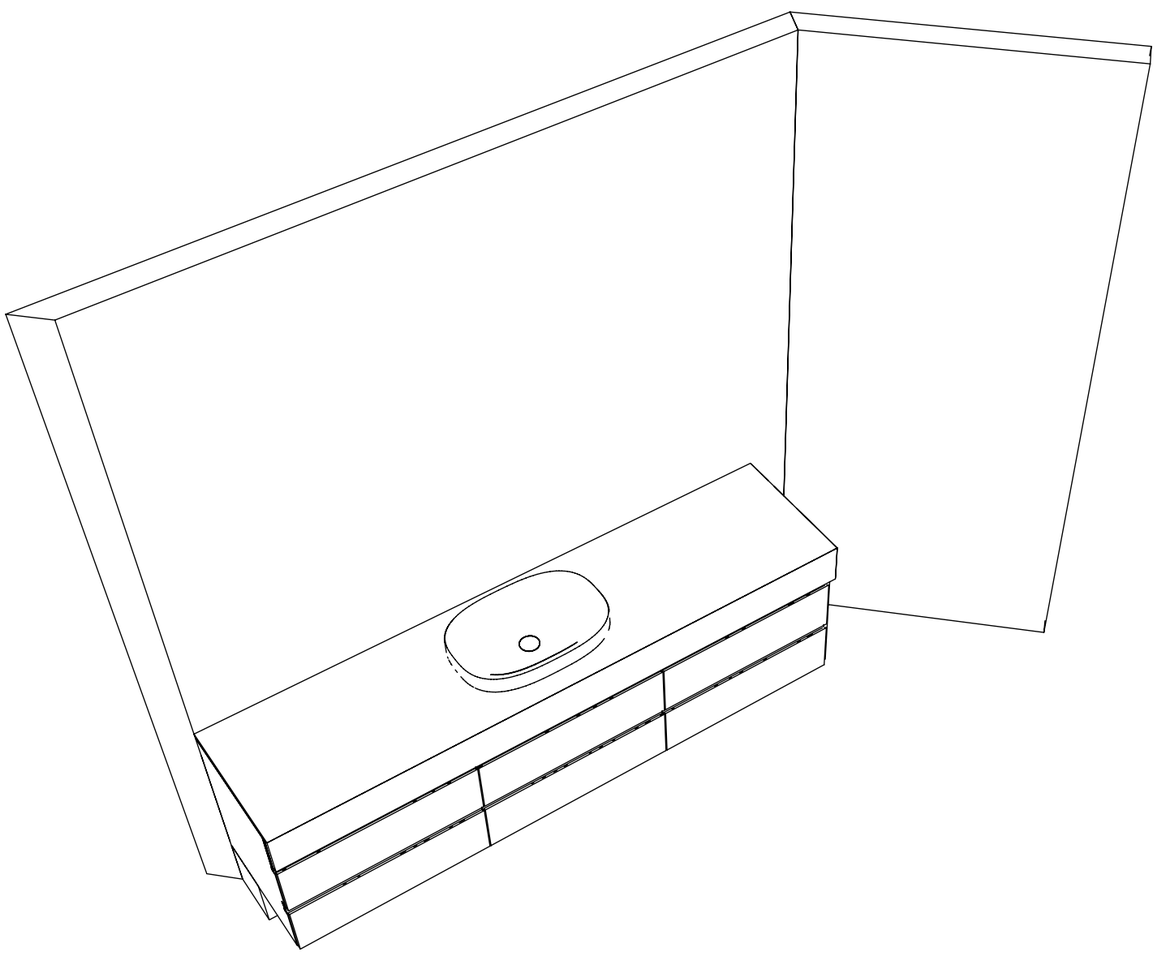


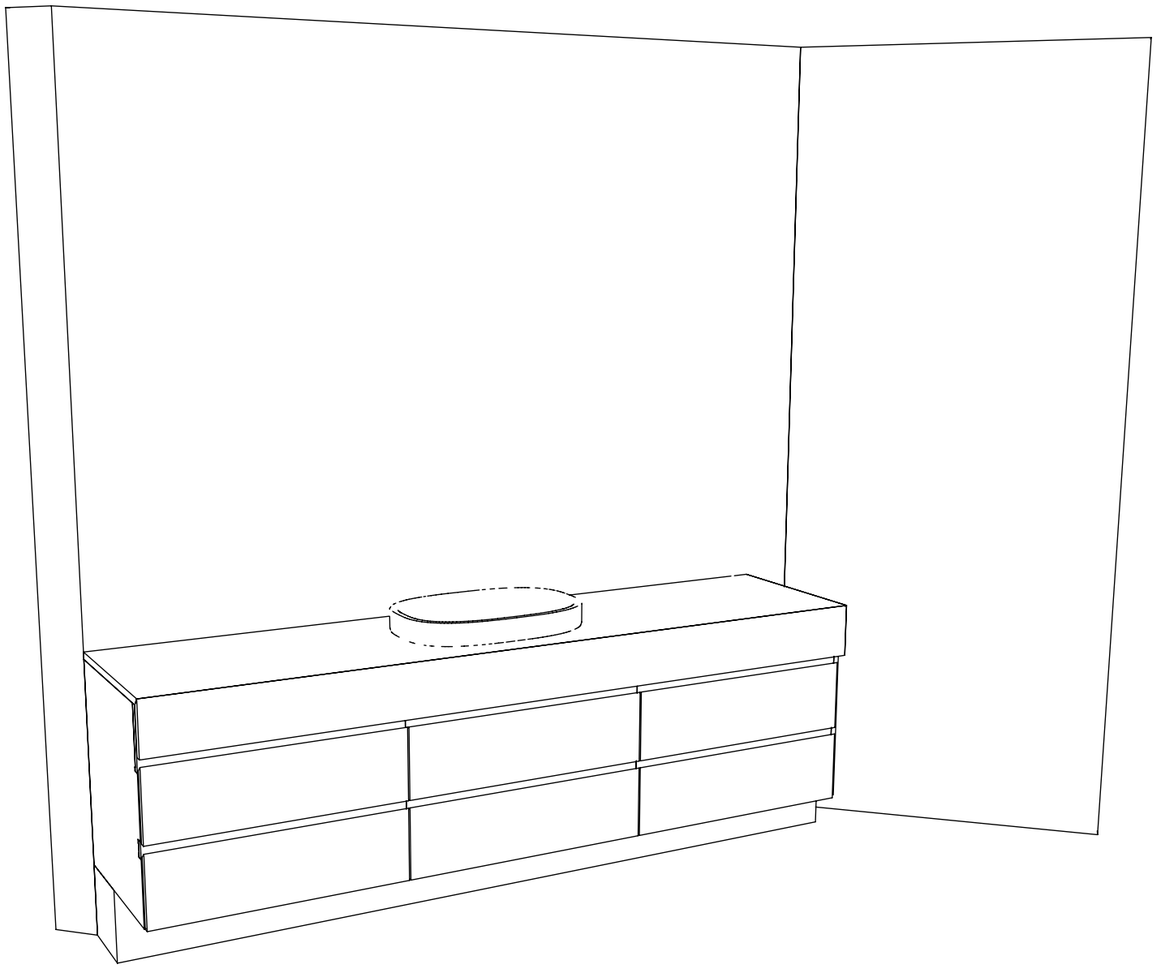

Client Approved Signature : ..... Date : .....

Kitchens By Resident Hero 32 Gateway Drive Phone: 0754471077 mark@residenthero.com.au www.residenthero.com.au	RHK6586 Greystone Constructions	**Scale: NTS**	**Sheet 3 of 3**
	Bathroom Vanity	Do not scale off this drawing.	Drawn By:
			Date: 28/10/26

Kitchenette Plan 1 : 20

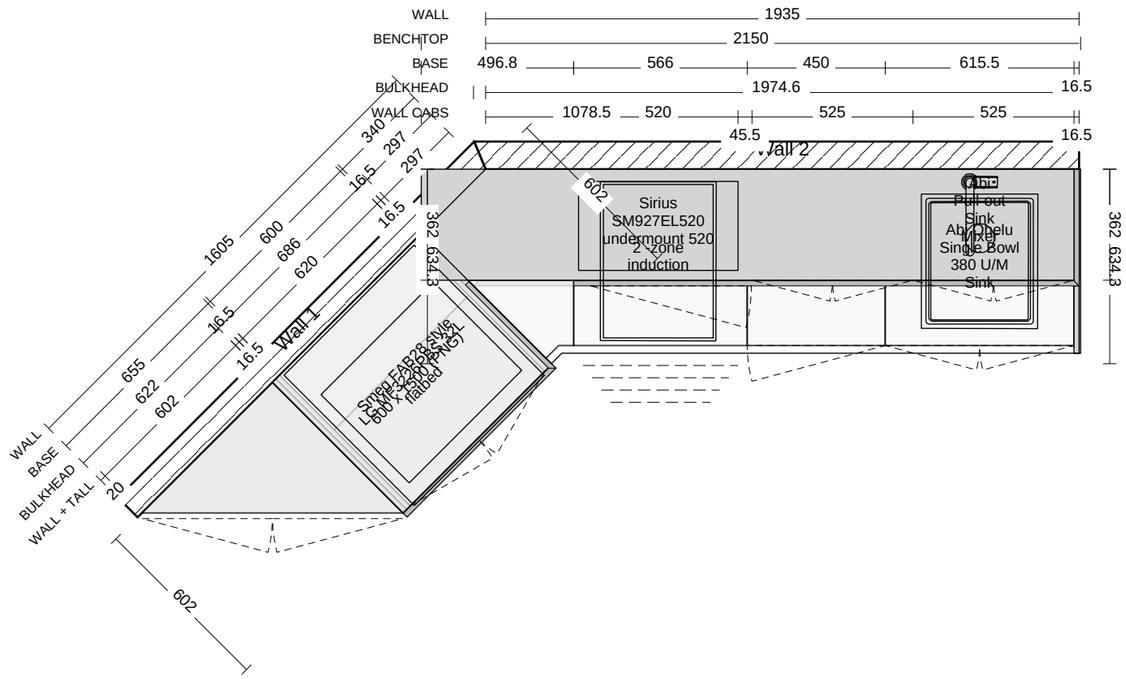

SPECIFICATIONS - Kitchenette
RHK6586 Greystone Constructions

BENCHTOP
-
20mm stone + 60mm mitred apron, 900 top. Product + colour TBC

FRONTS + PANELS
Flat Grain — Polytec - Boston Oak Woodmatt
PT Woodmatt Boston Oak flat. Fridge side panels 32 (2 x 16.5)
Kick: to match fronts. Bulkhead 200 flush with doors

HANDLES
Finger pull drawers, push to open doors

SINK
Abi Ohelu single bowl 380 undermount (under the 20 top), Abi pull-out sink mixer

CARCASS
Internal: Nikpol 16mm – Diamond Grey
External: PT Woodmatt 16mm – Boston Oak Woodmatt (BC-01)


HARDWARE
Hinges: Blum
Runners: DTC Dragon Pro 500mm

APPLIANCES
Miele CS7612FL cooktop, Sirius SM927EL520 rangehood, Miele G5481SCVi integrated DW, LG MF3226PBS microwave, Smeg 600 fridge

Client Approved Signature : ..... Date : .....

Kitchens By Resident Hero 32 Gateway Drive Phone: 0754471077 mark@residenthero.com.au www.residenthero.com.au	RHK6586 Greystone Constructions	**Scale: 1 : 20**	**Sheet 1 of 5**
	Kitchenette	Do not scale off this drawing.	Drawn By:
			Date: 28/10/26


Kitchenette Elevation Wall 1 1 : 20

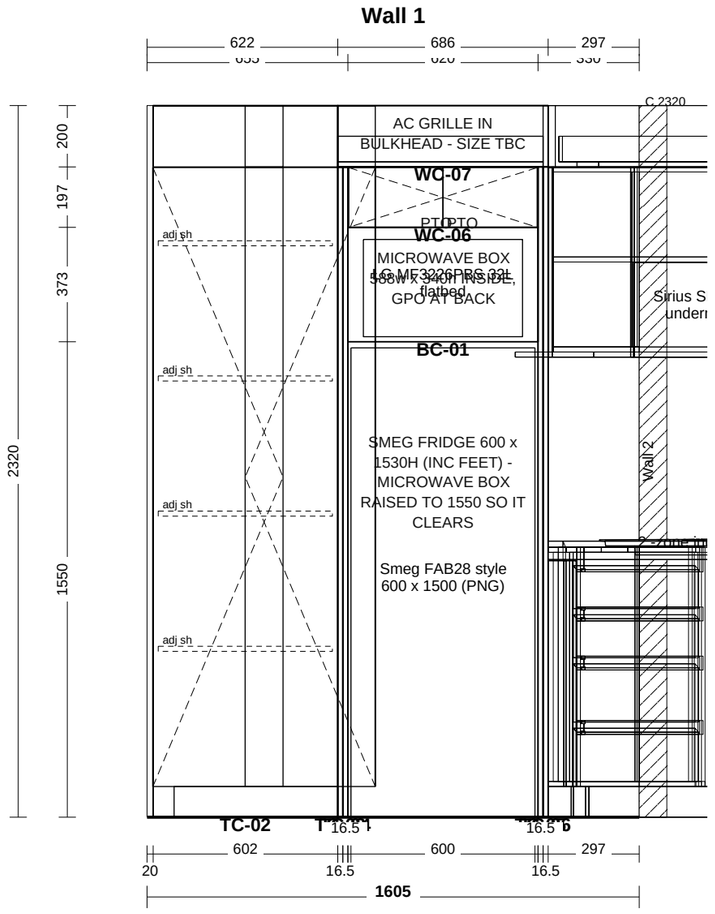

Client Approved Signature : ..... Date : .....

Kitchens By Resident Hero 32 Gateway Drive Phone: 0754471077 mark@residenthero.com.au www.residenthero.com.au	RHK6586 Greystone Constructions	**Scale: 1 : 20**	**Sheet 2 of 5**
	Kitchenette	Do not scale off this drawing.	Drawn By:
			Date: 28/10/26


Kitchenette Elevation Wall 2 1 : 20

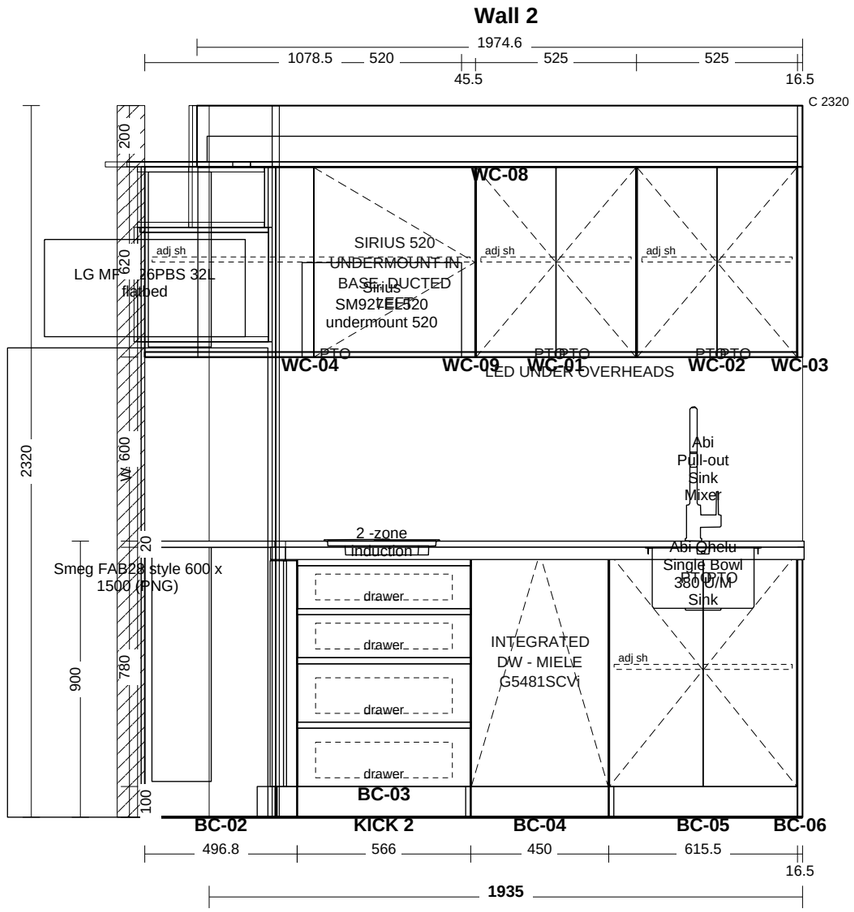


Client Approved Signature : ..... Date : .....

Kitchens By Resident Hero 32 Gateway Drive Phone: 0754471077 mark@residenthero.com.au www.residenthero.com.au	RHK6586 Greystone Constructions	**Scale: 1 : 20**	**Sheet 3 of 5**
	Kitchenette	Do not scale off this drawing.	Drawn By:
			Date: 28/10/26

Kitchenette 3D NTS

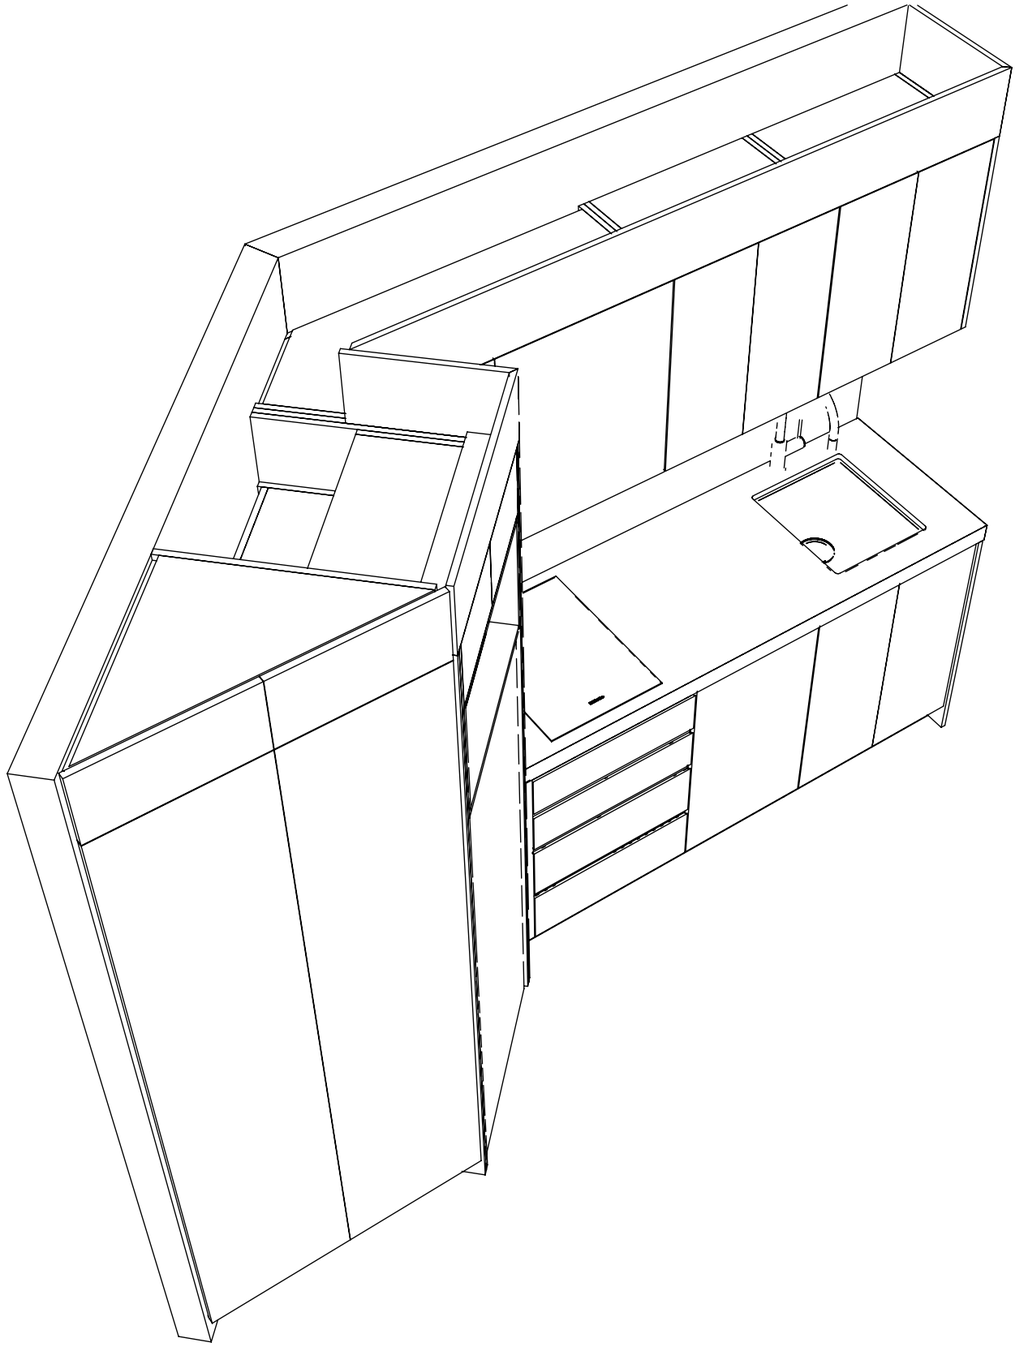


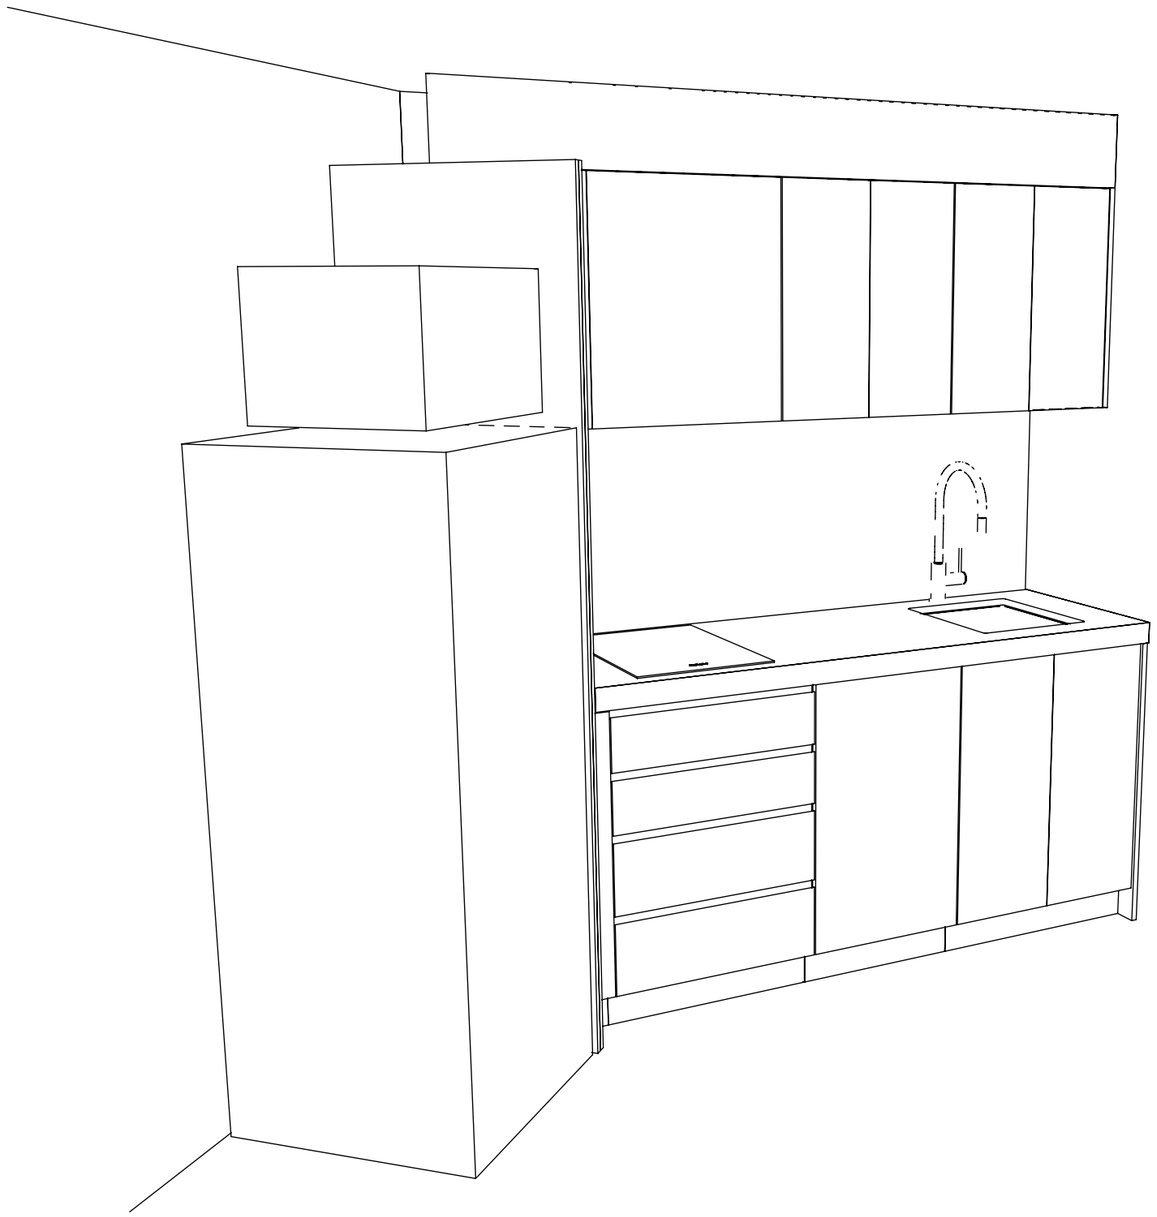

Client Approved Signature : ..... Date : .....

Kitchens By Resident Hero 32 Gateway Drive Phone: 0754471077 mark@residenthero.com.au www.residenthero.com.au	RHK6586 Greystone Constructions	**Scale: NTS**	**Sheet 4 of 5**
	Kitchenette	Do not scale off this drawing.	Drawn By:
			Date: 28/10/26

Kitchenette 3D NTS

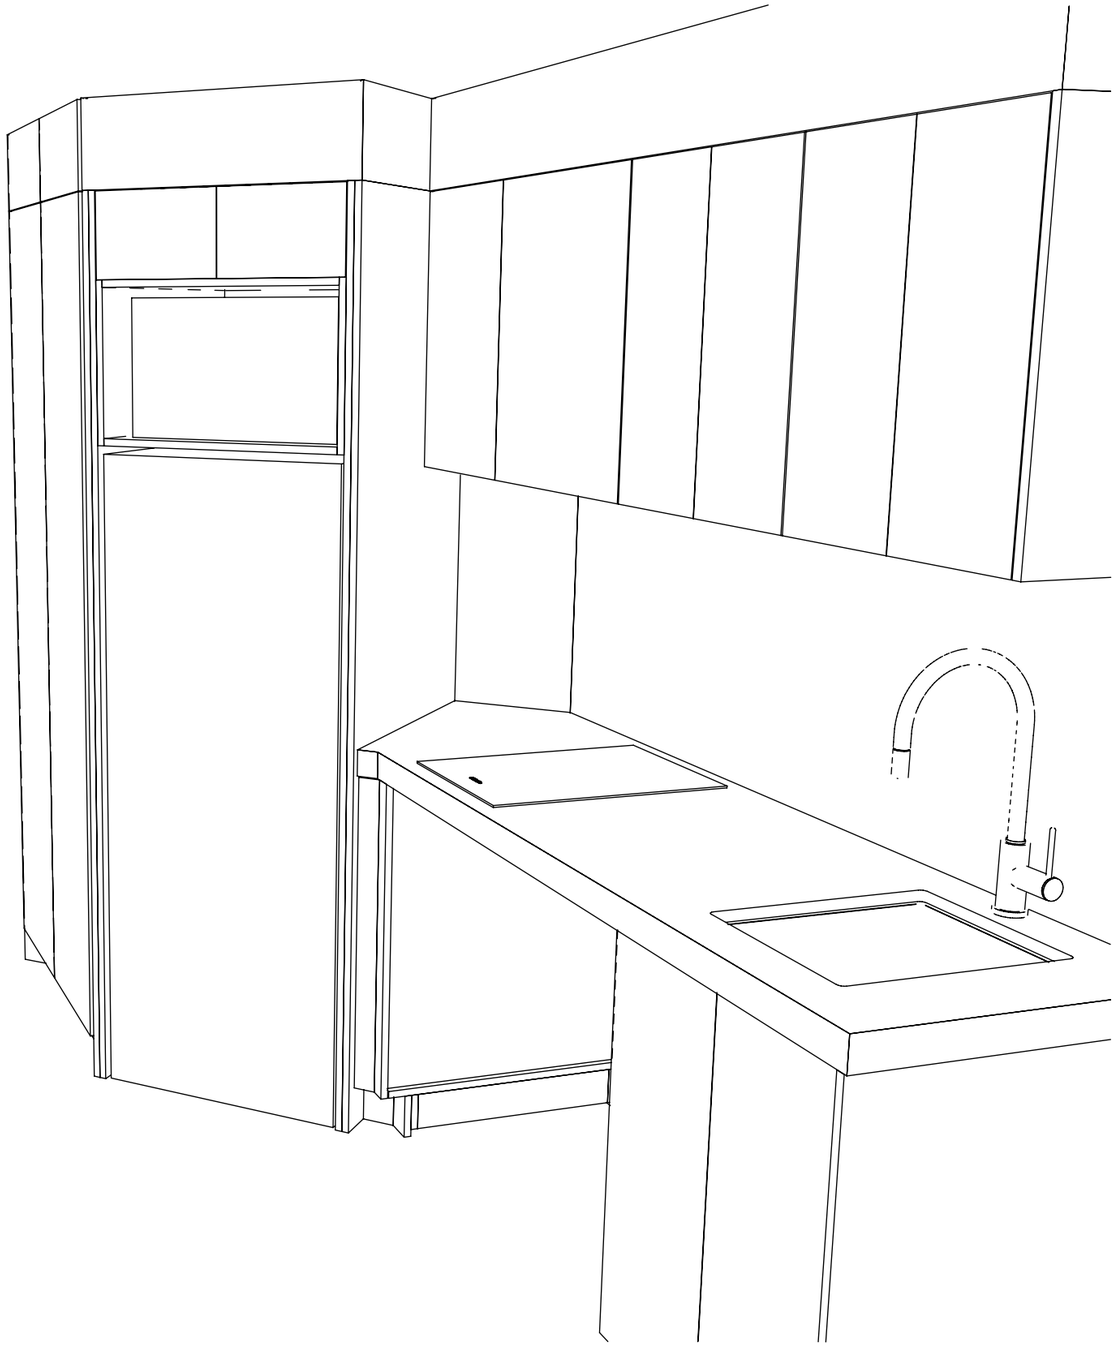

Client Approved Signature : ..... Date : .....

Kitchens By Resident Hero 32 Gateway Drive Phone: 0754471077 mark@residenthero.com.au www.residenthero.com.au	RHK6586 Greystone Constructions	**Scale: NTS**	**Sheet 5 of 5**
	Kitchenette	Do not scale off this drawing.	Drawn By:
			Date: 28/10/26