
Bathroom Vanity Plan

1 : 20

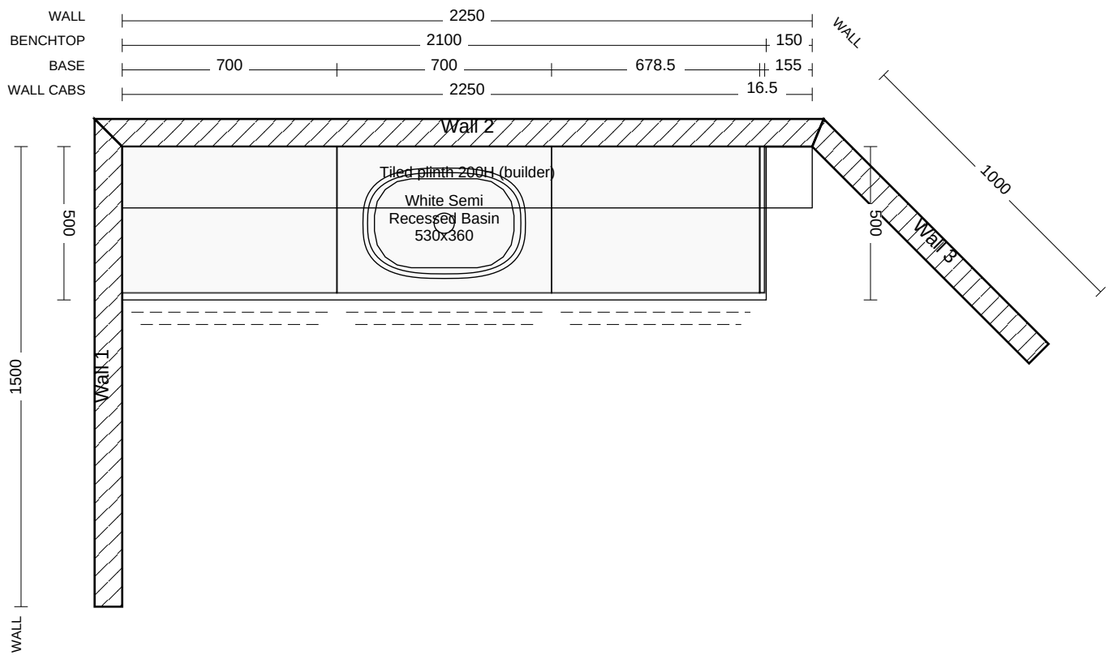

SPECIFICATIONS - Bathroom Vanity
RHK6586 Greystone Constructions

BENCHTOP
-
20mm stone + 150mm mitred apron (front + RH end), 785 top.
Product + colour TBC

FRONTS + PANELS
Flat Grain — Polytec - Boston Oak Woodmatt
PT Woodmatt Boston Oak flat

HANDLES
Finger pull drawers

BASIN
Semi-inset 530 x 360, wall spout + taps

CARCASS
Internal: Nikpol 16mm – Diamond Grey
Sits on 200H tiled plinth by builder


HARDWARE
Runners: DTC Dragon Pro 350mm / 400mm

Client Approved Signature : ..... Date : .....

Kitchens By Resident Hero
32 Gateway Drive
Phone: 0754471077
mark@residenthero.com.au
www.residenthero.com.au

RHK6586 Greystone Constructions	**Scale: 1 : 20**	**Sheet 1 of 3**
Bathroom Vanity	Do not scale off this drawing.	Drawn By:
		Date: 28/10/26


Bathroom Vanity Elevation Wall 2 1 : 20

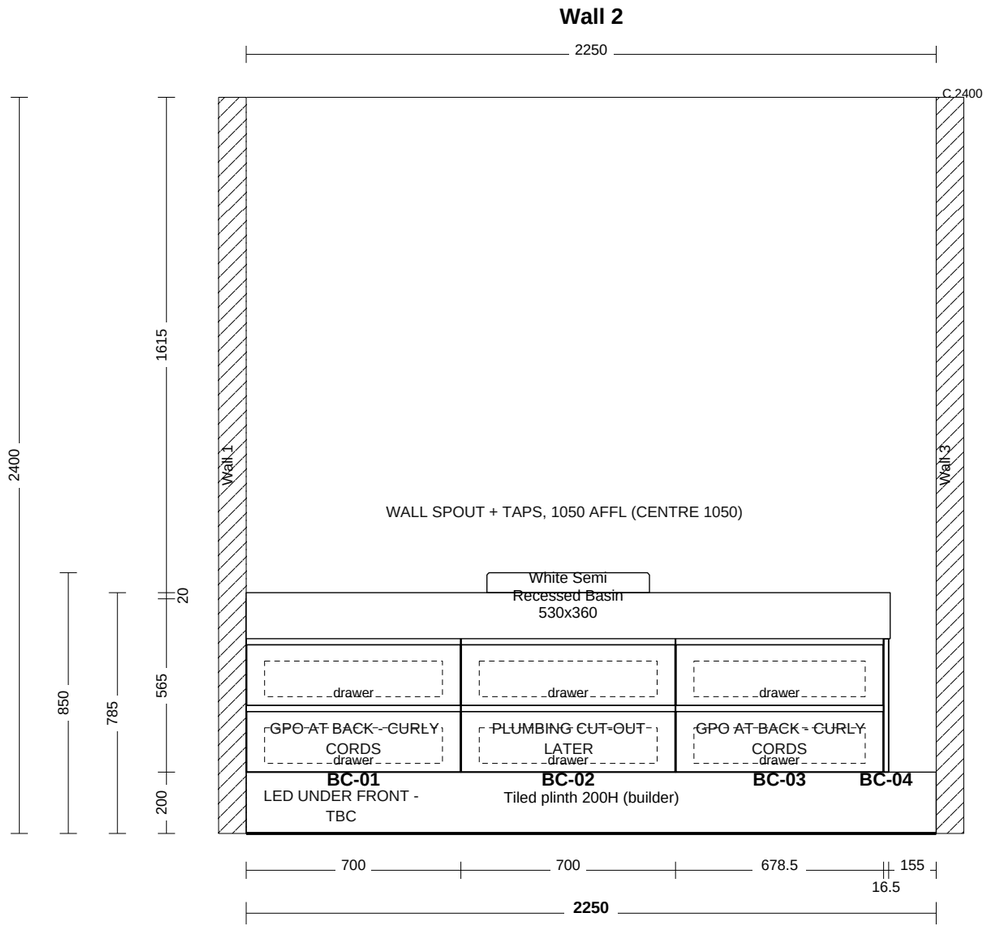


Client Approved Signature : ..... Date : .....

Kitchens By Resident Hero 32 Gateway Drive Phone: 0754471077 mark@residenthero.com.au www.residenthero.com.au	RHK6586 Greystone Constructions	**Scale: 1 : 20**	**Sheet 2 of 3**
	Bathroom Vanity	Do not scale off this drawing.	Drawn By:
			Date: 28/10/26

Bathroom Vanity 3D NTS

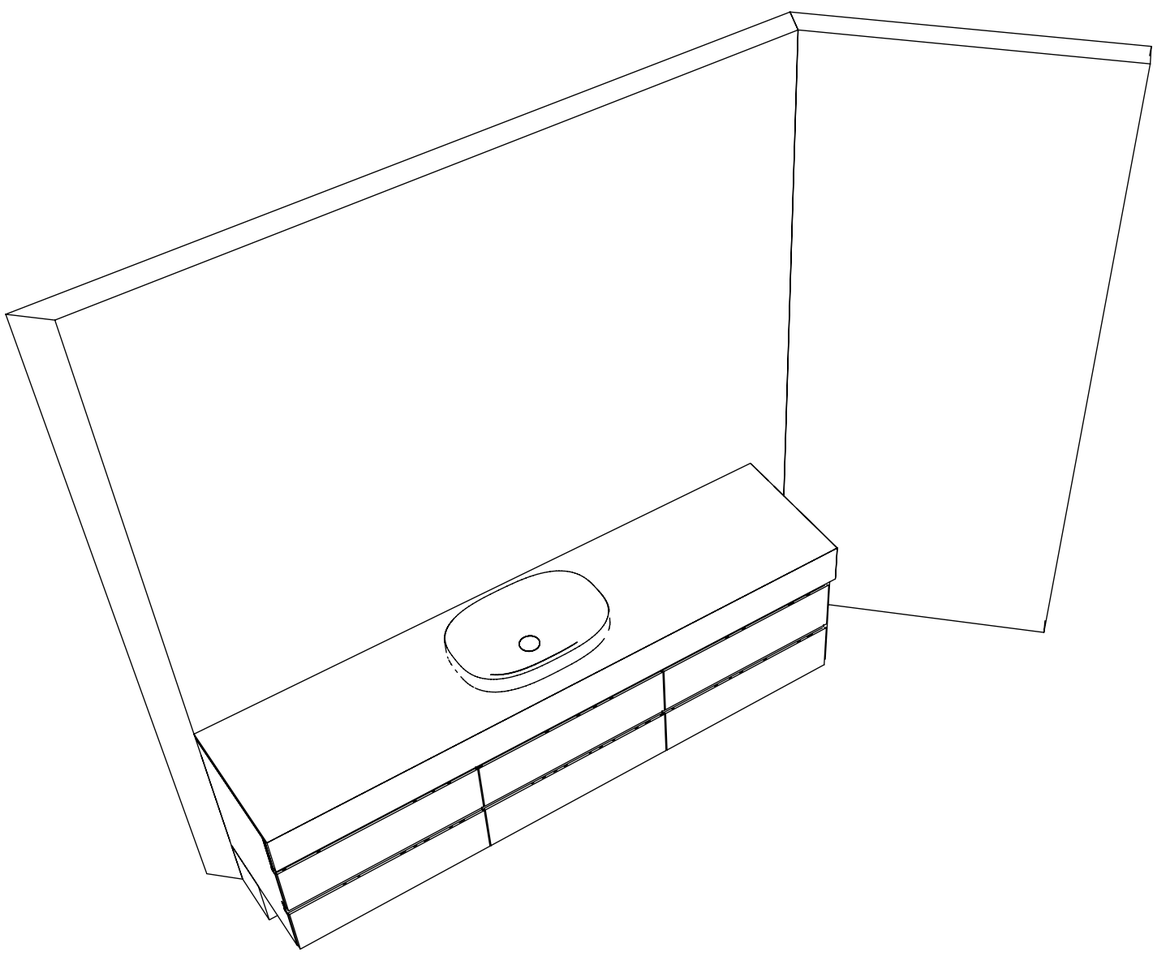

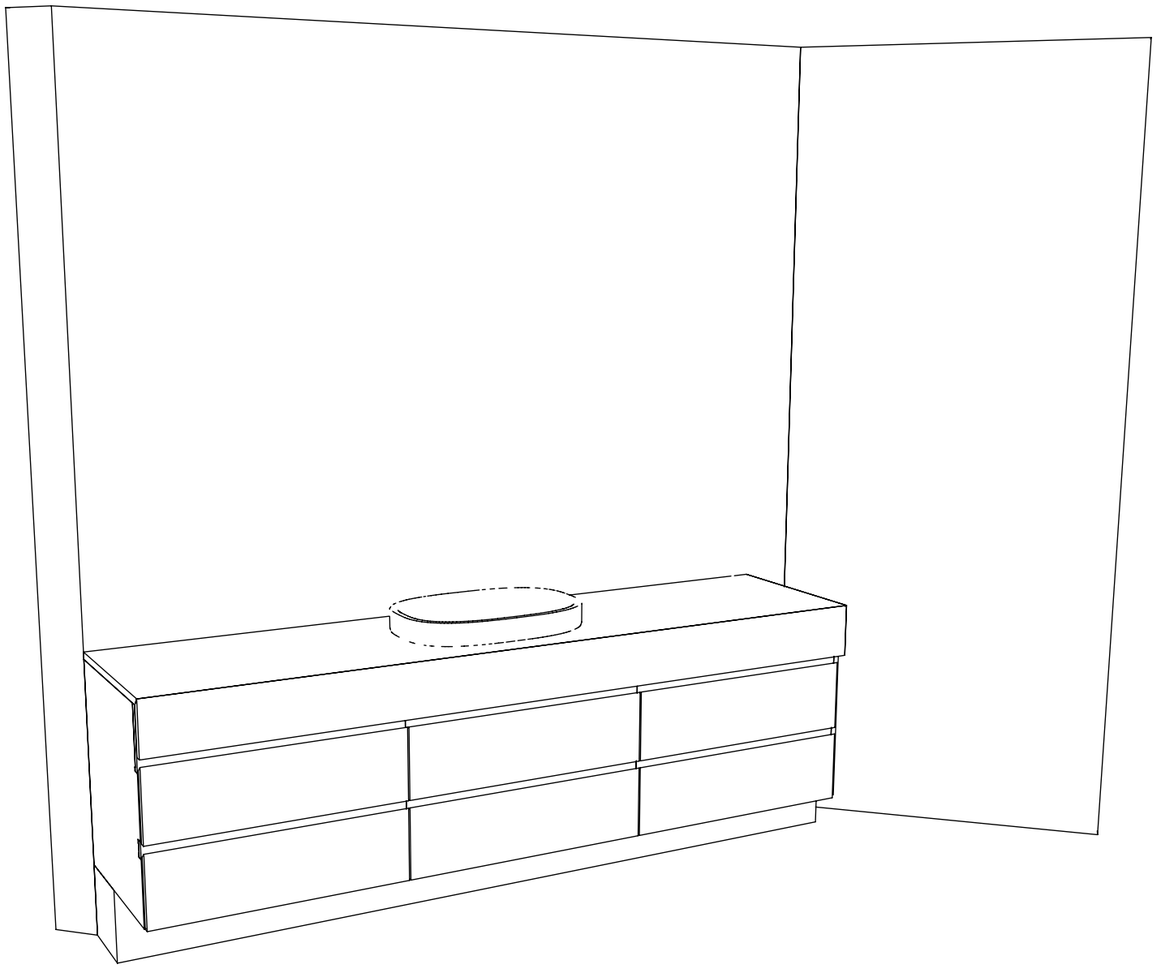

Client Approved Signature : ..... Date : .....

Kitchens By Resident Hero 32 Gateway Drive Phone: 0754471077 mark@residenthero.com.au www.residenthero.com.au	RHK6586 Greystone Constructions	**Scale: NTS**	**Sheet 3 of 3**
	Bathroom Vanity	Do not scale off this drawing.	Drawn By:
			Date: 28/10/26