
Bed 1 Robe + Study Plan

1 : 20

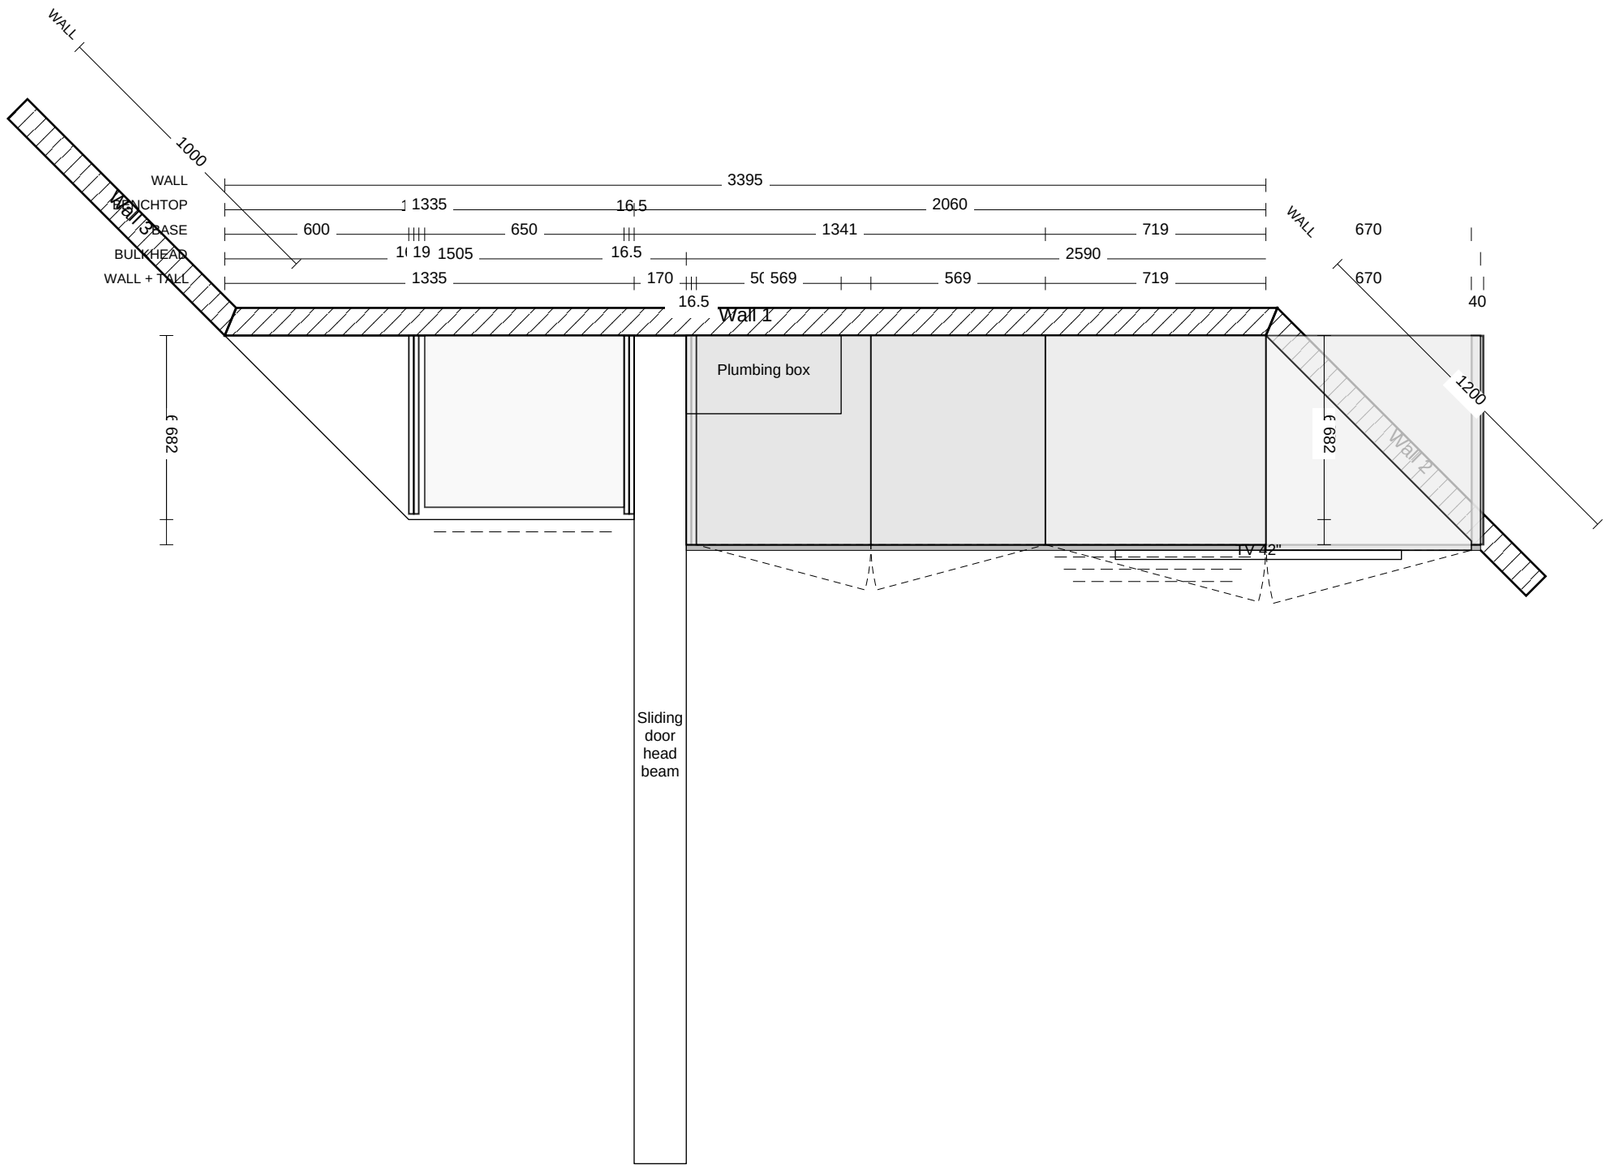

SPECIFICATIONS - Bed 1 Robe + Study
RHK6586 Greystone Constructions

BENCHTOP
-
Study desk 20mm stone, 45 deg waterfall end. Product + colour TBC

FRONTS + PANELS
Flat Grain — Polytec - Boston Oak Woodmatt
PT Woodmatt Boston Oak flat. 32 end panels (2 x 16.5 for now)
Kick: to match fronts

HANDLES
Push to open doors, finger pull drawers

CARCASS
Internal: Nikpol 16mm – Diamond Grey
External: PT Woodmatt 16mm – Boston Oak Woodmatt (BC-07)

HARDWARE
Hinges: Blum
Runners: DTC Dragon Pro 500mm


ACCESSORIES
30x15 oval hanging rails x 2. Safe by others

Client Approved Signature : ..... Date : .....

Kitchens By Resident Hero
32 Gateway Drive
Phone: 0754471077
mark@residenthero.com.au
www.residenthero.com.au

RHK6586 Greystone Constructions	**Scale: 1 : 20**	**Sheet 1 of 3**
Bed 1 Robe + Study	Do not scale off this drawing.	Drawn By:
		Date: 28/10/26


Bed 1 Robe + Study Elevation Wall 1 1 : 20

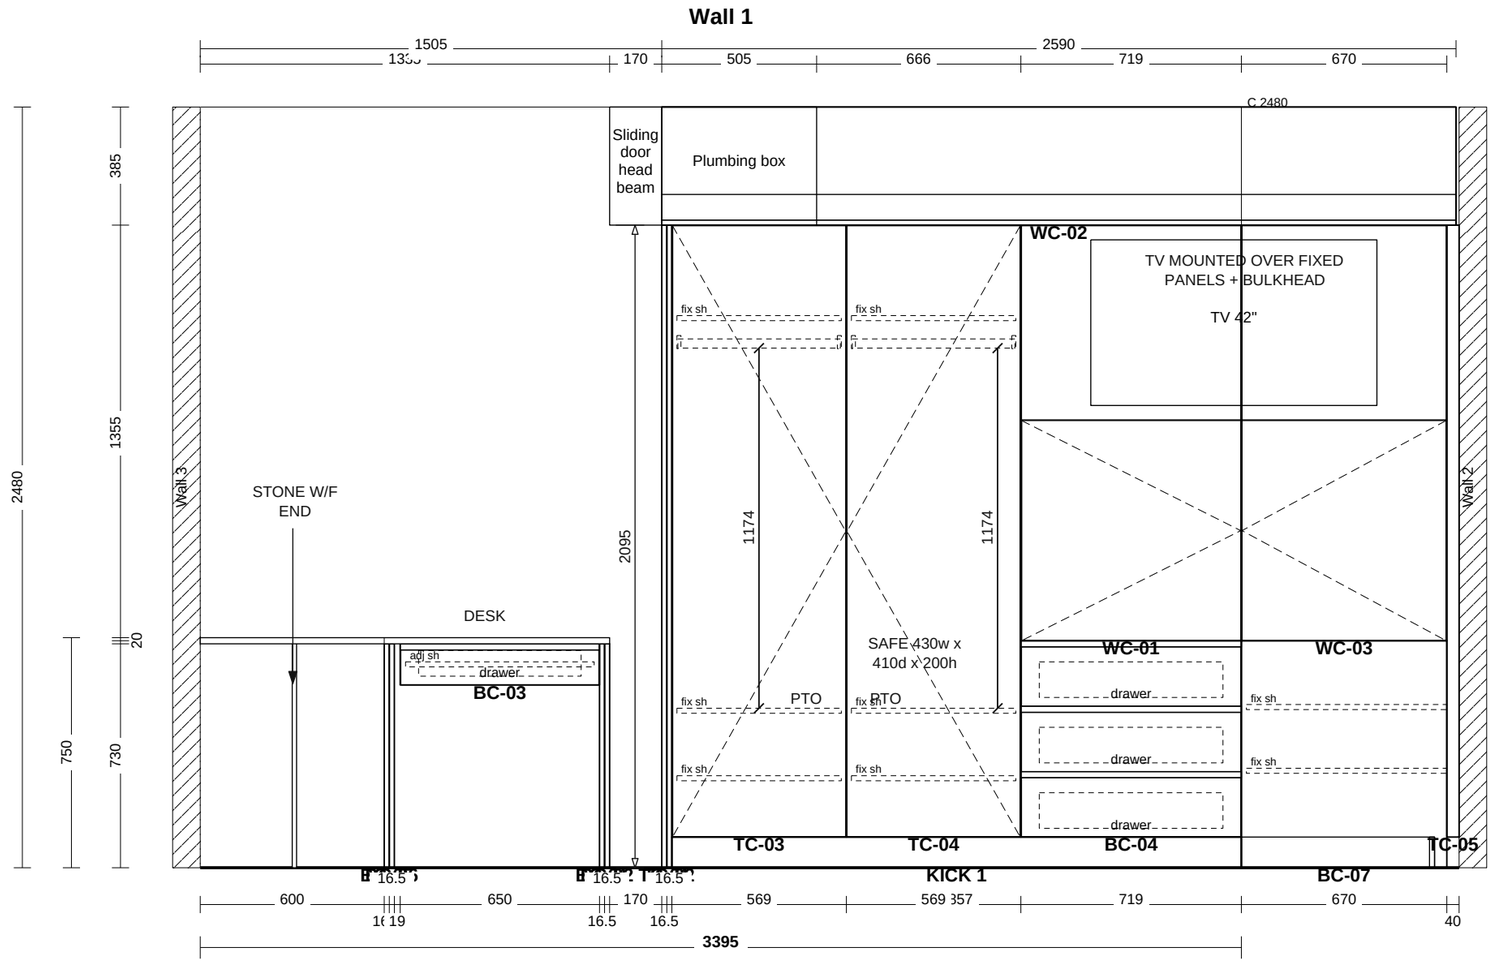


Client Approved Signature : ..... Date : .....

Kitchens By Resident Hero 32 Gateway Drive Phone: 0754471077 mark@residenthero.com.au www.residenthero.com.au	RHK6586 Greystone Constructions	**Scale: 1 : 20**	**Sheet 2 of 3**
	Bed 1 Robe + Study	Do not scale off this drawing.	Drawn By:
			Date: 28/10/26

Bed 1 Robe + Study 3D NTS

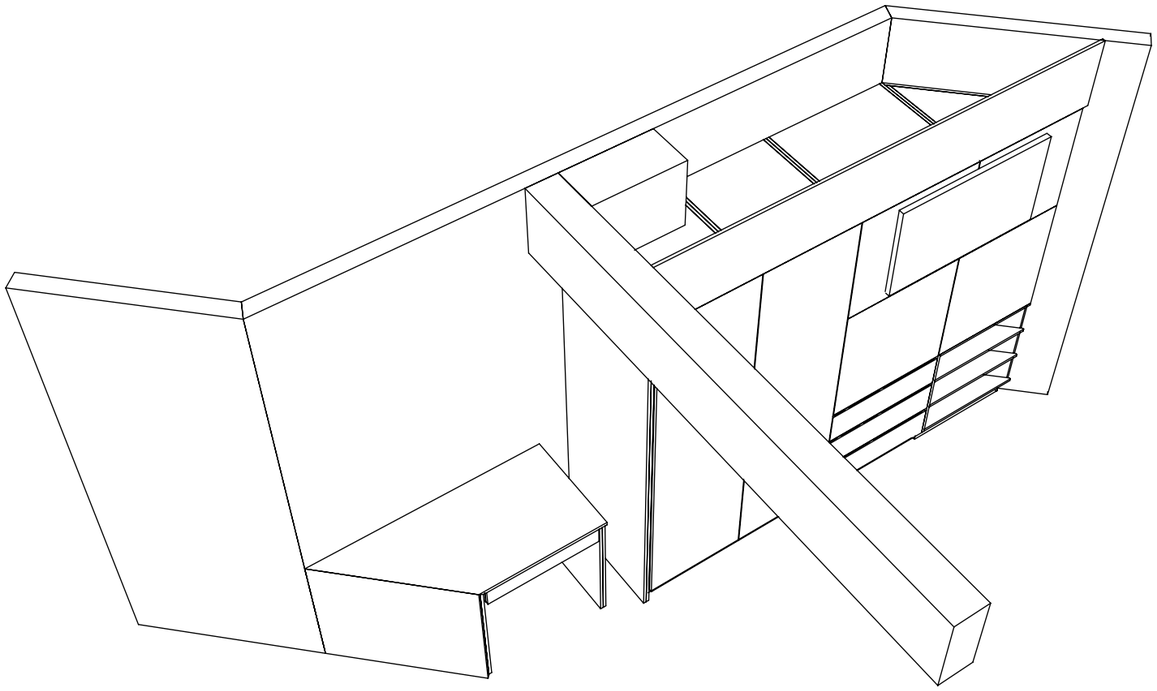

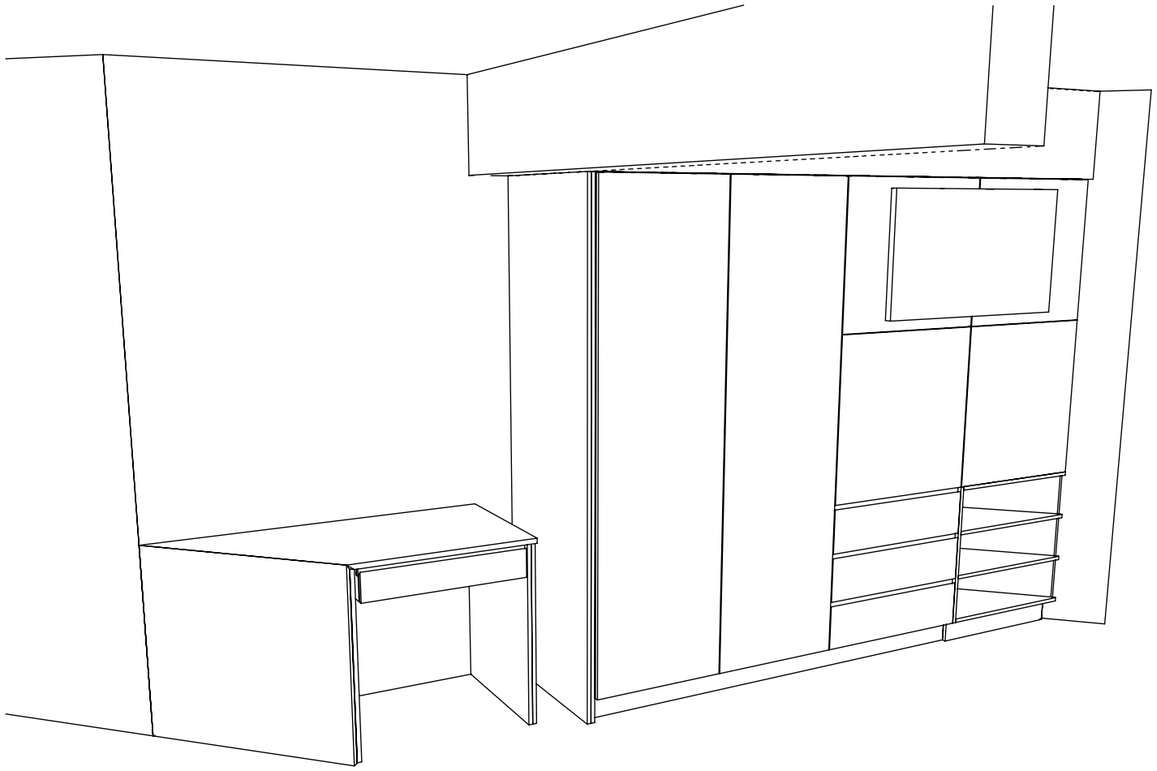

Client Approved Signature : ..... Date : .....

Kitchens By Resident Hero 32 Gateway Drive Phone: 0754471077 mark@residenthero.com.au www.residenthero.com.au	RHK6586 Greystone Constructions	**Scale: NTS**	**Sheet 3 of 3**
	Bed 1 Robe + Study	Do not scale off this drawing.	Drawn By:
			Date: 28/10/26