
Kitchenette Plan 1 : 20

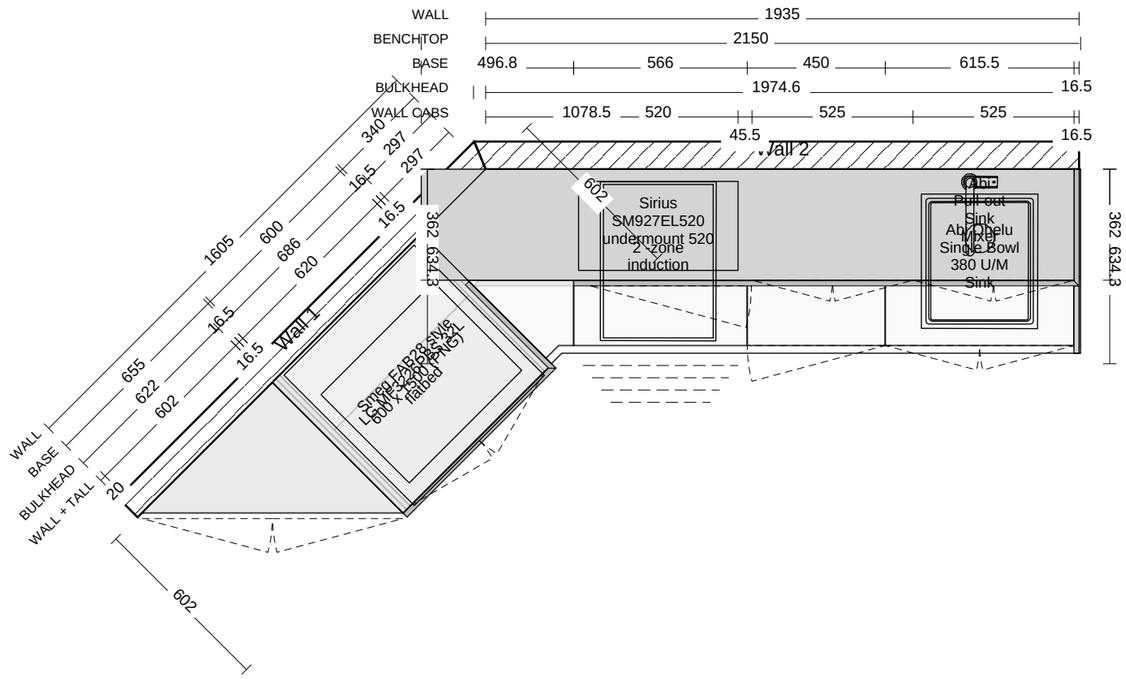

SPECIFICATIONS - Kitchenette
RHK6586 Greystone Constructions

BENCHTOP
-
20mm stone + 60mm mitred apron, 900 top. Product + colour TBC

FRONTS + PANELS
Flat Grain — Polytec - Boston Oak Woodmatt
PT Woodmatt Boston Oak flat. Fridge side panels 32 (2 x 16.5)
Kick: to match fronts. Bulkhead 200 flush with doors

HANDLES
Finger pull drawers, push to open doors

SINK
Abi Ohelu single bowl 380 undermount (under the 20 top), Abi pull-out sink mixer

CARCASS
Internal: Nikpol 16mm – Diamond Grey
External: PT Woodmatt 16mm – Boston Oak Woodmatt (BC-01)


HARDWARE
Hinges: Blum
Runners: DTC Dragon Pro 500mm

APPLIANCES
Miele CS7612FL cooktop, Sirius SM927EL520 rangehood, Miele G5481SCVi integrated DW, LG MF3226PBS microwave, Smeg 600 fridge

Client Approved Signature : ..... Date : .....

Kitchens By Resident Hero 32 Gateway Drive Phone: 0754471077 mark@residenthero.com.au www.residenthero.com.au	RHK6586 Greystone Constructions	**Scale: 1 : 20**	**Sheet 1 of 5**
	Kitchenette	Do not scale off this drawing.	Drawn By:
			Date: 28/10/26


Kitchenette Elevation Wall 1 1 : 20

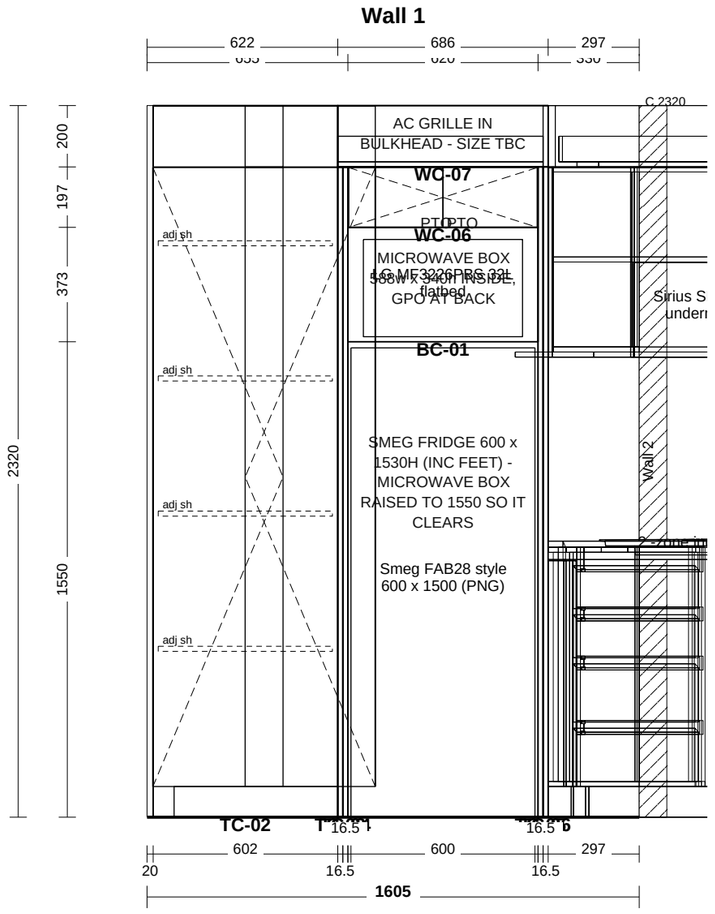

Client Approved Signature : ..... Date : .....

Kitchens By Resident Hero 32 Gateway Drive Phone: 0754471077 mark@residenthero.com.au www.residenthero.com.au	RHK6586 Greystone Constructions	**Scale: 1 : 20**	**Sheet 2 of 5**
	Kitchenette	Do not scale off this drawing.	Drawn By:
			Date: 28/10/26


Kitchenette Elevation Wall 2 1 : 20

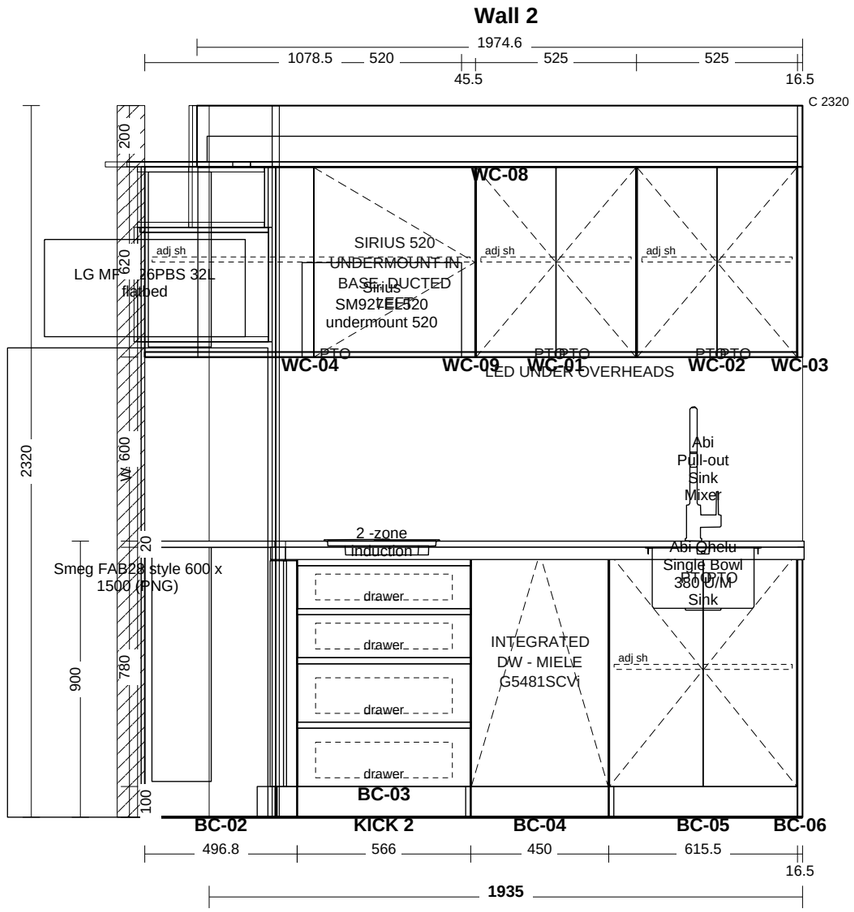


Client Approved Signature : ..... Date : .....

Kitchens By Resident Hero 32 Gateway Drive Phone: 0754471077 mark@residenthero.com.au www.residenthero.com.au	RHK6586 Greystone Constructions	**Scale: 1 : 20**	**Sheet 3 of 5**
	Kitchenette	Do not scale off this drawing.	Drawn By:
			Date: 28/10/26

Kitchenette 3D NTS

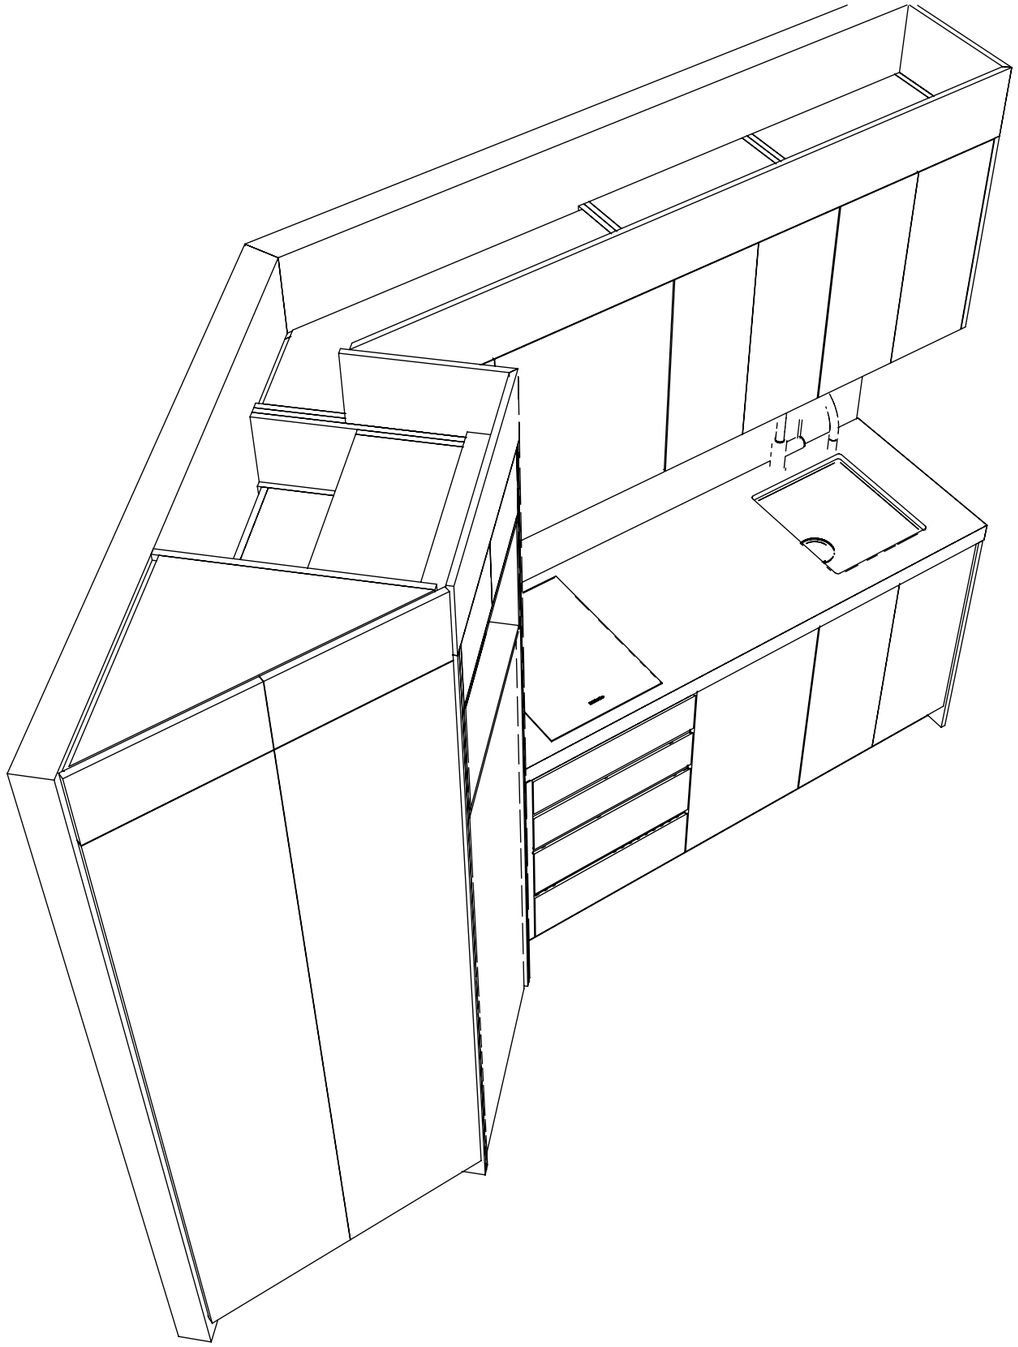


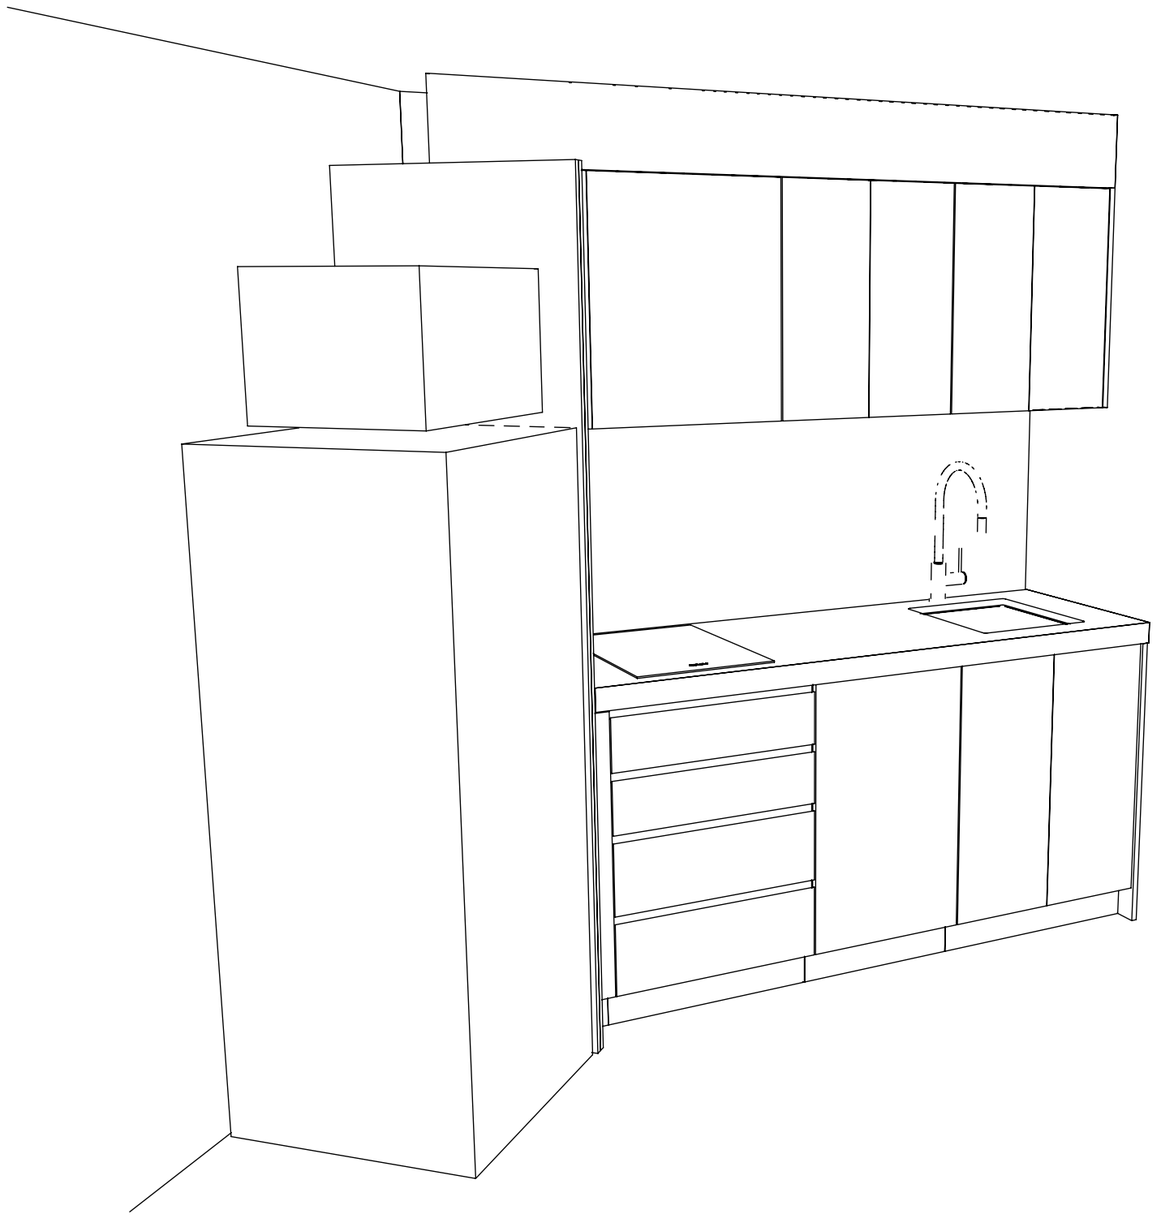

Client Approved Signature : ..... Date : .....

Kitchens By Resident Hero 32 Gateway Drive Phone: 0754471077 mark@residenthero.com.au www.residenthero.com.au	RHK6586 Greystone Constructions	**Scale: NTS**	**Sheet 4 of 5**
	Kitchenette	Do not scale off this drawing.	Drawn By:
			Date: 28/10/26

Kitchenette 3D NTS

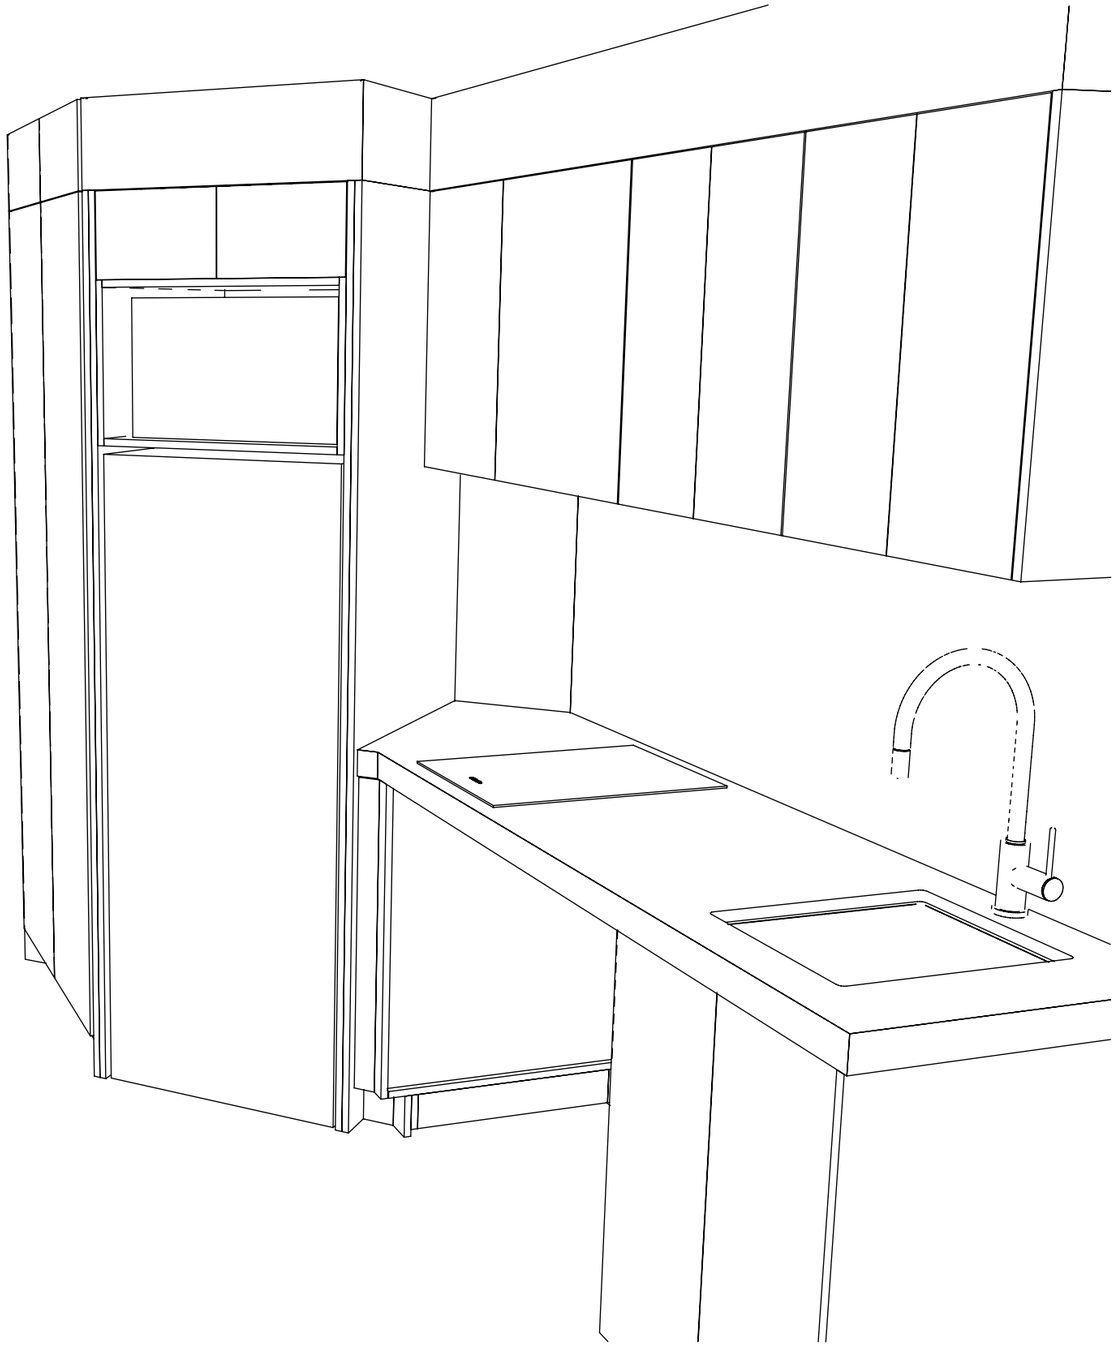

Client Approved Signature : ..... Date : .....

Kitchens By Resident Hero 32 Gateway Drive Phone: 0754471077 mark@residenthero.com.au www.residenthero.com.au	RHK6586 Greystone Constructions	**Scale: NTS**	**Sheet 5 of 5**
	Kitchenette	Do not scale off this drawing.	Drawn By:
			Date: 28/10/26