
Lounge TV Unit Plan

1 : 20

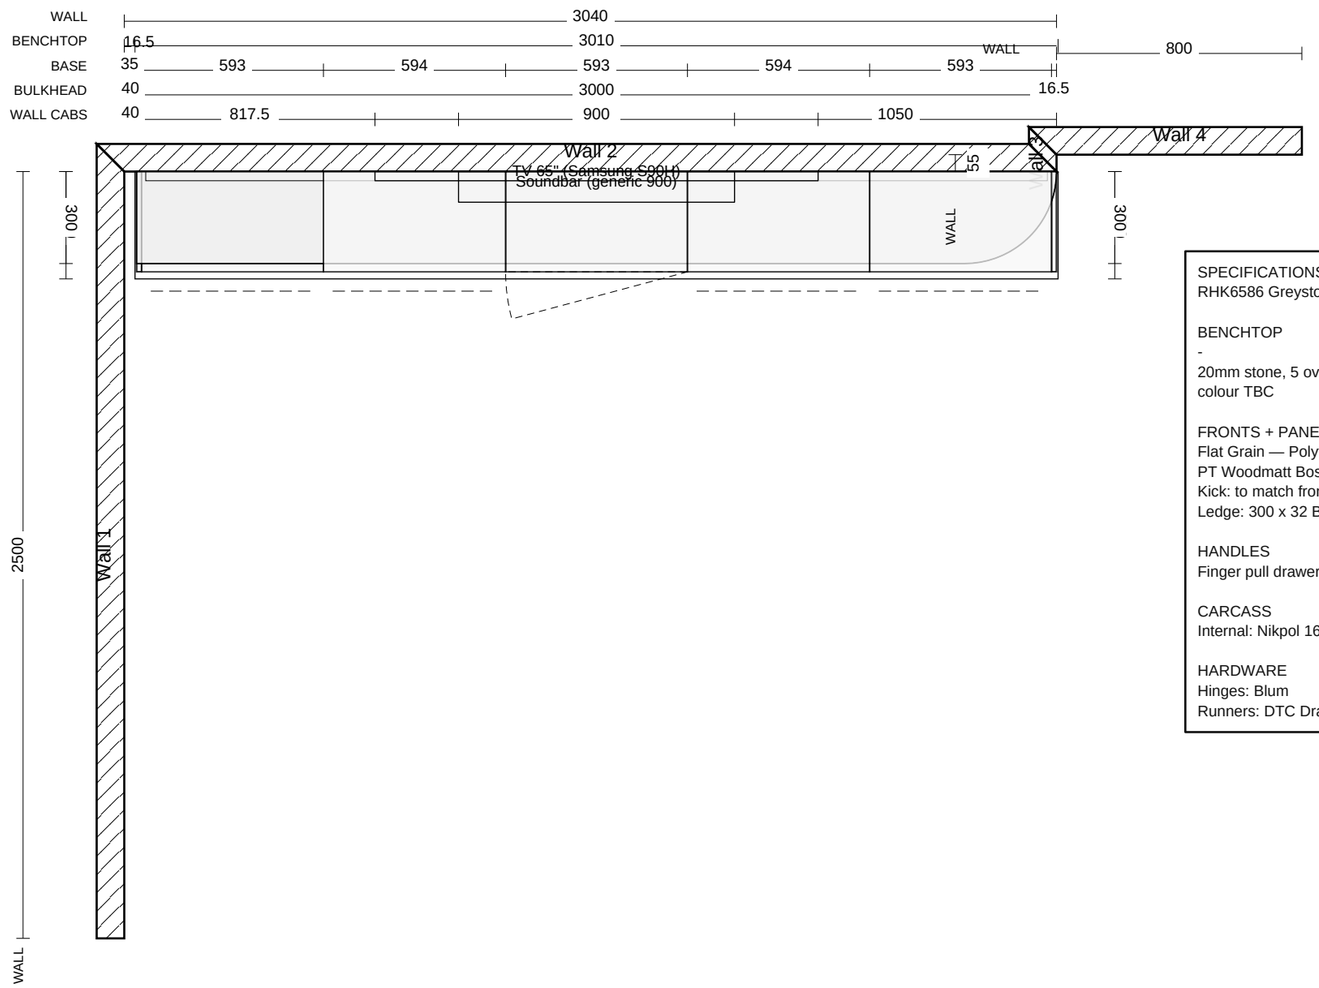

SPECIFICATIONS - Lounge TV Unit
RHK6586 Greystone Constructions

BENCHTOP
-
20mm stone, 5 overhang past fronts + end panels. Product + colour TBC

FRONTS + PANELS
Flat Grain — Polytec - Boston Oak Woodmatt
PT Woodmatt Boston Oak flat
Kick: to match fronts
Ledge: 300 x 32 Boston Oak, R300 RHS

HANDLES
Finger pull drawers, data store flap down. Locks on all fronts

CARCASS
Internal: Nikpol 16mm – Diamond Grey


HARDWARE
Hinges: Blum
Runners: DTC Dragon Pro 300mm

Client Approved Signature : ..... Date : .....

Kitchens By Resident Hero 32 Gateway Drive Phone: 0754471077 mark@residenthero.com.au www.residenthero.com.au	RHK6586 Greystone Constructions	**Scale: 1 : 20**	**Sheet 1 of 3**
	Lounge TV Unit	Do not scale off this drawing.	Drawn By:
			Date: 28/10/26

Lounge TV Unit Elevation Wall 2


1 : 20

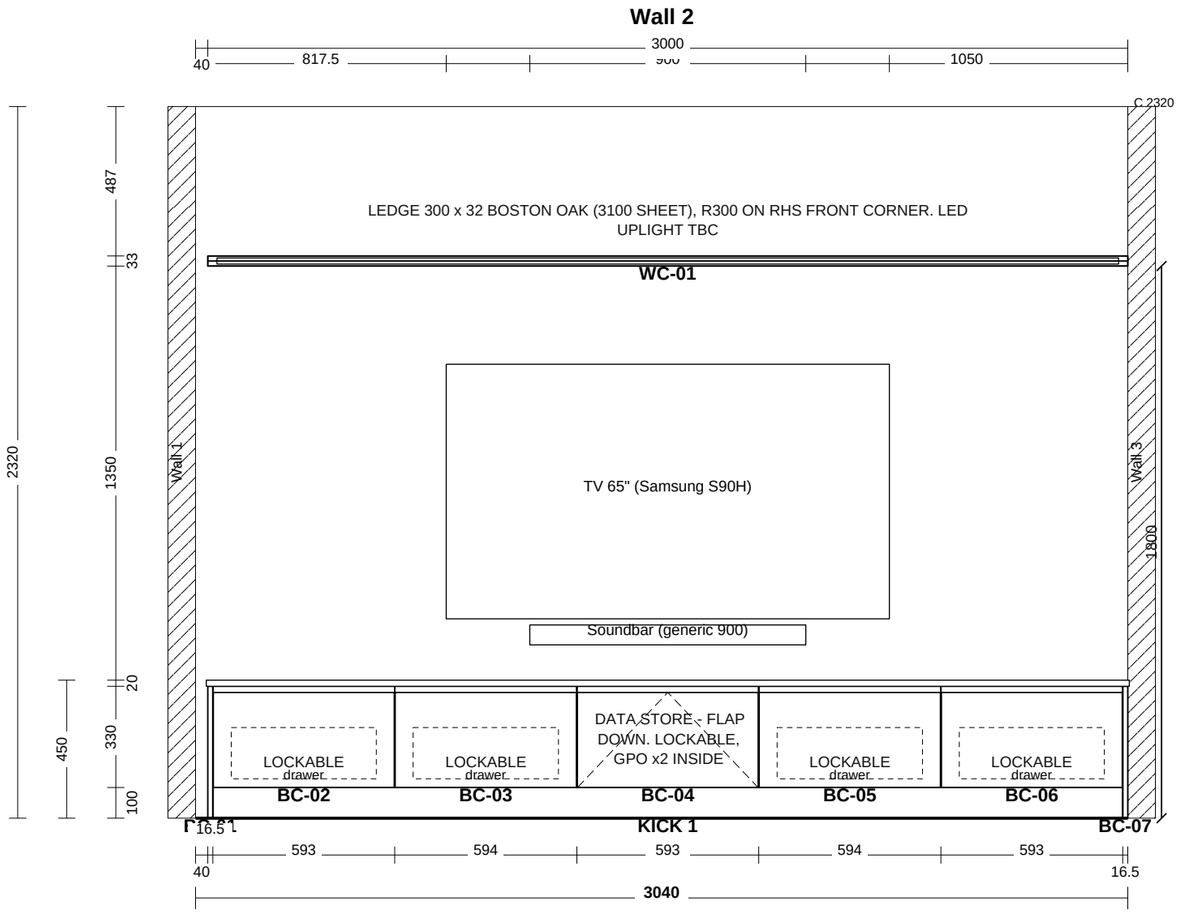


Client Approved Signature : ..... Date : .....

Kitchens By Resident Hero 32 Gateway Drive Phone: 0754471077 mark@residenthero.com.au www.residenthero.com.au	RHK6586 Greystone Constructions	**Scale: 1 : 20**	**Sheet 2 of 3**
	Lounge TV Unit	Do not scale off this drawing.	Drawn By:
			Date: 28/10/26

Lounge TV Unit 3D NTS

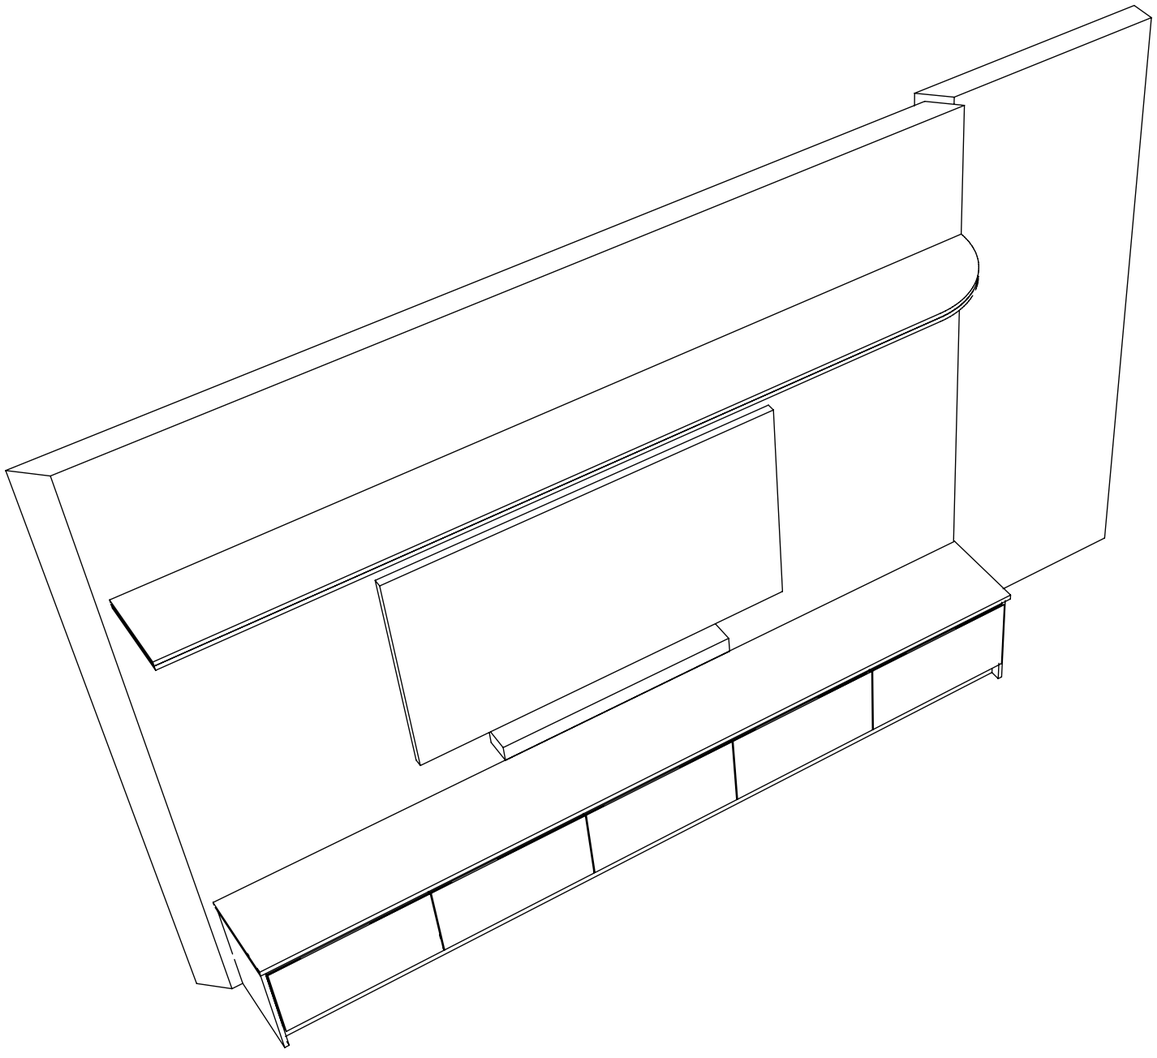

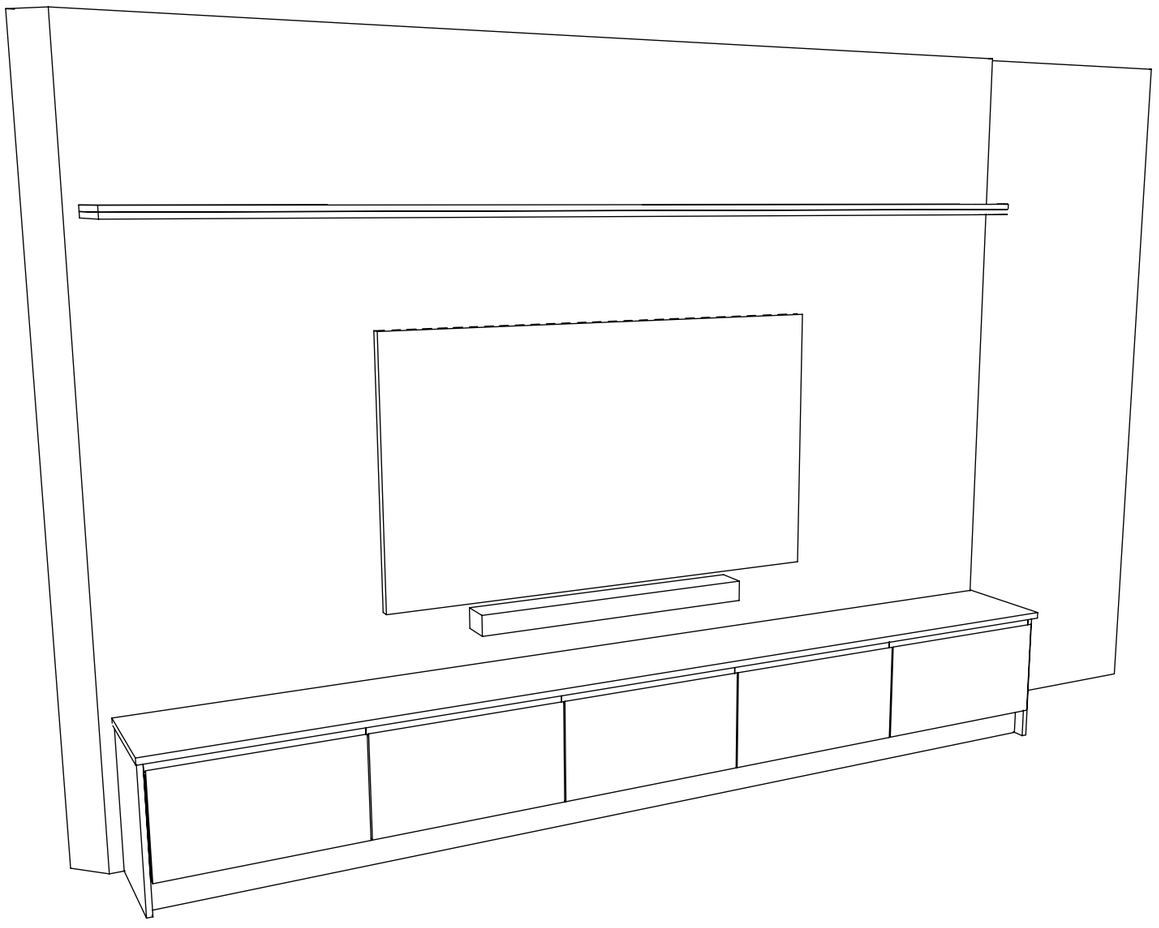

Client Approved Signature : ..... Date : .....

Kitchens By Resident Hero 32 Gateway Drive Phone: 0754471077 mark@residenthero.com.au www.residenthero.com.au	RHK6586 Greystone Constructions	**Scale: NTS**	**Sheet 3 of 3**
	Lounge TV Unit	Do not scale off this drawing.	Drawn By:
			Date: 28/10/26