GENERAL NOTES:
(Read In Conjunction With All Drawings)

DRAWINGS
Dimensions take preference over scale.
Report all discrepancies to the Architect
for clarification prior to construction commencing.

SET OUT
Builder to confirm the set out and all levels and
dimensions on site prior to commencement of work.

CONSTRUCTION
All construction shall comply with the requirements
of the B.C.A. Volume 2 for Class 1a building work.

ENGINEERING
To be read in conjunction with Engineers drawings
and soil report. Refer to engineering drawings for
structural design, footing and slab, tie down, bracing
and all structural details.

CONCRETE
All concrete construction to be in accordance with
AS2870.1 and AS3600.

TIMBER
All timber to be in accordance with AS1684 - 1999
and Structural Engineers drawings.

SEWER CONNECTION
All plumbing points to be connected to sewer
as per council requirements.

STORMWATER
All stormwater shall discharge as per Council
requirements.

POWER CONNECTION
Connect mains supply to meter box via underground
connection.

TERMITE PROTECTION
Provide an approved prorietary type termite
protection barrier to concrete slab and retaining
walls as per manufacturers spec. and in accordance
with the B.C.A. Part 3.1.3 & AS3660.1.

WATERPROOFING INTERNALLY
Waterproofing of internal wet areas shall comply
with the B.C.A. Part 3.8.1 and AS3740. Provide a
proprietary liquid or sheet membrane system and
fall to wastes.

SMOKE ALARMS
Provide hard wired smoke alarms in accordance
with the B.C.A Part 3.7.2 and AS3786.

STEELWORK
All steelwork, fittings and fixtures shall be
hot dipped galvanised.

ALUMINIUM & GLAZING
Shall be in accordance with AS2048 & AS1288,
and shall suit site terrain category. Alumin. framing
shall be clear anodised unless otherwise noted.

GUTTERS AND DOWNPIPES
Roof Plumber is to confirm gutter size and profile, downpipe size,
downpipe quantities, and downpipe locations with builder
prior to installation, all in accordance with the B.C.A Part 3.5.2 and
AS/NZS 3500.3: 2003.

POOL FENCING
All fences & balustrades enclosing swimming pool and over flow pool
to comply Performance Criteria 1 and Acceptable Solution 1 of
Mandatory Part 3.4 of the Queensland Development Code and
AS 1926.1 - 1993 & AS 1926.2 - 1995.

LANDSCAPING
Refer to Landscape Architect's drawings

ENERGY EFFICIENCY
Construction is to comply with B.C.A. Part 3.12
Energy Efficiency Requirements for Climate Zone 2,
and be in accordance with Performance Criteria 1 and
Acceptable Solution1 of Mandatory Part 4.1 of the
Queensalnd Development Code.

Provide roof ventilation to comply with B.C.A. Part 3.12.1.2

Provide energy efficient lighting in accordance with Performance
Criteria 3 and Acceptable Solution 3 of Mandatory Part 4.1 of the
Queensland Development Code.

WATER EFFICIENCY
Provide water saving shower roses (min. 3 star WELS rated)
in accordance with Performance Criteria 6 and Acceptable Solution 6
of Mandatory Part 4.1 of the Queensland Development Code.

Provide water saving tapware (min. 3 star WELS rated) to laundry
tubs, kitchen sinks and basins in accordance with Performance
Criteria 8 and Acceptable Solution 8 of Mandatory Part 4.1 of the
Queensland Development Code.

Ensure the pressure level of water supply does not exceed the levels
necessary for the proper functioning and operation of water fixtures and
fittings, by means in accordance with AS/NZS 3500.1 - 2003.

Provide water saving toilet cisterns (min. 4 star WELS rated) which have
a dual flush function and from which the volume of water provided does
not exceed the volume necessary for the proper functioning and
operation of the toilet, by means in accordance with Performance
Criteria 7 and Acceptable Solution 7 of Mandatory Part 4.1 of the
Queensland Develoment Code.

LIVABLE HOUSING DESIGN STANDARD
Provide compliance with Livable Housing Design Standard 2022
effective 1st October 2023.

SITE DETAILS:

SITE ADDRESS
Villas 149 & 150 - Laguna Retirement Estate
21 Lake Weyba Drive
Noosaville, Qld 4566

RPD
Lot 1 on SP 840222
Parish - Weyba
County - March

LOCAL AUTHORITY
Noosa Shire Council

SITE AREA
2.933 Ha

Drawing List	
Sheet	Title
WD-00	GENERAL NOTES
WD-01	EXISTING FLOOR PLAN
WD-02	SITE PLAN
WD-03	FLOOR PLAN
WD-04	ROOF PLAN
WD-05	ELECTRICAL PLAN
WD-06	ELEVATIONS
WD-07	ELEVATIONS
WD-08	SECTIONS
WD-10	KITCHEN DETAILS
WD-11	BATHROOM & ENSUITE DETAILS
WD-12	LAUNDRY & WARDROBE DETAILS
WD-20	FLOOR PLAN DIMENSIONS + EXT. WALL FINISHES
WD-30	SLAB SETOUT PLAN

ISSUE	DATE	DESCRIPTION
A	01/04/26	BUILDING APPROVAL ISSUE

© COPYRIGHT NOTICE
Copyright of this drawing and design is held permanently by Carma Building Group Pty Ltd. Unauthorised use of this drawing and / or design, or any variation thereof, will trigger immediate legal proceedings.

carma building group
Suite 2 / 199 Gympie Tce, Noosaville Q 456
T 07 5447 1250 F 07 5470 2586
E admin@carmabuildinggroup.com.au

PROJECT
VILLAS 149 & 150
LAGUNA ESTATE
21 LAKE WEYBA DRIVE
NOOSAVILLE

CLIENT
LAGUNA RETIREMENT ESTATE

DRAWING TITLE
GENERAL NOTES

SCALE	@ ORIGINAL SIZ
NTS	A3
DATE	DRAW
APRIL 2026	MW

DRAWING STATUS
FOR CONSTRUCTION

DRAWING NO.	ISSU
LRV149 WD-00	A

'STAGE 3'


STREET ADDRESS
13-21 Lake Weyba Drive, Noosaville, Qld 4566

RPD
Lot 1 on RP 840222
Parish - Weyba
County - March

LOCAL AUTHORITY
Noosa Shire Council

SITE AREA
2.933 Ha

EXISTING
VILLAS 149 & 150
TO BE DEMOLISHED
& REBUILT

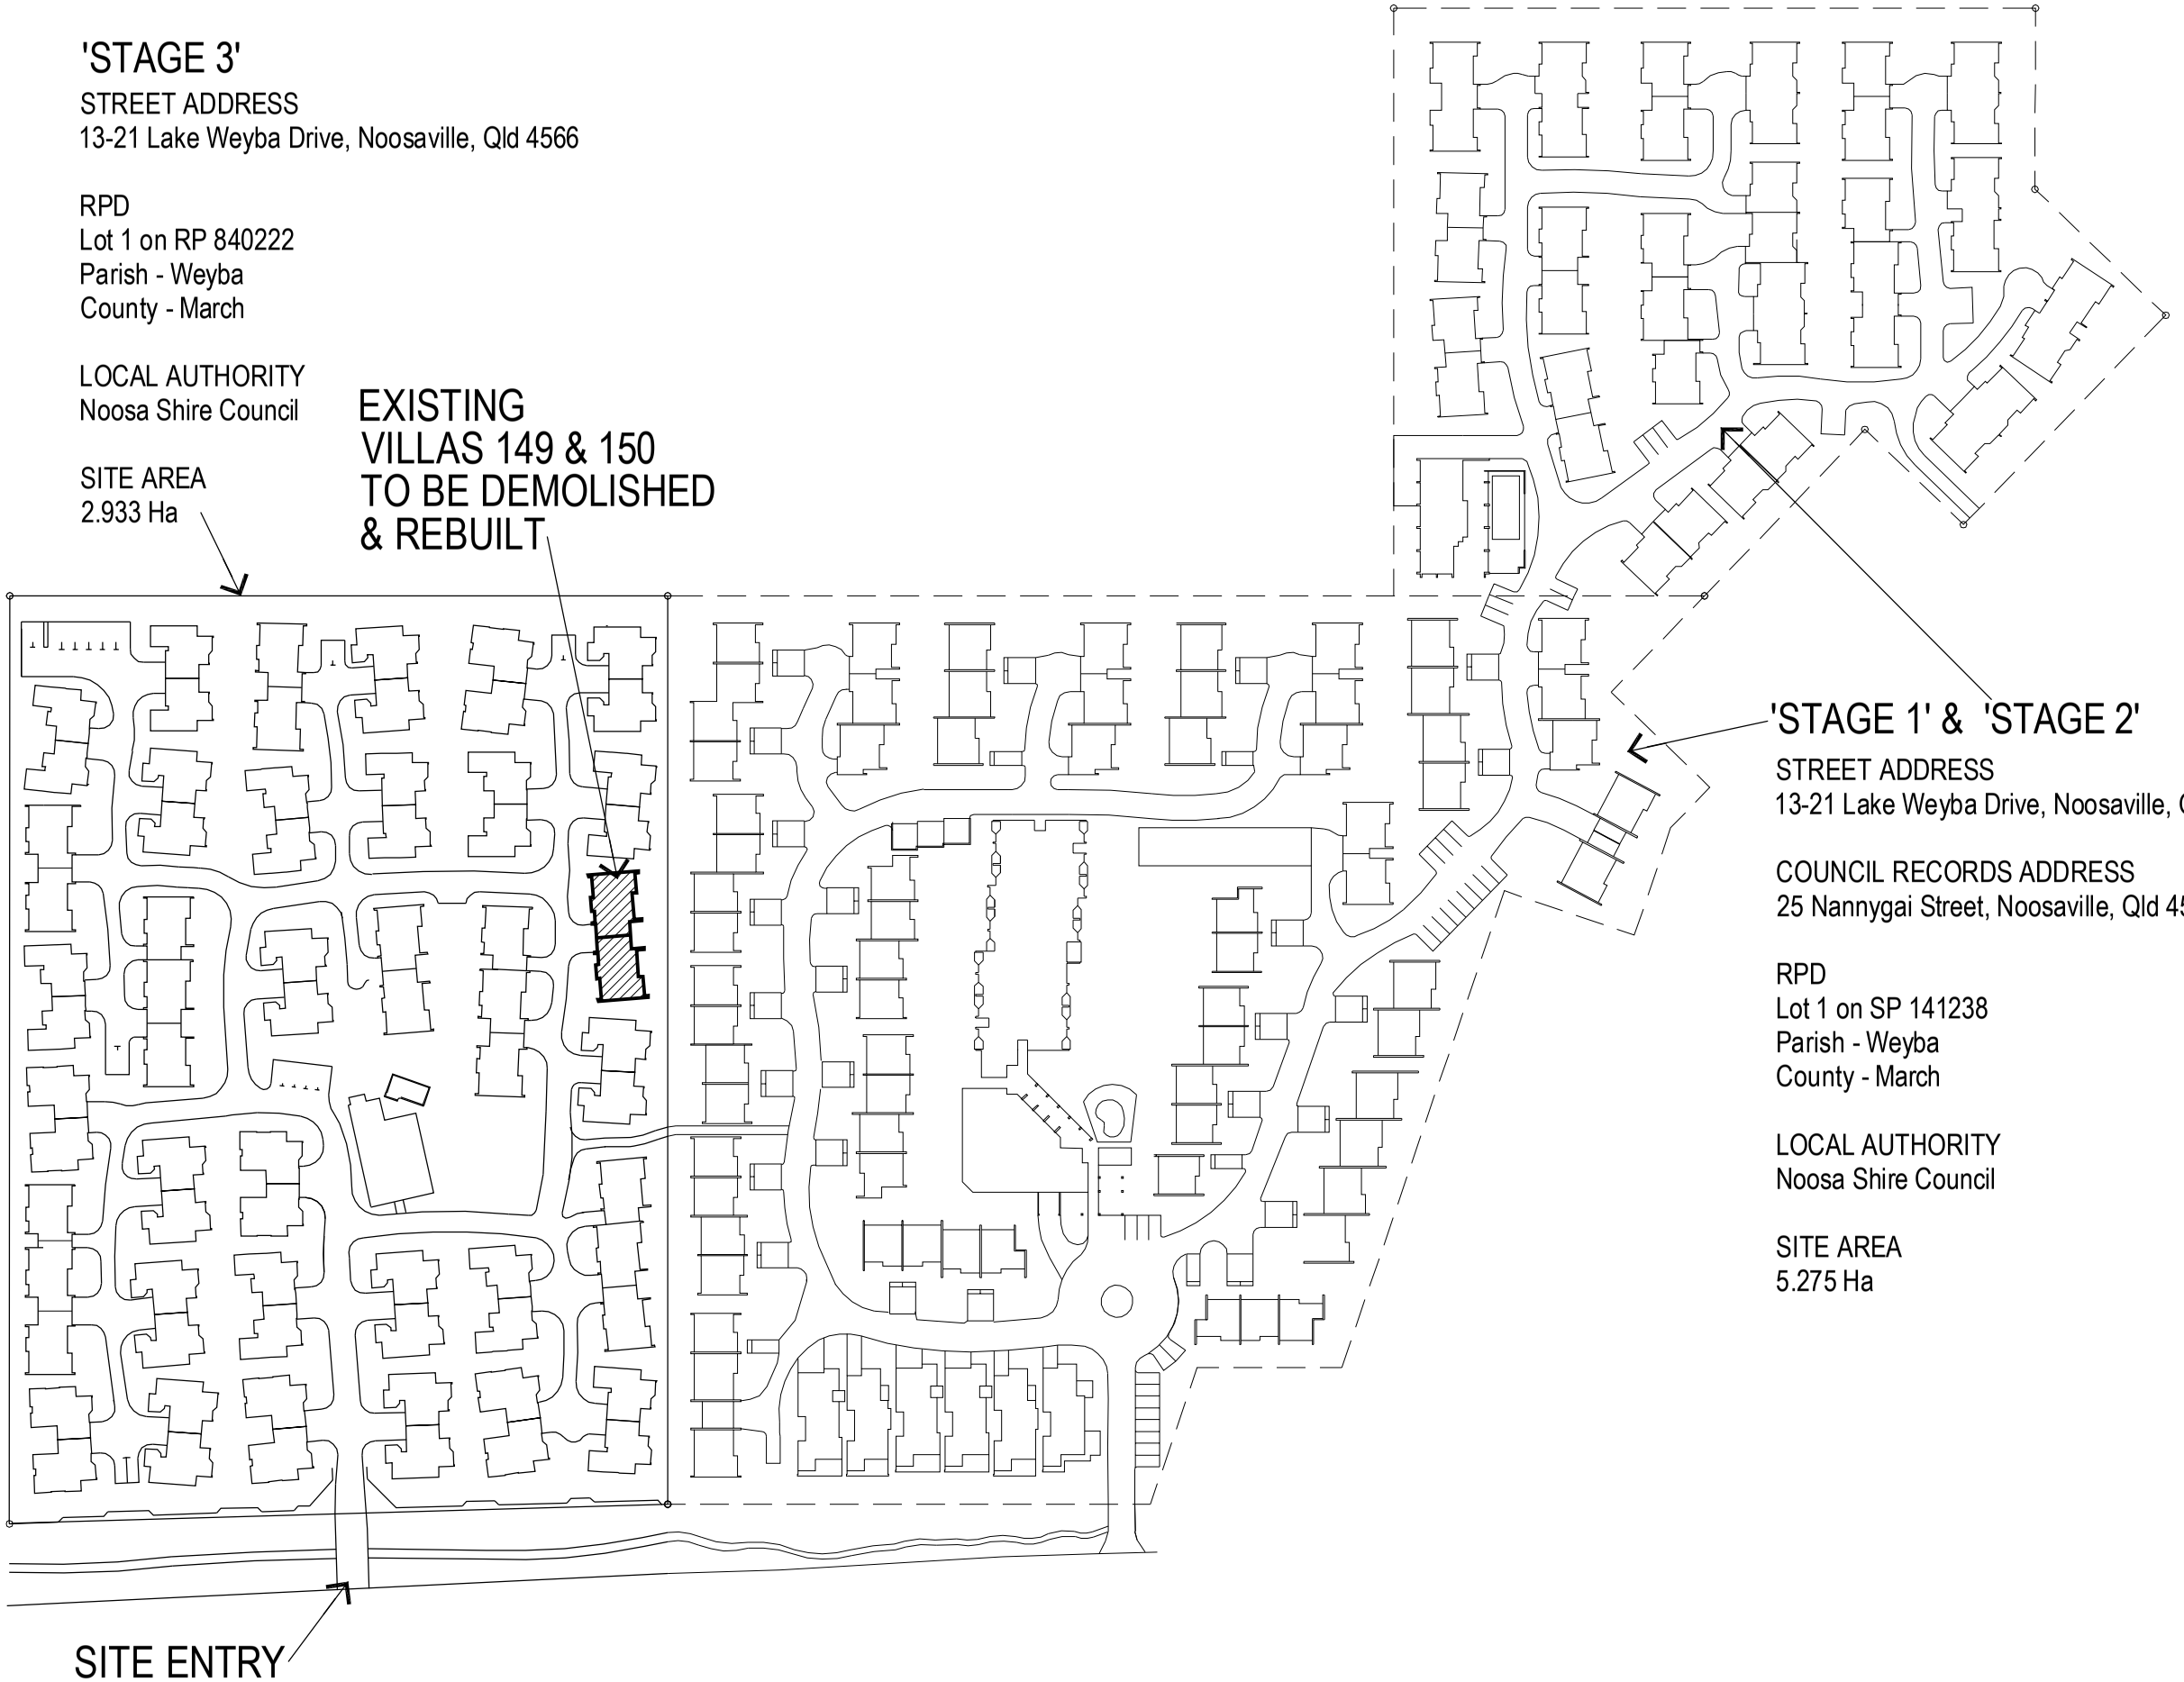

'STAGE 1' & 'STAGE 2'

STREET ADDRESS
13-21 Lake Weyba Drive, Noosaville, Qld 4566

COUNCIL RECORDS ADDRESS
25 Nannygai Street, Noosaville, Qld 4566

RPD
Lot 1 on SP 141238
Parish - Weyba
County - March

LOCAL AUTHORITY
Noosa Shire Council

SITE AREA
5.275 Ha

21 LAKE WEYBA DRIVE

ISSUE	DATE	DESCRIPTION
A	01/04/26	ISSUED FOR APPROVALS

© COPYRIGHT NOTICE
Copyright of this drawing and design is held permanently by Carma Building Group Pty Ltd. Unauthorised use of this drawing and / or design, or any variation thereof, will trigger immediate legal proceedings.


carma building group
Suite 2 / 199 Gympie Tce, Noosaville Q 45
T 07 5447 1250 F 07 5470 2586
E admin@carmabuildinggroup.com.au

PROJECT
VILLAS 149 & 150
LAGUNA ESTATE
21 LAKE WEYBA DRIVE
NOOSAVILLE

CLIENT
LAGUNA RETIREMENT ESTATE

DRAWING TITLE
SITE PLAN

SCALE	@ ORIGINAL SIZ
1:1500	A3
DATE	DRAW
APRIL 2026	MW
DRAWING STATUS	
FOR CONSTRUCTION	
DRAWING NO.	ISSU
LRV149 WD-01	A

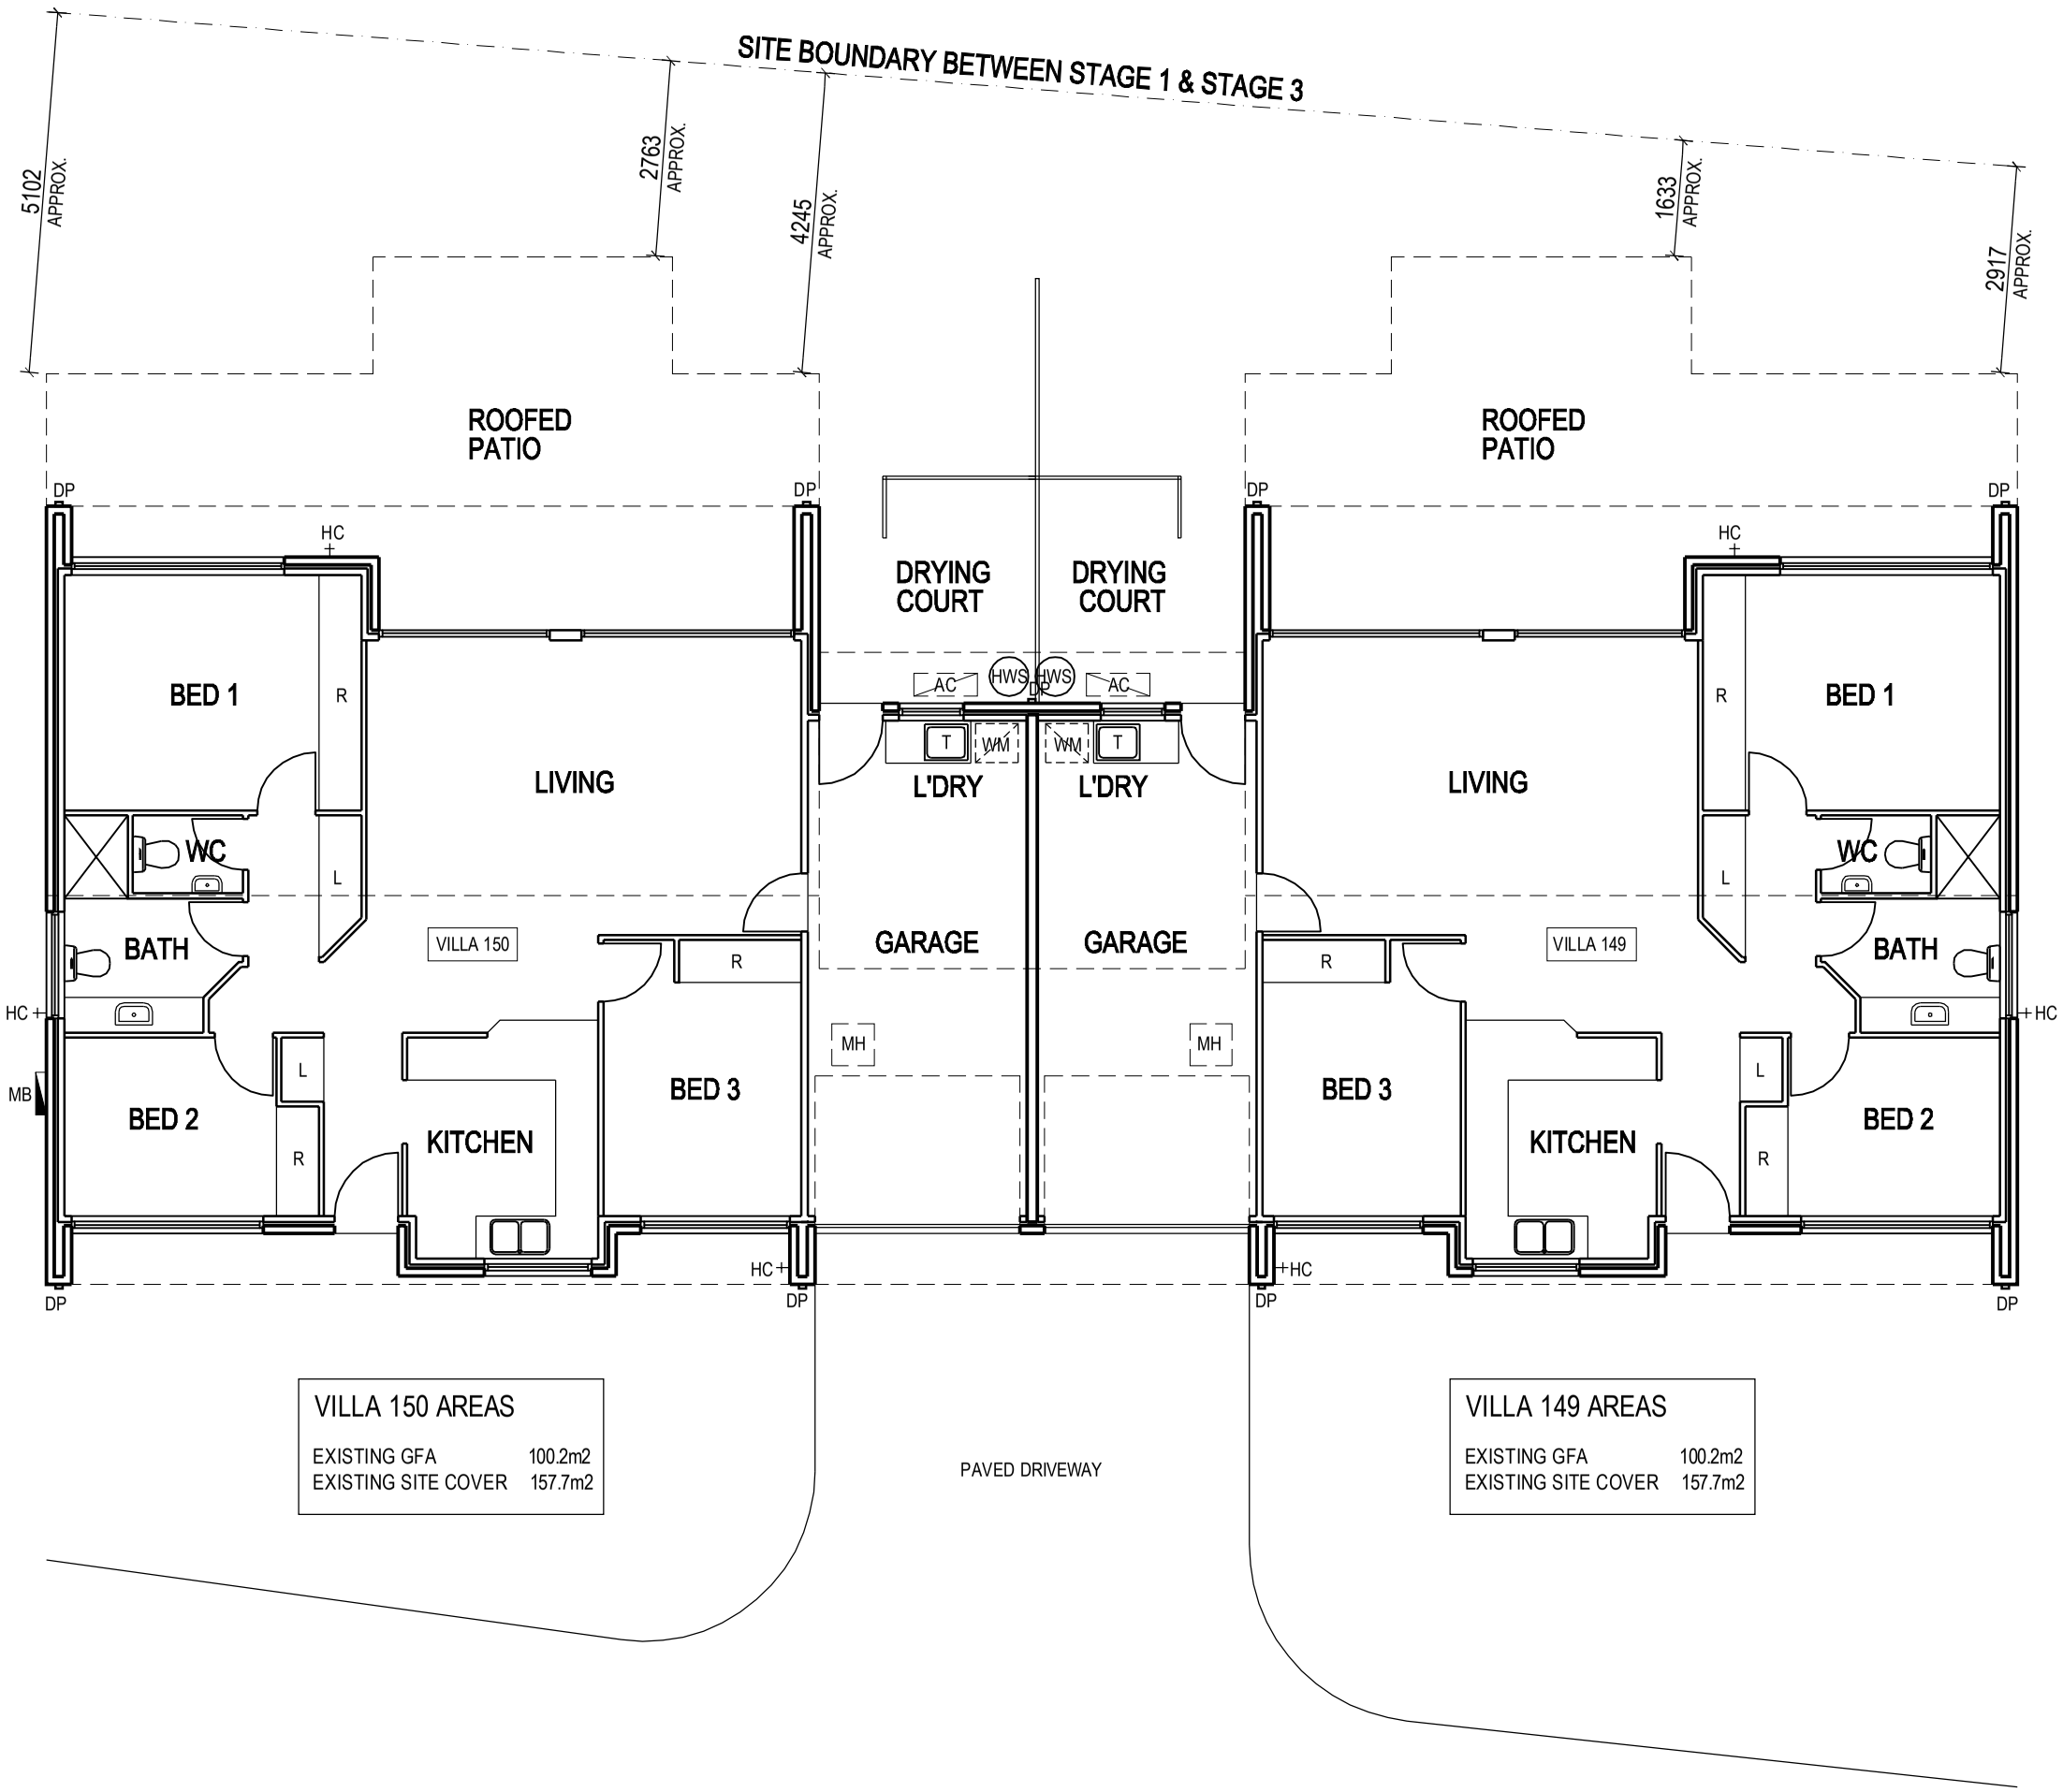

VILLA 150 AREAS	
EXISTING GFA	100.2m2
EXISTING SITE COVER	157.7m2

VILLA 149 AREAS	
EXISTING GFA	100.2m2
EXISTING SITE COVER	157.7m2

ISSUE	DATE	DESCRIPTION
A	01/04/26	ISSUED FOR APPROVALS

© COPYRIGHT NOTICE
Copyright of this drawing and design is held permanently by Carma Building Group Pty Ltd. Unauthorised use of this drawing and / or design, or any variation thereof, will trigger immediate legal proceedings.

carma building group
Suite 2 / 199 Gympie Tce, Noosaville Q 45
T 07 5447 1250 F 07 5470 2586
E admin@carmabuildinggroup.com.au

PROJECT
VILLAS 149 & 150
LAGUNA ESTATE
21 LAKE WEYBA DRIVE
NOOSAVILLE

CLIENT
LAGUNA RETIREMENT ESTATE

DRAWING TITLE
EXISTING FLOOR PLAN

SCALE	@ ORIGINAL SIZ
1:100	A3
DATE	DRAW
APRIL 2026	MW

DRAWING STATUS
FOR CONSTRUCTION

DRAWING NO.	ISSU
LRV149 WD-02	A

VILLA 150 AREAS
EXCL. EAVES


VILLA	132.6m2
GARAGE	22.1m2
ALFRESCO + TERRACE	27.3m2
PATIO	8.9m2
DRYING COURT	9.6m2
TOTAL - V150	200.5m2

FLOOR PLAN ABBREVIATIONS & LEGEND

AC	AIRCONDITIONER CONDENSOR
APPL	APPLIANCE CUPBD
BAL	BALUSTRADE
BB	BRICK BASE
BH	BULKHEAD OVER
BK	BENCH TOP
BL	BENCH
BR	BROOM CUPBD
BS	BASIN
BTH	BATH
CB	CIRCUIT BOARD
CL	CLOTHESLINE
CS	CAVITY SLIDING DOOR
CT	COOKTOP
DP	DOWNPIPE
DW	DISHWASHER SPACE
ED	EXTRACTOR FAN
EG	EAVES GUTTER
EW	EXISTING WINDOW
FNC	FENCE
FR	REFRIGERATOR SPACE
FW	FLOOR WASTE
GB	GAS BOTTLES
GT	GATE
HC	HOSE COCK
HWS	HOT WATER SYSTEM
L	LINEN CUPBOARD (4 SHELVES)
LT	LAUNDRY TROUGH
LC	LINEN CHUTE
MB	METER BOX
MH	MANHOLE 800 X 800
ORG	OVERFLOW RELIEF GULLY
P	PANTRY
PJ	PLUMBING JUNCTION POINT
R	WARDROBE
S	SINK
SCR	SCREEN
SD	SMOKE DETECTOR (INTERCONNECTED)
SH	SHELVES
SHR	SHOWER
SK	SKYLIGHT
SOB	SHOWER OVER BATH
SP	STEEL POST
SRD	SLIDING ROBE DOORS
SS	SERVICES SHAFT
T	LAUNDRY TUB
TP	TIMBER POST
TS	TOILET SUITE
UBO	UNDER BENCH OVEN
VB	VANITY BASIN
WM	WASHING MACHINE SPACE
WMT	WATER MAINS TAP
WO	WALL OVEN
WR	WINE RACK
WT	WATER TANK

VILLA 149 AREAS
EXCL. EAVES

VILLA	133.7m2
GARAGE	21.0m2
ALFRESCO + TERRACE	27.3m2
PATIO	8.9m2
DRYING COURT	8.2m2
TOTAL - V149	199.1m2

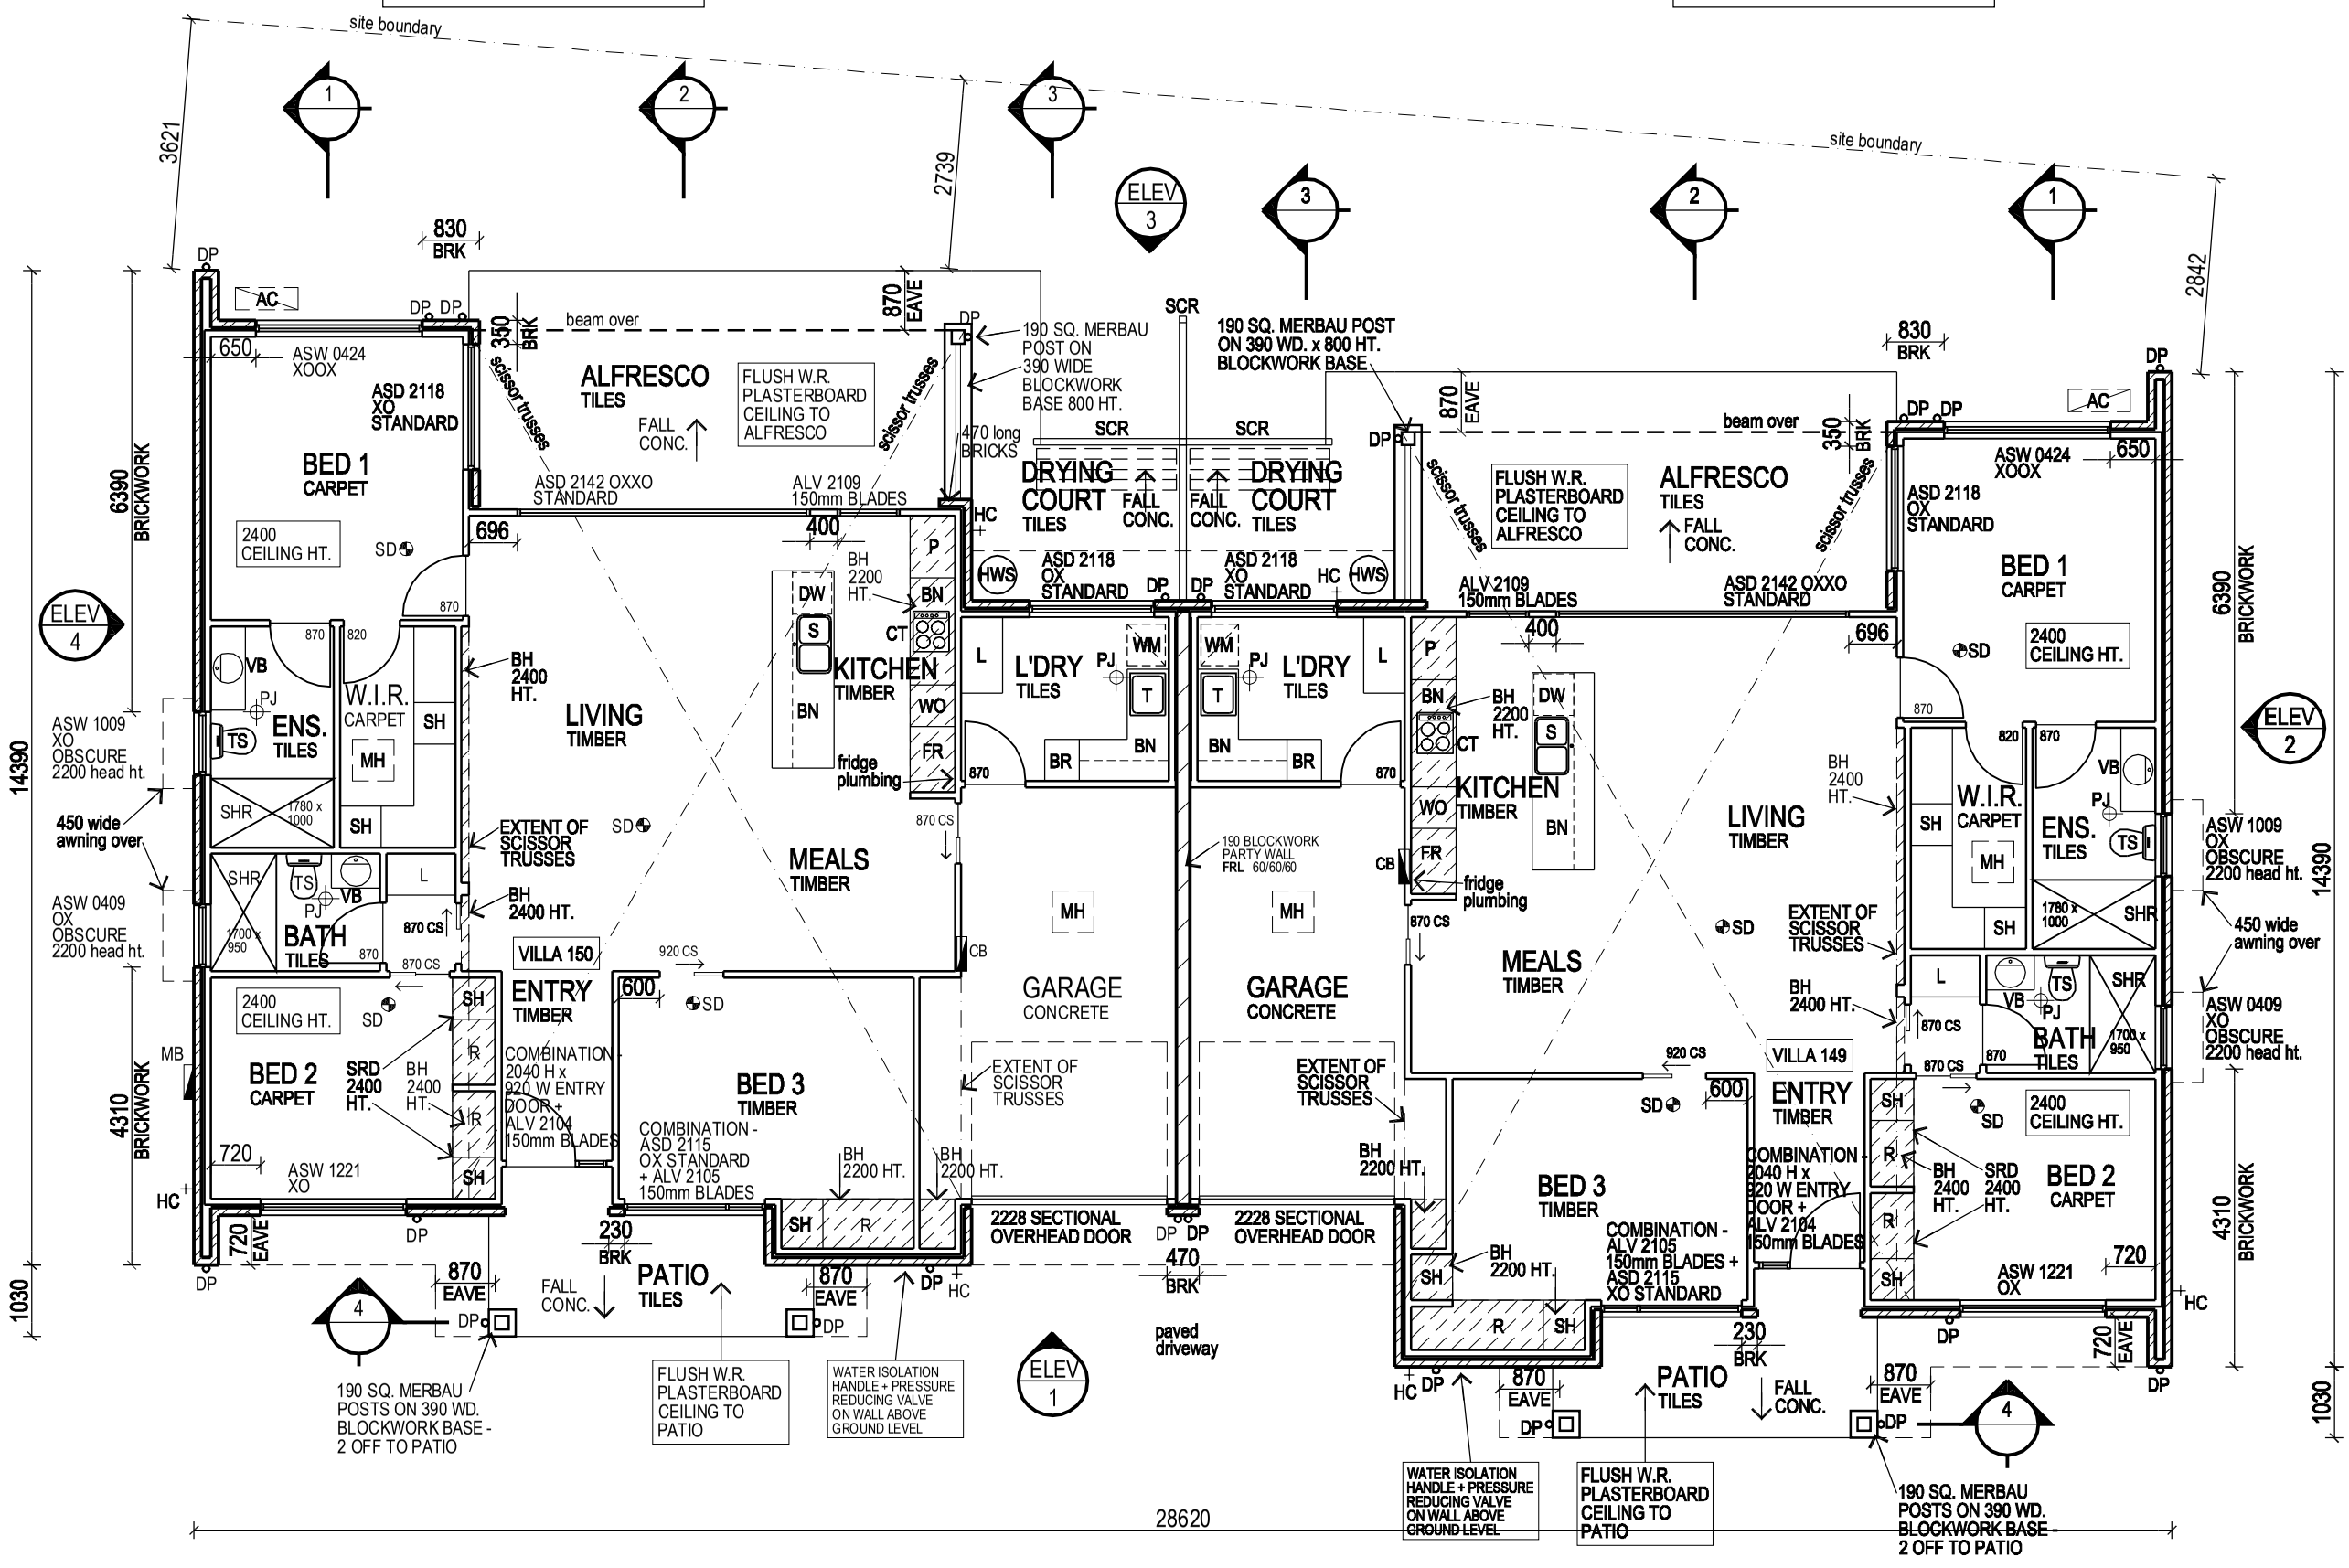

ISSUE	DATE	DESCRIPTION
A	01/04/26	ISSUED FOR APPROVALS
B	01/09/26	REAR TERRACE SLAB DELETED
C	25/10/26	DRYING COURT FLOOR NOW TILES

© COPYRIGHT NOTICE
Copyright of this drawing and design is held permanently by Carma Building Group Pty Ltd. Unauthorised use of this drawing and / or design, or any variation thereof, will trigger immediate legal proceedings.


carma building group
Suite 2 / 199 Gympie Tce, Noosaville Q 45
T 07 5447 1250 F 07 5470 2586
E admin@carmabuildinggroup.com.au

PROJECT
VILLAS 149 & 150
LAGUNA ESTATE
21 LAKE WEYBA DRIVE
NOOSAVILLE

CLIENT
LAGUNA RETIREMENT ESTATE

DRAWING TITLE
FLOOR PLAN

SCALE	1:100 @ ORIGINAL SIZ A3
DATE	APRIL 2026
DRAWN	MW
DRAWING STATUS	FOR CONSTRUCTION
DRAWING NO.	LRV149 WD-03
ISSUE	C

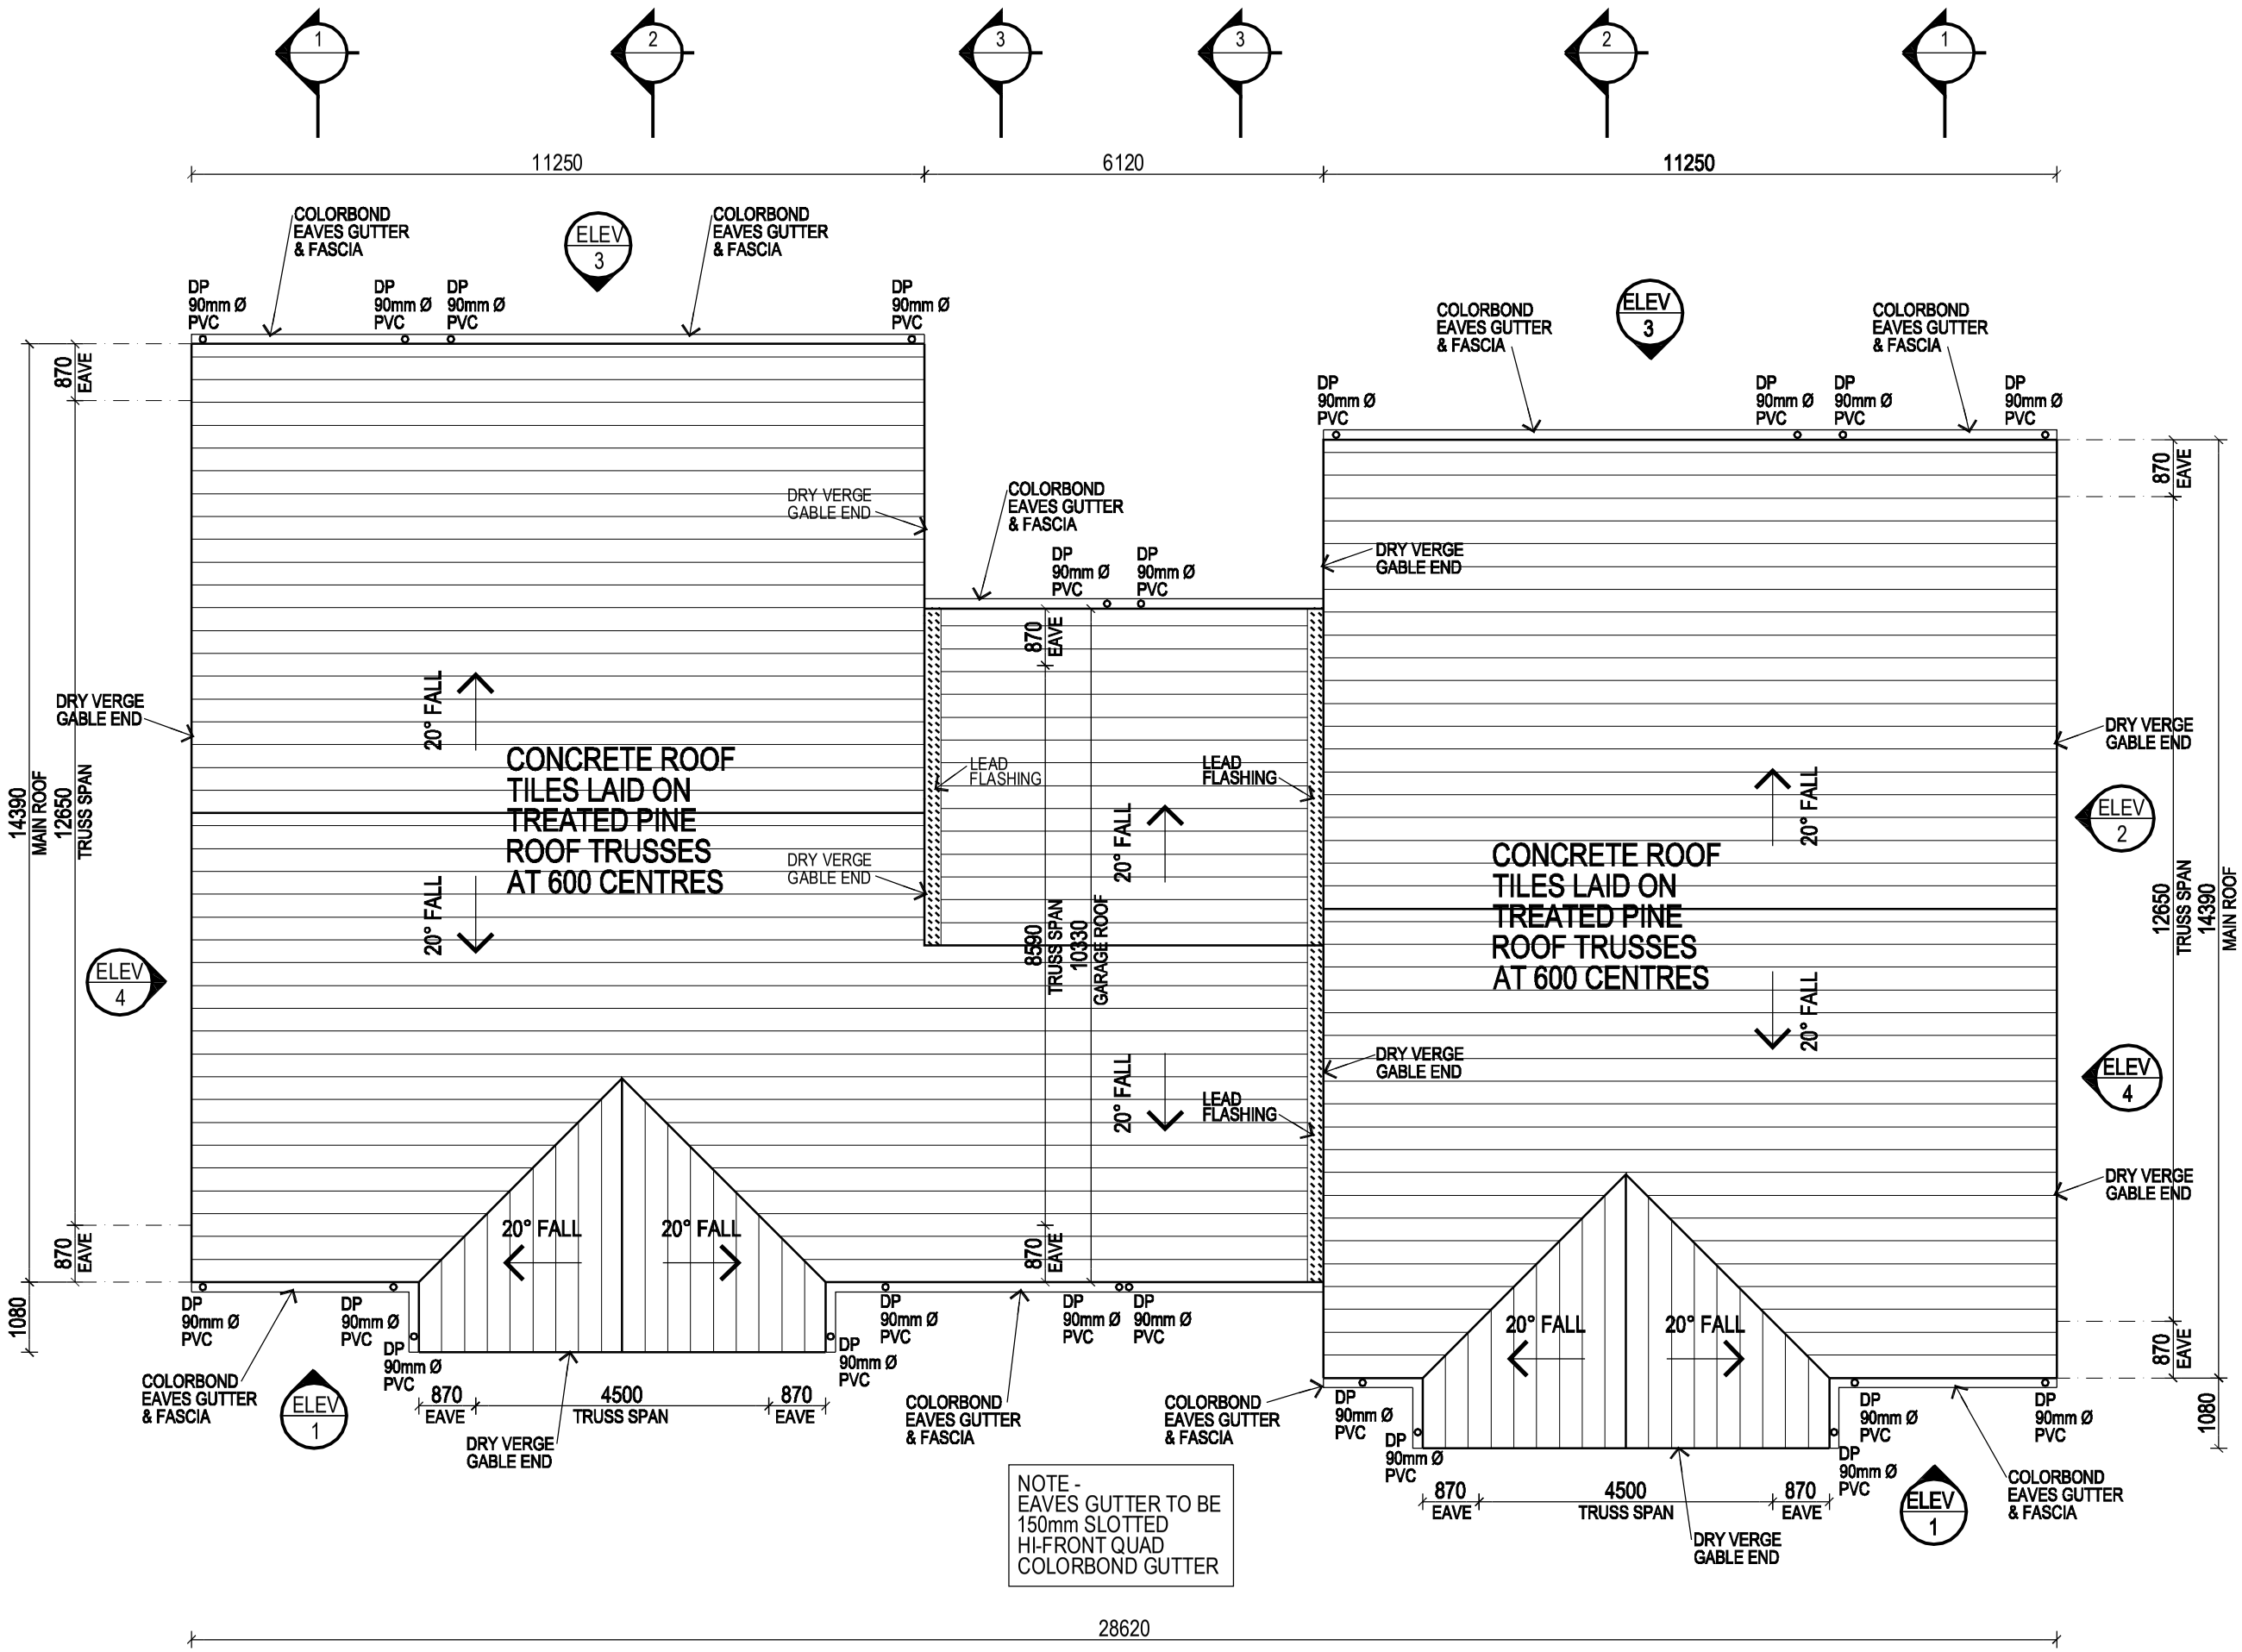

NOTE -
EAVES GUTTER TO BE
150mm SLOTTED
HI-FRONT QUAD
COLORBOND GUTTER

ISSUE	DATE	DESCRIPTION
A	01/04/26	ISSUED FOR APPROVALS

© COPYRIGHT NOTICE
Copyright of this drawing and design is held permanently by Carma Building Group Pty Ltd. Unauthorised use of this drawing and / or design, or any variation thereof, will trigger immediate legal proceedings.

carma building group
Suite 2 / 199 Gympie Tce, Noosaville Q 45(
T 07 5447 1250 F 07 5470 2586
E admin@carmabuildinggroup.com.au

PROJECT
VILLAS 149 & 150
LAGUNA ESTATE
21 LAKE WEYBA DRIVE
NOOSAVILLE

CLIENT
LAGUNA RETIREMENT ESTATE

DRAWING TITLE
ROOF PLAN

SCALE	@ ORIGINAL SIZ
1:100	A3
DATE	DRAW
APRIL 2026	MW

DRAWING STATUS
FOR CONSTRUCTION


DRAWING NO.	ISSU
LRV149 WD-04	A

ELECTRICAL PLAN ABBREVIATIONS & LEGEND

AC	AIRCONDITIONING CONDENSOR
ACC	AIRCONDITIONING CONTROL PANEL (1400 HT.)
BL	BAYONET LIGHT POINT
CB	CIRCUIT BOARD
CF	CEILING FAN
CFL	CEILING FAN WITH LIGHT
CT	COOKTOP
DAT	DATA POINT (ON 2nd PHONE LINE)
DB	DOOR BELL CHIME BUTTON
DGPO	DOUBLE GENERAL POWER OUTLET
DK	DECK UPLIGHT
DL	DOWNLIGHT
DMR	DIMMER SWITCH - UNIVERSAL TYPE
DV	DUCTED VACUUM SYSTEM INLET
DW	DISHWASHER
EXH	EXHAUST FAN / LIGHT COMBO WITH 2 SWITCHES
FL	FLUORESCENT STRIP LIGHT
GD	GARAGE DOOR CONTROLLER
HL	HEAT LAMP
HWS	HOT WATER SYSTEM
ICM	INTERCOM POINT
IXL	IXL TASTIC OR SIM. HEAT / EXHAUST LAMP
JB	JUNCTION BOX
MB	METER BOX
MLC	MOTORISED LOUVRE CONTROL SWITCH
MW	MICROWAVE
NBN	NATIONAL BROADBAND NETWORK BOX
PH	PHONE POINT
PND	PENDANT LIGHT
RA	RETURN AIR GRILLE
REF	REFRIGERATOR SPACE
RH	RANGEHOOD
SA	SUPPLY AIR REGISTER
SD	SMOKE DETECTOR (MAINS POWERED & INTERCONNECTED)
SGPO	SINGLE GENERAL POWER OUTLET
SL	SURFACE OR SOFFIT MOUNTED LIGHT
SNS	MOTION SENSOR
TV	TV POINT INCL. PAY TV
VC	VOLUME CONTROL FOR CEILING SPEAKERS
WL	WALL MOUNTED LIGHT FITTING
WM	WASHING MACHINE SPACE
WO	WALL OVEN
WR	WATER RESISTANT GPO

GPO HEIGHTS

BEHIND REFRIGERATOR - 1900 ABOVE FLOOR
FOR GARAGE DOOR OPENER - REFER PLAN
FOR DUCTED VACUUM SYSTEM MOTOR - 1500 ABOVE FLOOR
KITCHEN, BATHROOMS & LAUNDRY - 150 ABOVE BENCHTOP
BEHIND WASHING MACHINE - 1200 ABOVE FLOOR
ELSEWHERE - 300 ABOVE FLOOR

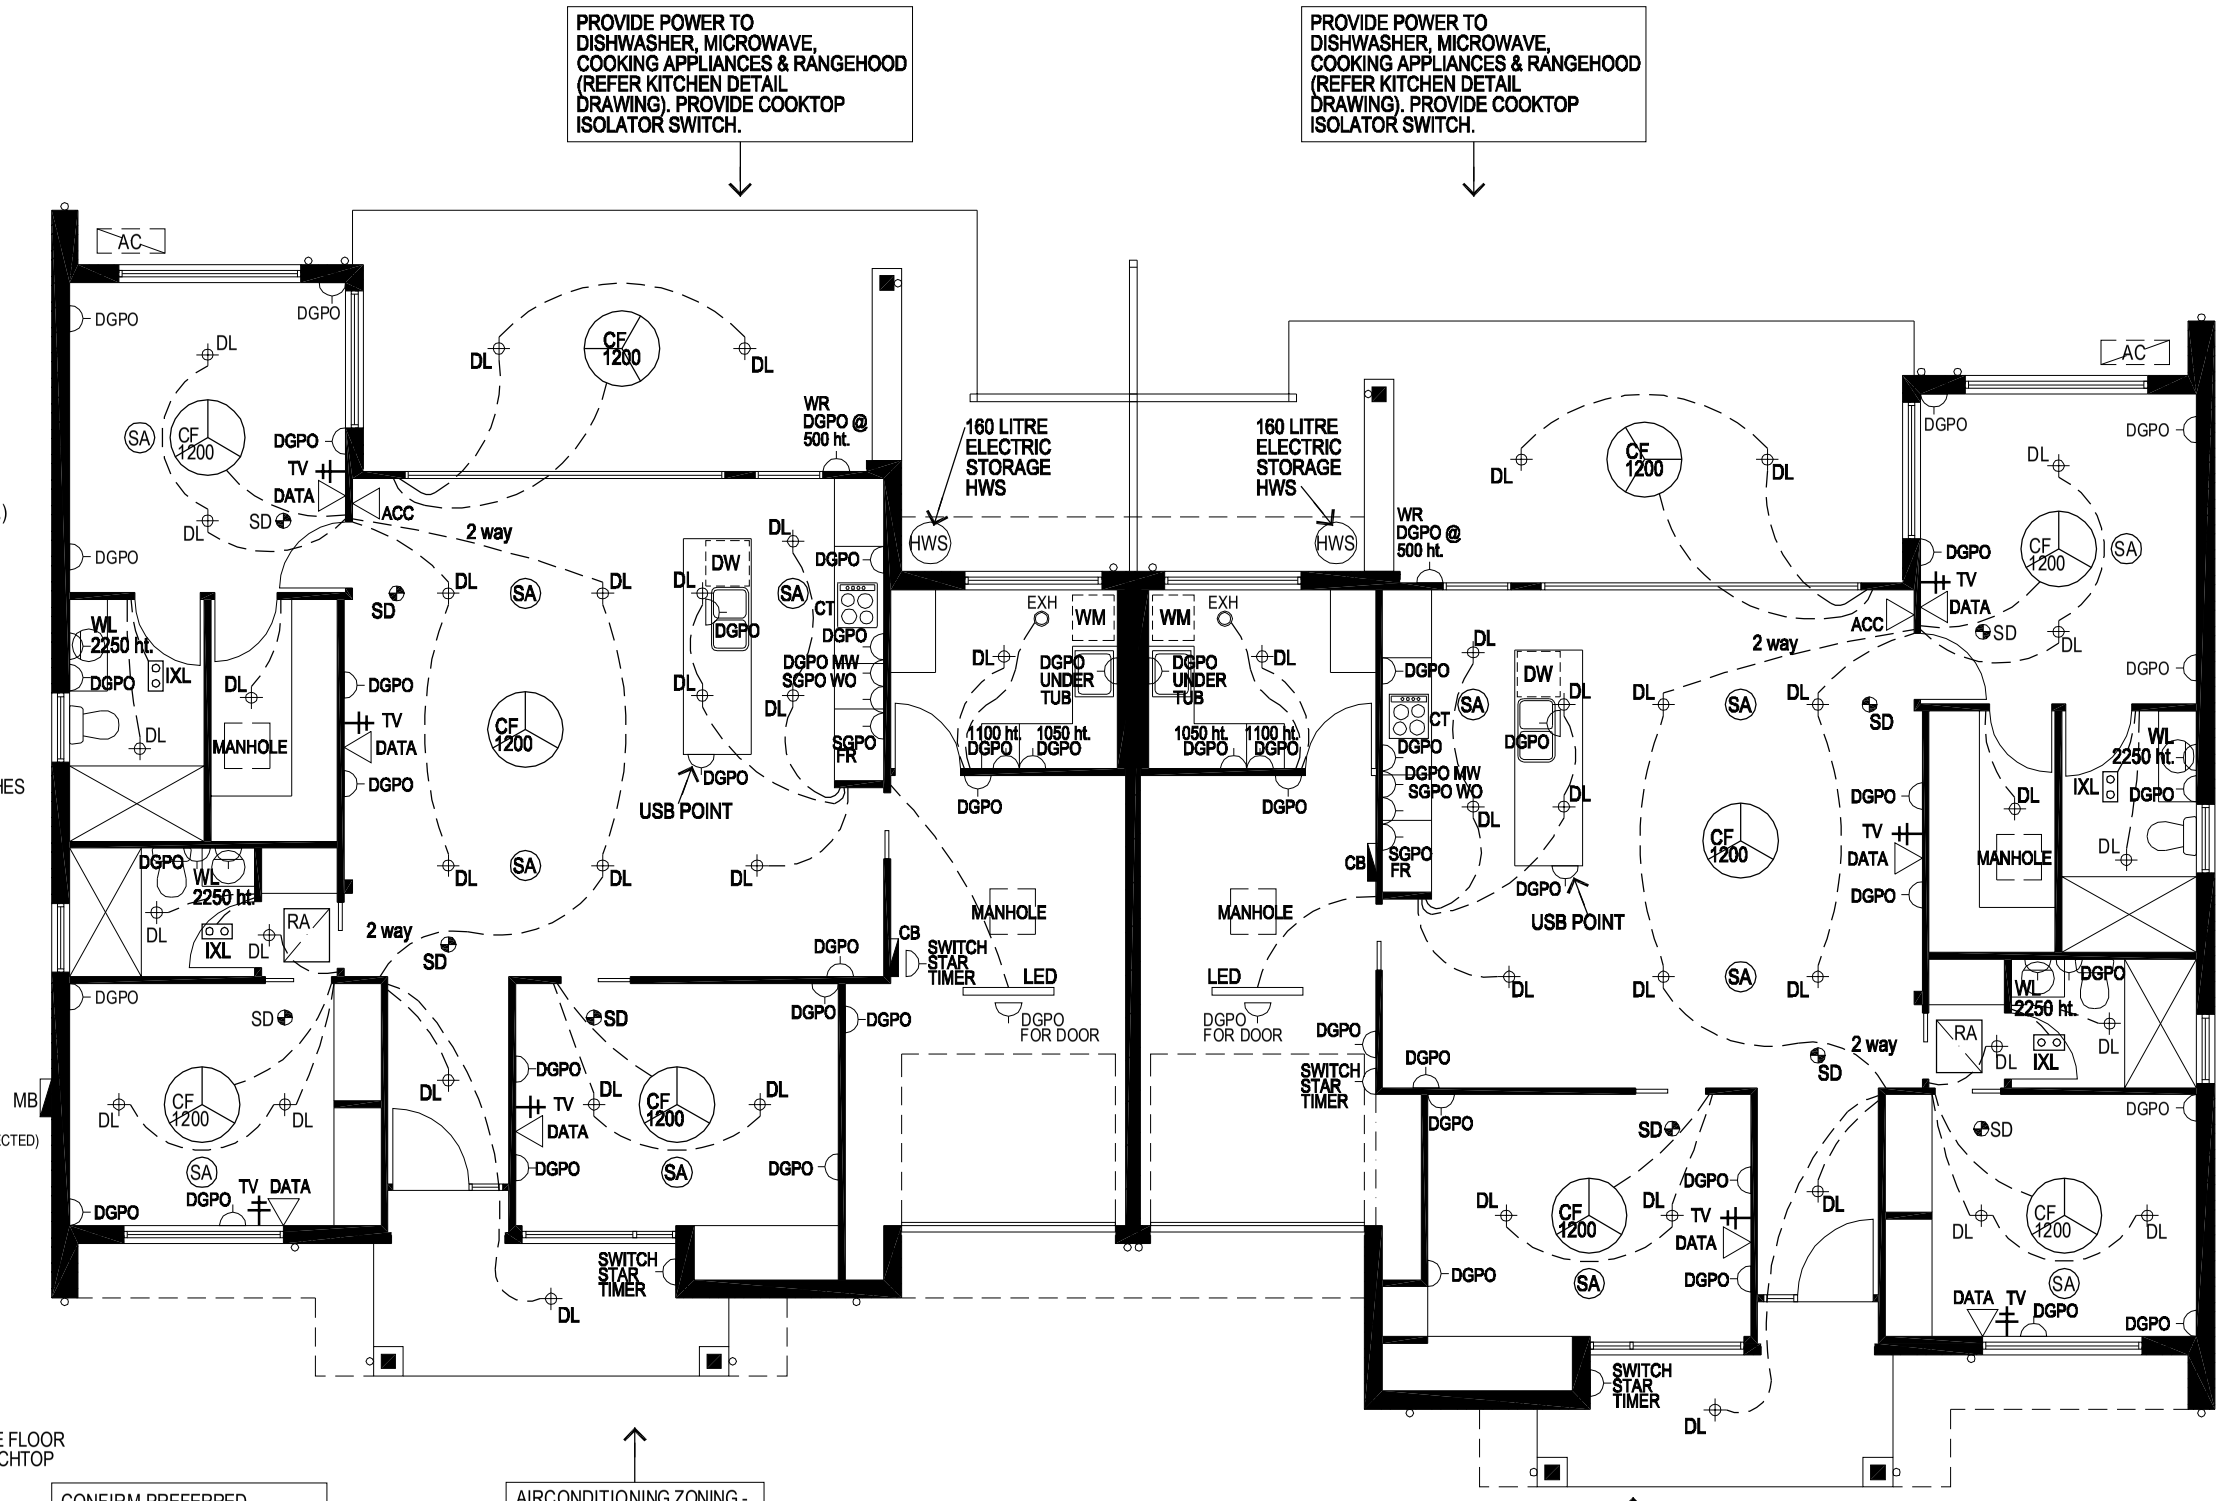

ISSUE	DATE	DESCRIPTION
A	01/04/26	ISSUED FOR APPROVALS
B	20/10/26	LIVING RM. SMOKE DETECTORS REVISED

© COPYRIGHT NOTICE
Copyright of this drawing and design is held permanently by Carma Building Group Pty Ltd. Unauthorised use of this drawing and / or design, or any variation thereof, will trigger immediate legal proceedings.

carma building group
Suite 2 / 199 Gympie Tce, Noosaville Q 45
T 07 5447 1250 F 07 5470 2586
E admin@carmabuildinggroup.com.au

PROJECT
VILLAS 149 & 150
LAGUNA ESTATE
21 LAKE WEYBA DRIVE
NOOSAVILLE


CLIENT
LAGUNA RETIREMENT ESTATE

DRAWING TITLE
ELECTRICAL PLAN

SCALE	@ ORIGINAL SIZ
1:100	A3
DATE	DRAW
APRIL 2026	MW

DRAWING STATUS
FOR CONSTRUCTION

DRAWING NO.	ISSU
LRV149 WD-05	B

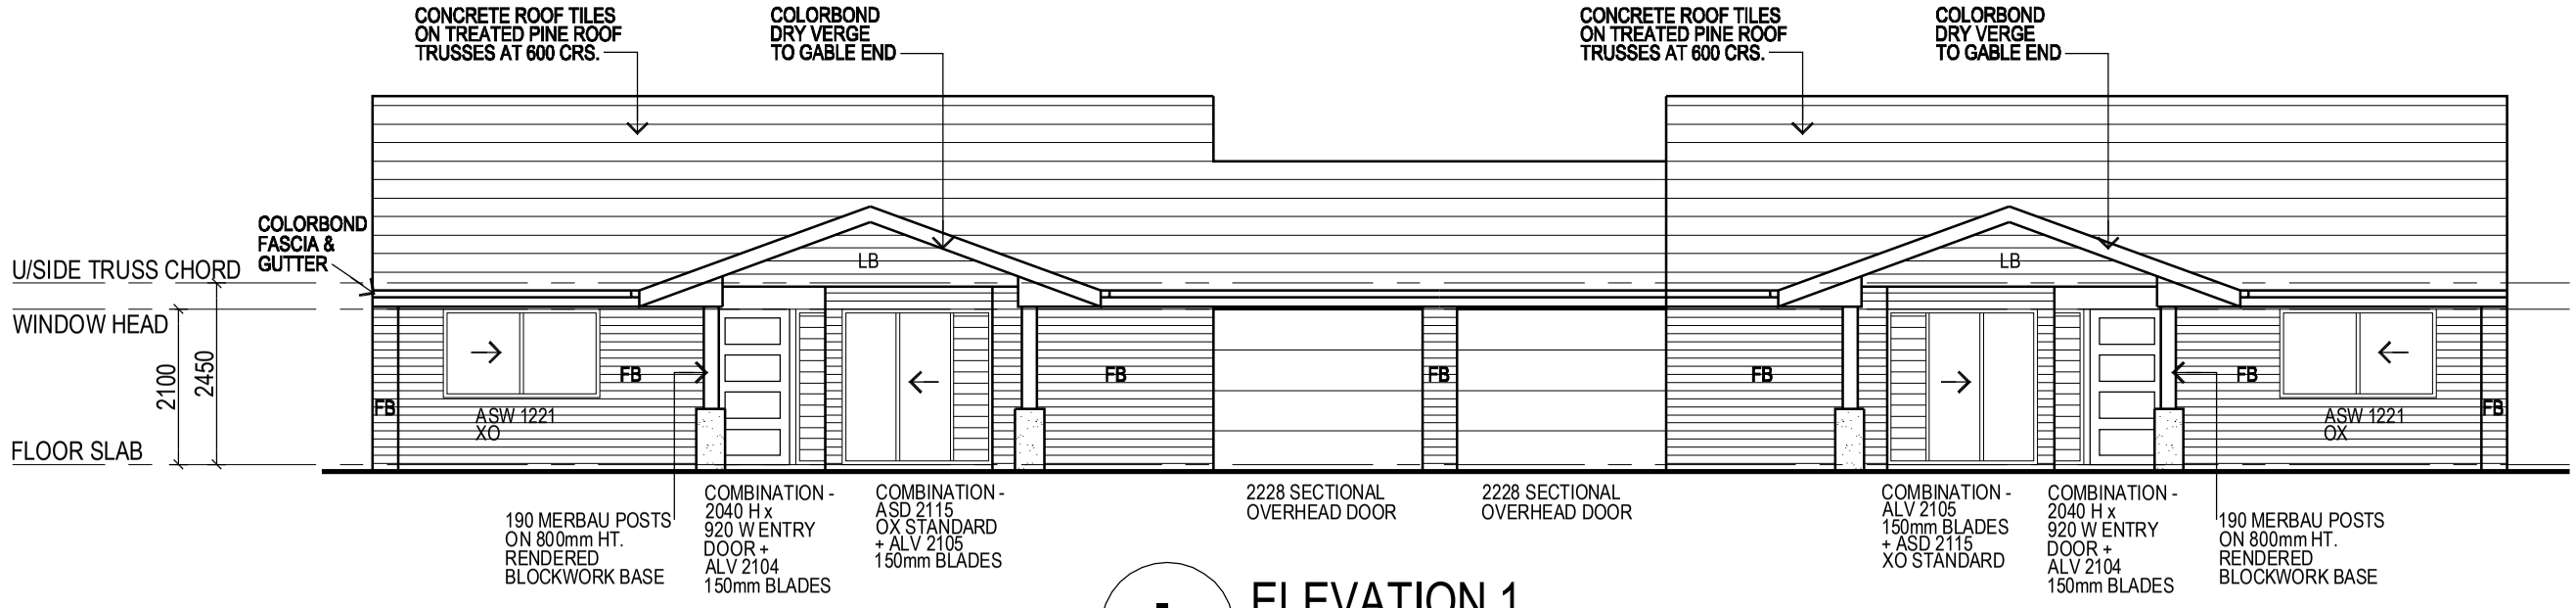

- ELEVATION 1

VILLAS 149 & 150 1:100


ELEVATIONS & SECTIONS ABBREVIATIONS & LEGEND

GENERAL ABBREVIATIONS

AC	AXON CLADDING
AWN	AWNING (PROJECTION NOTED)
BAL	BALUSTRADE
CH	CEILING HEIGHT
FB	FACE BRICKWORK
FFL	FINISHED FLOOR LEVEL
FGL	FINISHED GROUND LEVEL
FNC	FENCE
LB	LINEABOARD CLADDING
NGL	NATURAL GROUND LINE
OH	OVERHANG
RB	RENDERED BLUEBOARD
RM	RENDERED MASONRY
SC	SHADOWCLAD CLADDING
SIF	STONE INLAY FEATURE
TOW	TOP OF WALL
WH	WINDOW HEAD
WL	WALL LIGHT

WINDOW ABBREVIATIONS

AAW	ALUM. FRAMED AWNING WINDOW
ABD	ALUM. FRAMED BIFOLD STACKER DOOR
ABW	ALUM. FRAMED BIFOLD STACKER WINDOW
ACD	ALUM. FRAMED CASEMENT DOOR
ACW	ALUM. FRAMED CASEMENT WINDOW
ADH	ALUM. FRAMED DOUBLE HUNG WINDOW
AFD	ALUM. FRAMED FRENCH DOORS
AFG	ALUM. FRAMED FIXED GLAZING
ALV	ALUM. FRAMED LOUVRE WINDOW
ASD	ALUM. FRAMED SLIDING DOOR
ASH	ALUM.FRAMED SINGLE HUNG WINDOW
ASW	ALUM. FRAMED SLIDING WINDOW
CL	CLEAR GLAZING
OBS	OBSCURE GLAZING
SB	SOLAR BLOCK GLAZING
T	TINTED GLAZING

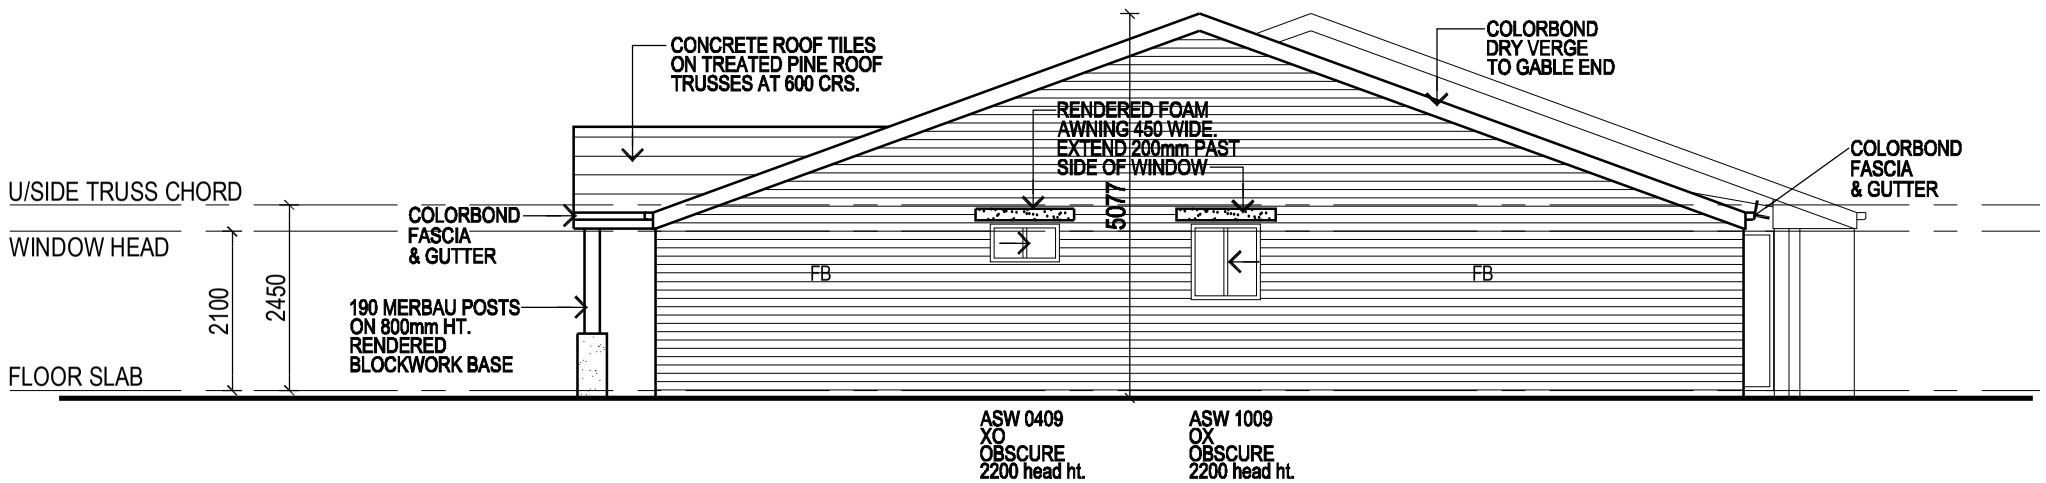

- ELEVATION 2

VILLAS 149 & 150 1:100

ISSUE	DATE	DESCRIPTION
A	01/04/26	ISSUED FOR APPROVALS

© COPYRIGHT NOTICE
Copyright of this drawing and design is held permanently by Carma Building Group Pty Ltd. Unauthorised use of this drawing and / or design, or any variation thereof, will trigger immediate legal proceedings.

carma building group
Suite 2 / 199 Gympie Tce, Noosaville Q 45
T 07 5447 1250 F 07 5470 2586
E admin@carmabuildinggroup.com.au

PROJECT
VILLAS 149 & 150
LAGUNA ESTATE
21 LAKE WEYBA DRIVE
NOOSAVILLE


CLIENT
LAGUNA RETIREMENT ESTATE

DRAWING TITLE
ELEVATIONS
Sheet 1 of 2

SCALE	@ ORIGINAL SIZ
1:100	A
DATE	DRAW
APRIL 2026	MW

DRAWING STATUS
FOR CONSTRUCTION

DRAWING NO.	ISSU
LRV149 WD-06	A

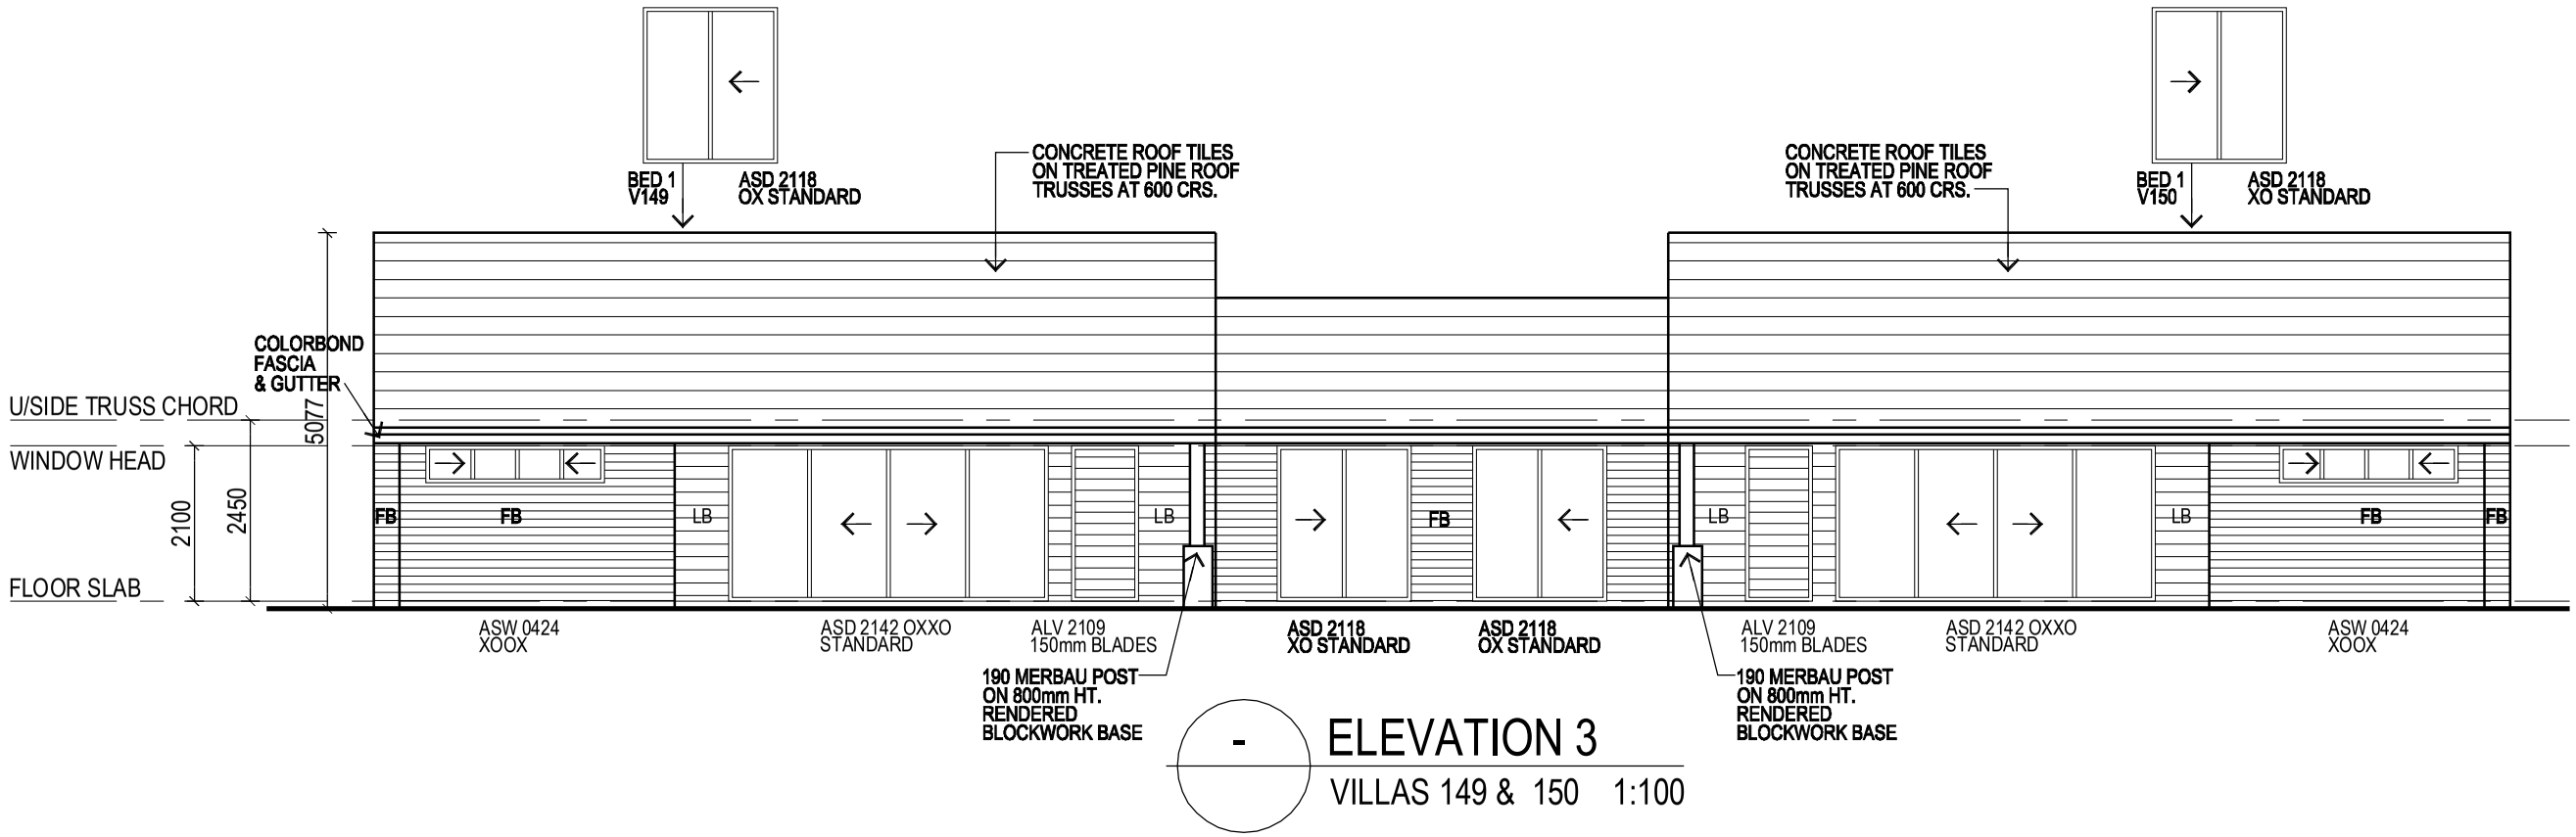

- ELEVATION 3

VILLAS 149 & 150 1:100


ELEVATIONS & SECTIONS ABBREVIATIONS & LEGEND

GENERAL ABBREVIATIONS

AC	AXON CLADDING
AWN	AWNING (PROJECTION NOTED)
BAL	BALUSTRADE
CH	CEILING HEIGHT
FB	FACE BRICKWORK
FFL	FINISHED FLOOR LEVEL
FGL	FINISHED GROUND LEVEL
FNC	FENCE
LB	LINEABOARD CLADDING
NGL	NATURAL GROUND LINE
OH	OVERHANG
RB	RENDERED BLUEBOARD
RM	RENDERED MASONRY
SC	SHADOWCLAD CLADDING
SIF	STONE INLAY FEATURE
TOW	TOP OF WALL
WH	WINDOW HEAD
WL	WALL LIGHT

WINDOW ABBREVIATIONS

AAW	ALUM. FRAMED AWNING WINDOW
ABD	ALUM. FRAMED BIFOLD STACKER DOOR
ABW	ALUM. FRAMED BIFOLD STACKER WINDOW
ACD	ALUM. FRAMED CASEMENT DOOR
ACW	ALUM. FRAMED CASEMENT WINDOW
ADH	ALUM. FRAMED DOUBLE HUNG WINDOW
AFD	ALUM. FRAMED FRENCH DOORS
AFG	ALUM. FRAMED FIXED GLAZING
ALV	ALUM. FRAMED LOUVRE WINDOW
ASD	ALUM. FRAMED SLIDING DOOR
ASH	ALUM.FRAMED SINGLE HUNG WINDOW
ASW	ALUM. FRAMED SLIDING WINDOW
CL	CLEAR GLAZING
OBS	OBSCURE GLAZING
SB	SOLAR BLOCK GLAZING
T	TINTED GLAZING

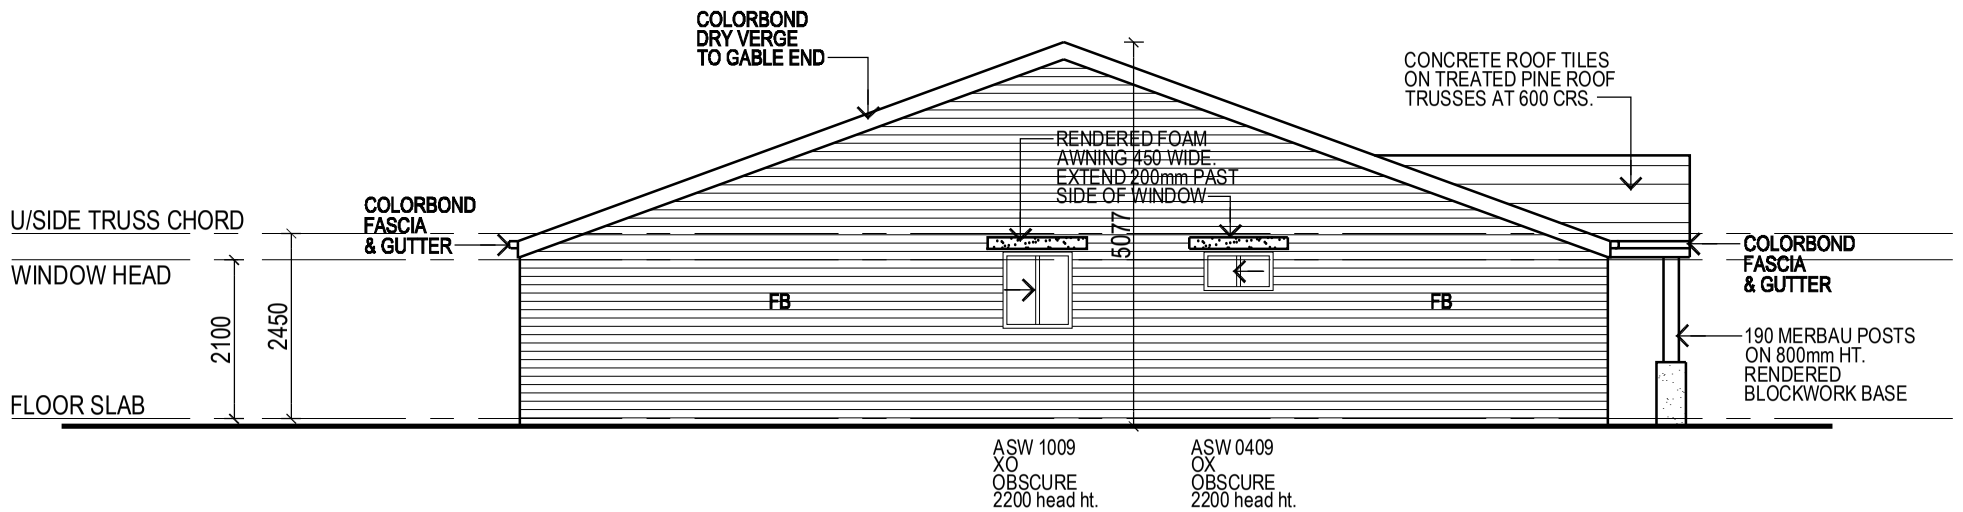

- ELEVATION 4

VILLAS 149 & 150 1:100

ISSUE	DATE	DESCRIPTION
A	01/04/26	ISSUED FOR APPROVALS

© COPYRIGHT NOTICE
Copyright of this drawing and design is held permanently by Carma Building Group Pty Ltd. Unauthorised use of this drawing and / or design, or any variation thereof, will trigger immediate legal proceedings.

carma building group
Suite 2 / 199 Gympie Tce, Noosaville Q 45(
T 07 5447 1250 F 07 5470 2586
E admin@carmabuildinggroup.com.au

PROJECT
VILLAS 149 & 150
LAGUNA ESTATE
21 LAKE WEYBA DRIVE
NOOSAVILLE

CLIENT
LAGUNA RETIREMENT ESTATE

DRAWING TITLE
ELEVATIONS
Sheet 2 of 2

SCALE	@ ORIGINAL SIZ
1:100	A
DATE	DRAW
APRIL 2026	MW

DRAWING STATUS
FOR CONSTRUCTION

DRAWING NO.	ISSU
LRV149 WD-07	A


ELEVATIONS & SECTIONS ABBREVIATIONS & LEGEND

GENERAL ABBREVIATIONS


AC	AXON CLADDING
AWN	AWNING (PROJECTION NOTED)
BAL	BALUSTRADE
CH	CEILING HEIGHT
FB	FACE BRICKWORK
FFL	FINISHED FLOOR LEVEL
FGL	FINISHED GROUND LEVEL
FNC	FENCE
LB	LINEABOARD CLADDING
NGL	NATURAL GROUND LINE
OH	OVERHANG
RB	RENDERED BLUEBOARD
RM	RENDERED MASONRY
SC	SHADOWCLAD CLADDING
SIF	STONE INLAY FEATURE
TOW	TOP OF WALL
WH	WINDOW HEAD
WL	WALL LIGHT

WINDOW ABBREVIATIONS


AAW	ALUM. FRAMED AWNING WINDOW
ABD	ALUM. FRAMED BIFOLD STACKER DOOR
ABW	ALUM. FRAMED BIFOLD STACKER WINDOW
ACD	ALUM. FRAMED CASEMENT DOOR
ACW	ALUM. FRAMED CASEMENT WINDOW
ADH	ALUM. FRAMED DOUBLE HUNG WINDOW
AFD	ALUM. FRAMED FRENCH DOORS
AFG	ALUM. FRAMED FIXED GLAZING
ALV	ALUM. FRAMED LOUVRE WINDOW
ASD	ALUM. FRAMED SLIDING DOOR
ASH	ALUM.FRAMED SINGLE HUNG WINDOW
ASW	ALUM. FRAMED SLIDING WINDOW
CL	CLEAR GLAZING
OBS	OBSCURE GLAZING
SB	SOLAR BLOCK GLAZING
T	TINTED GLAZING

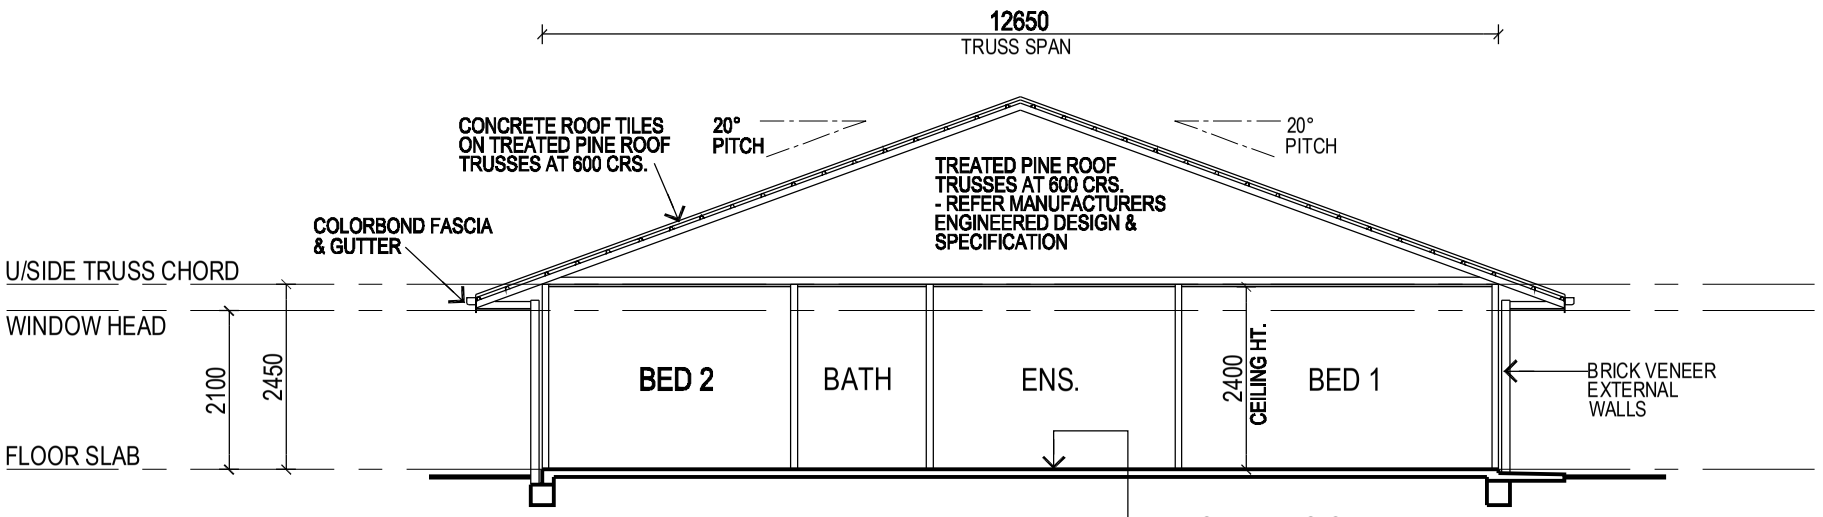


- SECTION 1
VILLAS 149 & 150 1:100

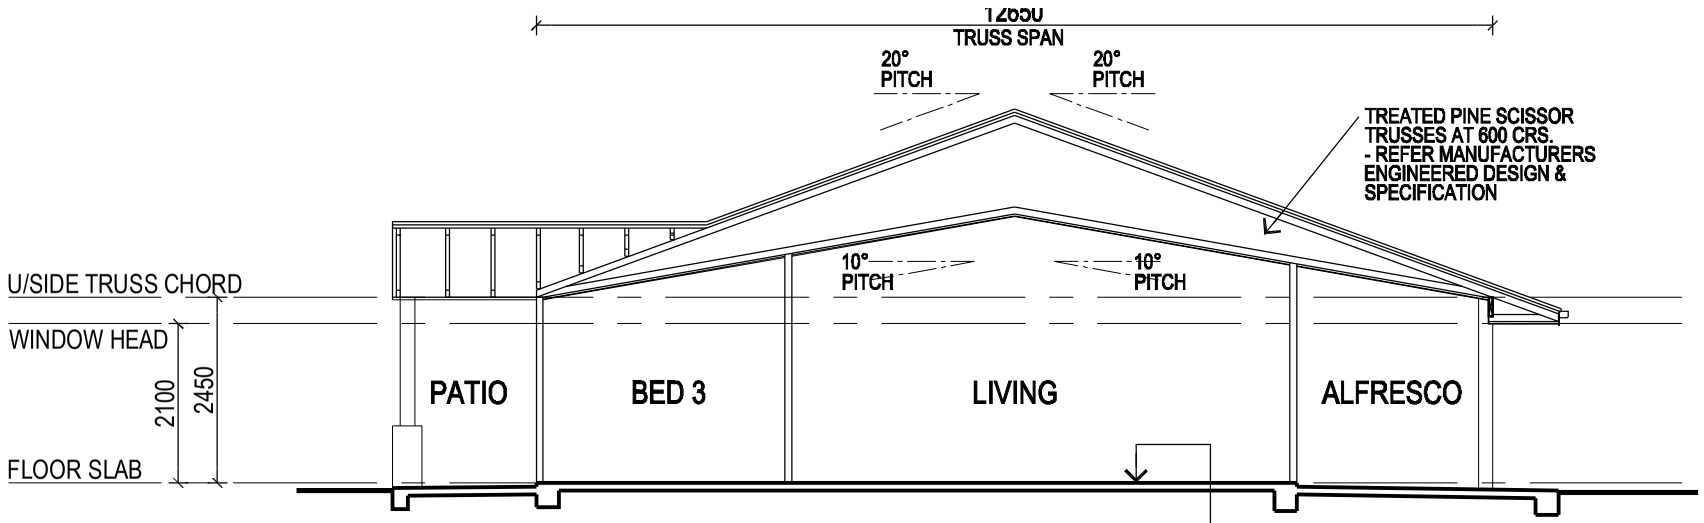

- SECTION 2
VILLAS 149 & 150 1:100

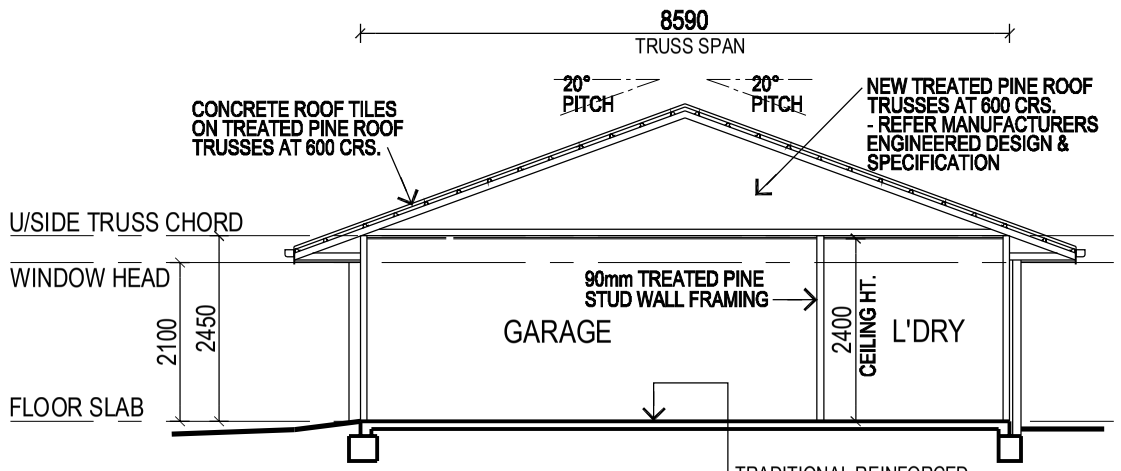

- SECTION 3
VILLAS 149 & 150 1:100

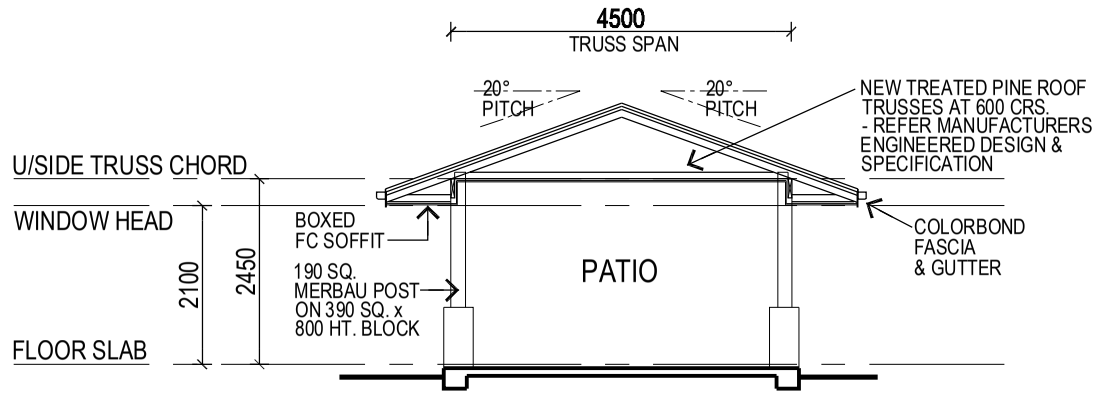

- SECTION 4
VILLAS 149 & 150 1:100

ISSUE	DATE	DESCRIPTION
A	01/04/26	ISSUED FOR APPROVALS

© COPYRIGHT NOTICE
Copyright of this drawing and design is held permanently by Carma Building Group Pty Ltd. Unauthorised use of this drawing and / or design, or any variation thereof, will trigger immediate legal proceedings.

carma building group
Suite 2 / 199 Gympie Tce, Noosaville Q 45
T 07 5447 1250 F 07 5470 2586
E admin@carmabuildinggroup.com.au

PROJECT
VILLAS 149 & 150
LAGUNA ESTATE
21 LAKE WEYBA DRIVE
NOOSAVILLE

CLIENT
LAGUNA RETIREMENT ESTATE

DRAWING TITLE
SECTIONS


SCALE	@ ORIGINAL SIZ
1:100	A
DATE	DRAW
APRIL 2026	M\

DRAWING STATUS
FOR CONSTRUCTION

DRAWING NO.	ISSU
LRV149 WD-08	A


INTERIOR ELEVATIONS ABBREVIATIONS & LEGEND

AP	APPLIANCE CUPBD. ROLLER SHUTTER
AR	ARCHITRAVE
BH	BULKHEAD
BN	BENCHTOP
BR	BROOM CUPBOARD
BSP	BATH SPOUT
BTH	BATH TUB
CD	CLOTHES DRYER
CO	CORNICE
CT	COOKTOP
DR	DRAWER
DV	DUCTED VACUUM INLET
DW	DISHWASHER
FR	FRIDGE RECESS
FT	FEATURE TILE
FW	FLOOR WASTE
GR	GRAB RAIL
GPO	GENERAL POWER OUTLET (DOUBLE)
KB	KICKBOARD
L	LINEN CUPBOARD
LAM	PLASTIC LAMINATE FINISH
MIR	MIRROR
MR	MICROWAVE RECESS
MXR	MIXER TAP
OH	OVERHEAD CUPBOARD
PB	PLASTERBOARD BULKHEAD
PL	PLASTERBOARD FINISH
PN	PANTRY
RBH	ROBE HOOK
RH	RANGEHOOD
SB	SHOWER BASKET
SCR	SHOWER SCREEN
SH	SHELF / SHELVES
SHR	SHOWER
SK	SKIRTING BOARD
SNK	SINK
SP	SPLASHBACK
SR	SHOWER ROSE
SRD	SLIDING ROBE DOORS
SSH	SHOWER SHELF
T	LAUNDRY TUB
TBS	TOILET BRUSH SET
TRG	TOWEL RING
TRH	TOILET ROLL HOLDER
TS	TOILET SUITE
TWL	TOWEL RAIL
VAN	VANITY BENCH
VB	VANITY BASIN
WM	WASHING MACHINE SPACE
WMT	WASHING MACHINE TAPS
WO	WALL OVEN
WR	WINE RACKS
WT	WALL TILES

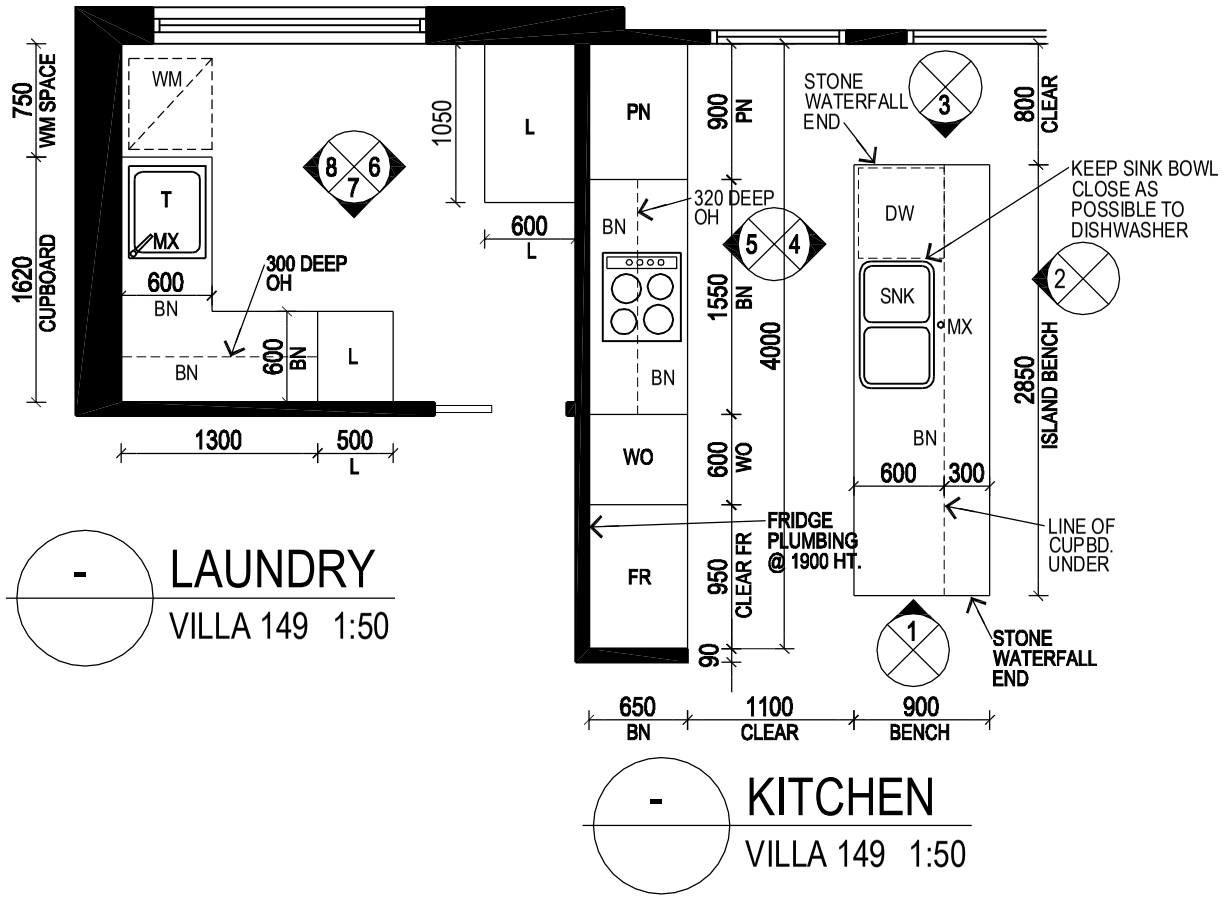


- LAUNDRY
VILLA 149 1:50


- KITCHEN
VILLA 149 1:50

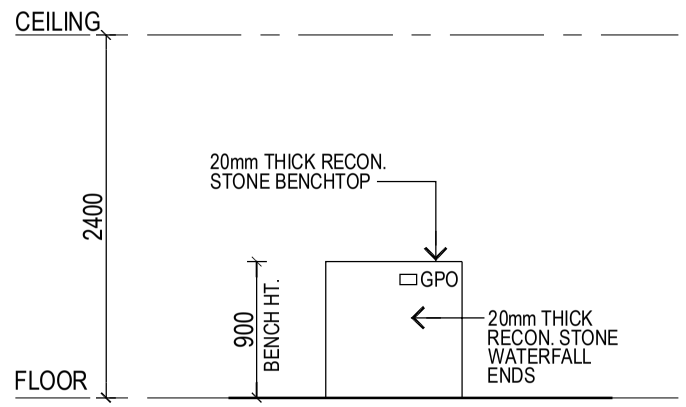

- ELEVATION 1
KITCHEN - V149 1:50

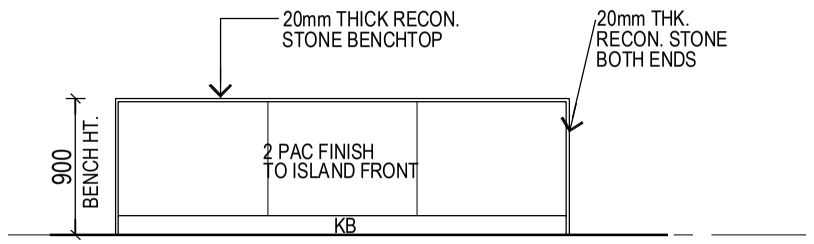


- ELEVATION 2
KITCHEN - V149 1:50

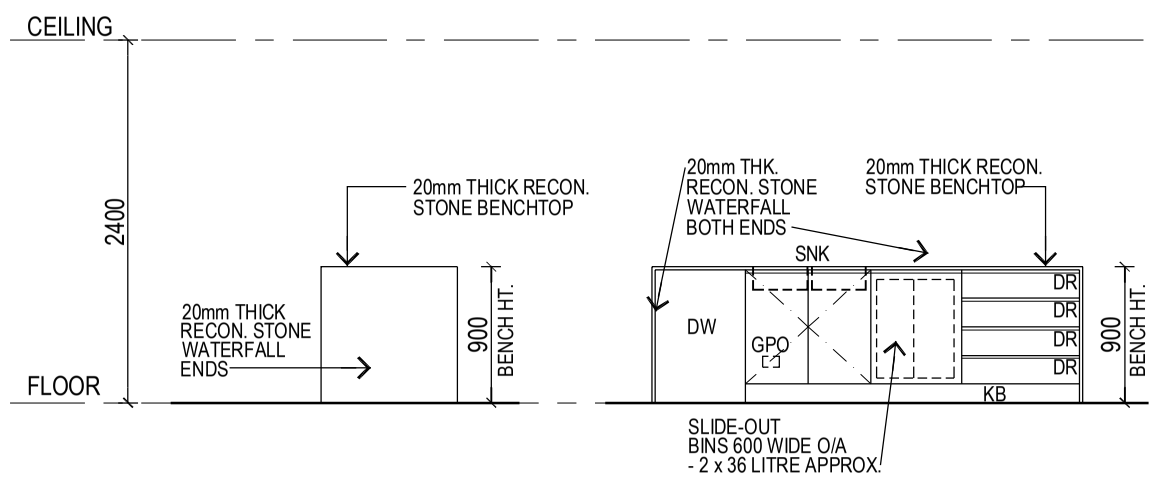

- ELEVATION 3
KITCHEN - V149 1:50

- ELEVATION 4
KITCHEN - V149 1:50

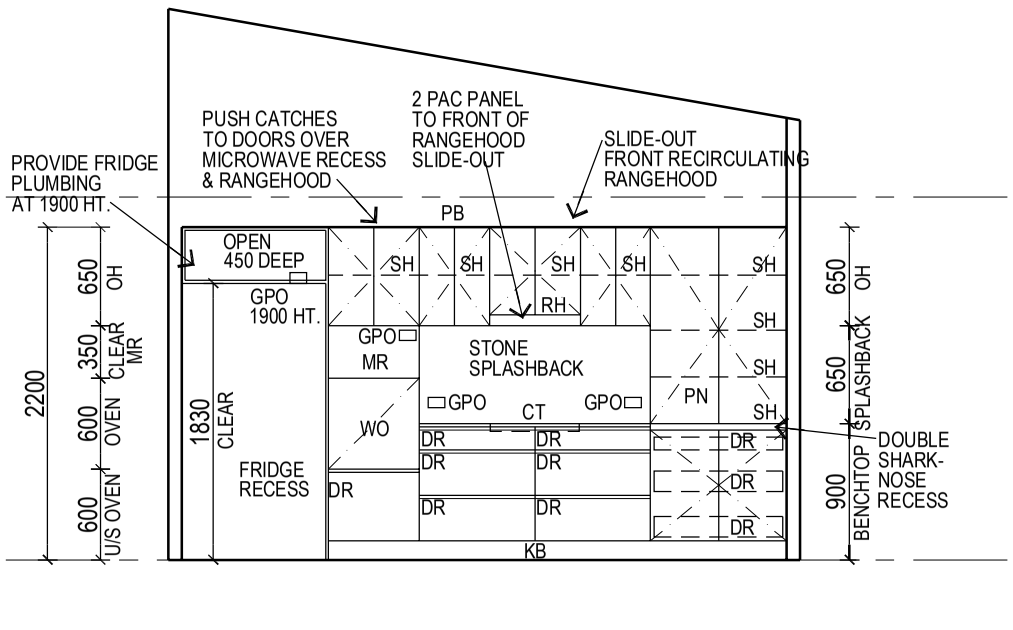

- ELEVATION 5
KITCHEN - V149 1:50

ISSUE	DATE	DESCRIPTION
A	01/07/26	ISSUED FOR CONSTRUCTION

© COPYRIGHT NOTICE
Copyright of this drawing and design is held permanently by Carma Building Group Pty Ltd. Unauthorised use of this drawing and / or design, or any variation thereof, will trigger immediate legal proceedings.

carma
building group
Suite 2 / 199 Gympie Tce, Noosaville Q 456
T 07 5447 1250 F 07 5470 2586
E admin@carmabuildinggroup.com.au

PROJECT
VILLAS 149 & 150
LAGUNA ESTATE
21 LAKE WEYBA DRIVE
NOOSAVILLE


CLIENT
LAGUNA RETIREMENT ESTATE

DRAWING TITLE
VILLA 149 -
KITCHEN &
LAUNDRY DETAILS

SCALE	@ ORIGINAL SIZ
1:50	A3
DATE	DRAW
JULY 2026	MW

DRAWING STATUS
FOR CONSTRUCTION

DRAWING NO.	ISSU
LRV149 WD-10	A

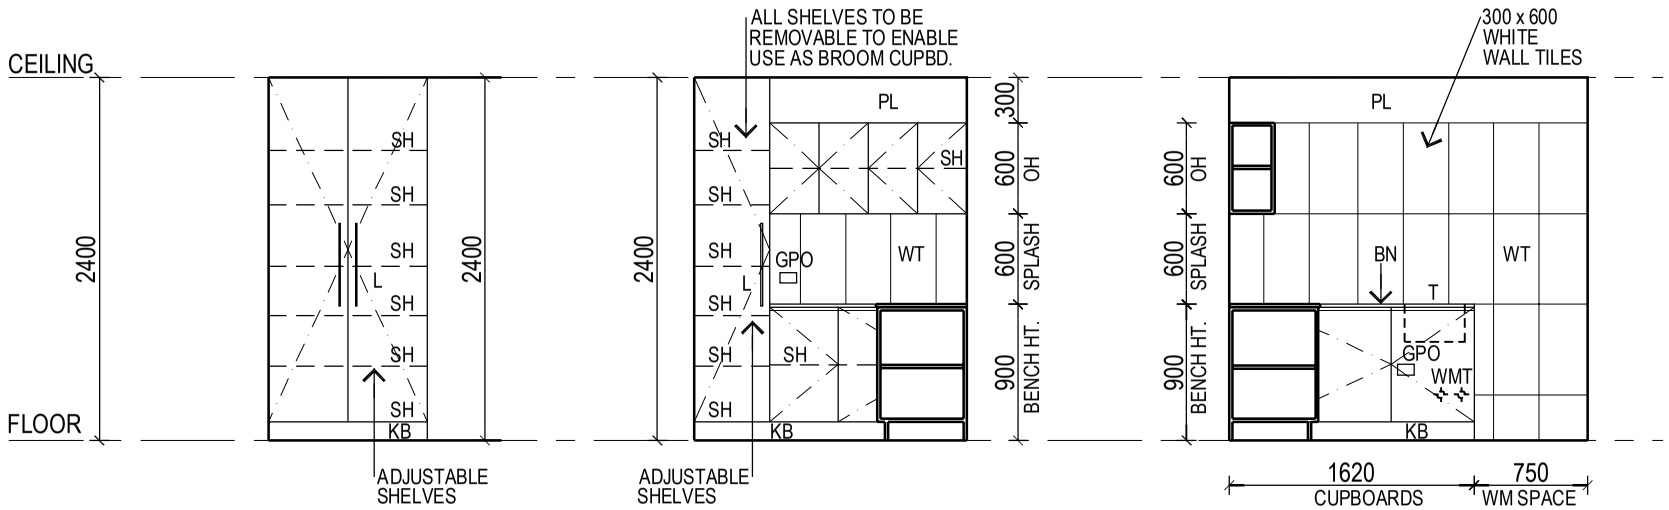


- ELEVATION 6
LAUNDRY - V149 1:50

- ELEVATION 7
LAUNDRY - V149 1:50

- ELEVATION 8
LAUNDRY - V149 1:50

- W.I. ROBE
VILLA 149 1:50


- ENSUITE
VILLA 149 1:50

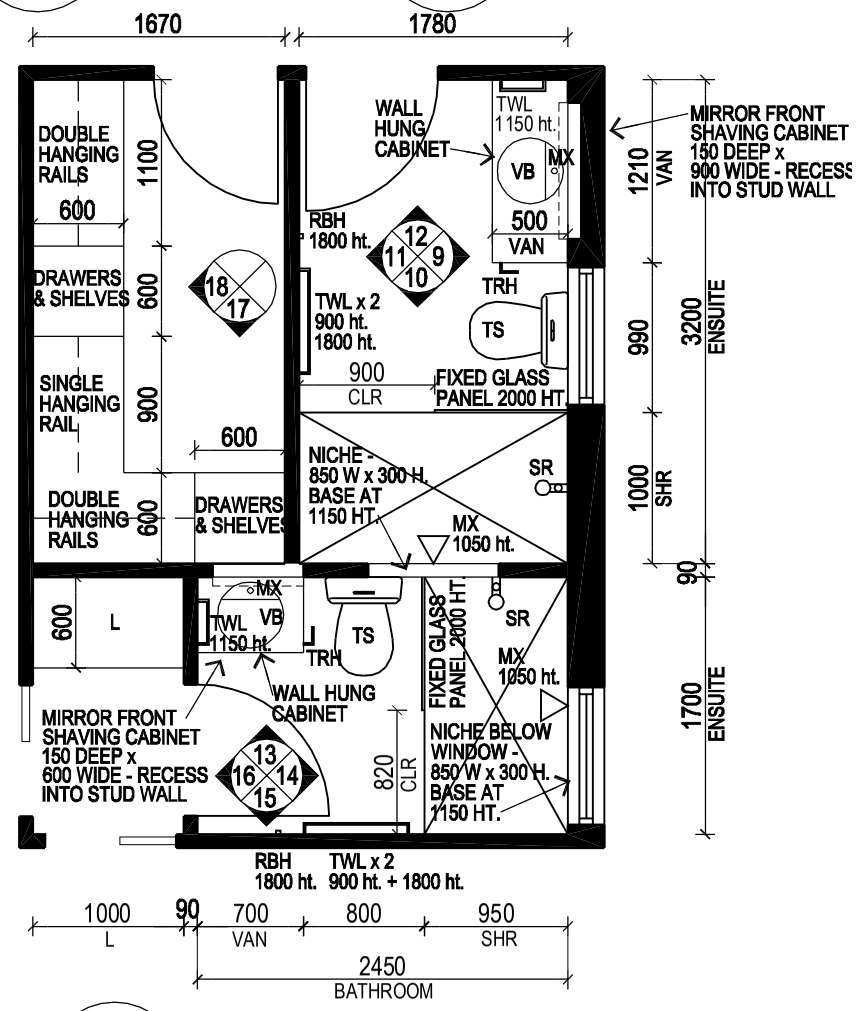

- BATHROOM
VILLA 149 1:50

INTERIOR ELEVATIONS ABBREVIATIONS & LEGEND

AP	APPLIANCE CUPBD. ROLLER SHUTTER
AR	ARCHITRAVE
BH	BULKHEAD
BN	BENCHTOP
BR	BROOM CUPBOARD
BSP	BATH SPOUT
BTH	BATH TUB
CD	CLOTHES DRYER
CO	CORNICE
CT	COOKTOP
DR	DRAWER
DV	DUCTED VACUUM INLET
DW	DISHWASHER
FR	FRIDGE RECESS
FT	FEATURE TILE
FW	FLOOR WASTE
GR	GRAB RAIL
GPO	GENERAL POWER OUTLET (DOUBLE)
KB	KICKBOARD
L	LINEN CUPBOARD
LAM	PLASTIC LAMINATE FINISH
MIR	MIRROR
MR	MICROWAVE RECESS
MXR	MIXER TAP
OH	OVERHEAD CUPBOARD
PB	PLASTERBOARD BULKHEAD
PL	PLASTERBOARD FINISH
PN	PANTRY
RBH	ROBE HOOK
RH	RANGEHOOD
SB	SHOWER BASKET
SCR	SHOWER SCREEN
SH	SHELF / SHELVES
SHR	SHOWER
SK	SKIRTING BOARD
SNK	SINK
SP	SPLASHBACK
SR	SHOWER ROSE
SRD	SLIDING ROBE DOORS
SSH	SHOWER SHELF
T	LAUNDRY TUB
TBS	TOILET BRUSH SET
TRG	TOWEL RING
TRH	TOILET ROLL HOLDER
TS	TOILET SUITE
TWL	TOWEL RAIL
VAN	VANITY BENCH
VB	VANITY BASIN
WM	WASHING MACHINE SPACE
WMT	WASHING MACHINE TAPS
WO	WALL OVEN
WR	WINE RACKS
WT	WALL TILES

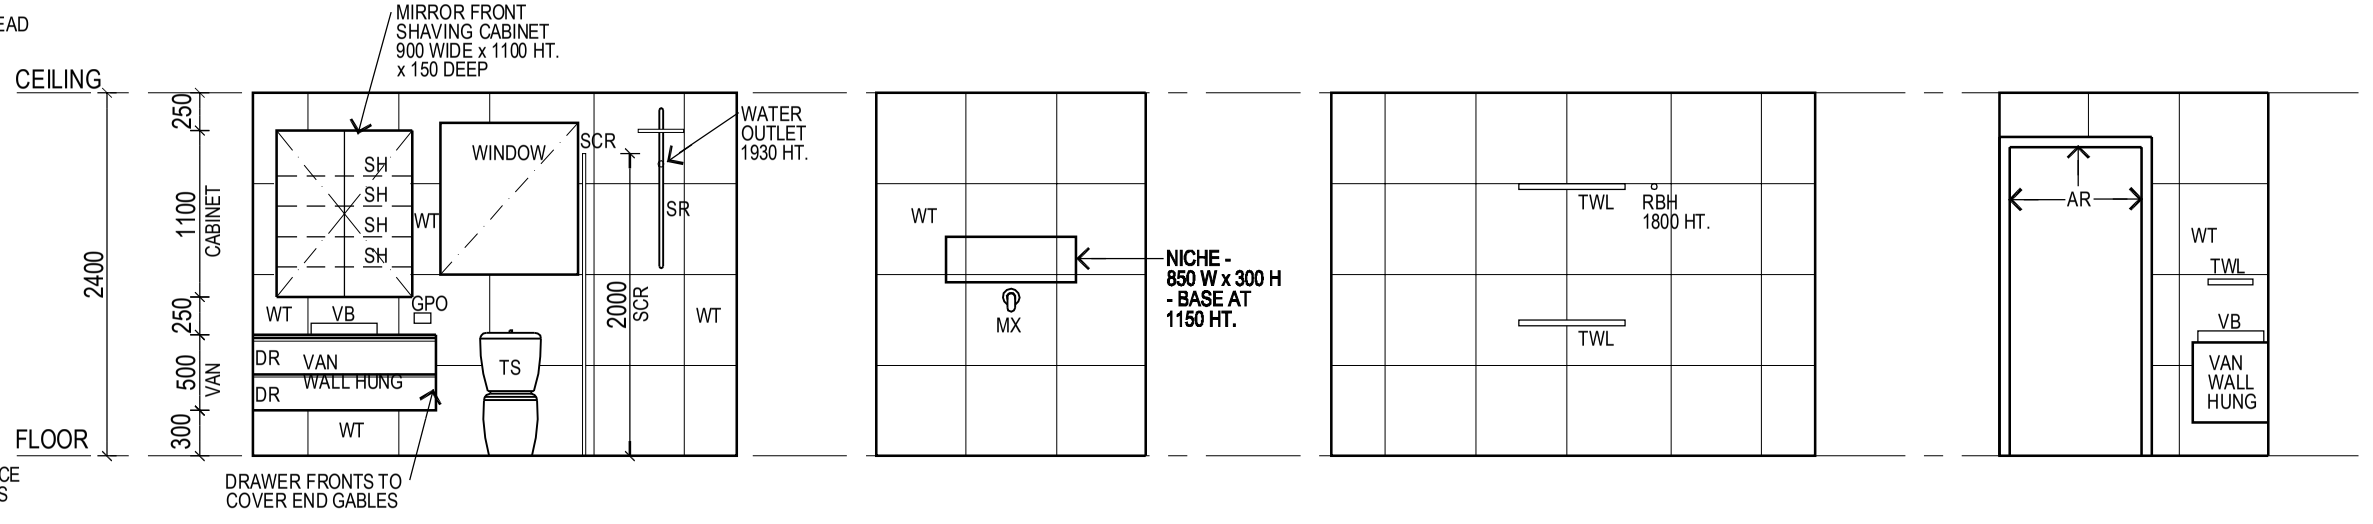

- ELEVATION 9
ENSUITE - V149 1:50

- ELEVATION 10
ENSUITE - V149 1:50

- ELEVATION 11
ENSUITE - V149 1:50

- ELEVATION 12
ENSUITE - V149 1:50

ISSUE	DATE	DESCRIPTION
A	01/07/26	ISSUED FOR CONSTRUCTION

© COPYRIGHT NOTICE
Copyright of this drawing and design is held permanently by Carma Building Group Pty Ltd. Unauthorised use of this drawing and / or design, or any variation thereof, will trigger immediate legal proceedings.

carma building group
Suite 2 / 199 Gympie Tce, Noosaville Q 45
T 07 5447 1250 F 07 5470 2586
E admin@carmabuildinggroup.com.au

PROJECT
VILLAS 149 & 150
LAGUNA ESTATE
21 LAKE WEYBA DRIVE
NOOSAVILLE

CLIENT
LAGUNA RETIREMENT ESTATE


DRAWING TITLE
VILLA 149 - LAUNDRY, BATHROOM, ENSUITE & W.I. ROBE DETAILS

SCALE @ ORIGINAL SIZ
1:50 A3

DATE DRAW
JULY 2026 MW

DRAWING STATUS
FOR CONSTRUCTION

DRAWING NO. ISSU
LRV149 WD-11 A

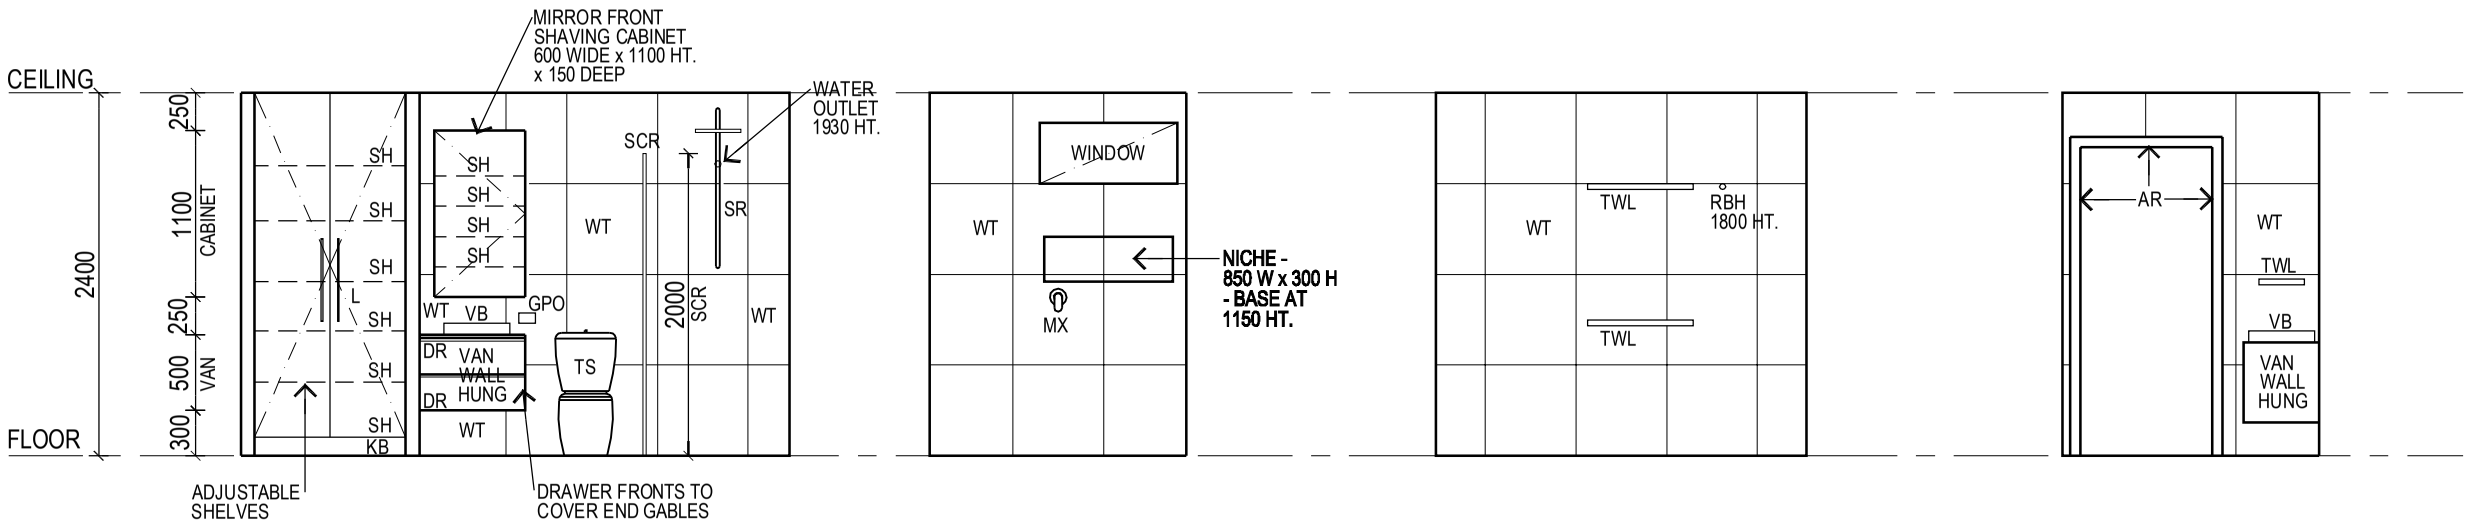


- ELEVATION 13
BATHROOM - V149 1:50


- ELEVATION 14
BATHROOM - V149 1:50

- ELEVATION 15
BATHROOM - V149 1:50

- ELEVATION 16
BATHROOM - V149 1:50

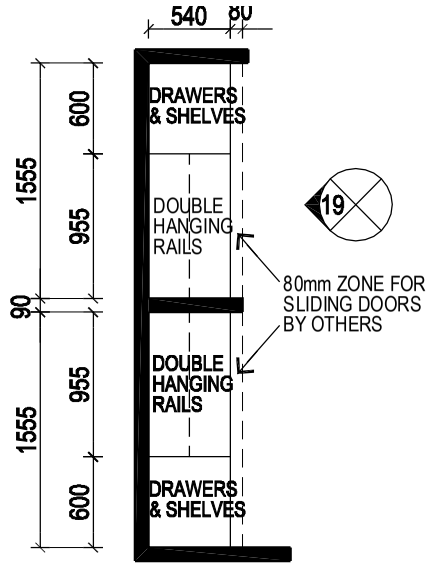


- BED 2 ROBE
VILLA 149 1:50

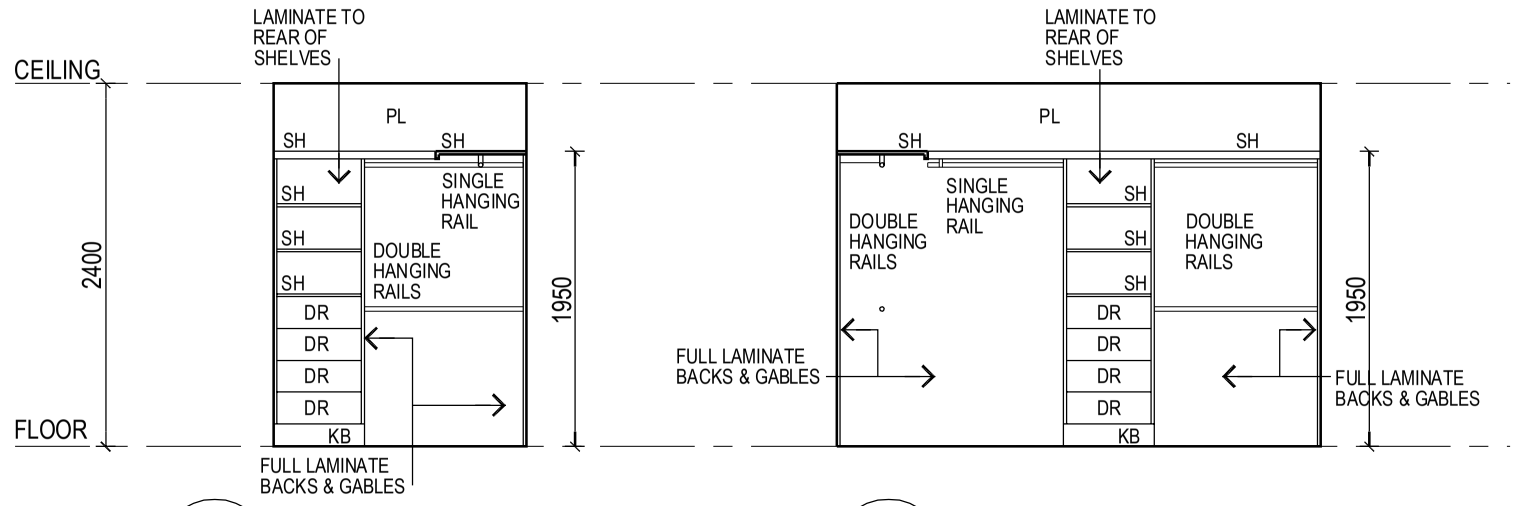


- ELEVATION 17
BED 1 W.I.R. - V149 1:50

- ELEVATION 18
BED 1 W.I.R. - V149 1:50

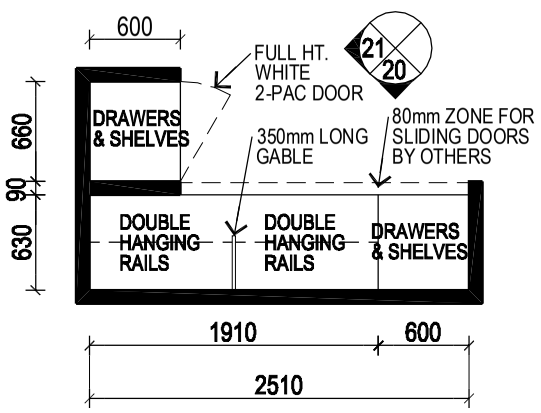

- BED 3 ROBE
VILLA 149 1:50

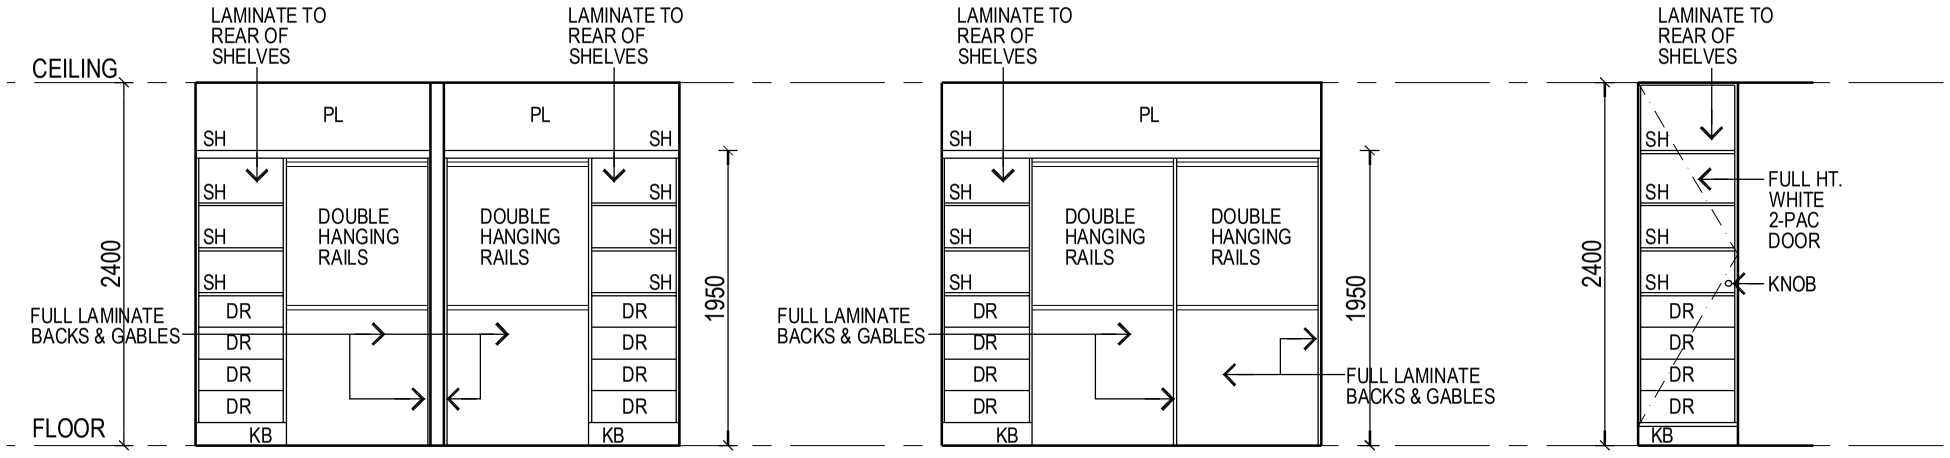

- ELEVATION 19
BED 2 ROBE - V149 1:50

- ELEVATION 20
BED 3 ROBE - V149 1:50

- ELEVATION 21
BED 3 ROBE - V149 1:50

ISSUE	DATE	DESCRIPTION
A	01/07/26	ISSUED FOR CONSTRUCTION

© COPYRIGHT NOTICE
Copyright of this drawing and design is held permanently by Carma Building Group Pty Ltd. Unauthorised use of this drawing and / or design, or any variation thereof, will trigger immediate legal proceedings.

carma building group
Suite 2 / 199 Gympie Tce, Noosaville Q 456
T 07 5447 1250 F 07 5470 2586
E admin@carmabuildinggroup.com.au

PROJECT
VILLAS 149 & 150
LAGUNA ESTATE
21 LAKE WEYBA DRIVE
NOOSAVILLE

CLIENT
LAGUNA RETIREMENT ESTATE

DRAWING TITLE
VILLA 149 - BATHROOM & ROBE DETAILS


SCALE	@ ORIGINAL SIZ
1:50	A3
DATE	DRAW
JULY 2026	MW

DRAWING STATUS
FOR CONSTRUCTION

DRAWING NO.	ISSU
LRV149 WD-12	A

INTERIOR ELEVATIONS ABBREVIATIONS & LEGEND


AP	APPLIANCE CUPBD. ROLLER SHUTTER
AR	ARCHITRAVE
BH	BULKHEAD
BN	BENCHTOP
BR	BROOM CUPBOARD
BSP	BATH SPOUT
BTH	BATH TUB
CD	CLOTHES DRYER
CO	CORNICE
CT	COOKTOP
DR	DRAWER
DV	DUCTED VACUUM INLET
DW	DISHWASHER
FR	FRIDGE RECESS
FT	FEATURE TILE
FW	FLOOR WASTE
GR	GRAB RAIL
GPO	GENERAL POWER OUTLET (DOUBLE)
KB	KICKBOARD
L	LINEN CUPBOARD
LAM	PLASTIC LAMINATE FINISH
MIR	MIRROR
MR	MICROWAVE RECESS
MXR	MIXER TAP
OH	OVERHEAD CUPBOARD
PB	PLASTERBOARD BULKHEAD
PL	PLASTERBOARD FINISH
PN	PANTRY
RBH	ROBE HOOK
RH	RANGEHOOD
SB	SHOWER BASKET
SCR	SHOWER SCREEN
SH	SHELF / SHELVES
SHR	SHOWER
SK	SKIRTING BOARD
SNK	SINK
SP	SPLASHBACK
SR	SHOWER ROSE
SRD	SLIDING ROBE DOORS
SSH	SHOWER SHELF
T	LAUNDRY TUB
TBS	TOILET BRUSH SET
TRG	TOWEL RING
TRH	TOILET ROLL HOLDER
TS	TOILET SUITE
TWL	TOWEL RAIL
VAN	VANITY BENCH
VB	VANITY BASIN
WM	WASHING MACHINE SPACE
WMT	WASHING MACHINE TAPS
WO	WALL OVEN
WR	WINE RACKS
WT	WALL TILES

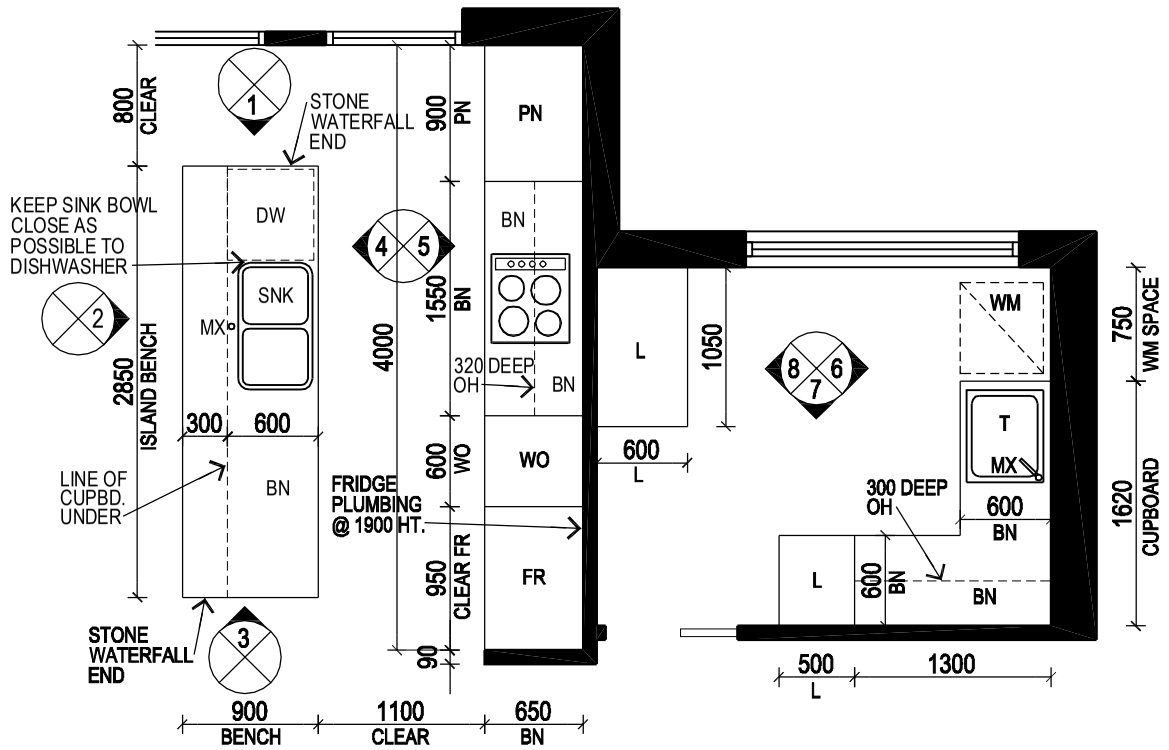


- KITCHEN
VILLA 150 1:50




- LAUNDRY
VILLA 150 1:50

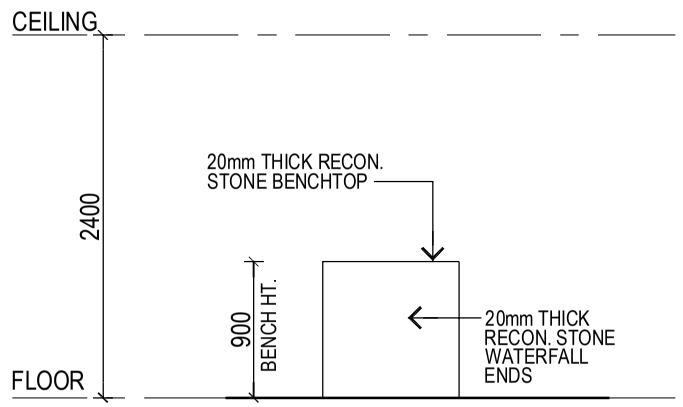


- ELEVATION 1
KITCHEN - V150 1:50

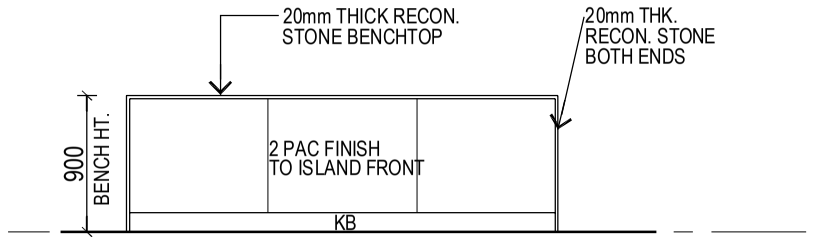


- ELEVATION 2
KITCHEN - V150 1:50

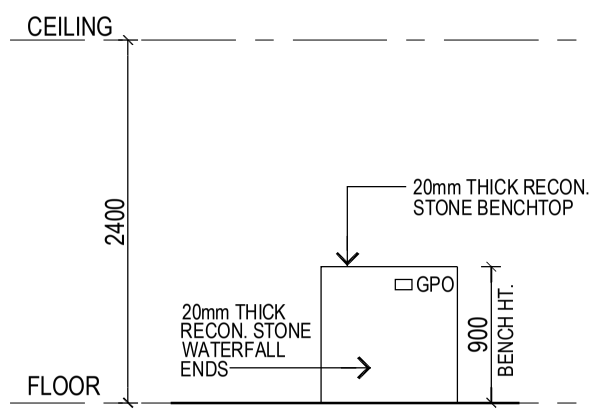

- ELEVATION 3
KITCHEN - V150 1:50

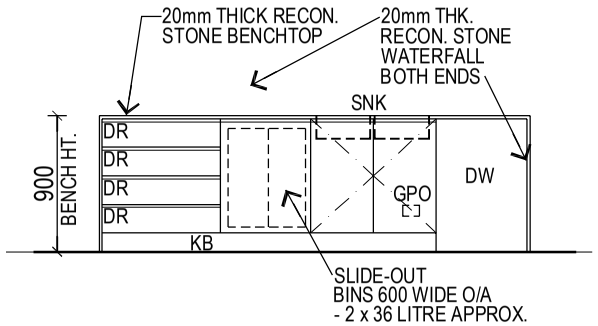

- ELEVATION 4
KITCHEN - V150 1:50

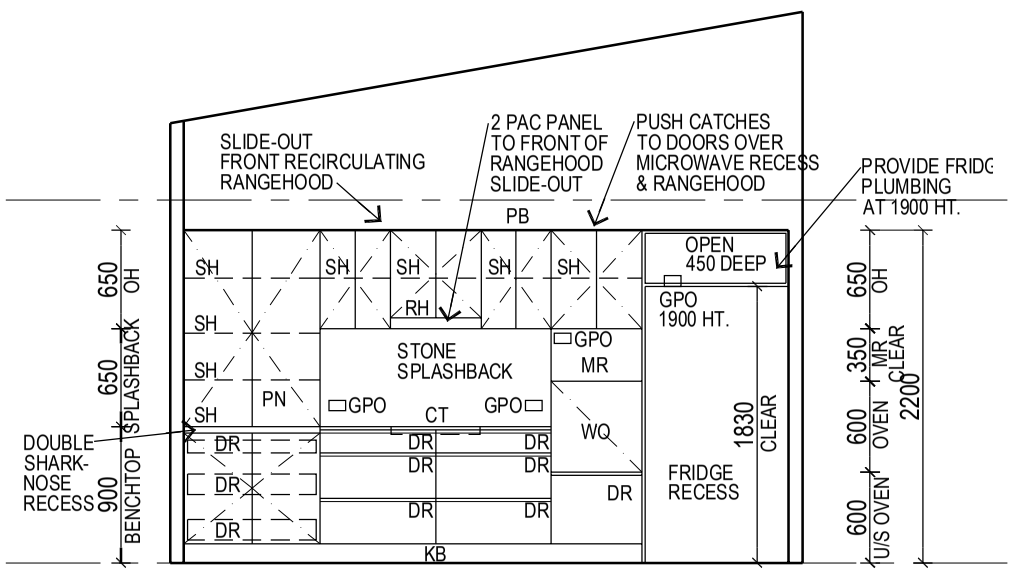

- ELEVATION 5
KITCHEN - V150 1:50

ISSUE	DATE	DESCRIPTION
A	01/07/26	ISSUED FOR CONSTRUCTION

© COPYRIGHT NOTICE
Copyright of this drawing and design is held permanently by Carma Building Group Pty Ltd. Unauthorised use of this drawing and / or design, or any variation thereof, will trigger immediate legal proceedings.

carma building group
Suite 2 / 199 Gympie Tce, Noosaville Q 45
T 07 5447 1250 F 07 5470 2586
E admin@carmabuildinggroup.com.au

PROJECT
VILLAS 149 & 150
LAGUNA ESTATE
21 LAKE WEYBA DRIVE
NOOSAVILLE


CLIENT
LAGUNA RETIREMENT ESTATE

DRAWING TITLE
VILLA 150 - KITCHEN & LAUNDRY DETAILS

SCALE	@ ORIGINAL SIZ
1:50	A3
DATE	DRAW
JULY 2026	MW

DRAWING STATUS
FOR CONSTRUCTION

DRAWING NO.	ISSU
LRV149 WD-13	A

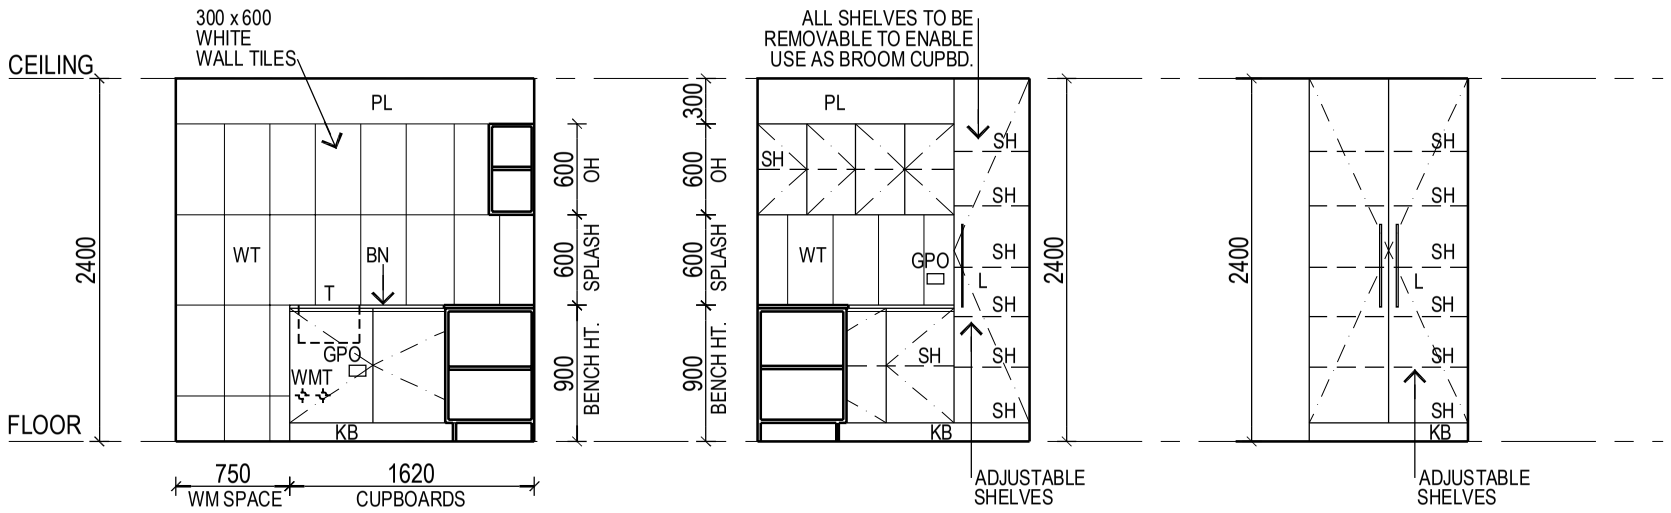


- ELEVATION 6
LAUNDRY - V150 1:50

- ELEVATION 7
LAUNDRY - V150 1:50

- ELEVATION 8
LAUNDRY - V150 1:50

- ENSUITE
VILLA 150 1:50

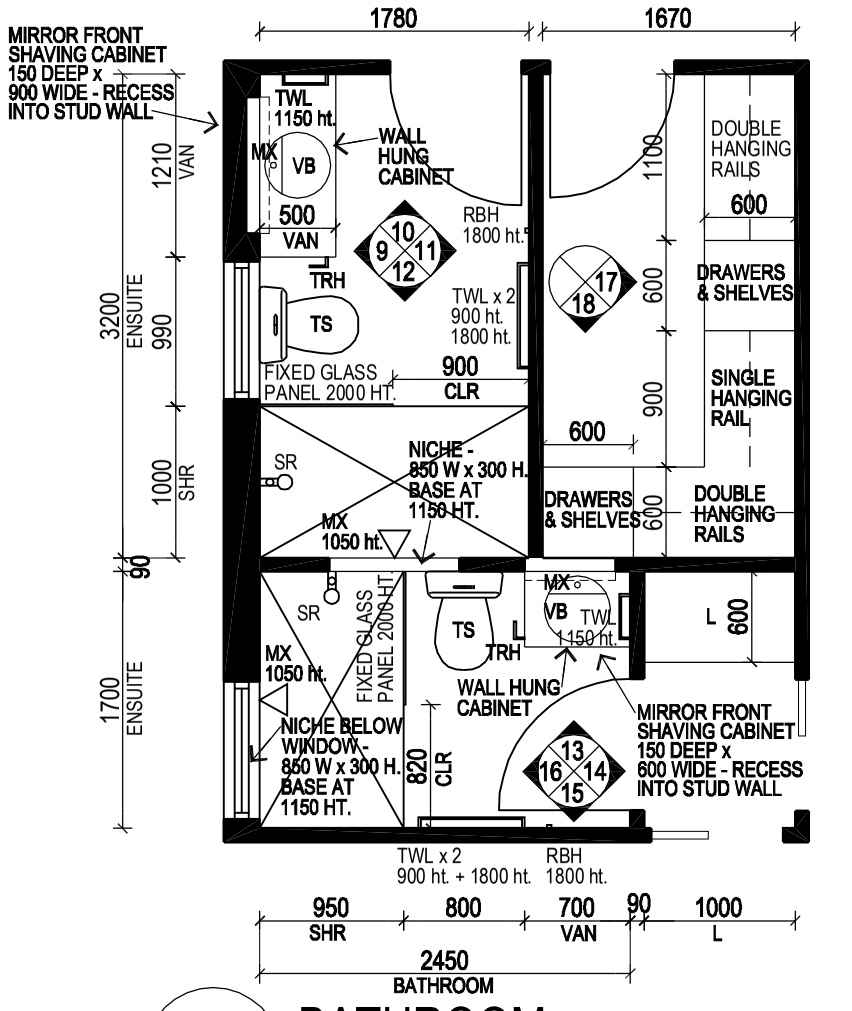


- BATHROOM
VILLA 150 1:50


- W.I. ROBE
VILLA 150 1:50

INTERIOR ELEVATIONS ABBREVIATIONS & LEGEND


AP	APPLIANCE CUPBD. ROLLER SHUTTER
AR	ARCHITRAVE
BH	BULKHEAD
BN	BENCHTOP
BR	BROOM CUPBOARD
BSP	BATH SPOUT
BTH	BATH TUB
CD	CLOTHES DRYER
CO	CORNICE
CT	COOKTOP
DR	DRAWER
DV	DUCTED VACUUM INLET
DW	DISHWASHER
FR	FRIDGE RECESS
FT	FEATURE TILE
FW	FLOOR WASTE
GR	GRAB RAIL
GPO	GENERAL POWER OUTLET (DOUBLE)
KB	KICKBOARD
L	LINEN CUPBOARD
LAM	PLASTIC LAMINATE FINISH
MIR	MIRROR
MR	MICROWAVE RECESS
MXR	MIXER TAP
OH	OVERHEAD CUPBOARD
PB	PLASTERBOARD BULKHEAD
PL	PLASTERBOARD FINISH
PN	PANTRY
RBH	ROBE HOOK
RH	RANGEHOOD
SB	SHOWER BASKET
SCR	SHOWER SCREEN
SH	SHELF / SHELVES
SHR	SHOWER
SK	SKIRTING BOARD
SNK	SINK
SP	SPLASHBACK
SR	SHOWER ROSE
SRD	SLIDING ROBE DOORS
SSH	SHOWER SHELF
T	LAUNDRY TUB
TBS	TOILET BRUSH SET
TRG	TOWEL RING
TRH	TOILET ROLL HOLDER
TS	TOILET SUITE
TWL	TOWEL RAIL
VAN	VANITY BENCH
VB	VANITY BASIN
WM	WASHING MACHINE SPACE
WMT	WASHING MACHINE TAPS
WO	WALL OVEN
WR	WINE RACKS
WT	WALL TILES

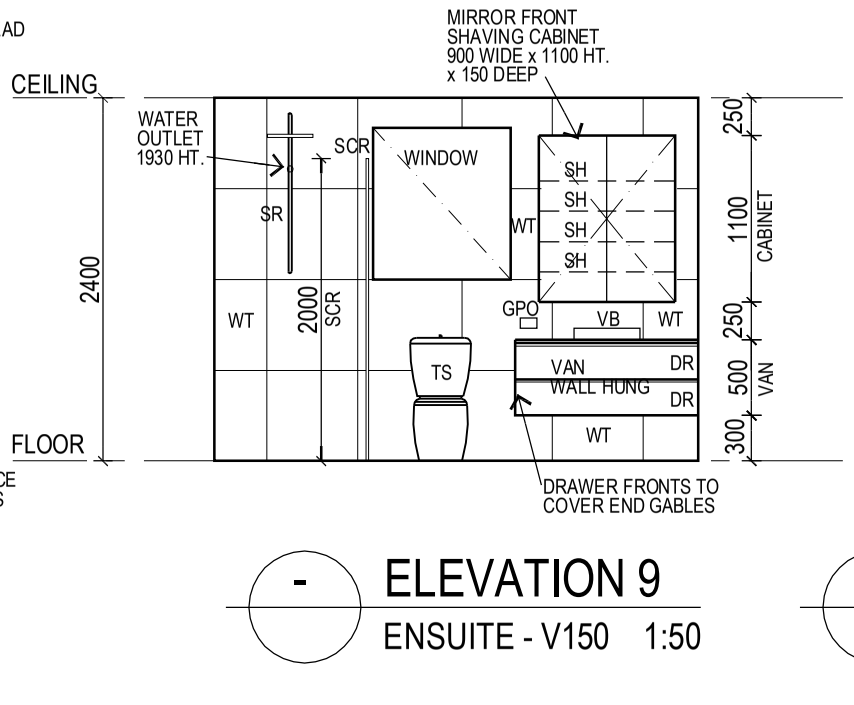


- ELEVATION 9
ENSUITE - V150 1:50

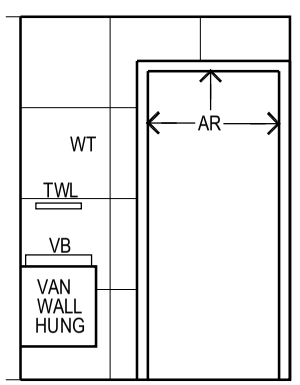

- ELEVATION 10
ENSUITE - V150 1:50

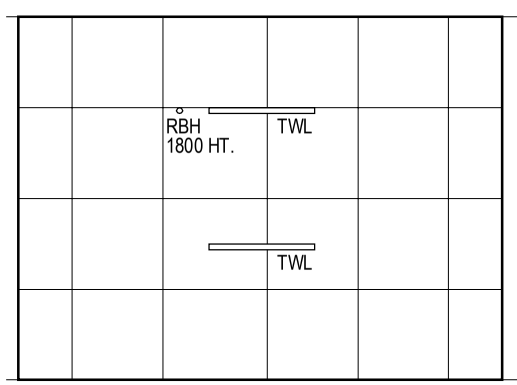

- ELEVATION 11
ENSUITE - V150 1:50

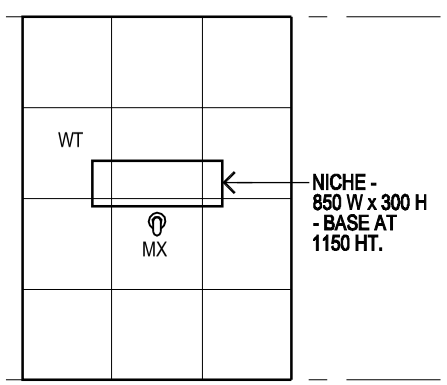

- ELEVATION 12
ENSUITE - V150 1:50

ISSUE	DATE	DESCRIPTION
A	01/07/26	ISSUED FOR CONSTRUCTION

© COPYRIGHT NOTICE
Copyright of this drawing and design is held permanently by Carma Building Group Pty Ltd. Unauthorised use of this drawing and / or design, or any variation thereof, will trigger immediate legal proceedings.

carma
building group
Suite 2 / 199 Gympie Tce, Noosaville Q 45
T 07 5447 1250 F 07 5470 2586
E admin@carmabuildinggroup.com.au

PROJECT
VILLAS 149 & 150
LAGUNA ESTATE
21 LAKE WEYBA DRIVE
NOOSAVILLE


CLIENT
LAGUNA RETIREMENT ESTATE

DRAWING TITLE
VILLA 150 -
LAUNDRY, BATHROOM, ENSUITE & W.I. ROBE DETAILS

SCALE	@ ORIGINAL SIZ
1:50	A3
DATE	DRAW
JULY 2026	MW

DRAWING STATUS
FOR CONSTRUCTION

DRAWING NO.	ISSU
LRV149 WD-14	A

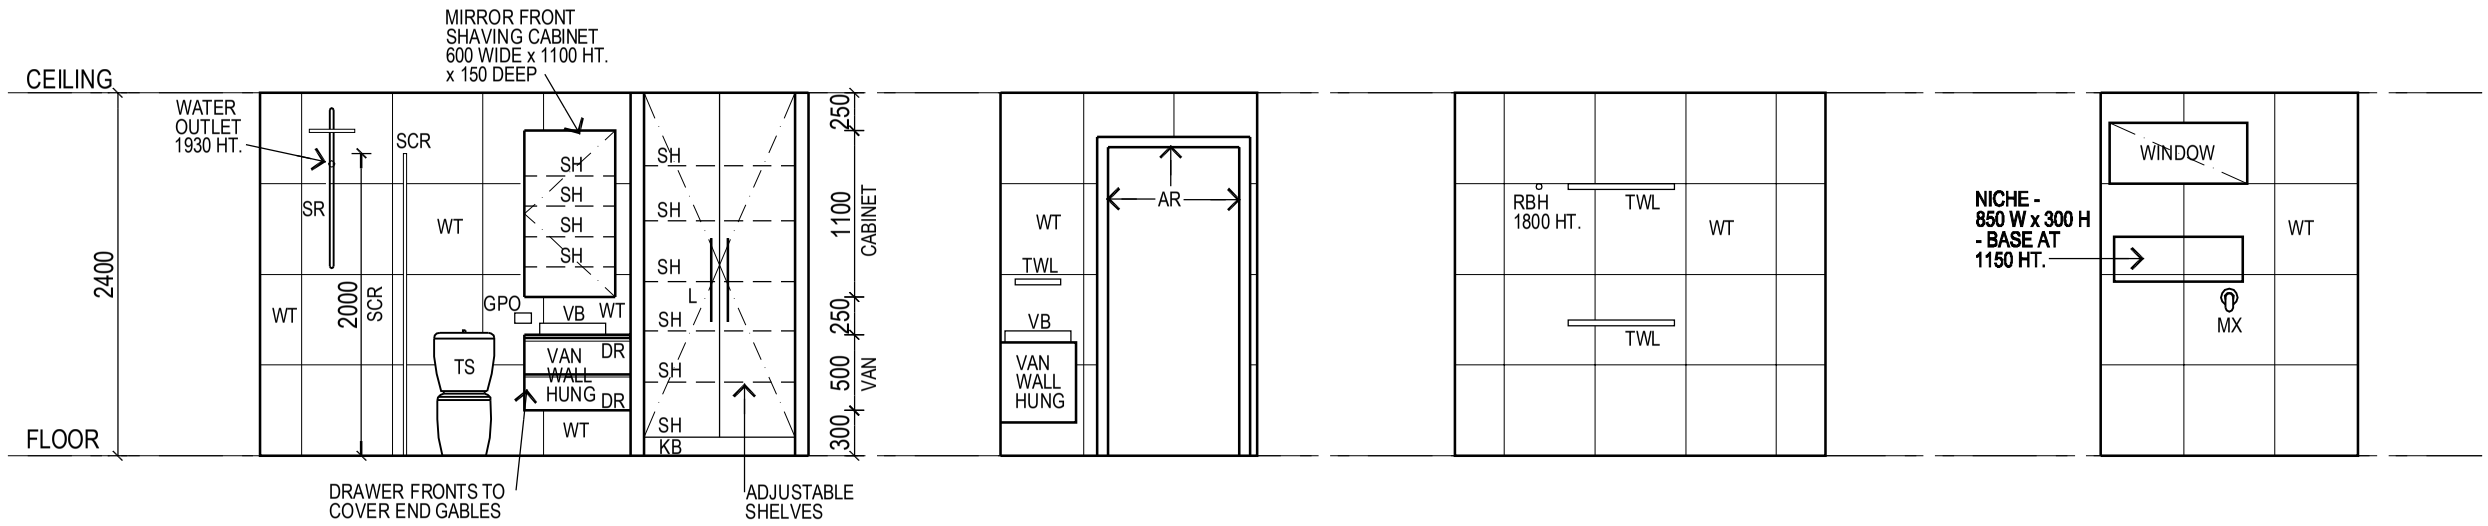


- ELEVATION 13
BATHROOM - V150 1:50


- ELEVATION 14
BATHROOM - V150 1:50

- ELEVATION 15
BATHROOM - V150 1:50


- ELEVATION 16
BATHROOM - V150 1:50

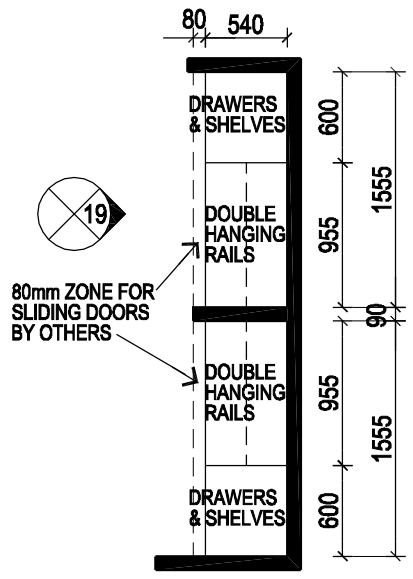

- BED 2 ROBE
VILLA 150 1:50

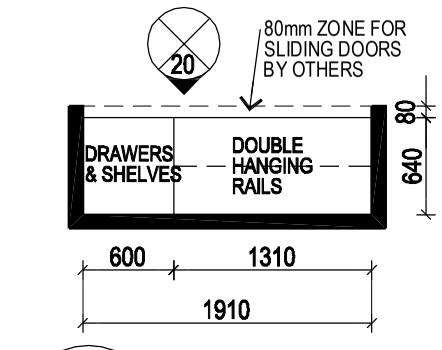


- BED 3 ROBE
VILLA 150 1:50

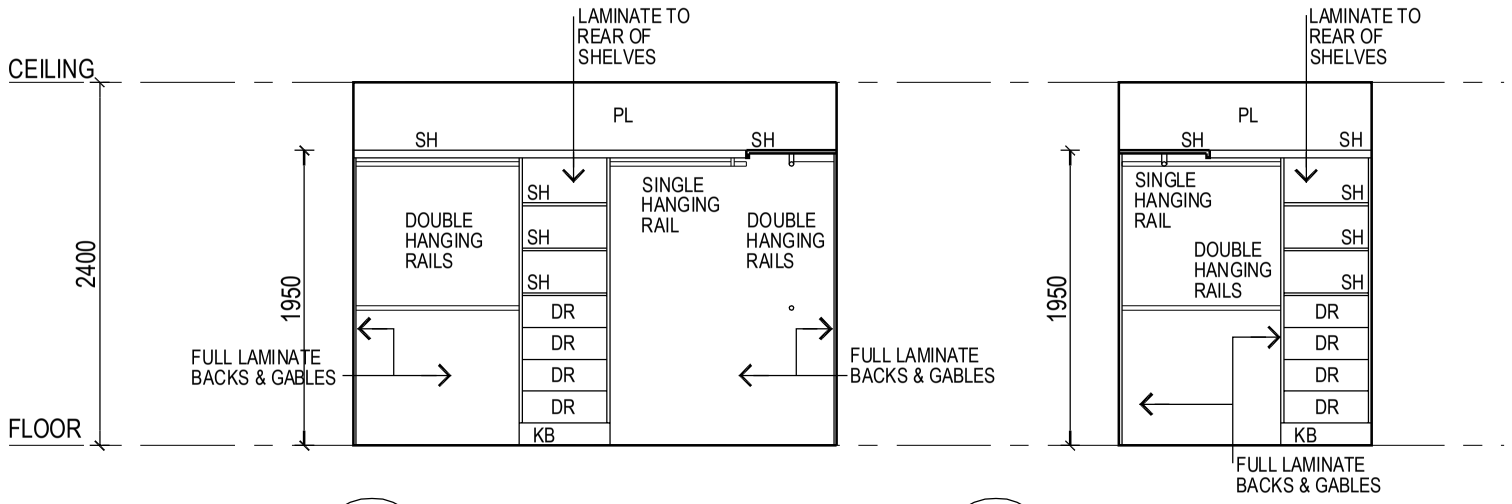

- ELEVATION 17
BED 1 W.I.R. - V150 1:50

- ELEVATION 18
BED 1 W.I.R. - V150 1:50

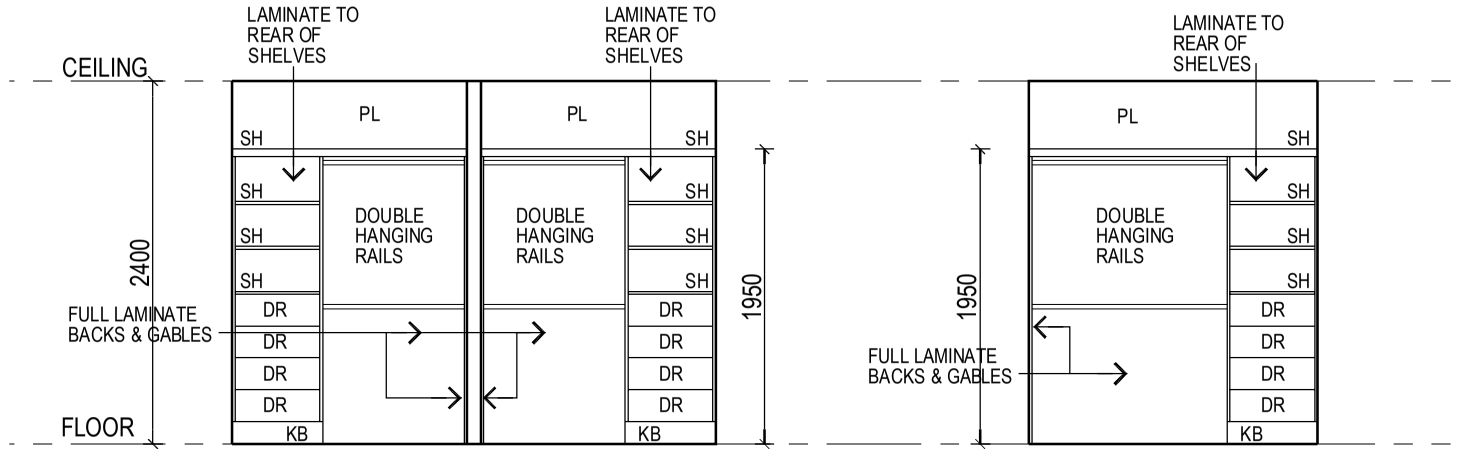

- ELEVATION 19
BED 2 ROBE - V150 1:50

- ELEVATION 20
BED 3 ROBE - V150 1:50

ISSUE	DATE	DESCRIPTION
A	01/07/26	ISSUED FOR CONSTRUCTION

© COPYRIGHT NOTICE
Copyright of this drawing and design is held permanently by Carma Building Group Pty Ltd. Unauthorised use of this drawing and / or design, or any variation thereof, will trigger immediate legal proceedings.

carma building group
Suite 2 / 199 Gympie Tce, Noosaville Q 45
T 07 5447 1250 F 07 5470 2586
E admin@carmabuildinggroup.com.au

PROJECT
VILLAS 149 & 150
LAGUNA ESTATE
21 LAKE WEYBA DRIVE
NOOSAVILLE


CLIENT
LAGUNA RETIREMENT ESTATE

DRAWING TITLE
VILLA 150 - BATHROOM & ROBE DETAILS

SCALE	@ ORIGINAL SIZ
1:50	A3
DATE	DRAW
JULY 2026	MW

DRAWING STATUS
FOR CONSTRUCTION

DRAWING NO.	ISSU
LRV149 WD-15	A

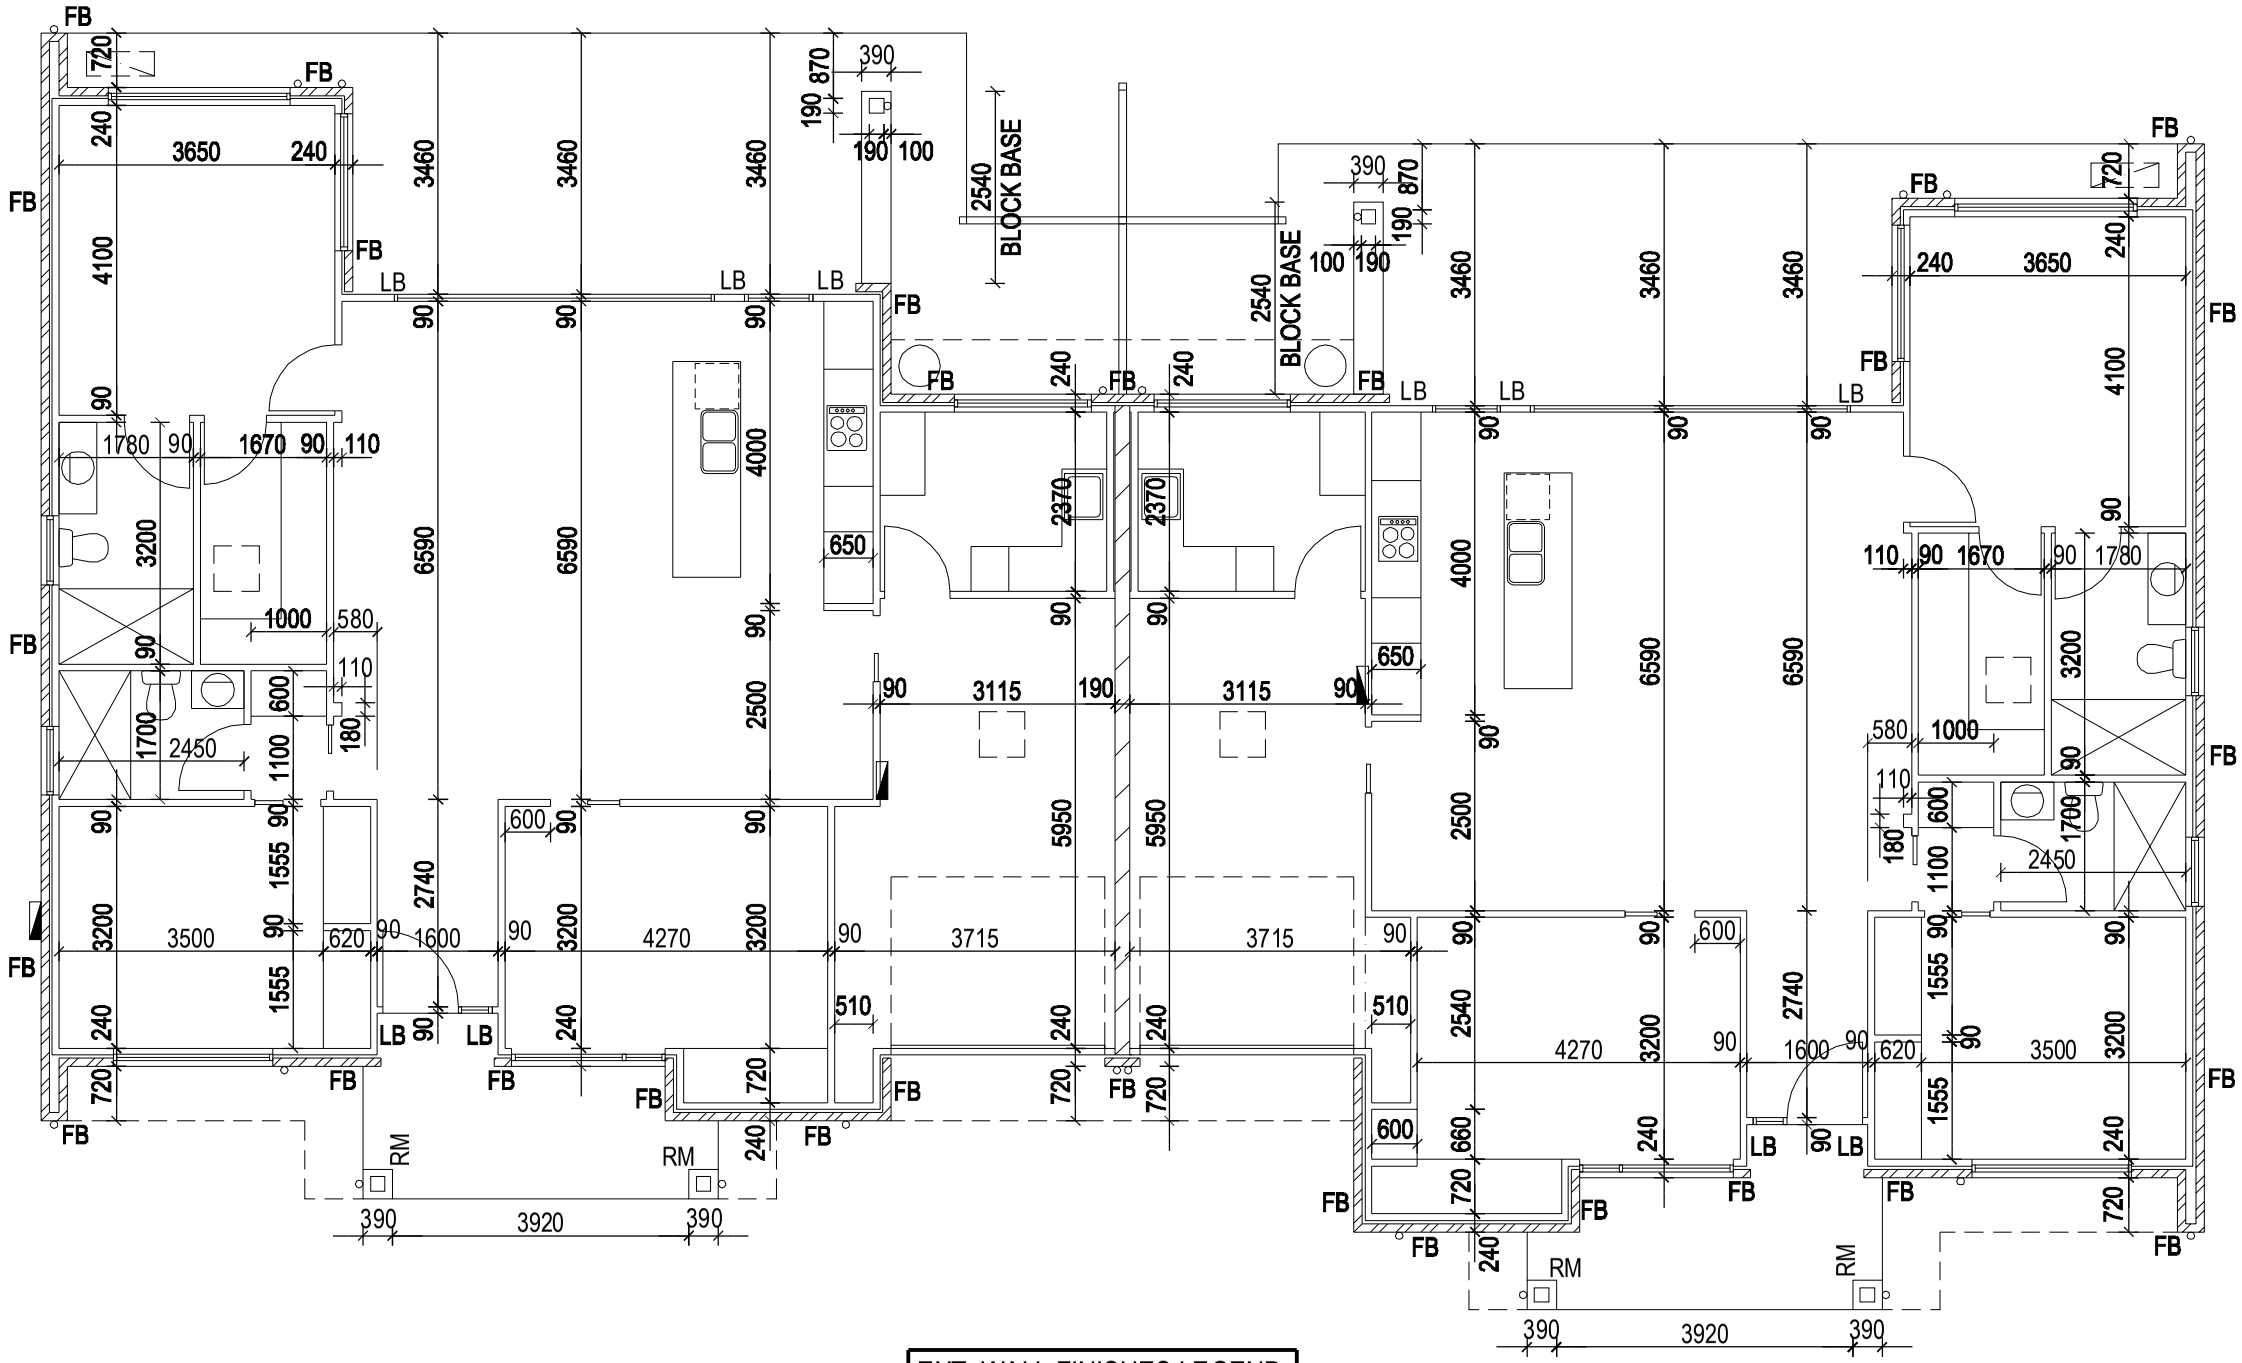

EXT. WALL FINISHES LEGEND	
FB	FACE BRICKWORK
LB	LINEA-BOARD CLADDING
RB	RENDERED BLUEBOARD
RM	RENDERED MASONRY

ISSUE	DATE	DESCRIPTION
A	01/04/26	ISSUED FOR APPROVALS

© COPYRIGHT NOTICE
Copyright of this drawing and design is held permanently by Carma Building Group Pty Ltd. Unauthorised use of this drawing and / or design, or any variation thereof, will trigger immediate legal proceedings.

carma building group
Suite 2 / 199 Gympie Tce, Noosaville Q 45
T 07 5447 1250 F 07 5470 2586
E admin@carmabuildinggroup.com.au

PROJECT
VILLAS 149 & 150
LAGUNA ESTATE
21 LAKE WEYBA DRIVE
NOOSAVILLE


CLIENT
LAGUNA RETIREMENT ESTATE

DRAWING TITLE
FLOOR PLAN DIMENSIONED & EXTERNAL WALL FINISHES

SCALE	@ ORIGINAL SIZ
1:100	A3
DATE	DRAW
APRIL 2026	MW

DRAWING STATUS
FOR CONSTRUCTION

DRAWING NO.	ISSU
LRV149 WD-20	A

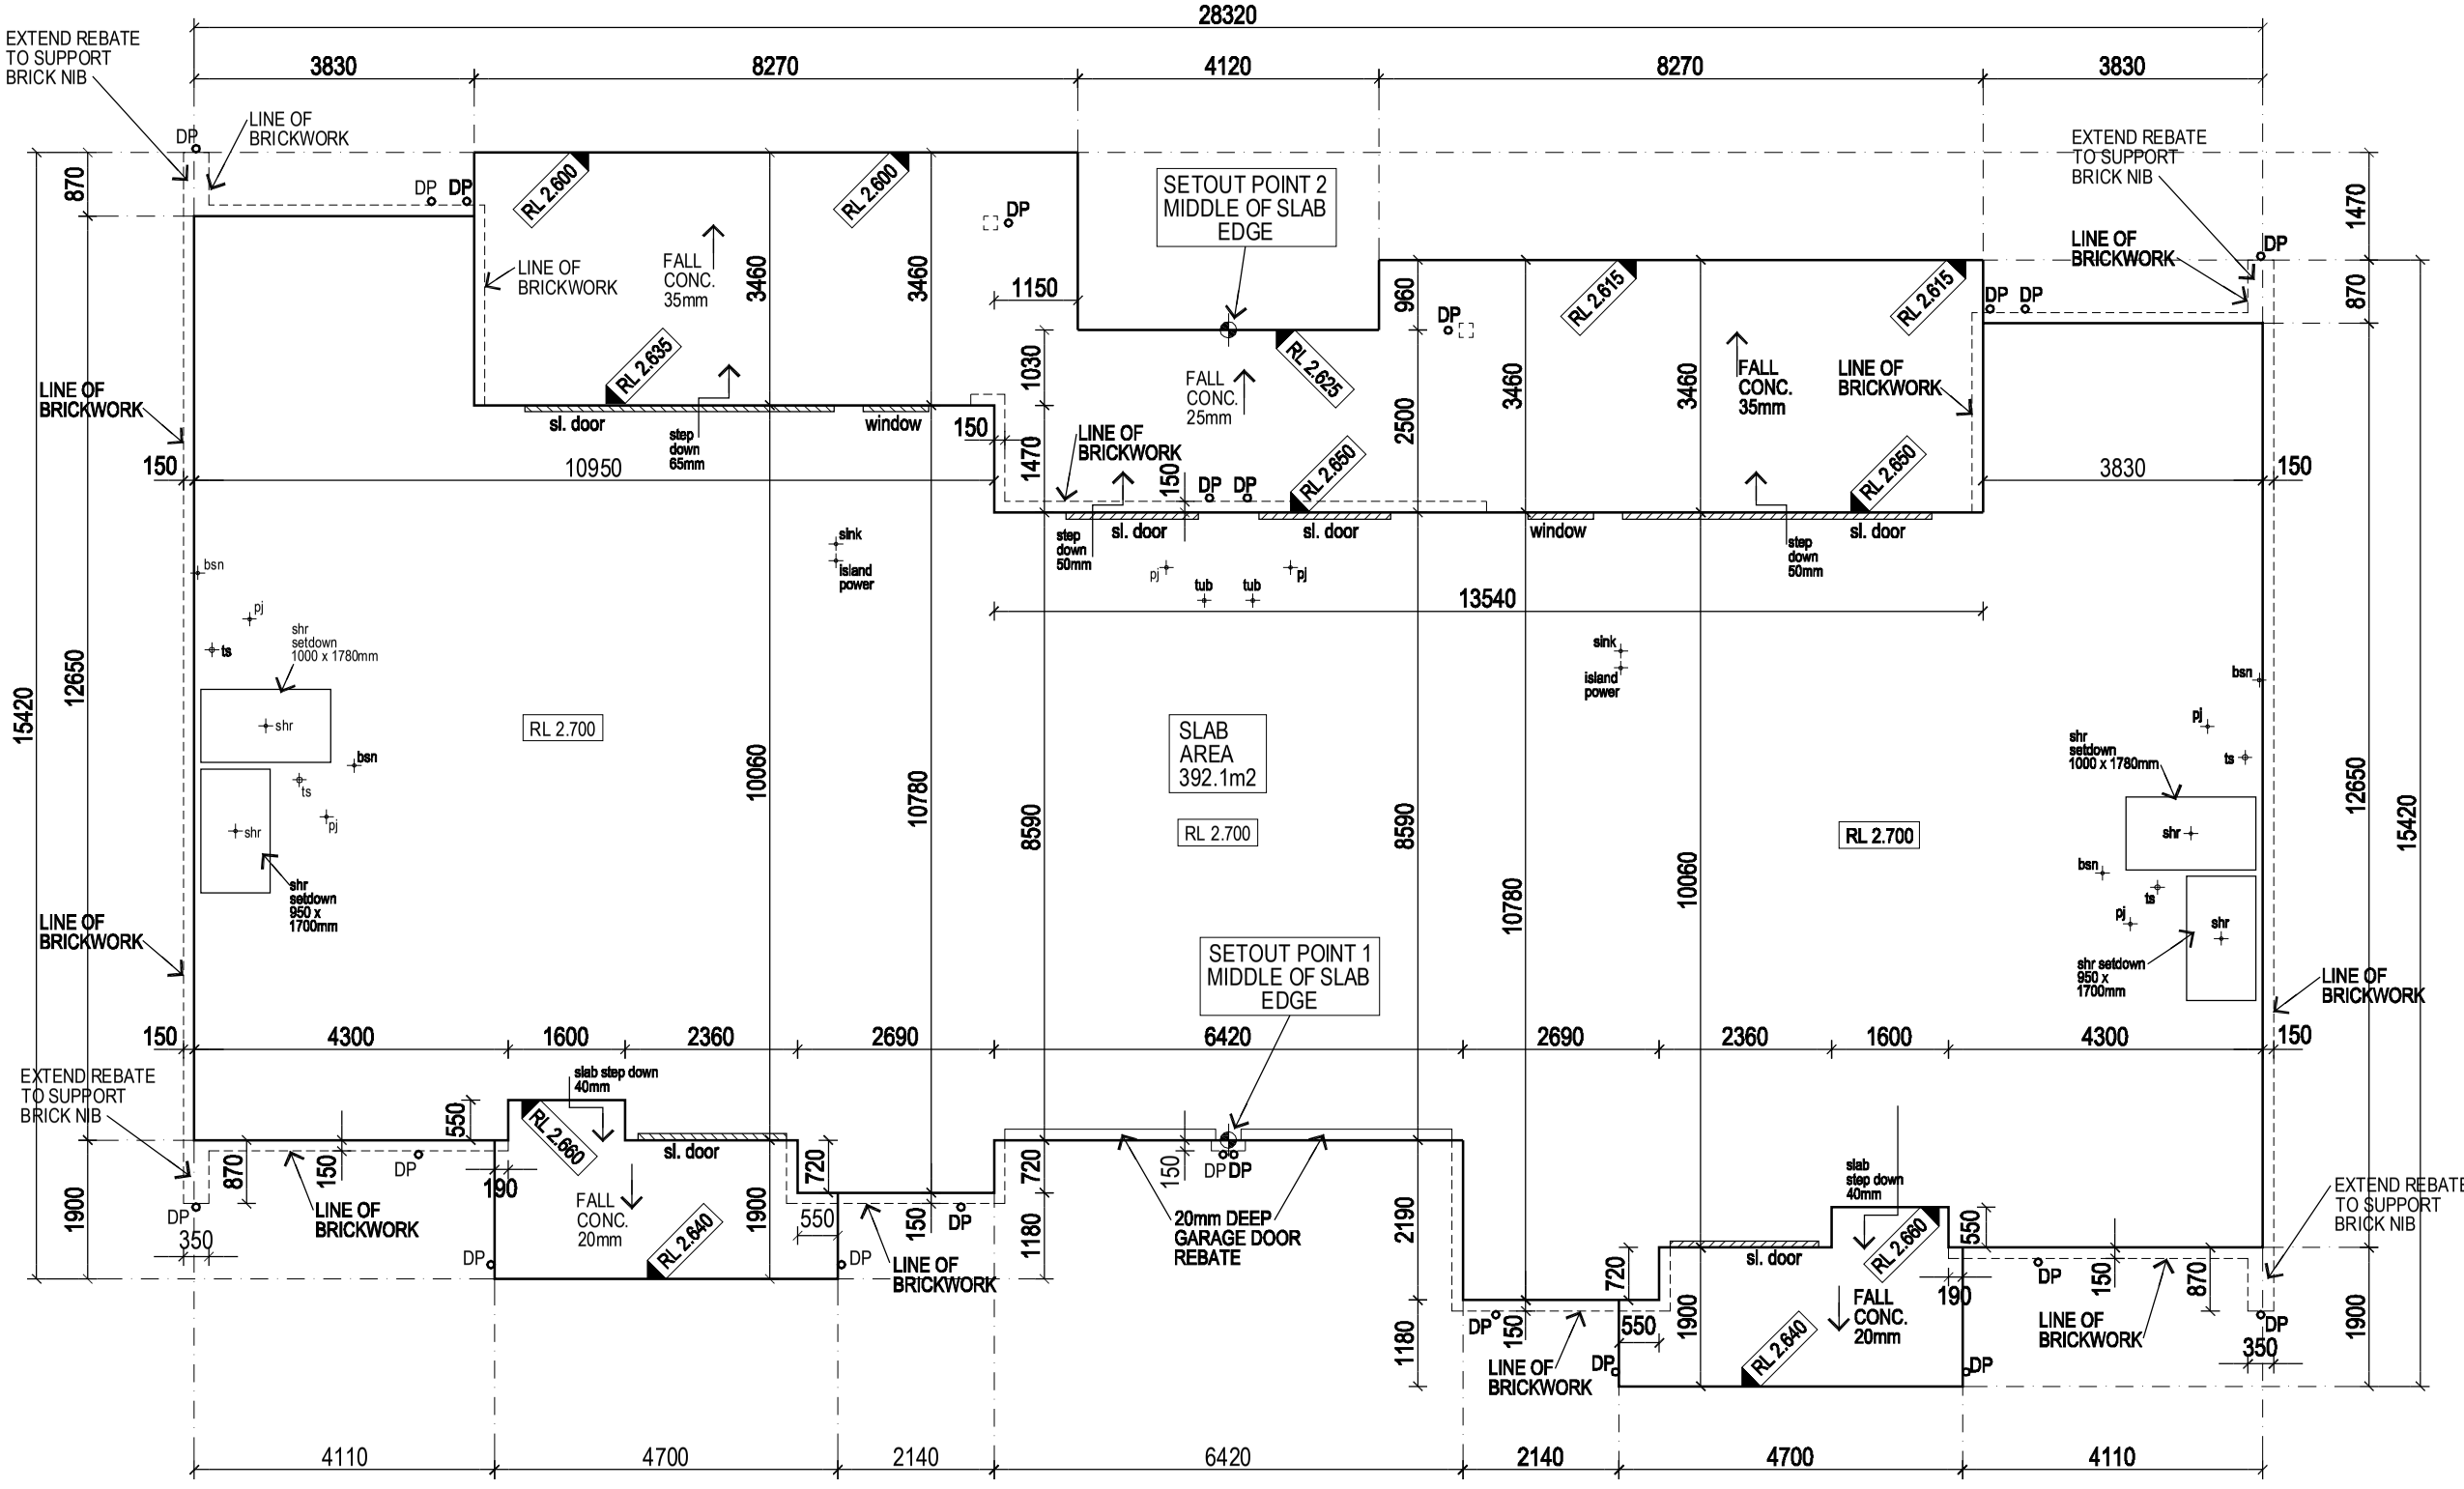

ISSUE	DATE	DESCRIPTION
A	01/04/26	ISSUED FOR APPROVALS
B	27/08/26	REAR TERRACE SLAB DELETED BOTH VILLAS

© COPYRIGHT NOTICE
Copyright of this drawing and design is held permanently by Carma Building Group Pty Ltd. Unauthorised use of this drawing and / or design, or any variation thereof, will trigger immediate legal proceedings.

carma building group
Suite 2 / 199 Gympie Tce, Noosaville Q 45
T 07 5447 1250 F 07 5470 2586
E admin@carmabuildinggroup.com.au

PROJECT
VILLAS 149 & 150
LAGUNA ESTATE
21 LAKE WEYBA DRIVE
NOOSAVILLE

CLIENT
LAGUNA RETIREMENT ESTATE

DRAWING TITLE
SLAB PLAN

SCALE	@ ORIGINAL SIZ
1:100	A3
DATE	DRAW
APRIL 2026	MW

DRAWING STATUS
FOR CONSTRUCTION

DRAWING NO.	ISSU
LRV149 WD-30	B



ISSUE	DATE	DESCRIPTION
A	01/04/26	ISSUED FOR APPROVALS

© COPYRIGHT NOTICE
Copyright of this drawing and design is held permanently by Carma Building Group Pty Ltd. Unauthorised use of this drawing and / or design, or any variation thereof, will trigger immediate legal proceedings.

carma building group
Suite 2 / 199 Gympie Tce, Noosaville Q 45(
T 07 5447 1250 F 07 5470 2586
E admin@carmabuildinggroup.com.au

PROJECT
VILLAS 149 & 150
LAGUNA ESTATE
21 LAKE WEYBA DRIVE
NOOSAVILLE

CLIENT
LAGUNA RETIREMENT ESTATE

DRAWING TITLE
LOCALITY PLAN

SCALE	@ ORIGINAL SIZ
1:200	A3
DATE	DRAW
APRIL 2026	MW

DRAWING STATUS
FOR CONSTRUCTION

DRAWING NO.	ISSU
LRV149 WD-50	A