FINISHES

LAM01 - LAMINEX ELEGANT OAK
LAM02 - LAMINEX ARIES. COLOUR TBC
ST01 - BRECCIATE PRIMAVERA MARBLE
ST02 - YDL MAHAL IVORY
MEL01 - WHITE MELAMINE INTERNAL CARCASS

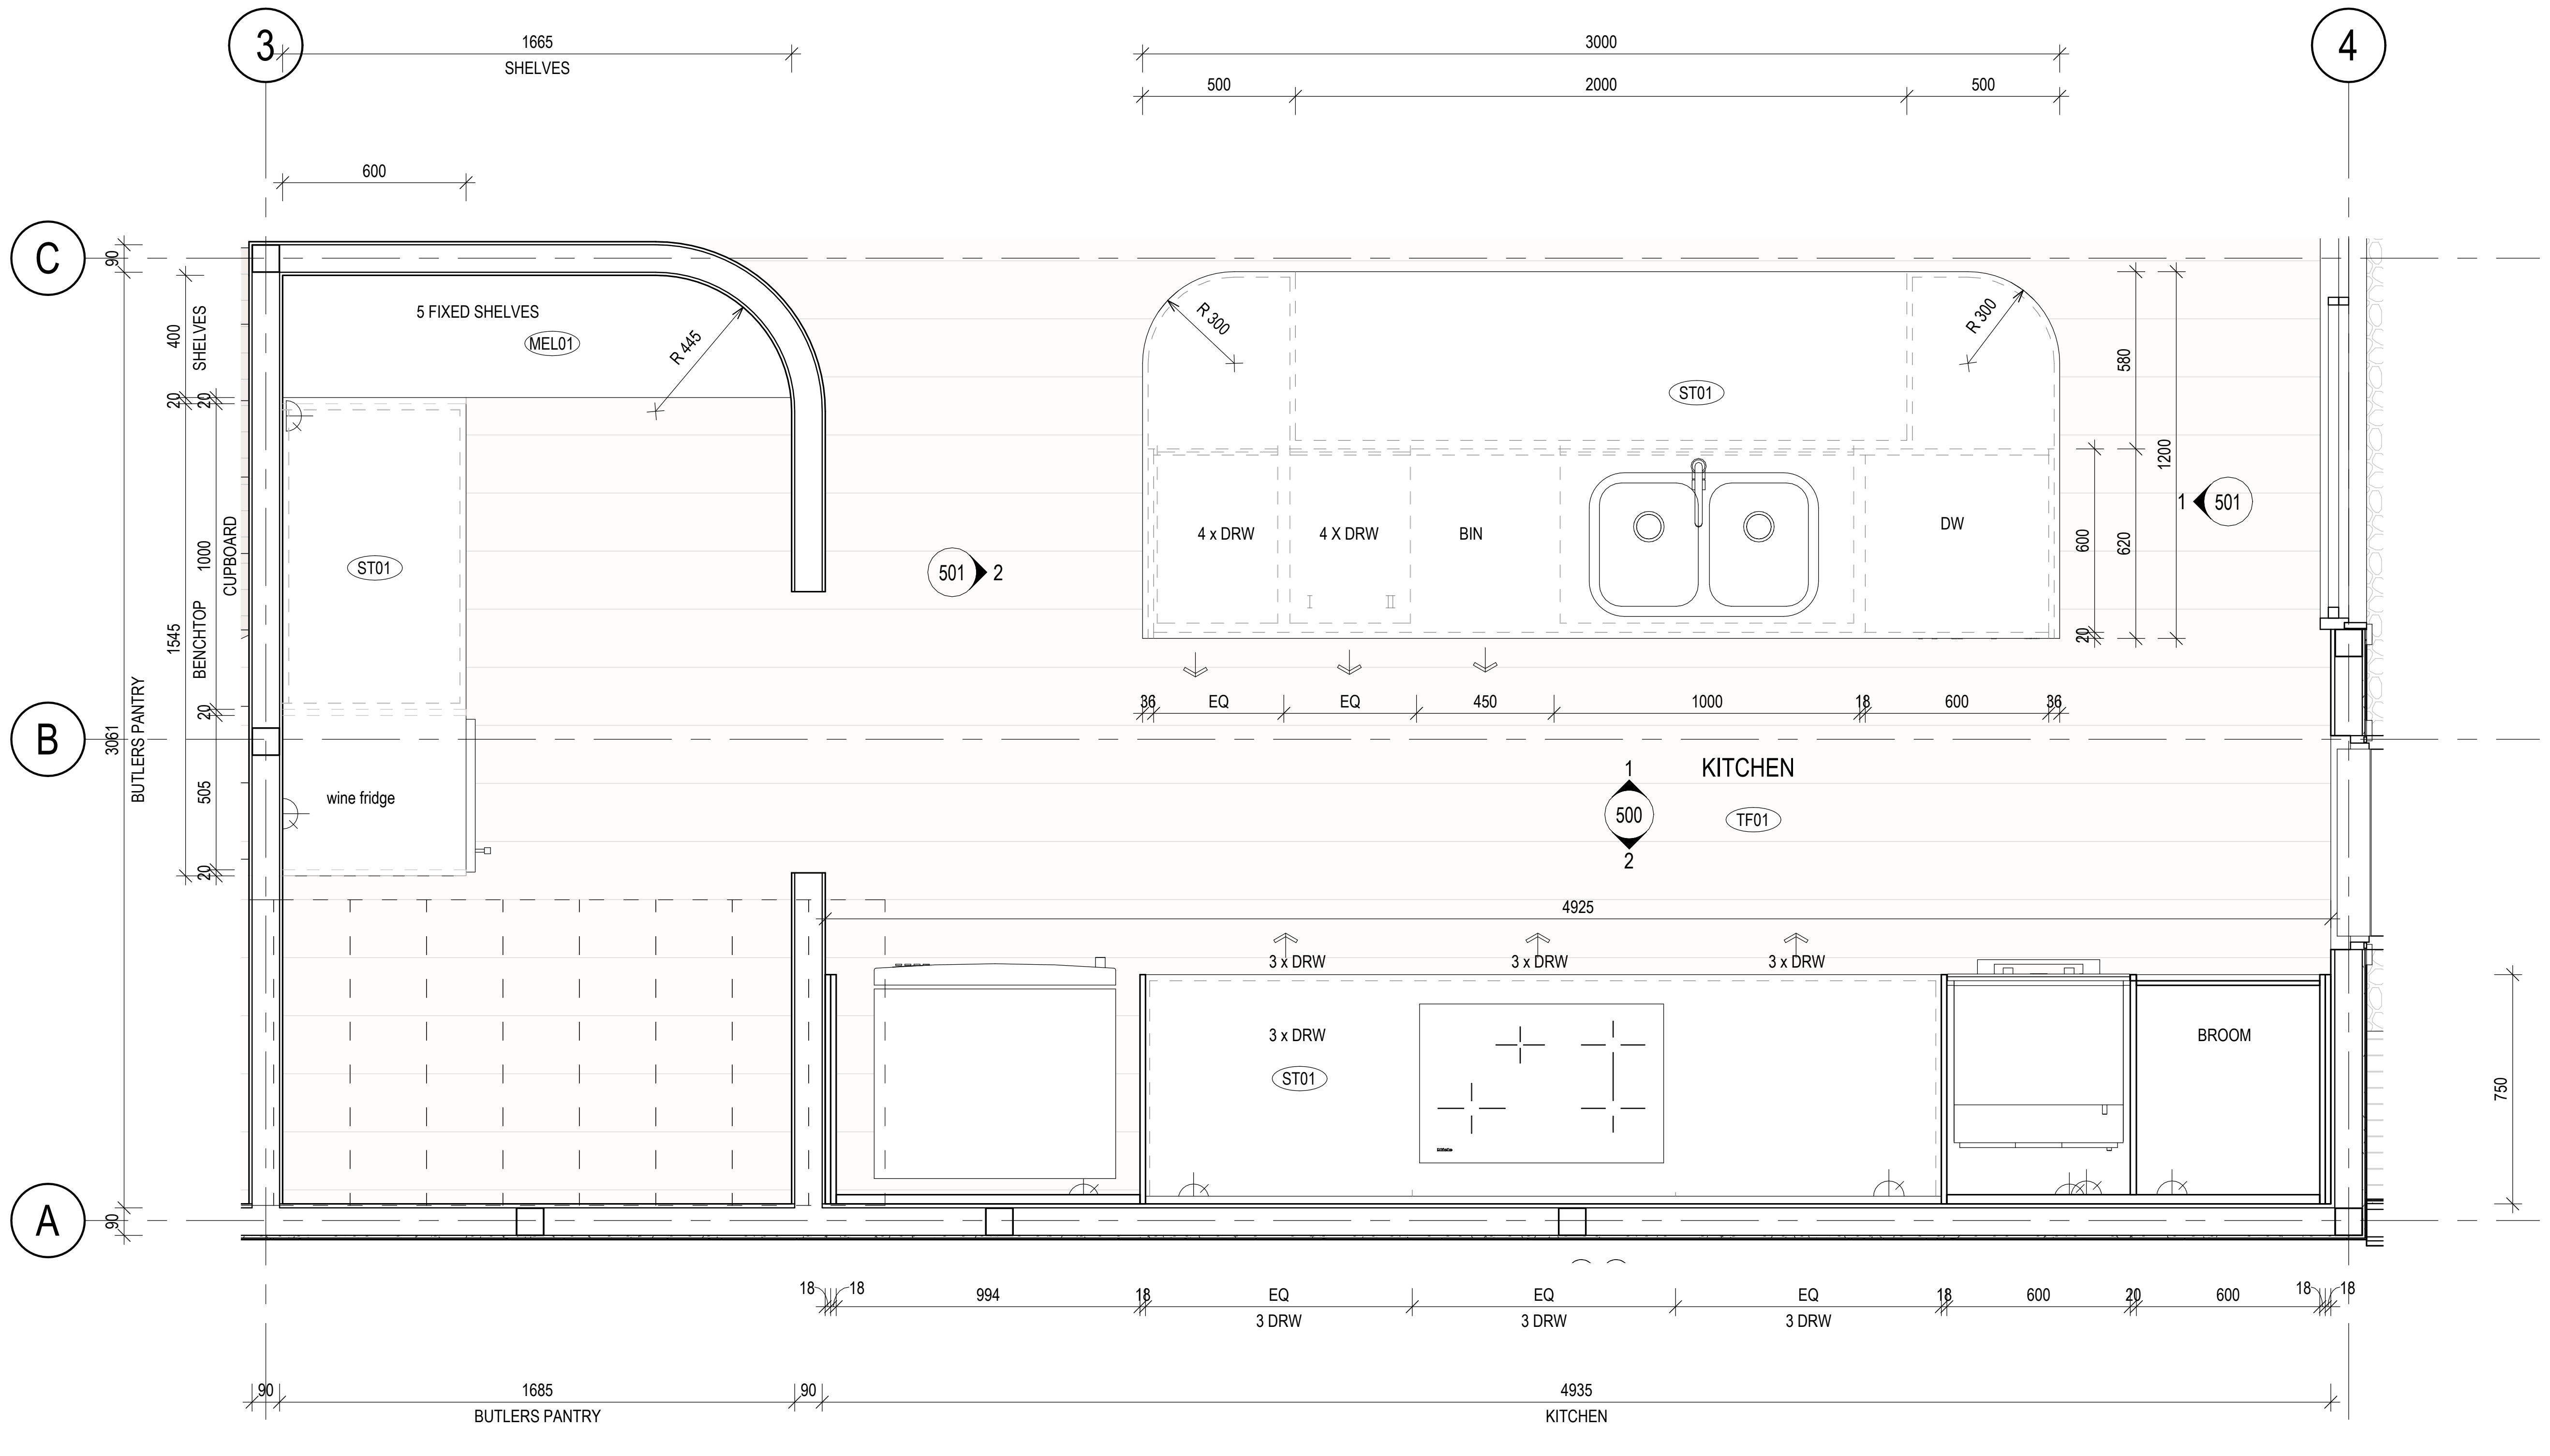

3
203
KITCHEN LAYOUT - PLAN
1 : 20

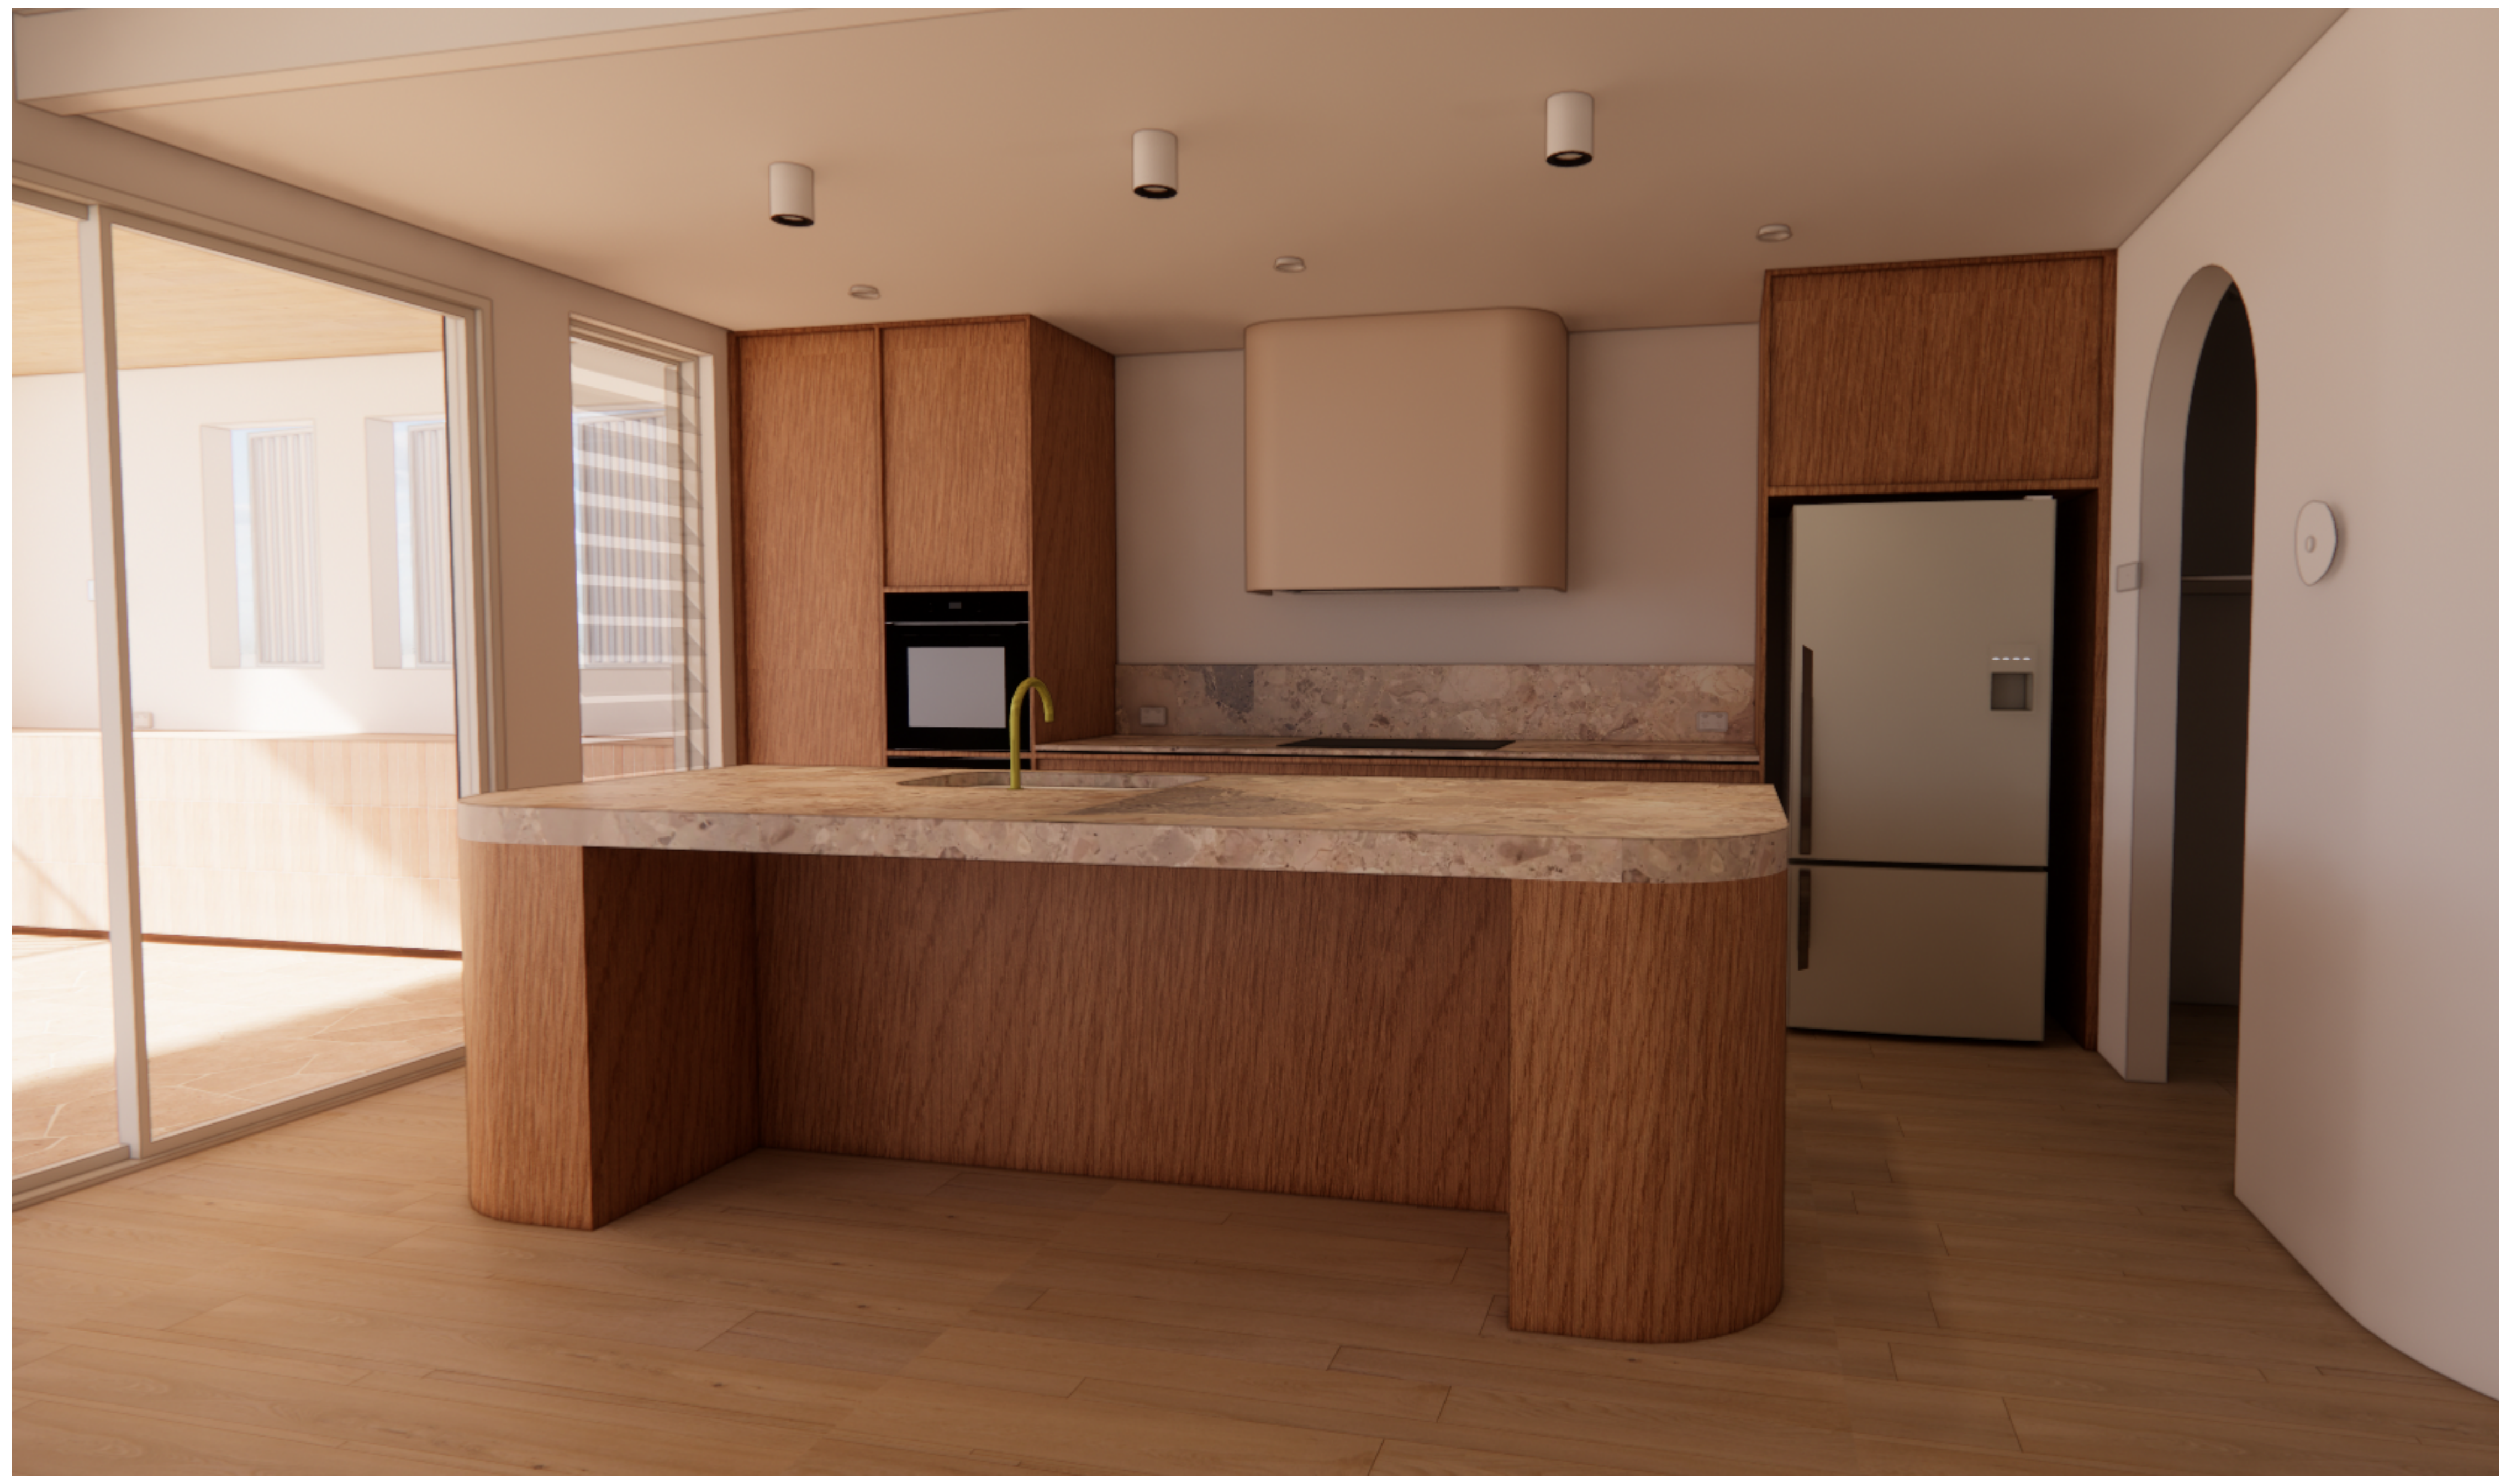

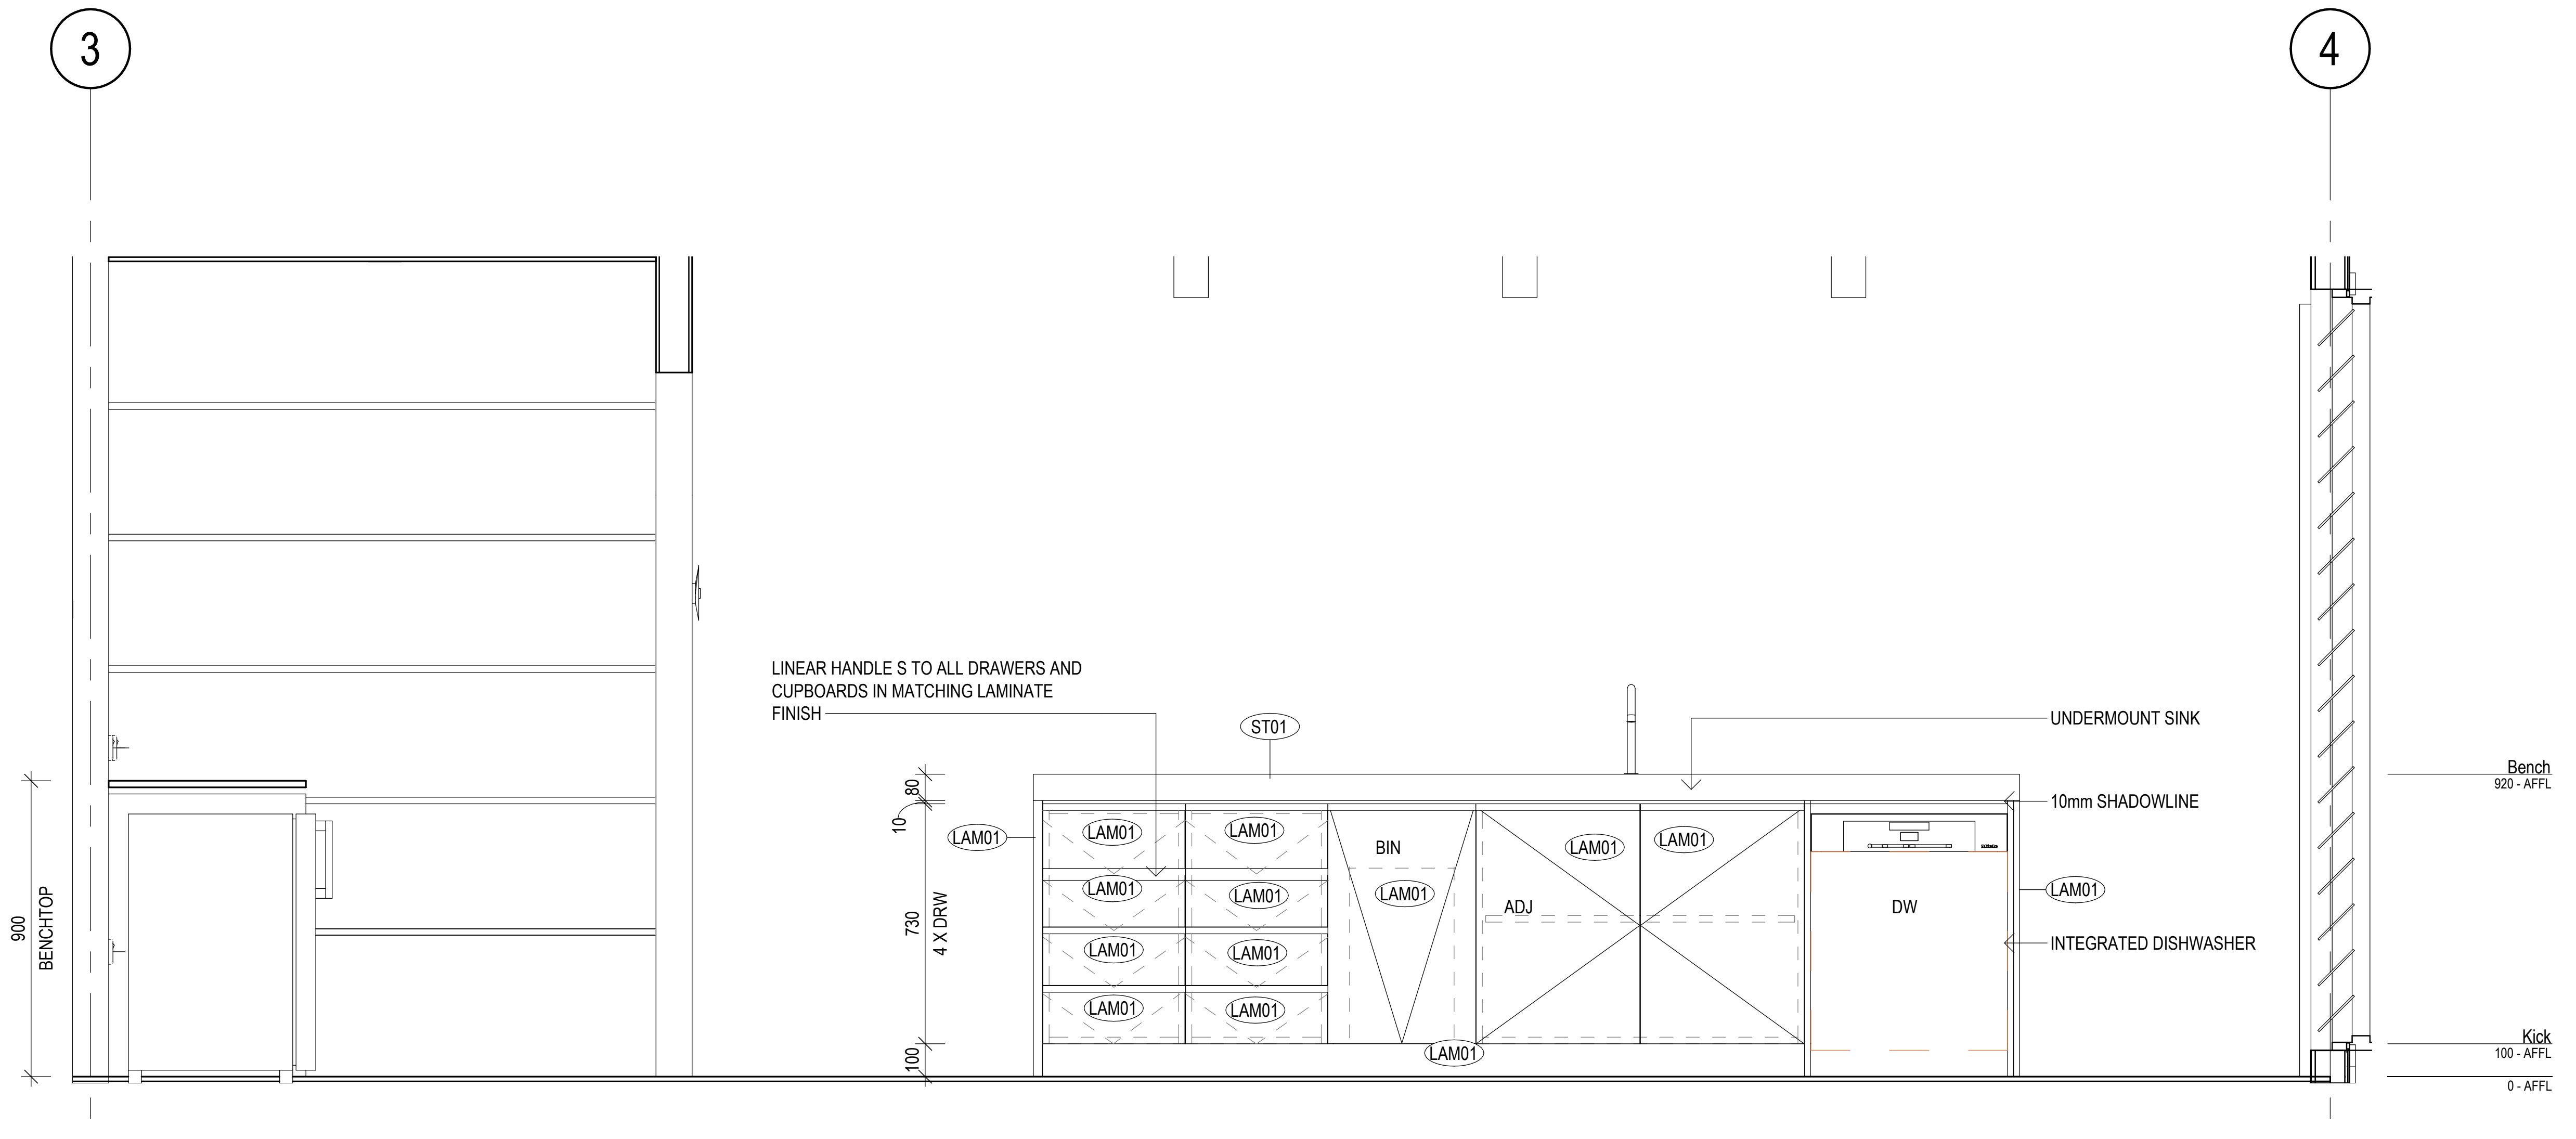

1
106
KITCHEN - ELEVATION A
1 : 20

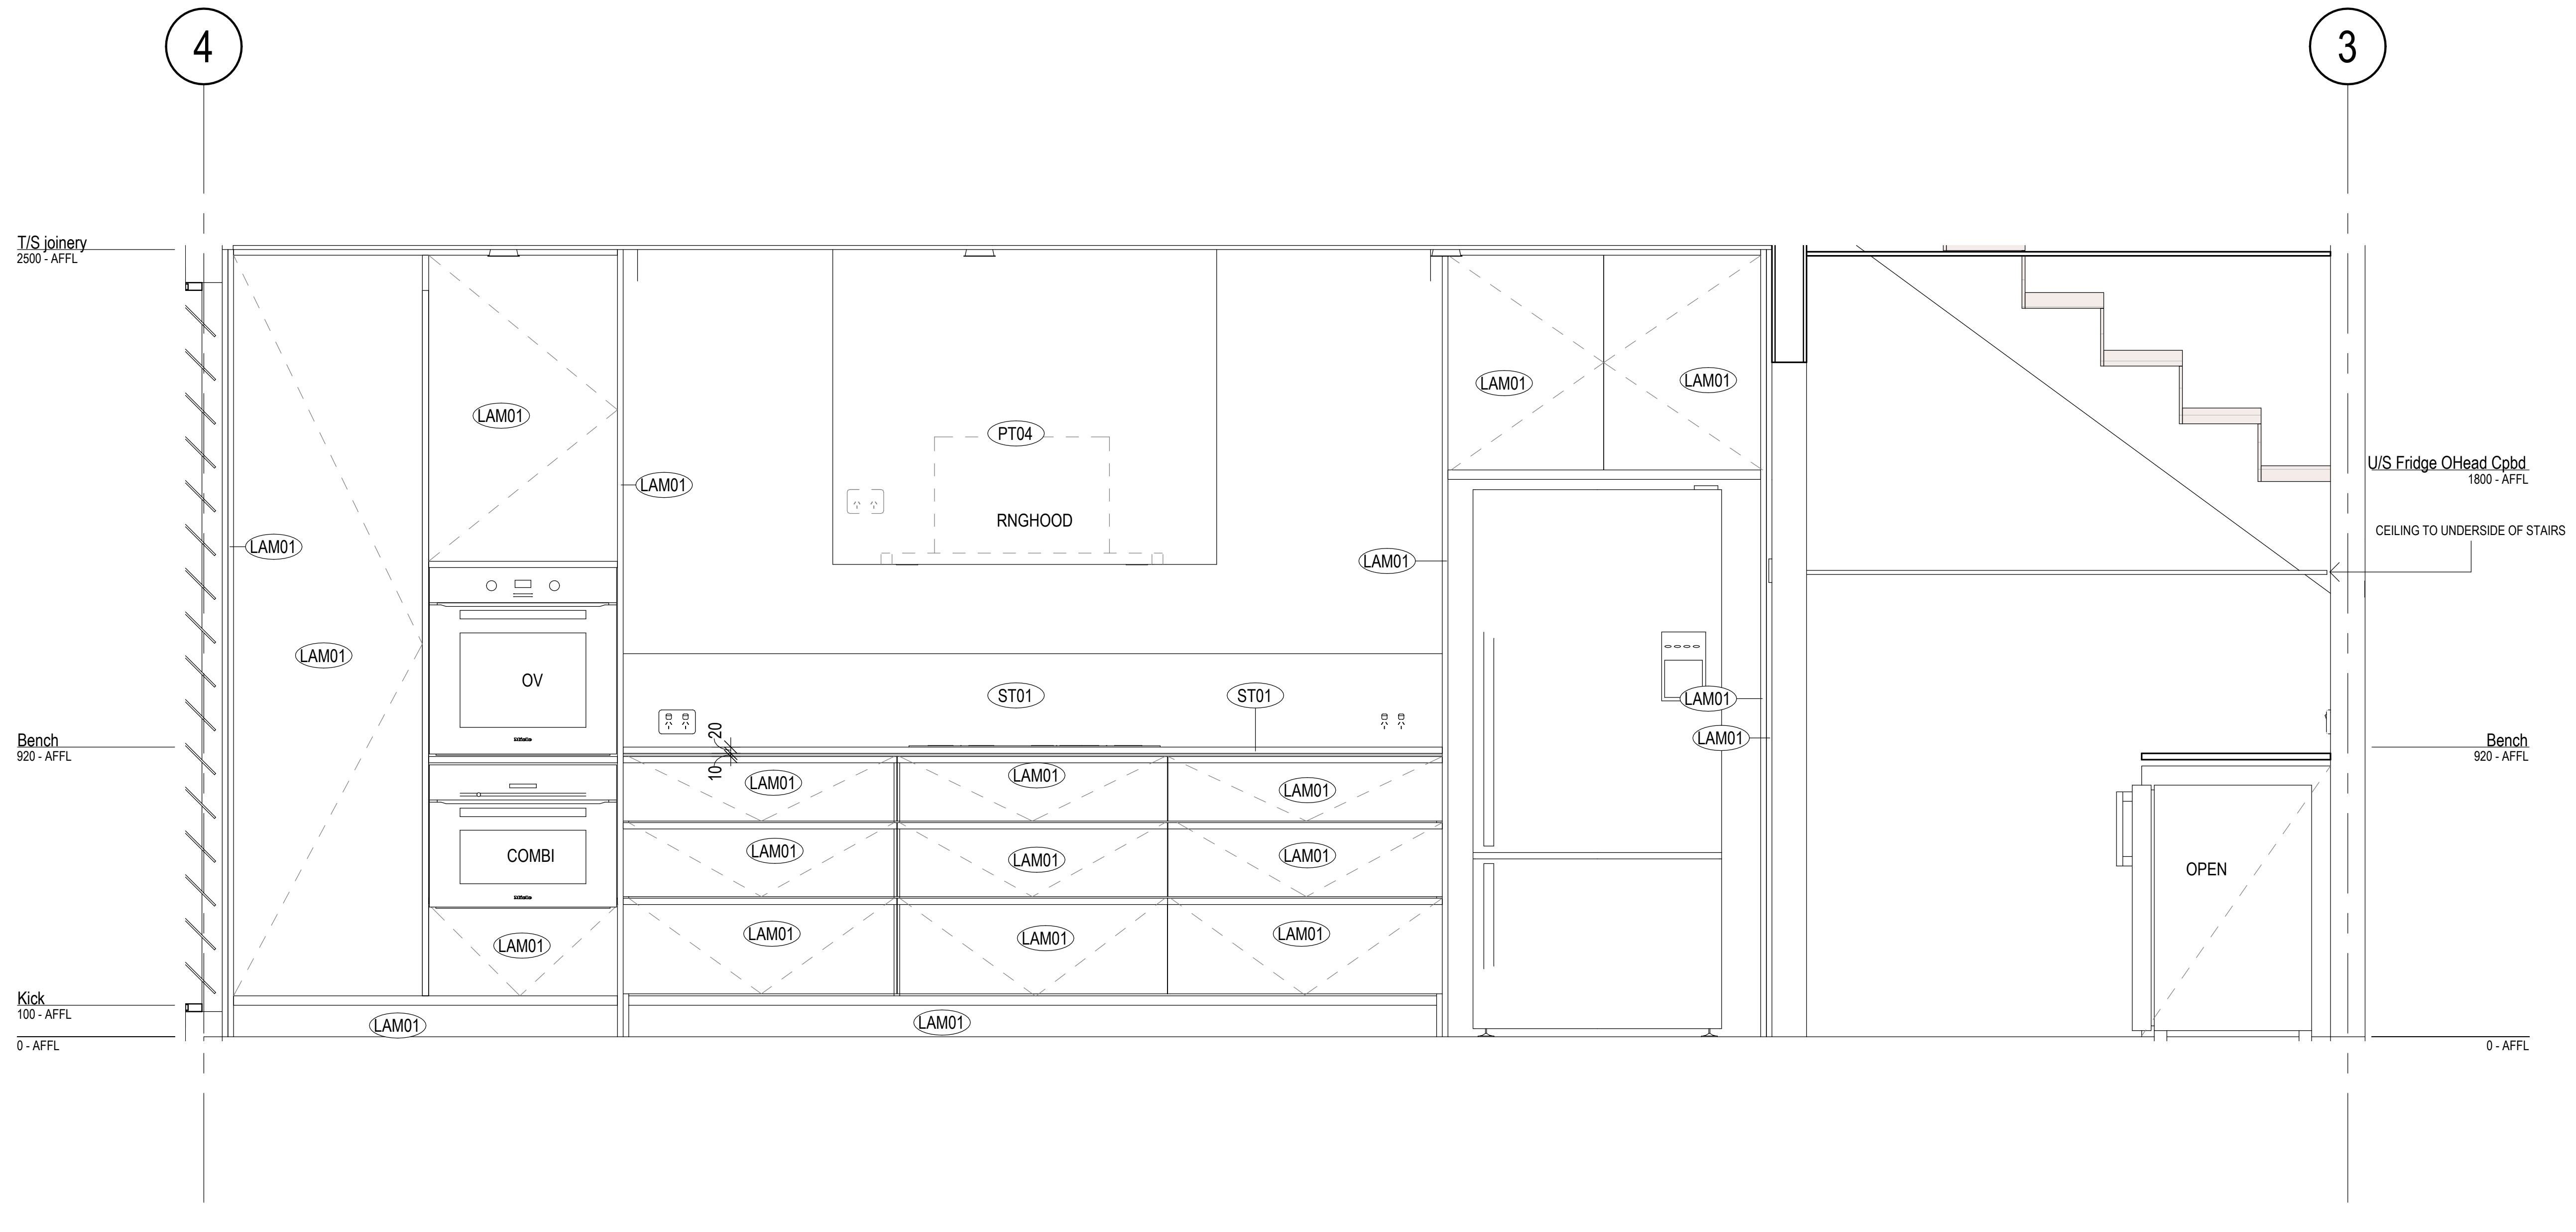

2
106
KITCHEN - ELEVATION B
1 : 20

16/08/2026 8:17:24 PM
C:\Users\KatherineB\OneDrive - nettletontribe\38 Howard\Revit\Concstruction\38 HOWARD_PROPOSED_ARCH (1).rvt

Client

Client Logo

Issue	Description	Date
B	JOINERY ISSUE 1	16-08-2026
A	ISSUE FOR CONSTRUCTION	26-05-2026

Builder and/or subcontractors shall verify all project dimensions before commencing on-site work or off-site fabrication. Figured dimensions shall take precedence over scaled dimensions. This drawing is copyright and cannot be reproduced in whole or in part or by any medium without the written permission of Katherine Blackham.

Builder

Builders Logo

Project Name
38 Howard Street
Project Address
38 Howard Street, Grange QLD

Key Plan
0 2000 5000

Drawing Title:
KITCHEN - PLAN & ELEVATIONS

Checker: **KB**
Sheet Size: **A1**
Scale: **1:20**
Drawing Number: **2025-01_500**
Issue: **B**

FINISHES

LAM01 - LAMINEX ELEGANT OAK
LAM02 - LAMINEX ARIES. COLOUR TBC
ST01 - BRECCIATE PRIMAVERA MARBLE
ST02 - YDL MAHAL IVORY
MEL01 - WHITE MELAMINE INTERNAL CARCASS

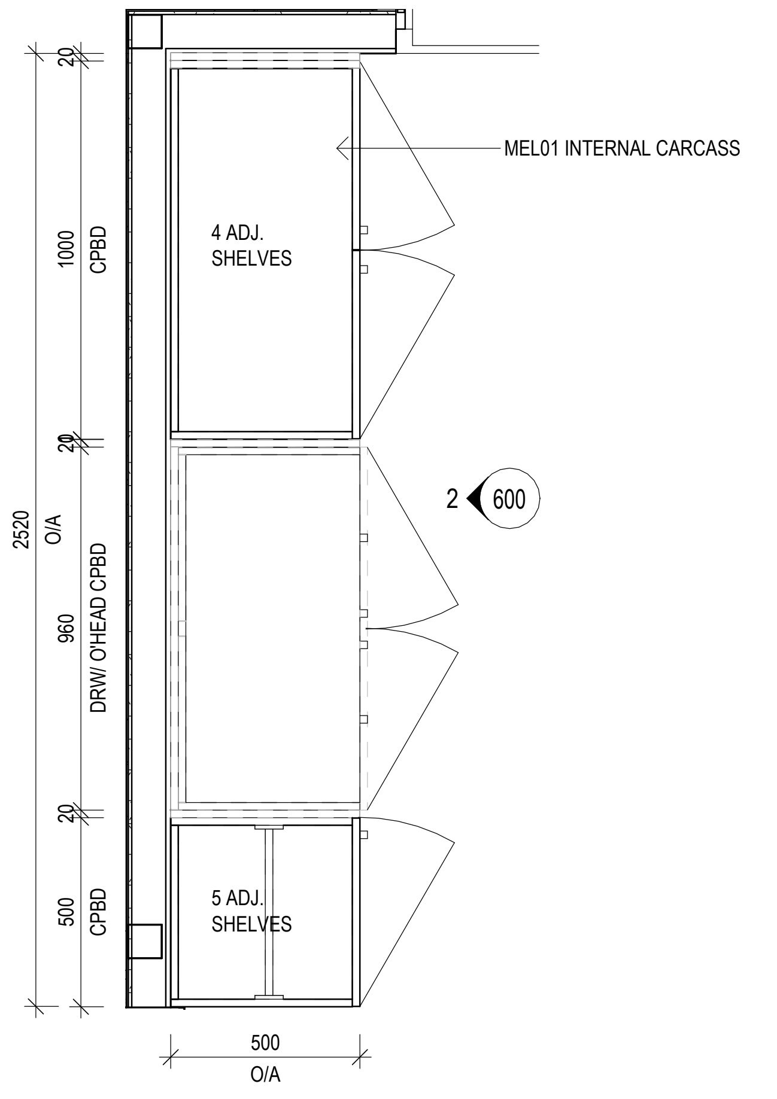

1 / 203 J01 ENTRY JOINERY
1 : 20

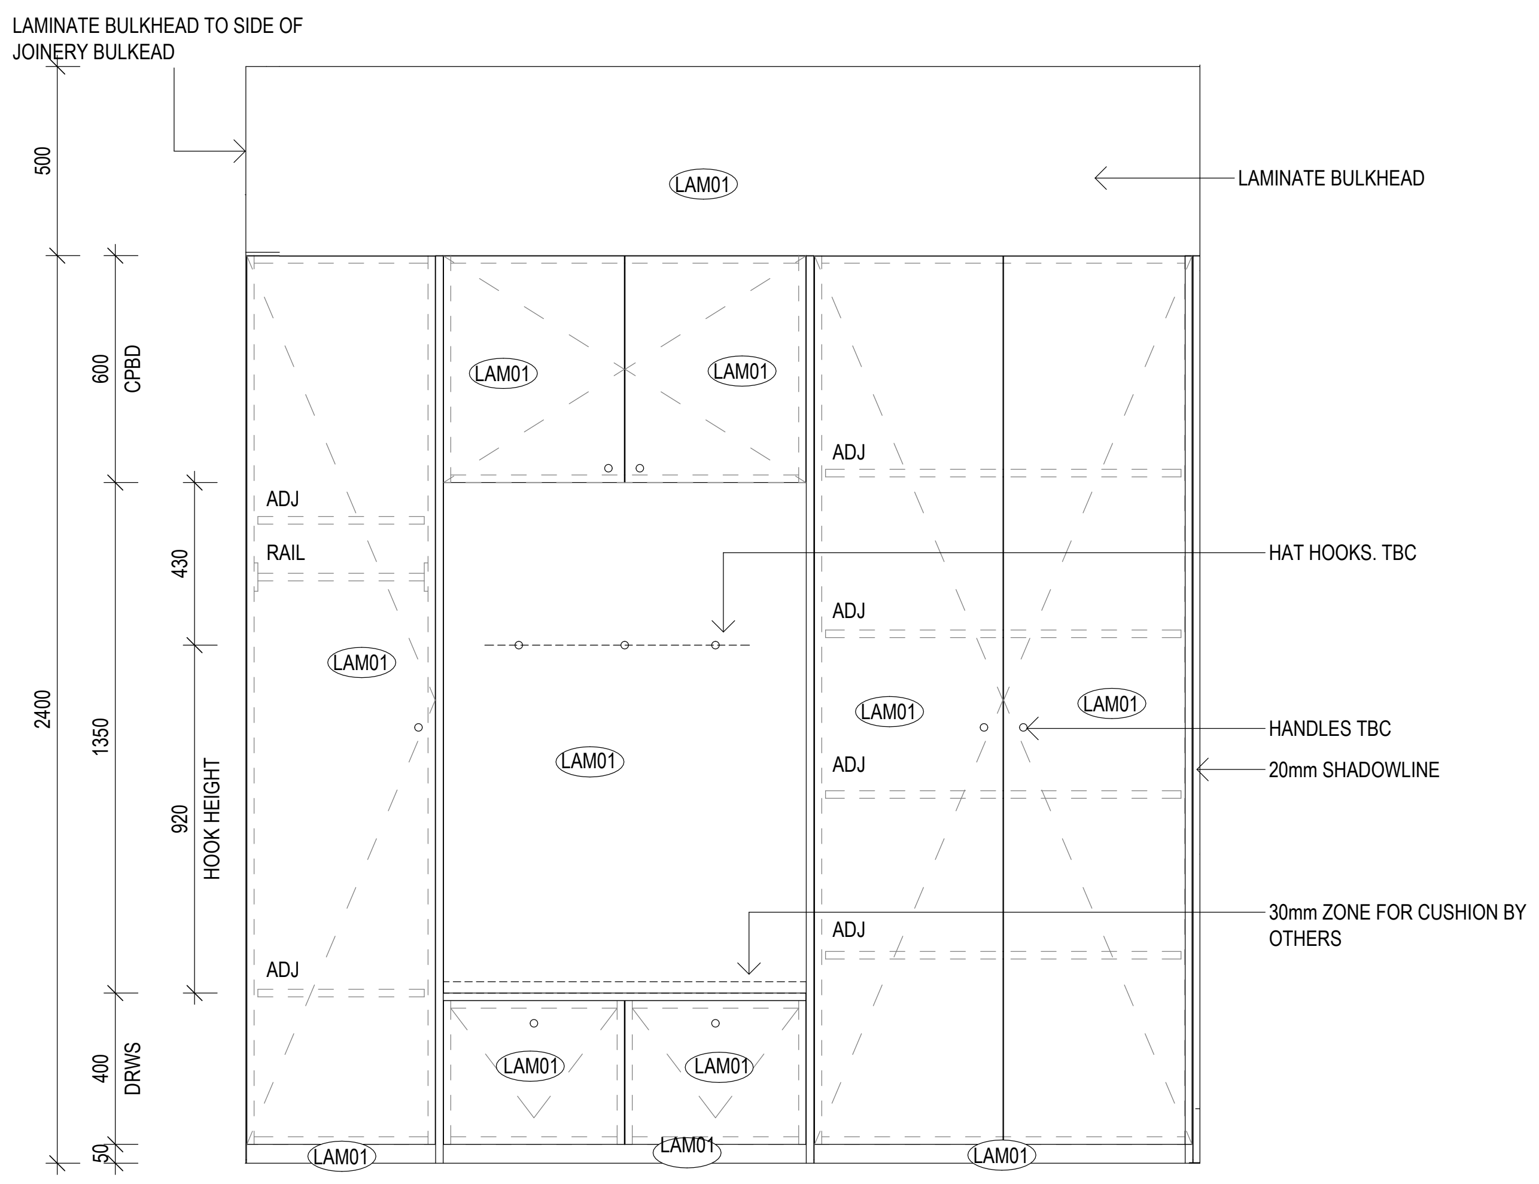

2 / 106 J01 ENTRY JOINERY - ELEVATION
1 : 20

NOTE: PROPRIETARY HANDLES TBC

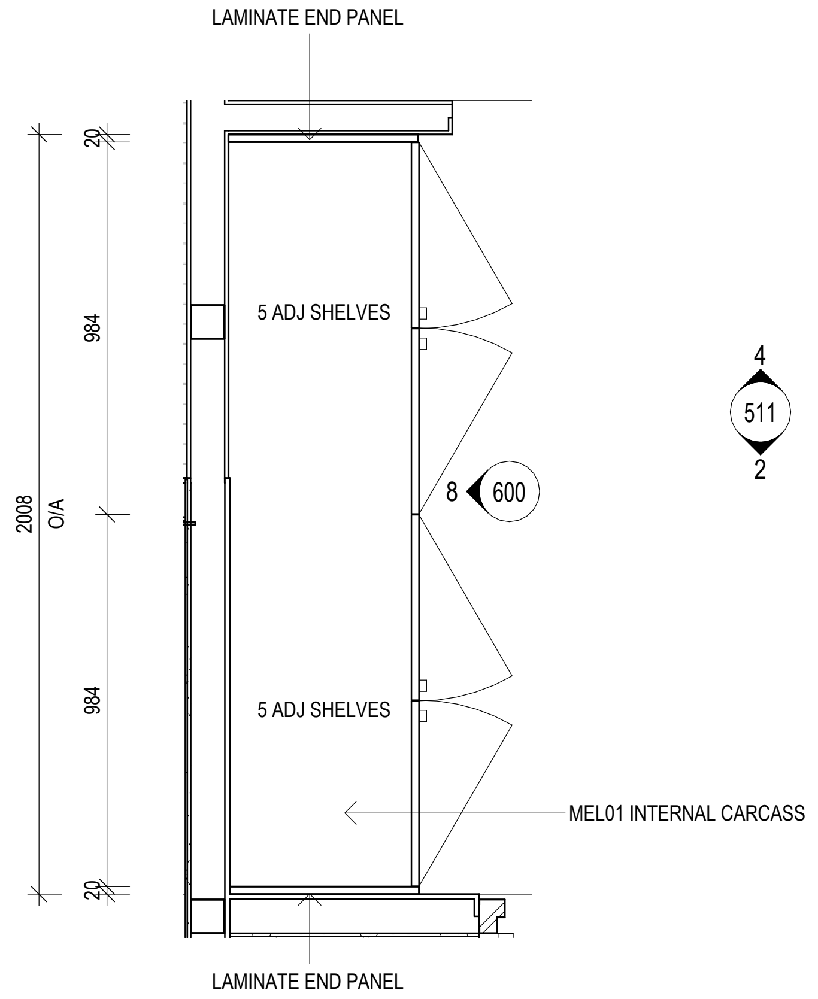

7 / 203 J02 - LAUNDRY CPBD
1 : 20

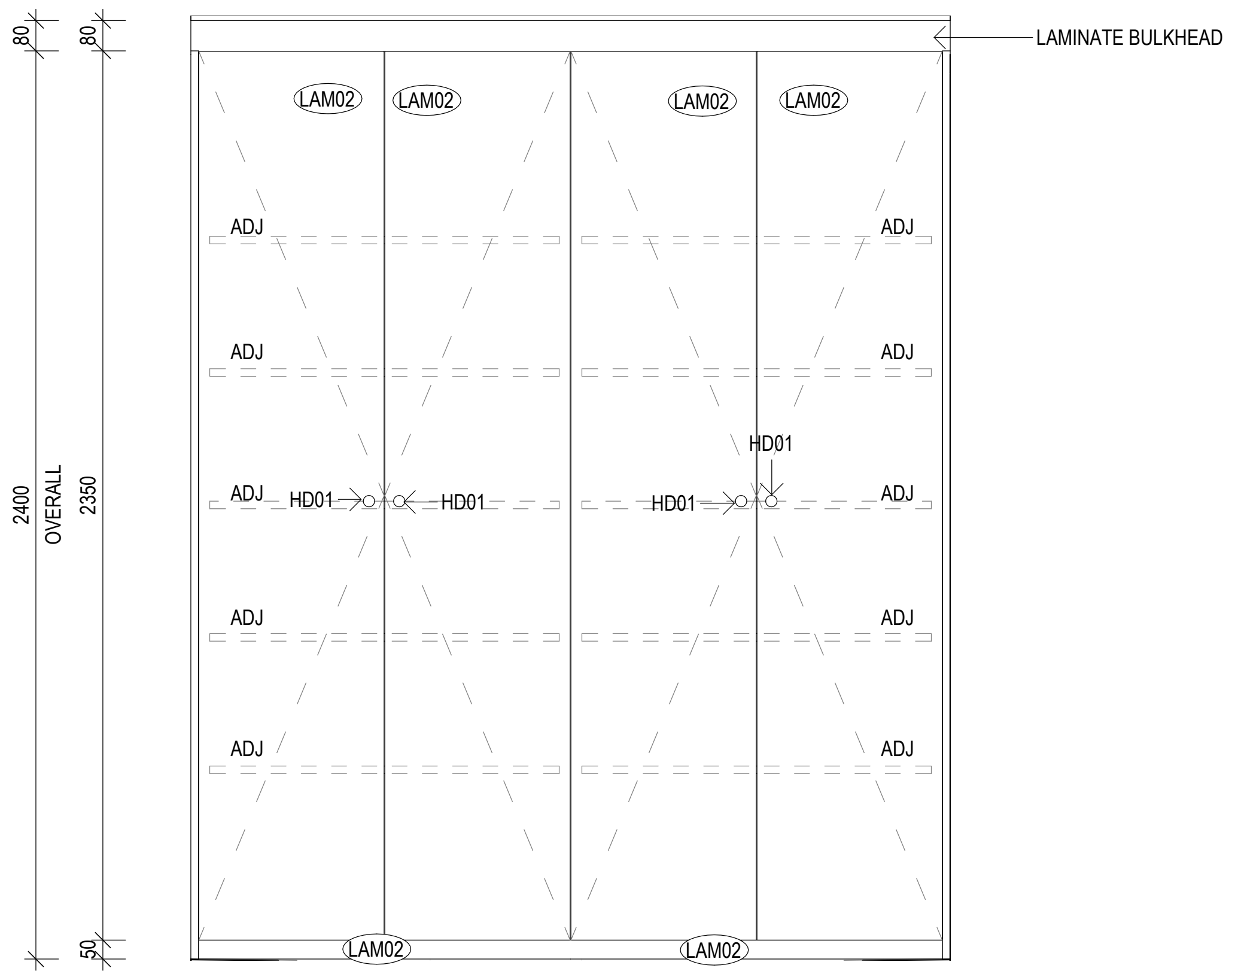

8 / 106 J02 - LAUNDRY CPBD - ELEVATION
1 : 20

NOTE: PROPRIETARY HANDLES TBC

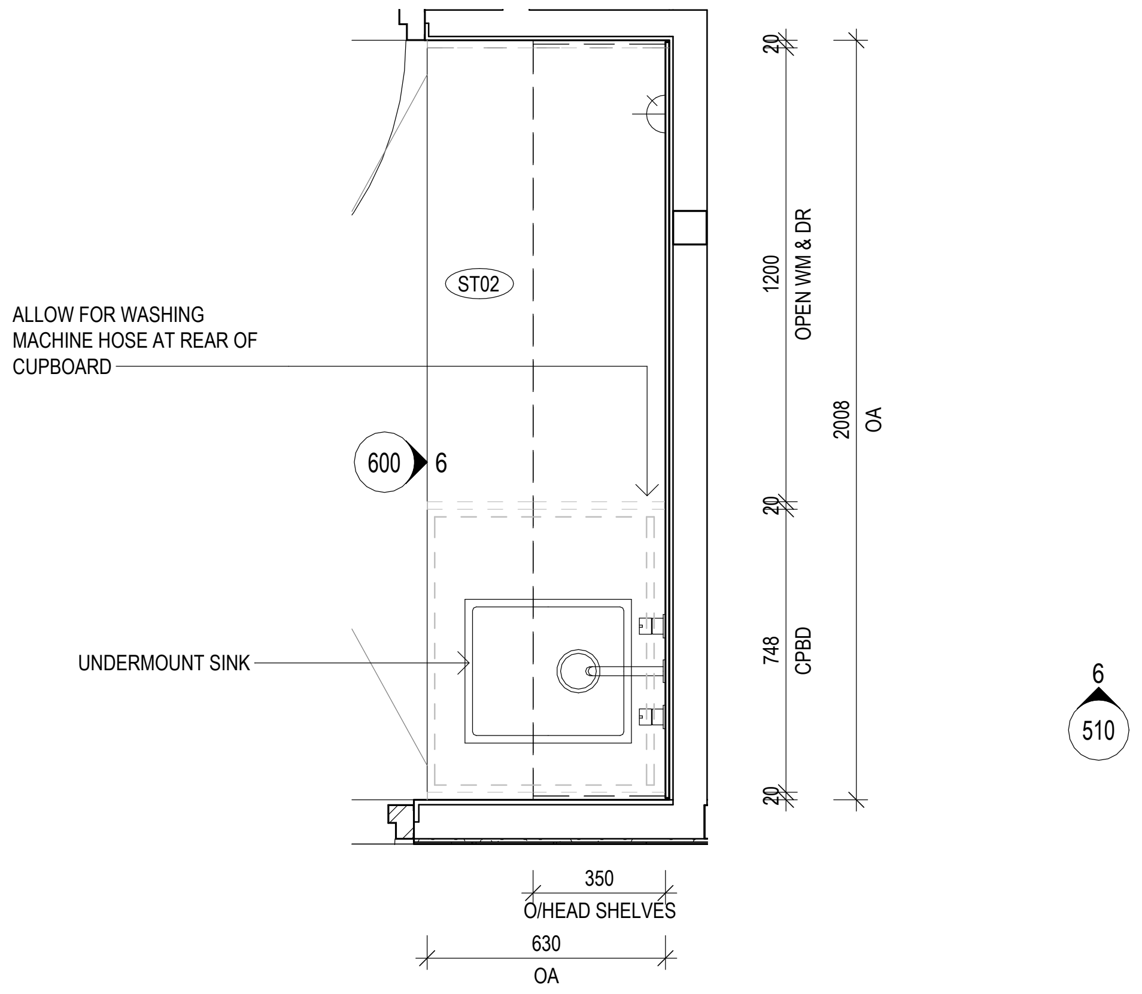

5 / 203 J03 - LAUNDRY JOINERY
1 : 20

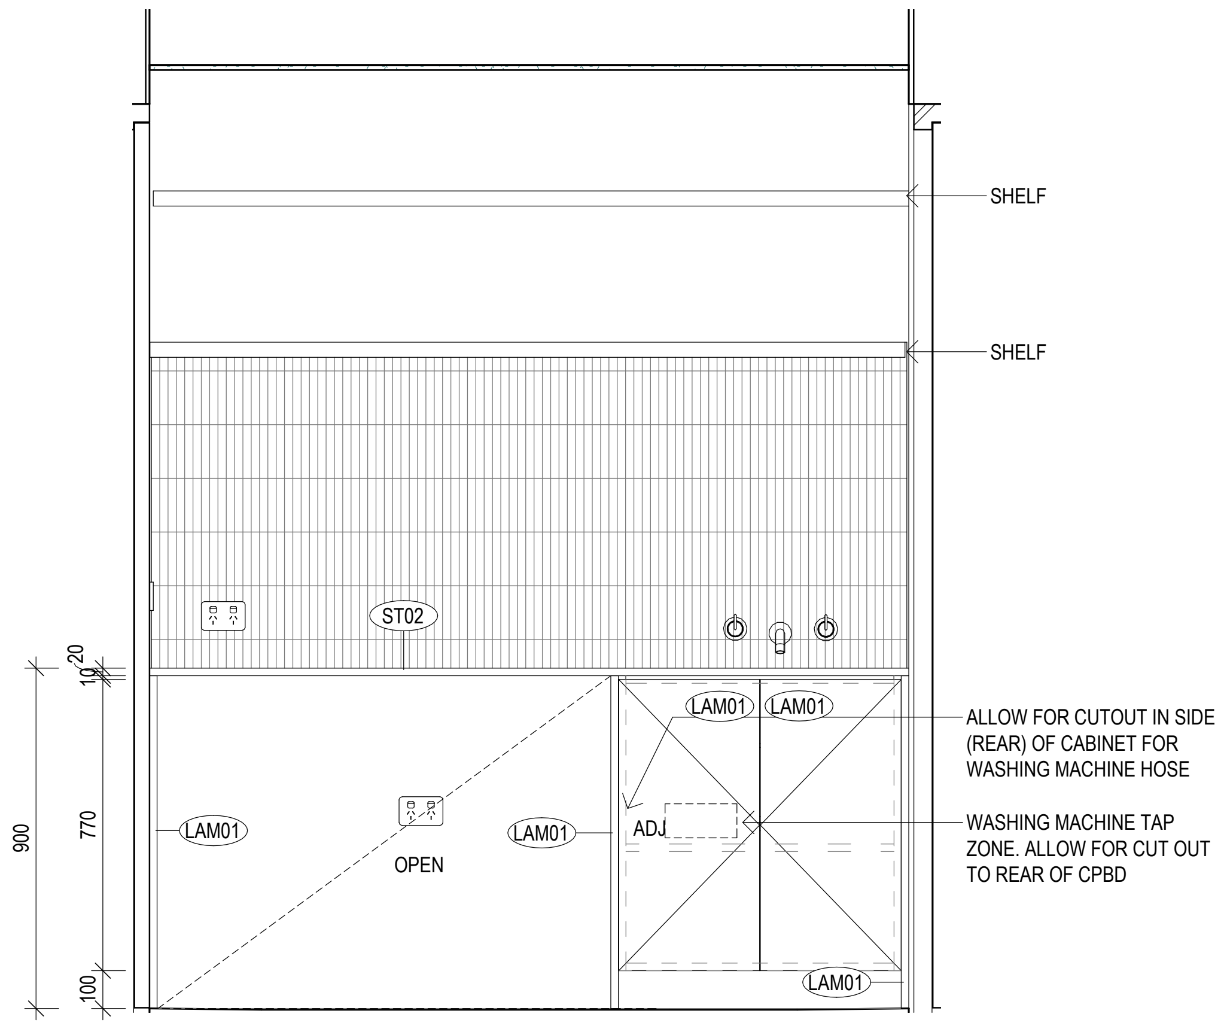
SHELF
SHELF
ST02
LAM01
OPEN
ADJ
ALLOW FOR CUTOUT IN SIDE (REAR) OF CABINET FOR WASHING MACHINE HOSE
WASHING MACHINE TAP ZONE. ALLOW FOR CUT OUT TO REAR OF CPBD
20
10
900
770
100

6 / 106 J03 - LAUNDRY ELEVATION
1 : 20

NOTE: PROPRIETARY HANDLES TBC

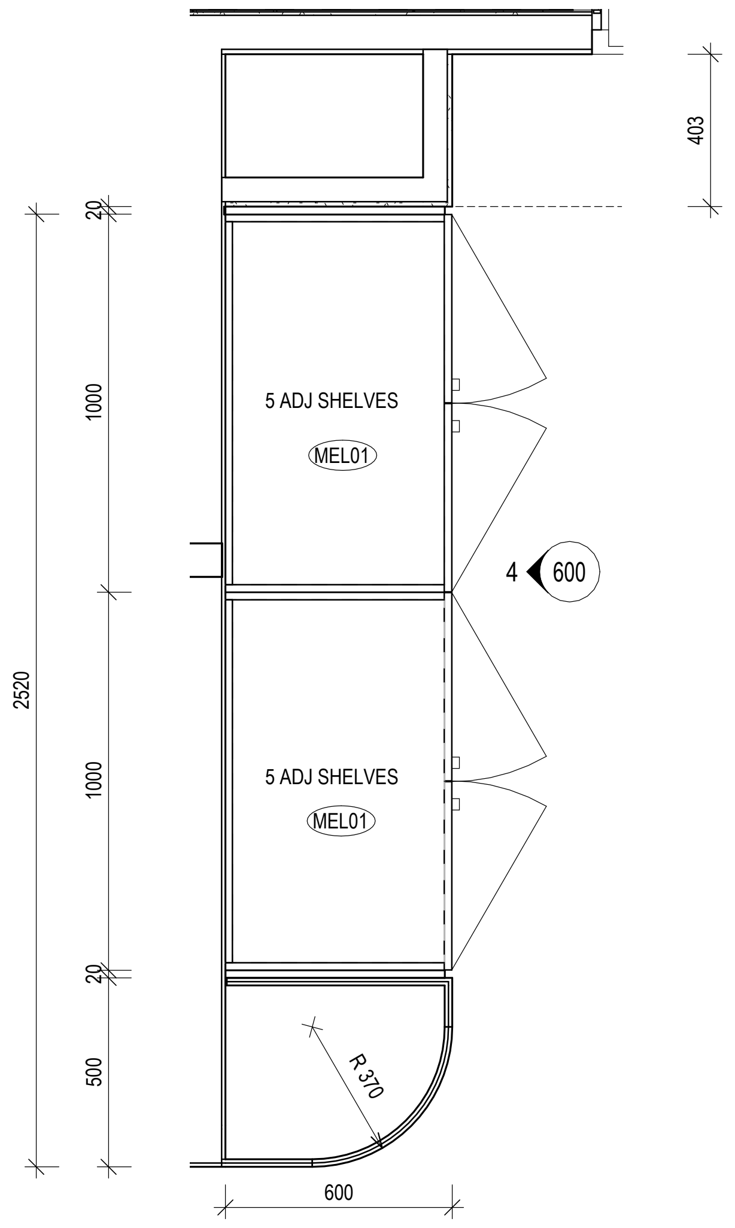

3 / 203 J06 - LIVING ROOM JOINERY
1 : 20

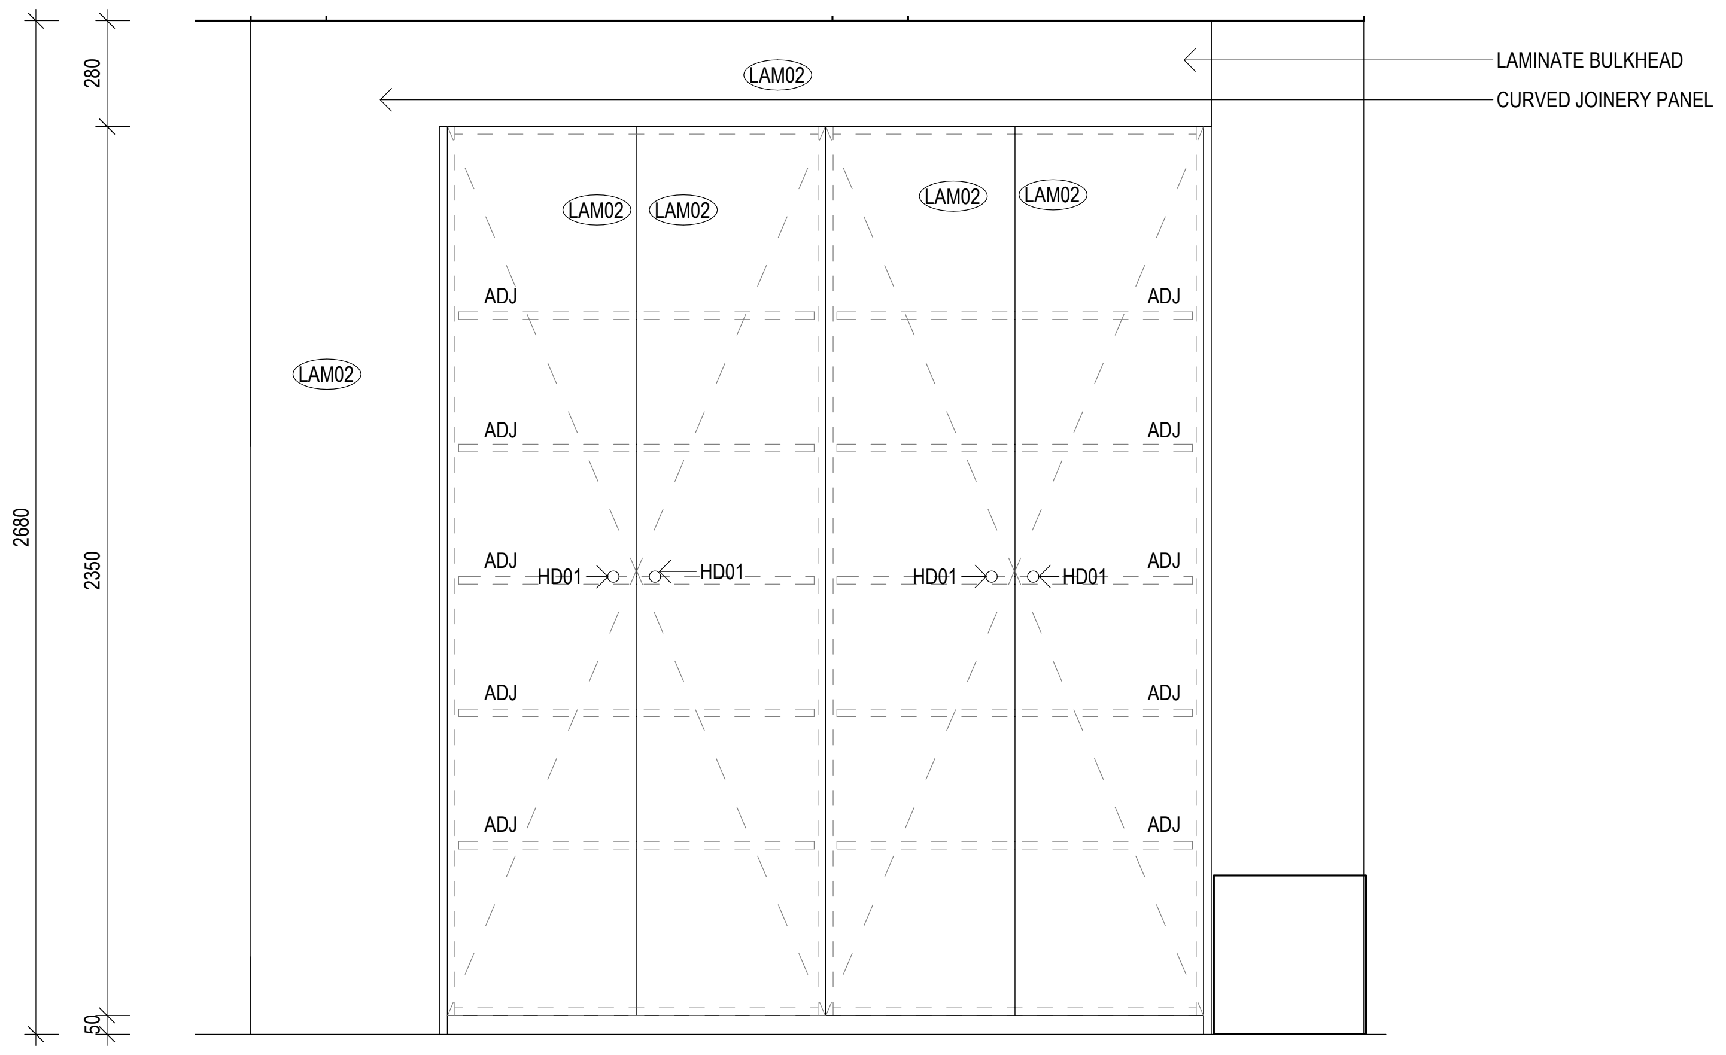

4 / 106 J06 - LIVING ROOM JOINERY - ELEVATION
1 : 20

NOTE: PROPRIETARY HANDLES TBC

C:\Users\KatherineB\OneDrive - nettletontribe\38 Howard\Revit\Concstruction\38 HOWARD_PROPOSED_ARCH (1).rvt

16/08/2026 8:17:26 PM

Client

Client Logo

Issue	Description	Date
A	JOINERY ISSUE 1	16-08-2026

Builder and/or subcontractors shall verify all project dimensions before commencing on-site work or off-site fabrication. Figured dimensions shall take precedence over scaled dimensions. This drawing is copyright and cannot be reproduced in whole or in part or by any medium without the written permission of Katherine Blackham.

Builder

Builders Logo

Project Name
38 Howard Street
Project Address
38 Howard Street, Grange QLD

Key Plan
0 2000 5000

Drawing Title:
JOINERY - J01

Checker: **KB**
Sheet Size: **A1**
Scale: **1:10**
Drawing Number: **2025-01_600**
Issue: **A**

FINISHES

LAM01 - LAMINEX ELEGANT OAK
LAM02 - LAMINEX ARIES. COLOUR TBC
ST01 - BRECCIATE PRIMAVERA MARBLE
ST02 - YDL MAHAL IVORY
MEL01 - WHITE MELAMINE INTERNAL CARCASS

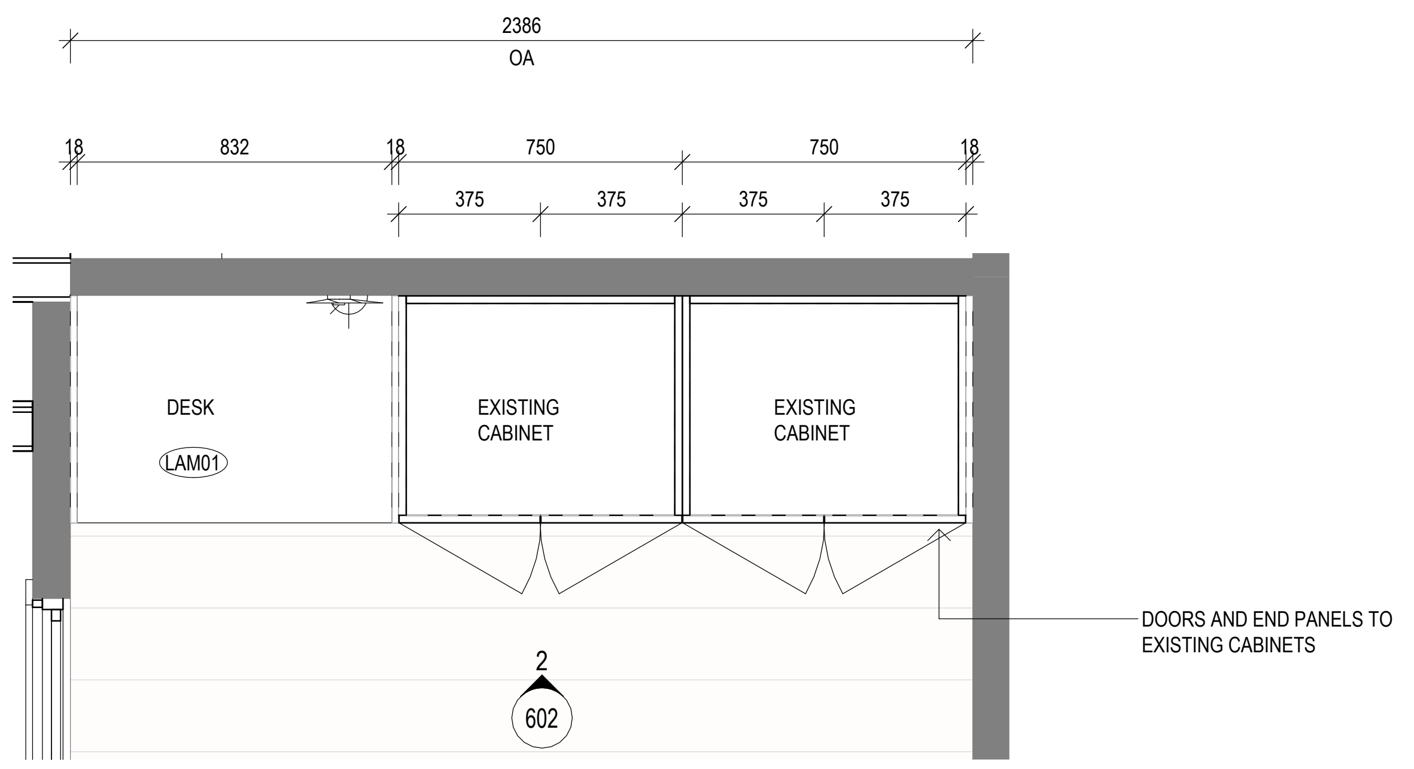

1 / 203 J07 - PLAYROOM JOINERY
1 : 20

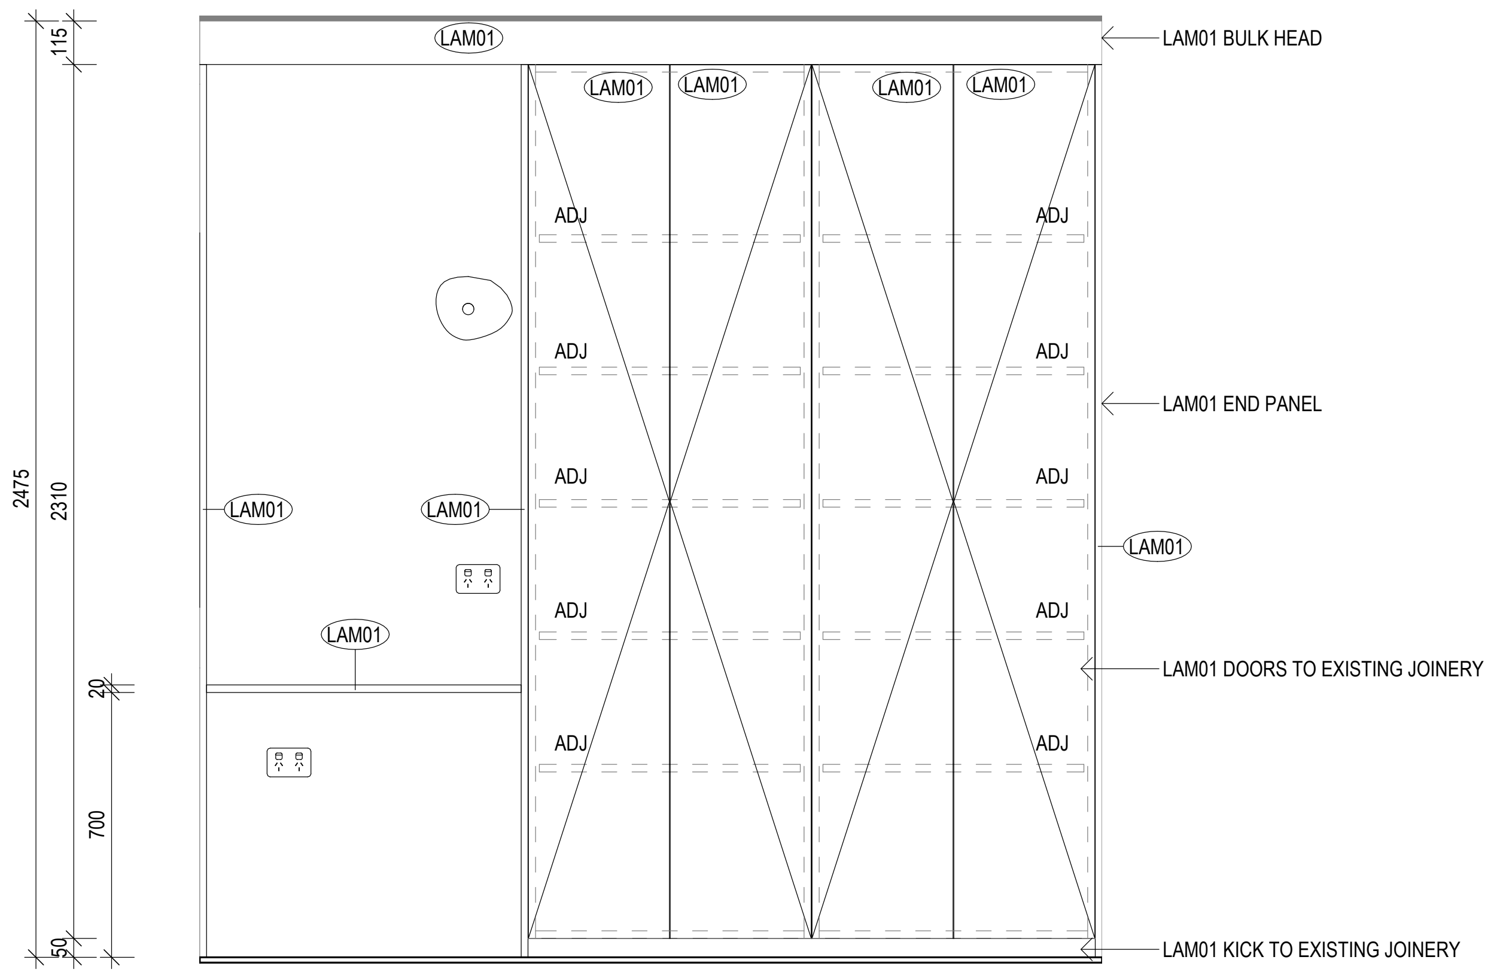

2 / 104 J07 - PLAYROOM JOINERY - ELEVATION
1 : 20

NOTE: PROPRIETARY HANDLES TBC

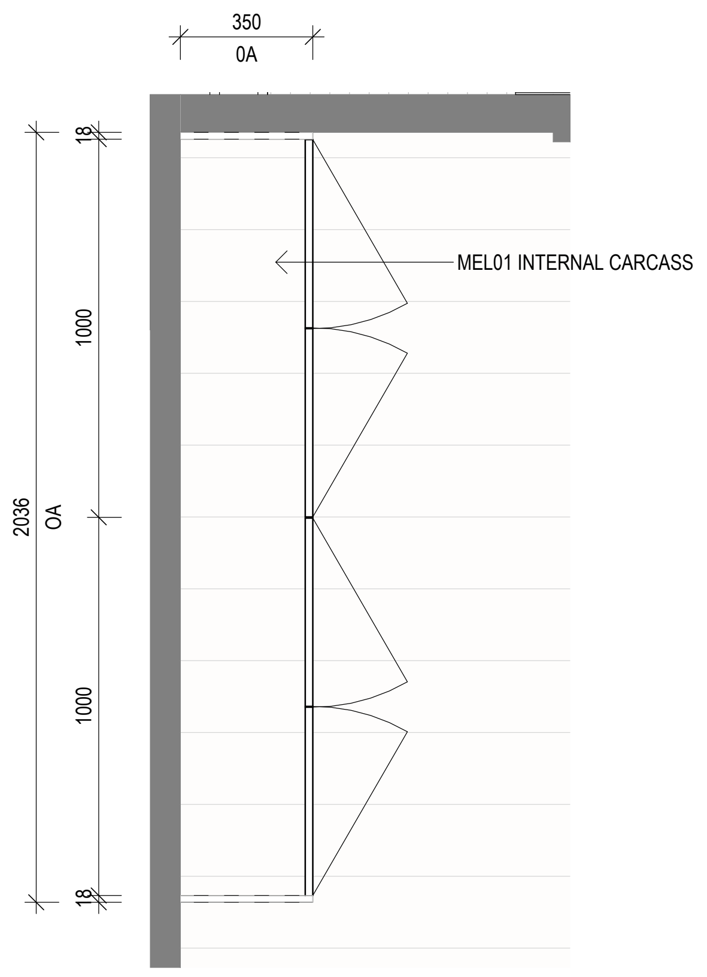

4 / 203 J08 - BED 2
1 : 20

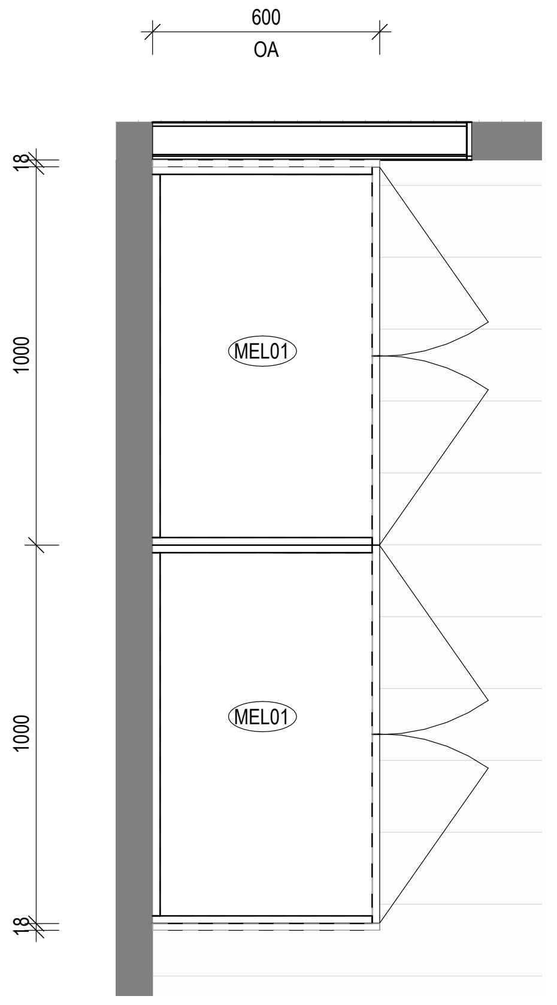

5 / 203 J08 - BED 3
1 : 20

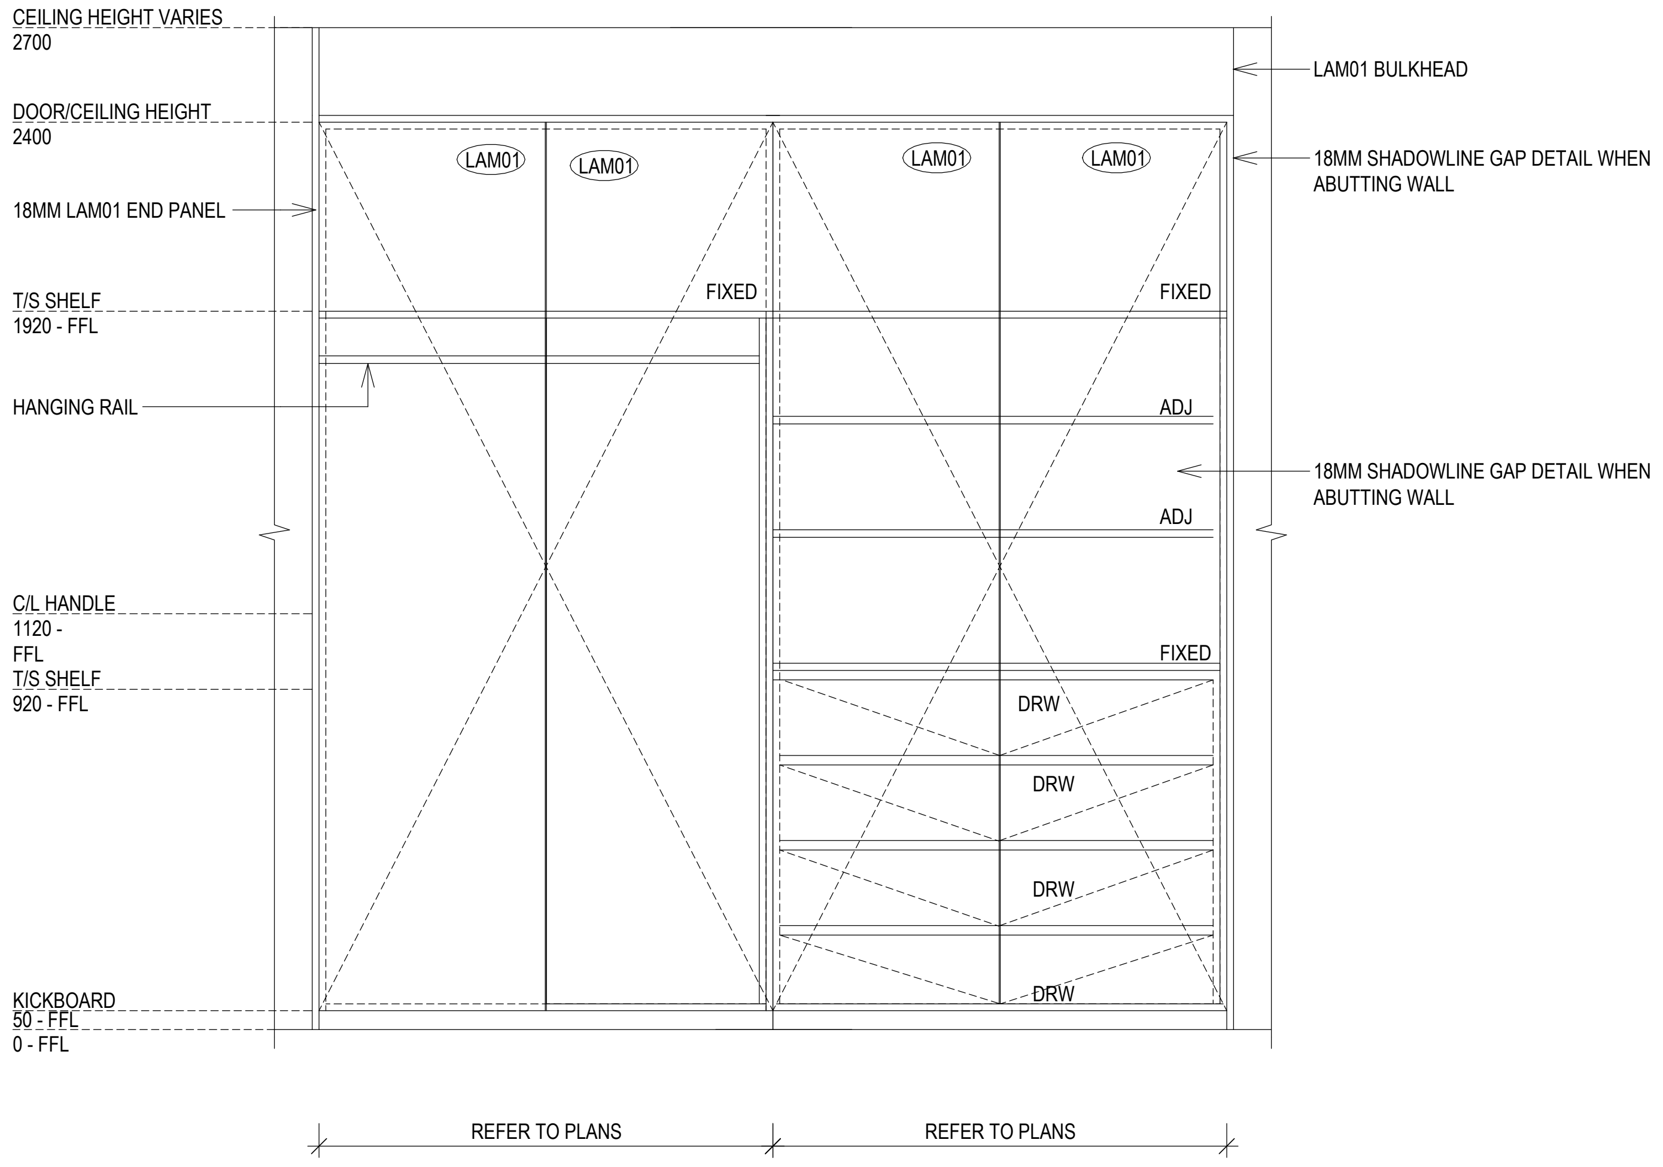

3 J08 - 2 CUPBOARD ROBE - ELEVATION
1 : 20

NOTE: PROPRIETARY HANDLES TBC

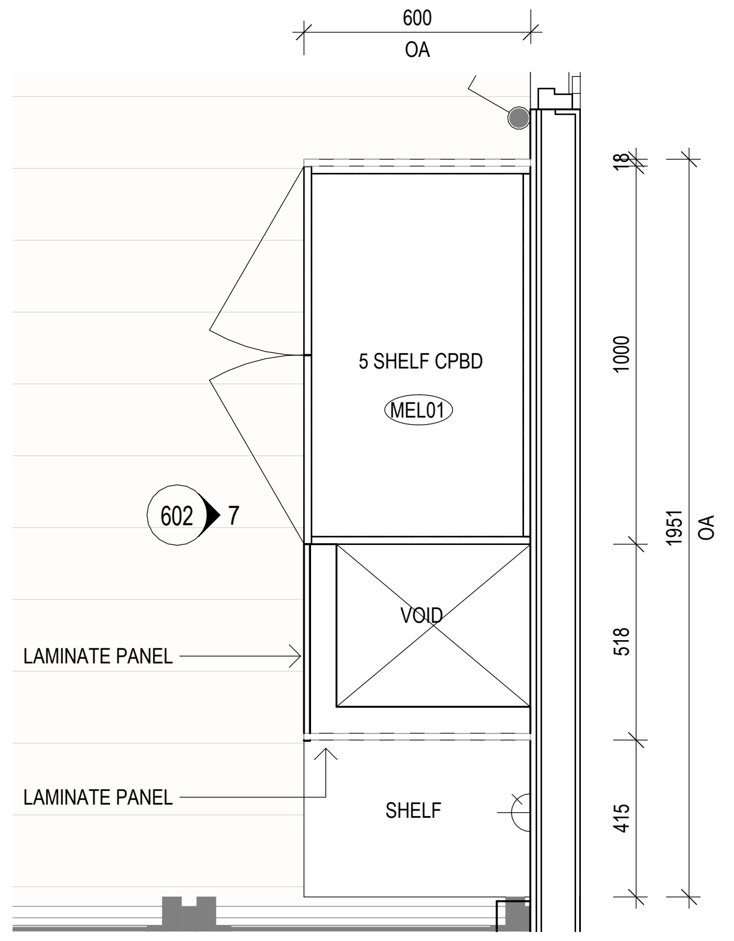

6 / 203 J10 - STORAGE
1 : 20

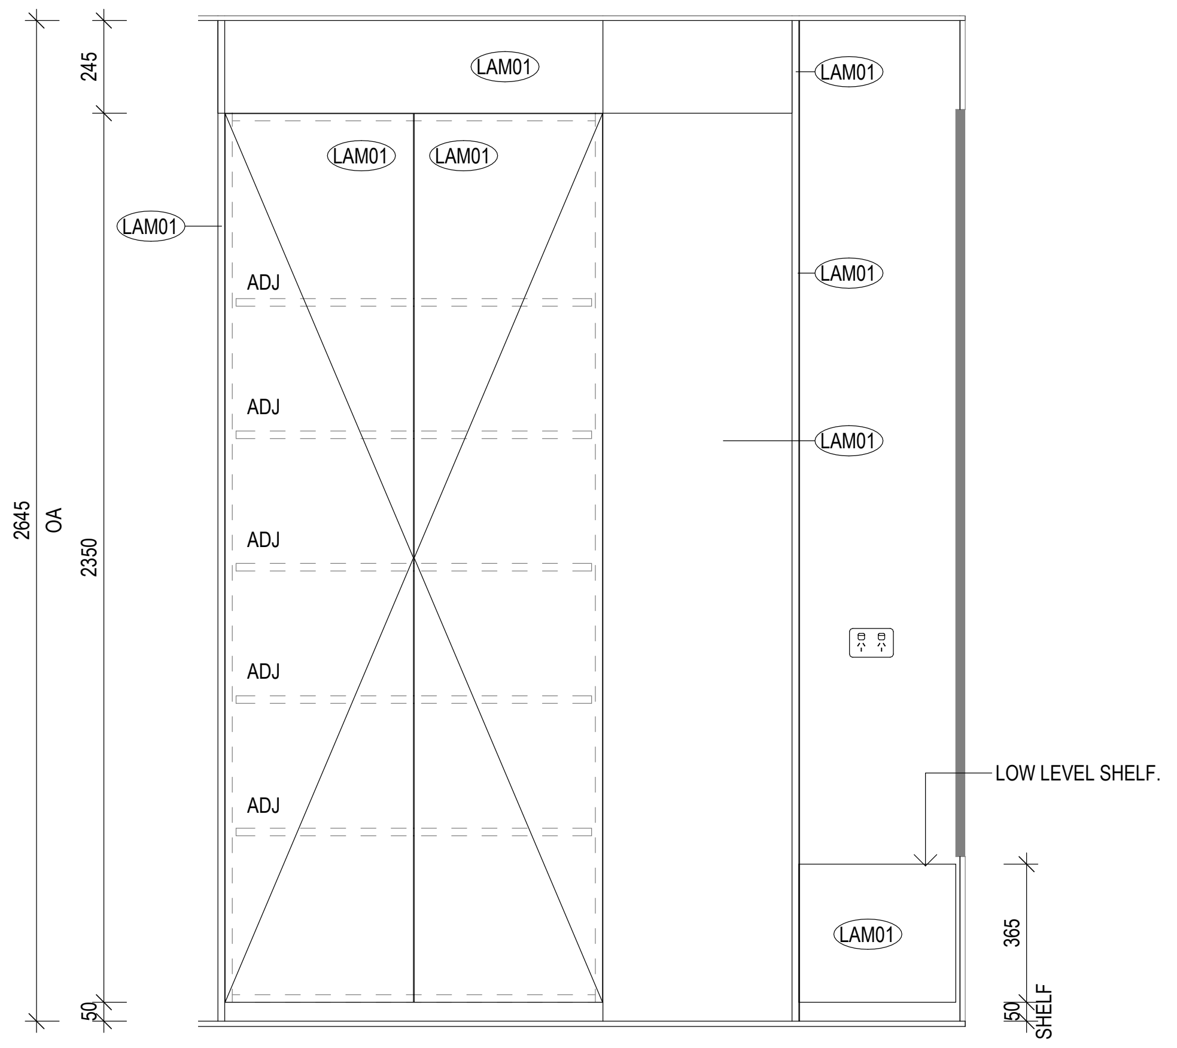

7 / 104 J10 - STORAGE - ELEVATION

NOTE: PROPRIETARY HANDLES TBC

Client

Client Logo

Issue	Description	Date
A	JOINERY ISSUE 1	16-08-2026

Builder and/or subcontractors shall verify all project dimensions before commencing on-site work or off-site fabrication. Figured dimensions shall take precedence over scaled dimensions. This drawing is copyright and cannot be reproduced in whole or in part or by any medium without the written permission of Katherine Blackham.

Builder

Builders Logo

Project Name
38 Howard Street
Project Address
38 Howard Street, Grange QLD

Key Plan
0 2000 5000

Drawing Title:
JOINERY

Checker: **KB**
Sheet Size: **A1**
Scale: **1:20**
Drawing Number: **2025-01_602**
Issue: **A**

16/08/2026 8:17:28 PM C:\Users\KatherineB\OneDrive - nettletontribe\38 Howard\Revit\Concstruction\38 HOWARD_PROPOSED_ARCH (1).rvt

FINISHES

LAM01 - LAMINEX ELEGANT OAK
LAM02 - LAMINEX ARIES. COLOUR TBC
ST01 - BRECCIATE PRIMAVERA MARBLE
ST02 - YDL MAHAL IVORY
MEL01 - WHITE MELAMINE INTERNAL CARCASS

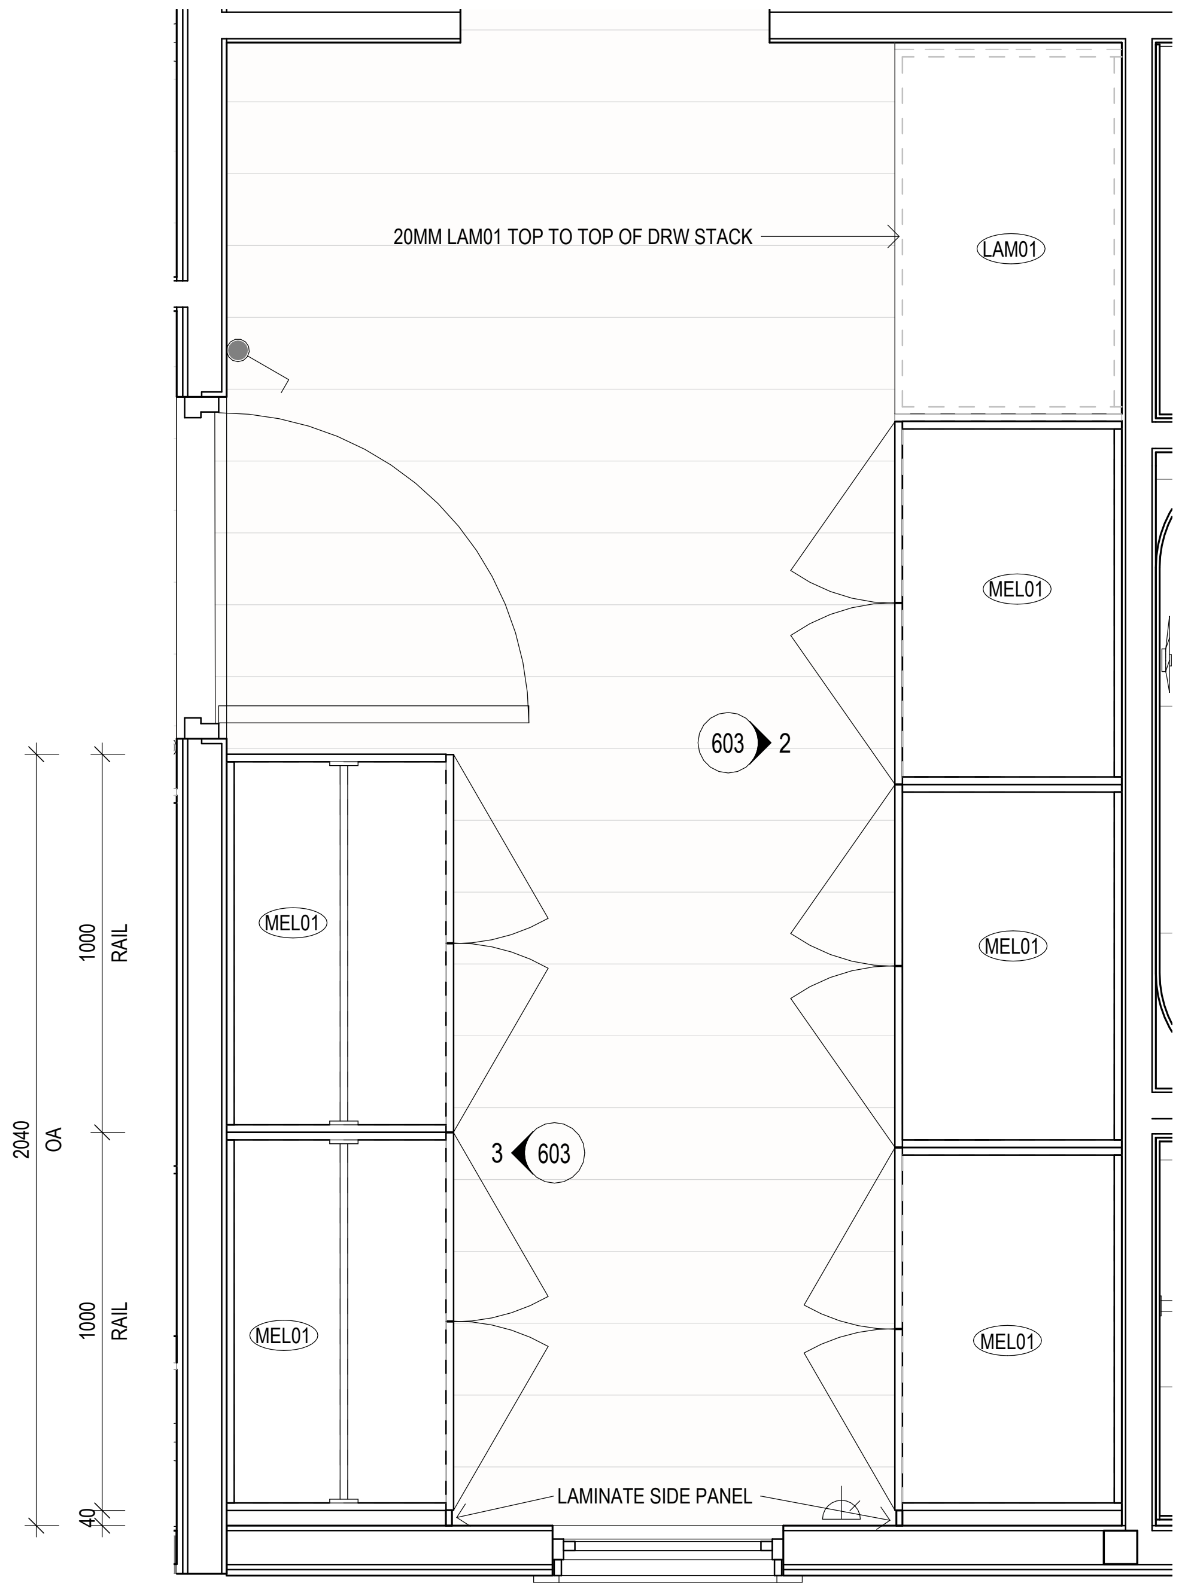

1 203 J11 - WIR
1 : 20

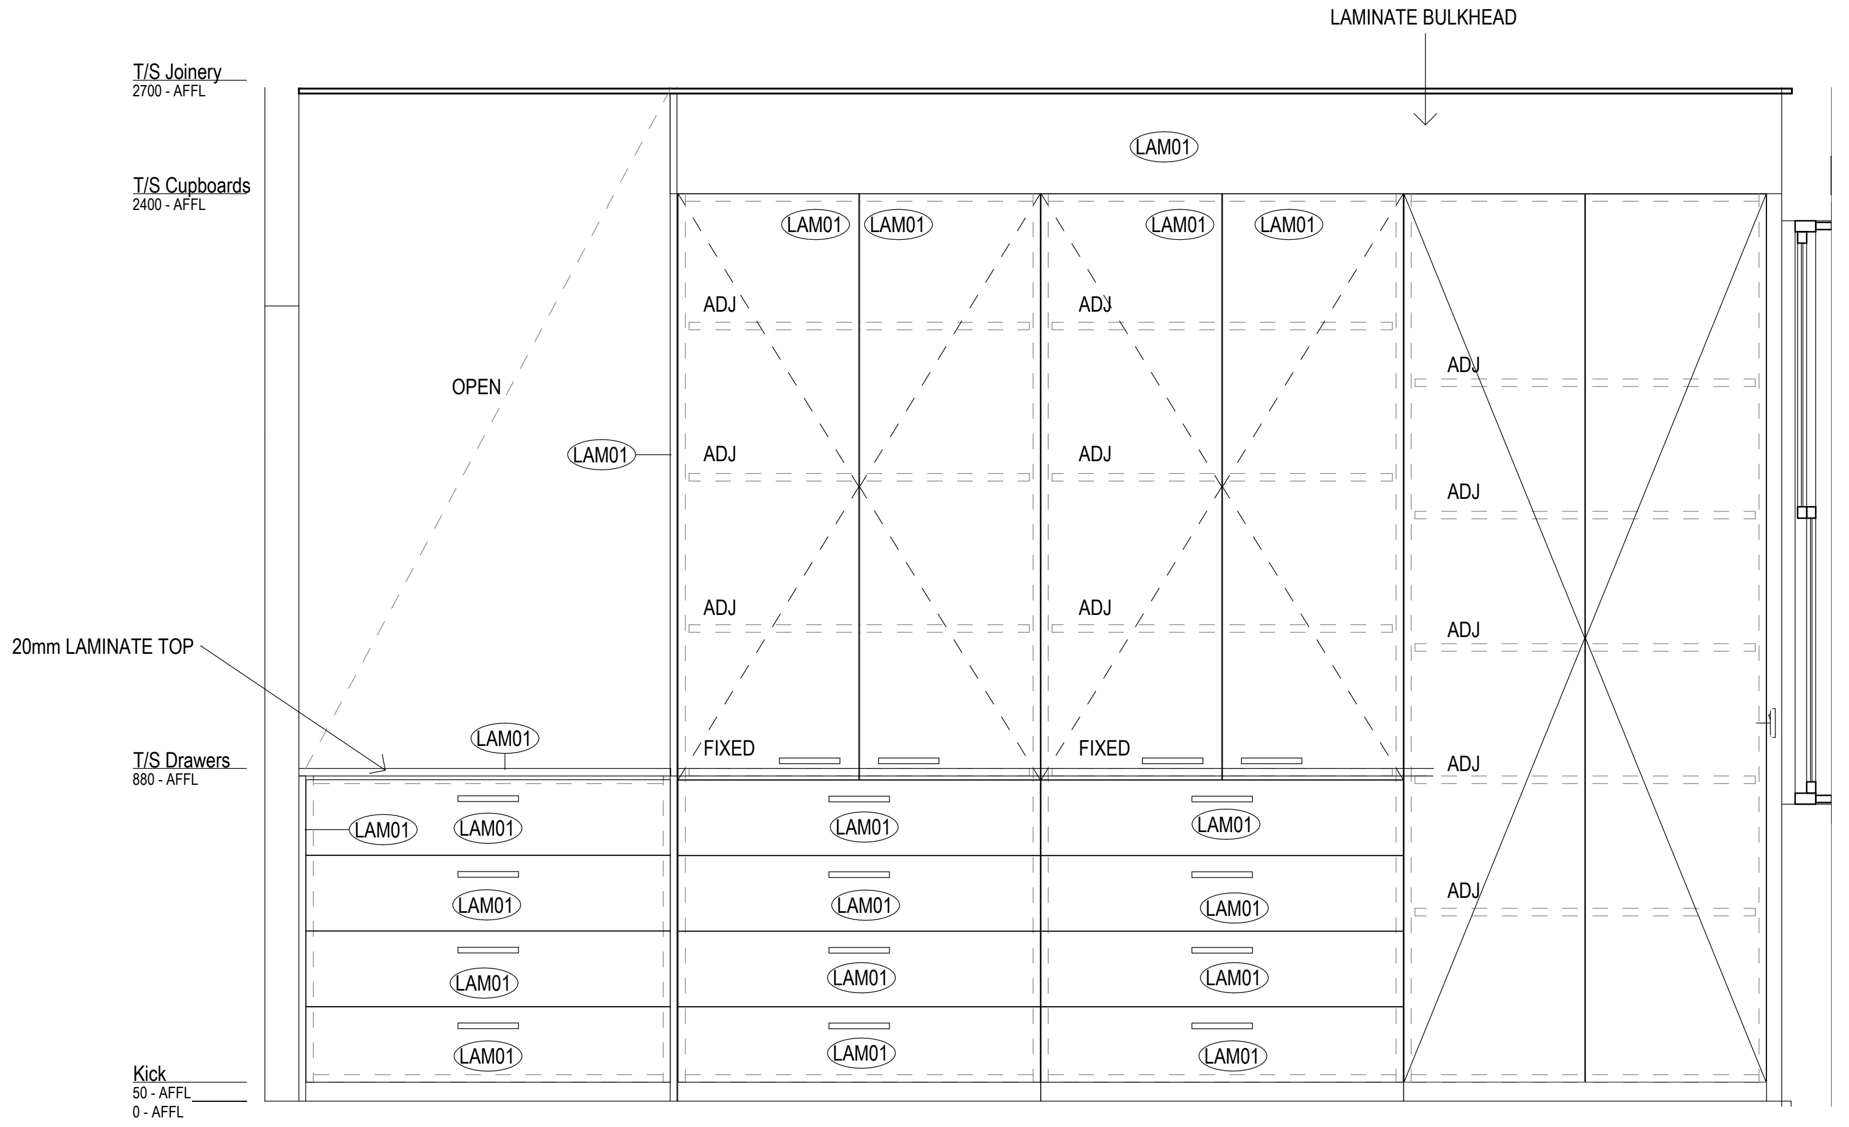

2 104 J11 - WIR ELEVATION A
1 : 20

NOTE: PROPRIETARY HANDLES TBC

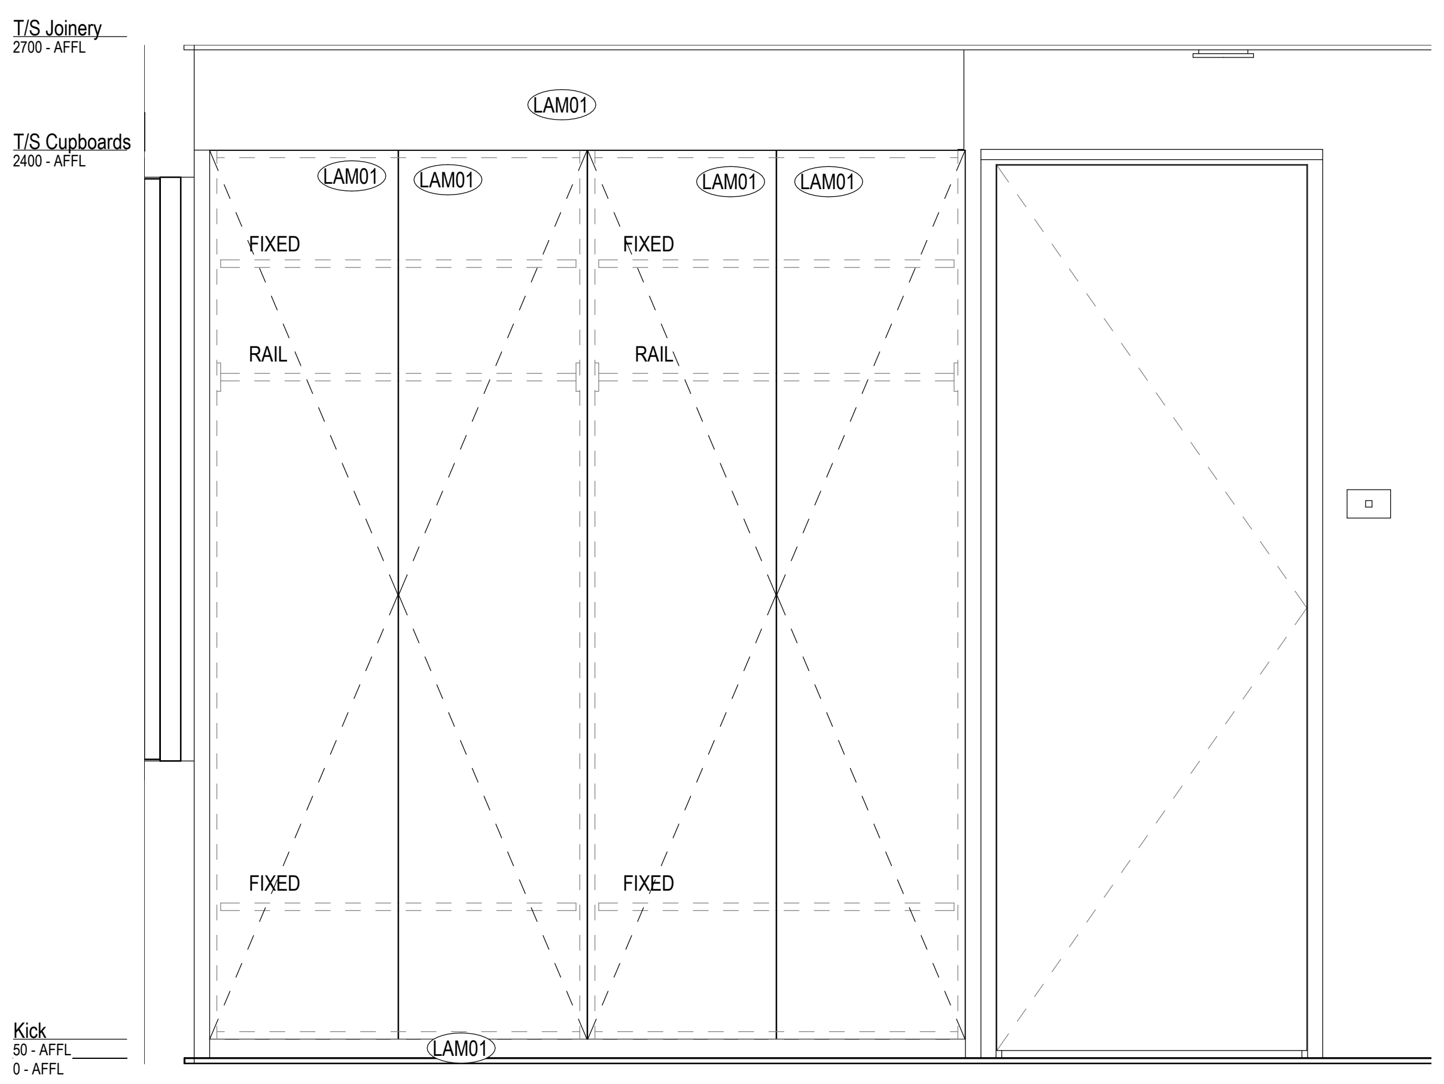

3 104 J11 - WIR - ELEVATION B
1 : 20

NOTE: PROPRIETARY HANDLES TBC

16/08/2026 8:17:30 PM C:\Users\KatherineB\OneDrive - nettletontribe\38 Howard\Revit\Concstruction\38 HOWARD_PROPOSED_ARCH (1).rvt

Client

Client Logo

Issue	Description	Date
A	JOINERY ISSUE 1	16-08-2026

Builder and/or subcontractors shall verify all project dimensions before commencing on-site work or off-site fabrication. Figured dimensions shall take precedence over scaled dimensions. This drawing is copyright and cannot be reproduced in whole or in part or by any medium without the written permission of Katherine Blackham.

Builder

Builders Logo

Project Name
38 Howard Street
Project Address
38 Howard Street, Grange QLD

Key Plan
0 400 1000

Drawing Title:
JOINERY

Checker: **KB**
Sheet Size: **A1**
Scale: **1:20**
Drawing Number: **2025-01_603**
Issue: **A**