


Bench Seat Plan 1 : 20
Bench Seat Elev 2 1 : 20
Bench Seat 3D 1 : 10

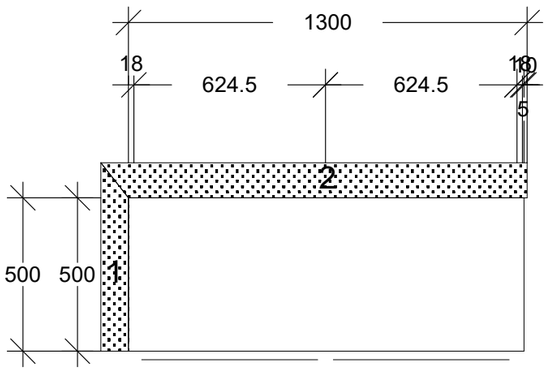

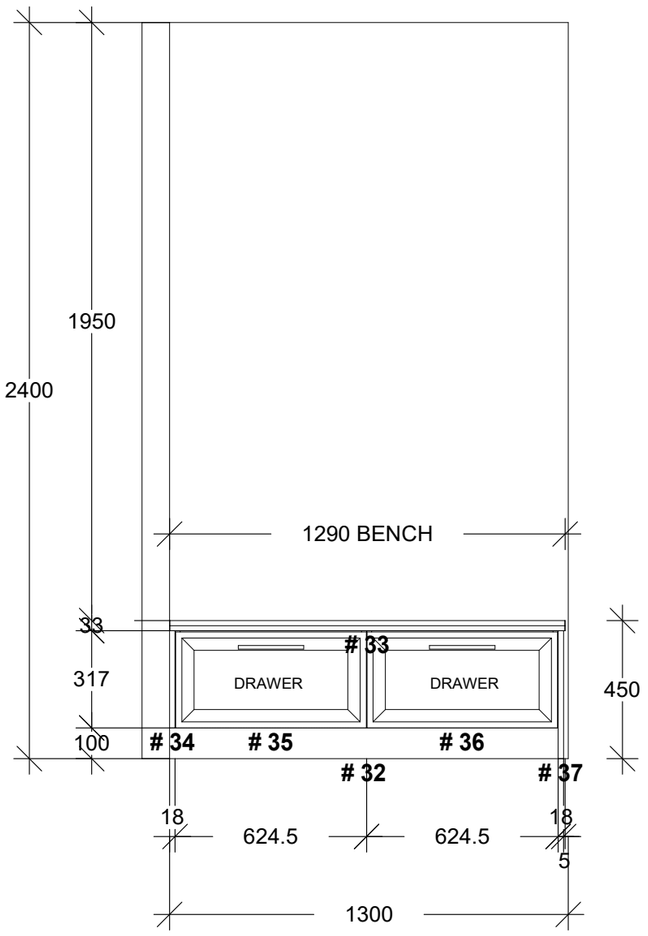

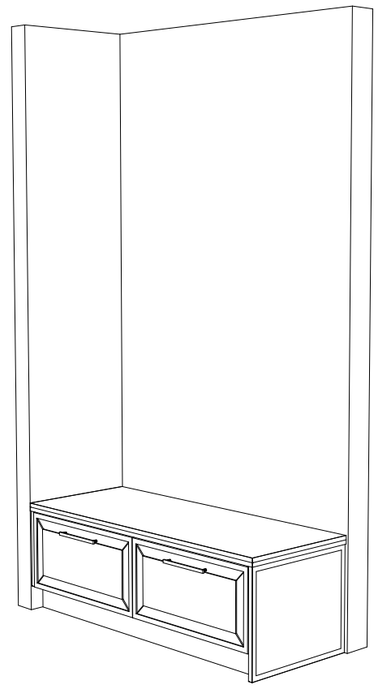

BENCH TOPS : 33mm Polytec Boston Oak WM

INTERNAL CARCASE COLOUR: 16mm Whiteboard

BASE DOOR COLOUR : 21mm 2pac Shaker Style Taubmans Almond Milk Satin

HANDLES : C247 - Linear Montrose Cabinet Handle - Antique Bronze Finish 192mm Centre

KICKS : To Match Doors Above

HARDWARE :

BLUM SOFT CLOSE HINGES
NIKPOL DRAGON PRO SOFT CLOSE DRAWERS

Client Approved Signature : ..... Date : .....

Kitchens By Resident Hero
32 Gateway Drive
Noosaville, QLD 4566
Phone: Fax:
www.residenthero.com.au

RHK6406 Tanya Rataj -	**Scale:**	**Sheet 1 of 11**
Joinery	Do not scale off this drawing.	Drawn By:
20 Kyle Crt Doonan	, ,	Date: 16/06/26

All drawings are copyright & are owned & controlled by Kitchens By Resident Hero

Linen Elev 2
Linen Plan
Linen 3D

1 : 20
1 : 20
1 " = 1 '

INTERNAL CARCASE COLOUR: 16mm Whiteboard

BASE DOOR COLOUR : 21mm 2pac Shaker Style
Taubmans Almond Milk Satin


HANDLES : C247 Linear Montrose 320mm Antique Bronze


KICKS : To Match Doors Above

HARDWARE :

BLUM SOFT CLOSE HINGES
NIKPOL DRAGON PRO SOFT CLOSE DRAWERS



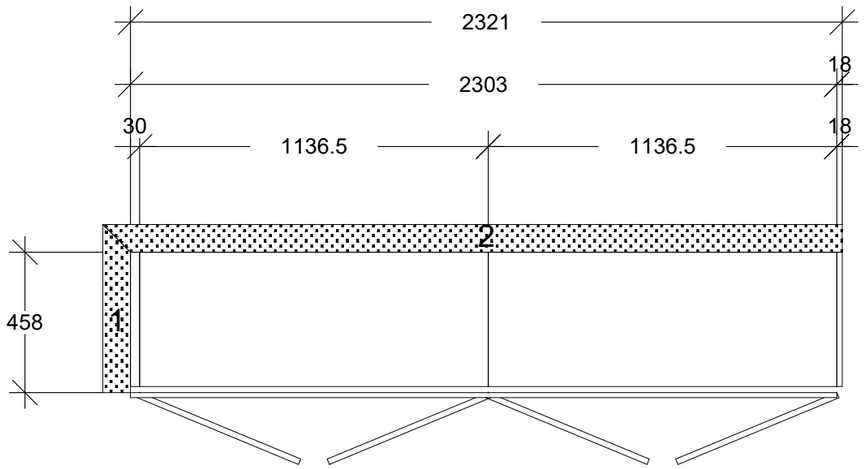

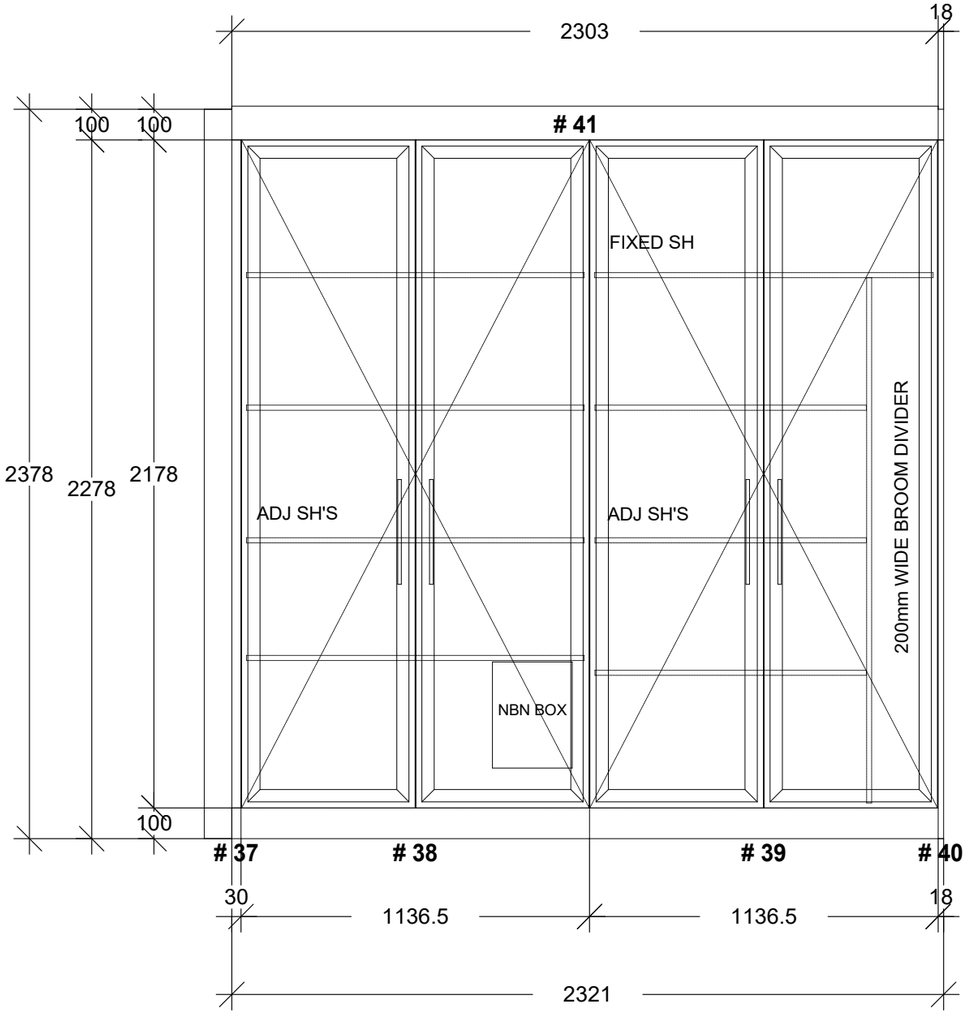


Client Approved Signature : ..... Date : .....

RESIDENT HERO
Kitchens By Resident Hero
32 Gateway Drive
Noosaville, QLD 4566
Phone: Fax:
www.residenthero.com.au

RHK6406 Tanya Rataj -	**Scale:**	**Sheet 2 of 11**
Joinery	Do not scale off this drawing.	Drawn By:
20 Kyle Crt Doonan	, ,	Date: 16/06/26

All drawings are copyright & are owned & controlled by Kitchens By Resident Hero

Coffee Nook 3D 1 : 10
Coffee Nook Plan 1 : 20

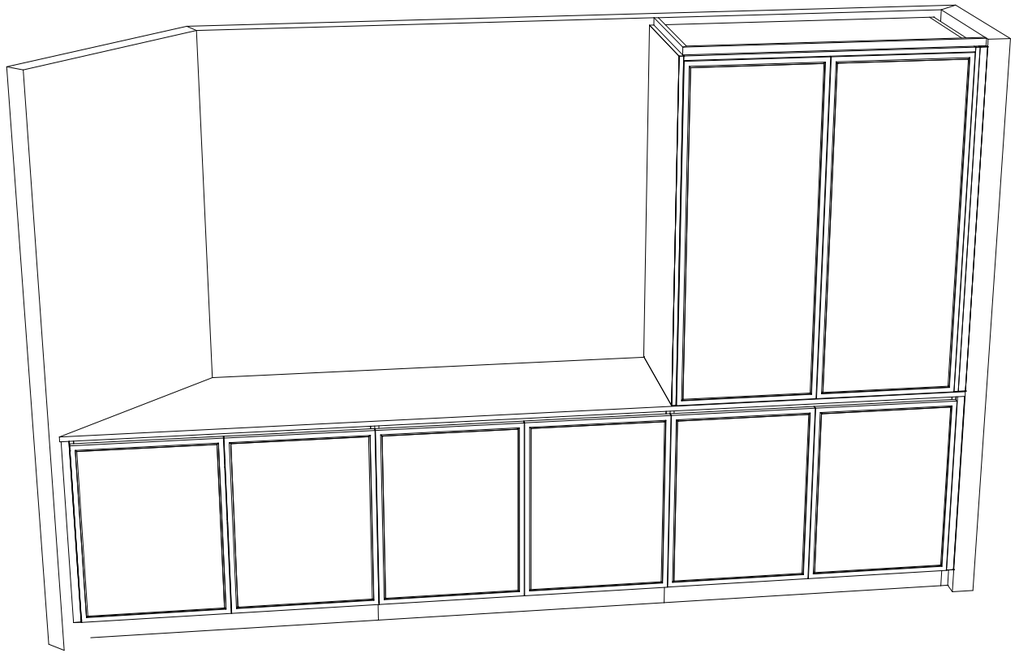

BENCH TOPS : 20mm Stone Ambassador " Le Taj "
Including Pocket Door Cupboard

POCKET DOOR INTERNAL
CARCASS COLOUR : 16mm Polytec Boston Oak WM

INTERNAL CARCASE COLOUR: 16mm Whiteboard

BASE DOOR COLOUR : 21mm 2pac Shaker Style
Taubmans Almond Milk Satin


HANDLES : Fingerpull - Setback
Pocket Door Handles - C247 Linear
Montrose 320mm Antique Bronze

KICKS : To Match Doors Above

HARDWARE :

BLUM SOFT CLOSE HINGES
NIKPOL DRAGON PRO SOFT CLOSE DRAWERS
POCKET DOOR

LED LIGHTS TO UNDERSIDE OF 2x SHELVES IN
POCKET DOOR CABINET

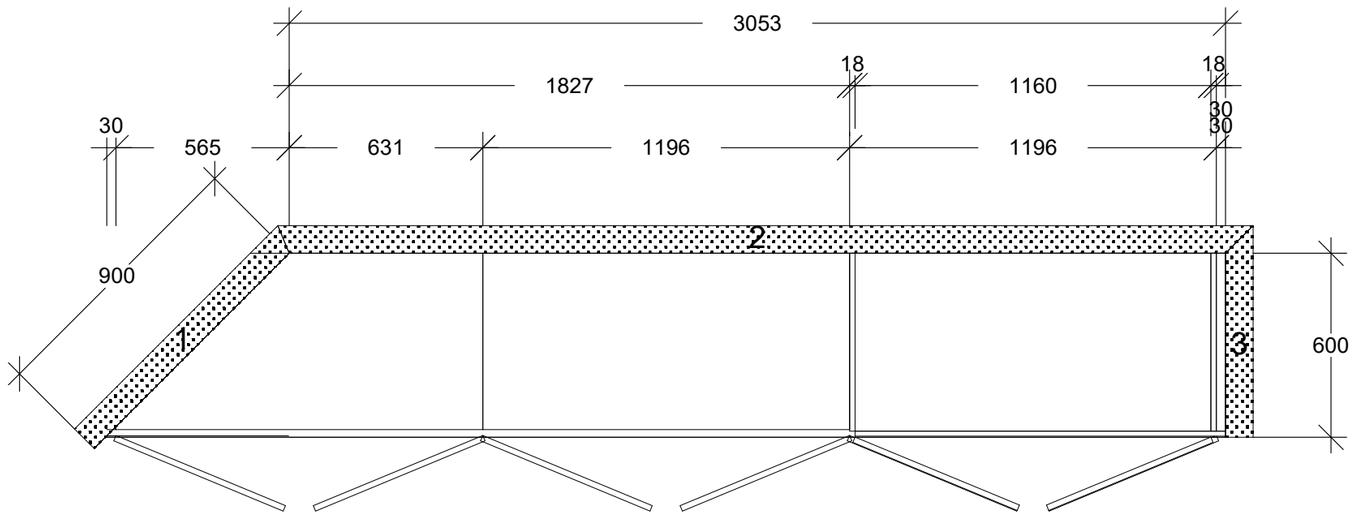

Client Approved Signature : ..... Date : .....


Kitchens By Resident Hero
32 Gateway Drive
Noosaville, QLD 4566
Phone: Fax:
www.residenthero.com.au

RHK6406 Tanya Rataj -	**Scale:**	**Sheet 3 of 11**
Joinery	Do not scale off this drawing.	Drawn By:
20 Kyle Crt Doonan	, ,	Date: 16/06/26

All drawings are copyright & are owned & controlled by Kitchens By Resident Hero

Coffee Nook Elev 2

1 : 20

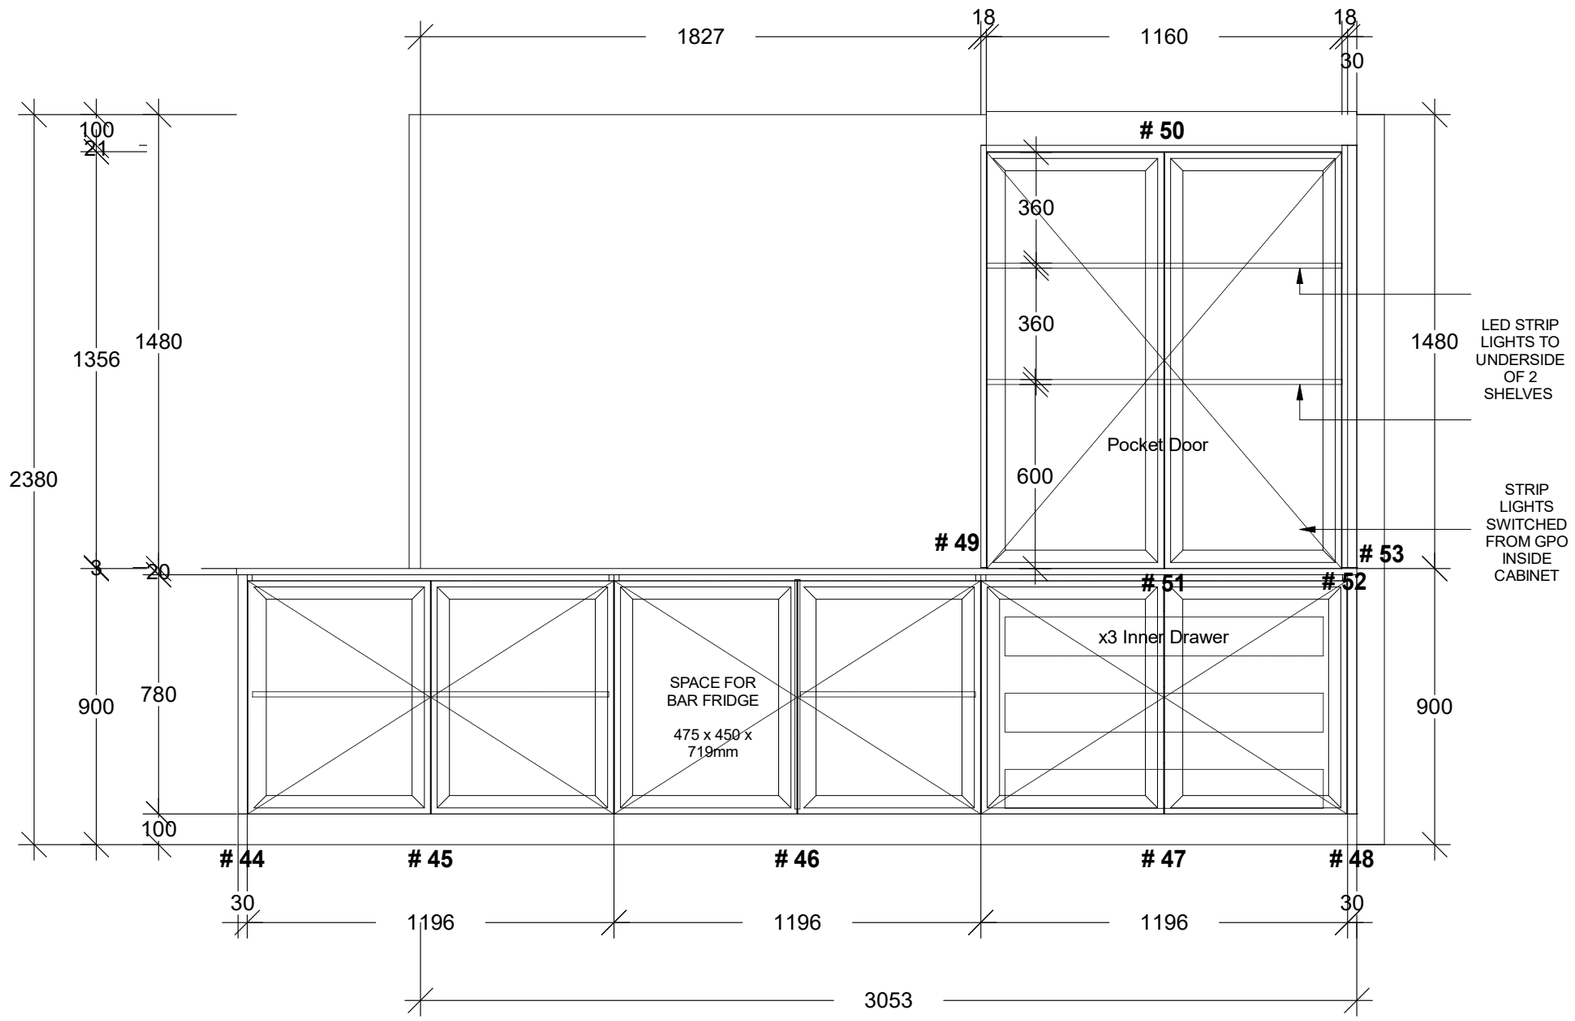

Client Approved Signature : ..... Date : .....

Kitchens By Resident Hero 32 Gateway Drive Noosaville, QLD 4566 Phone: Fax: www.residenthero.com.au	RHK6406 Tanya Rataj -	**Scale:1 : 20**	**Sheet 4 of 11**
	Joinery	Do not scale off this drawing.	Drawn By:
	20 Kyle Crt Doonan	, ,	Date: 16/06/26

All drawings are copyright & are owned & controlled by Kitchens By Resident Hero

Kitchen Plan

1 : 20

BENCH TOPS : 20mm Stone Ambassador " Le Taj "

ISLAND BENCHTOP : 20mm Stone Ambassador " Le Taj " with 2x Waterfall Ends

INTERNAL CARCASE COLOUR: 16mm Whiteboard

BASE DOOR COLOUR : 21mm 2pac Shaker Style
Taubmans Almond Milk Satin

TALL DOOR & ISLAND
BASE DOOR COLOUR: 16mm Polytec Boston Oak WM


BULKHEAD: 100mm High - Finished in 2pac - Flush with Carcase

HANDLES : Fingerpull - Setback on all shaker doors
TALL DOORS - Momo "linear" Appliance Pull 320mm in Antique Bronze
ISLAND - Intergrated Angled Handle

KICKS : To Match Doors Above

HARDWARE :

BLUM SOFT CLOSE HINGES
NIKPOL DRAGON PRO SOFT CLOSE DRAWERS

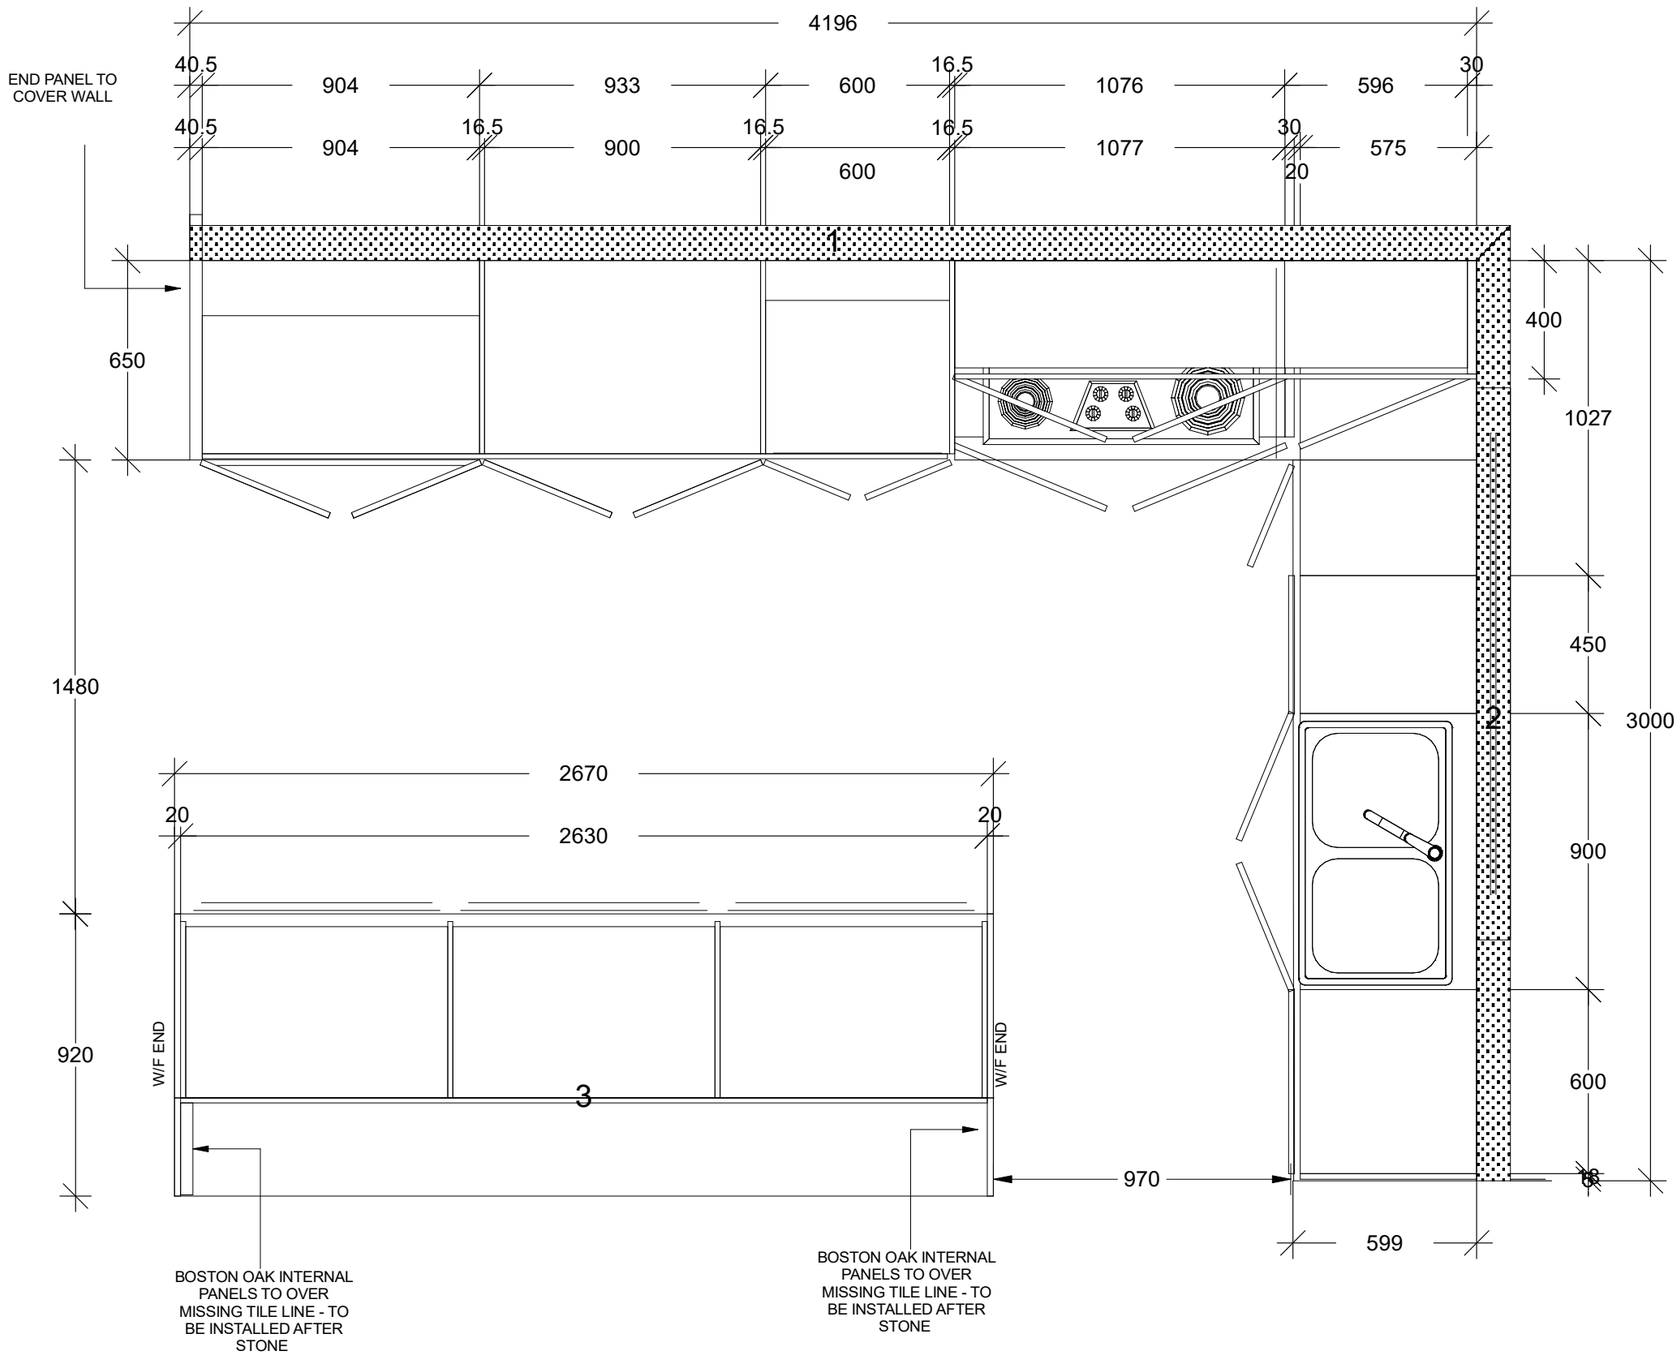

Client Approved Signature : ..... Date : .....


Kitchens By Resident Hero
32 Gateway Drive
Noosaville, QLD 4566
Phone: Fax:
www.residenthero.com.au

RHK6406 Tanya Rataj -	**Scale:1 : 20**	**Sheet 5 of 11**
Joinery	Do not scale off this drawing.	Drawn By:
20 Kyle Crt Doonan	, ,	Date: 16/06/26

All drawings are copyright & are owned & controlled by Kitchens By Resident Hero

Kitchen Elev 1

1 : 20

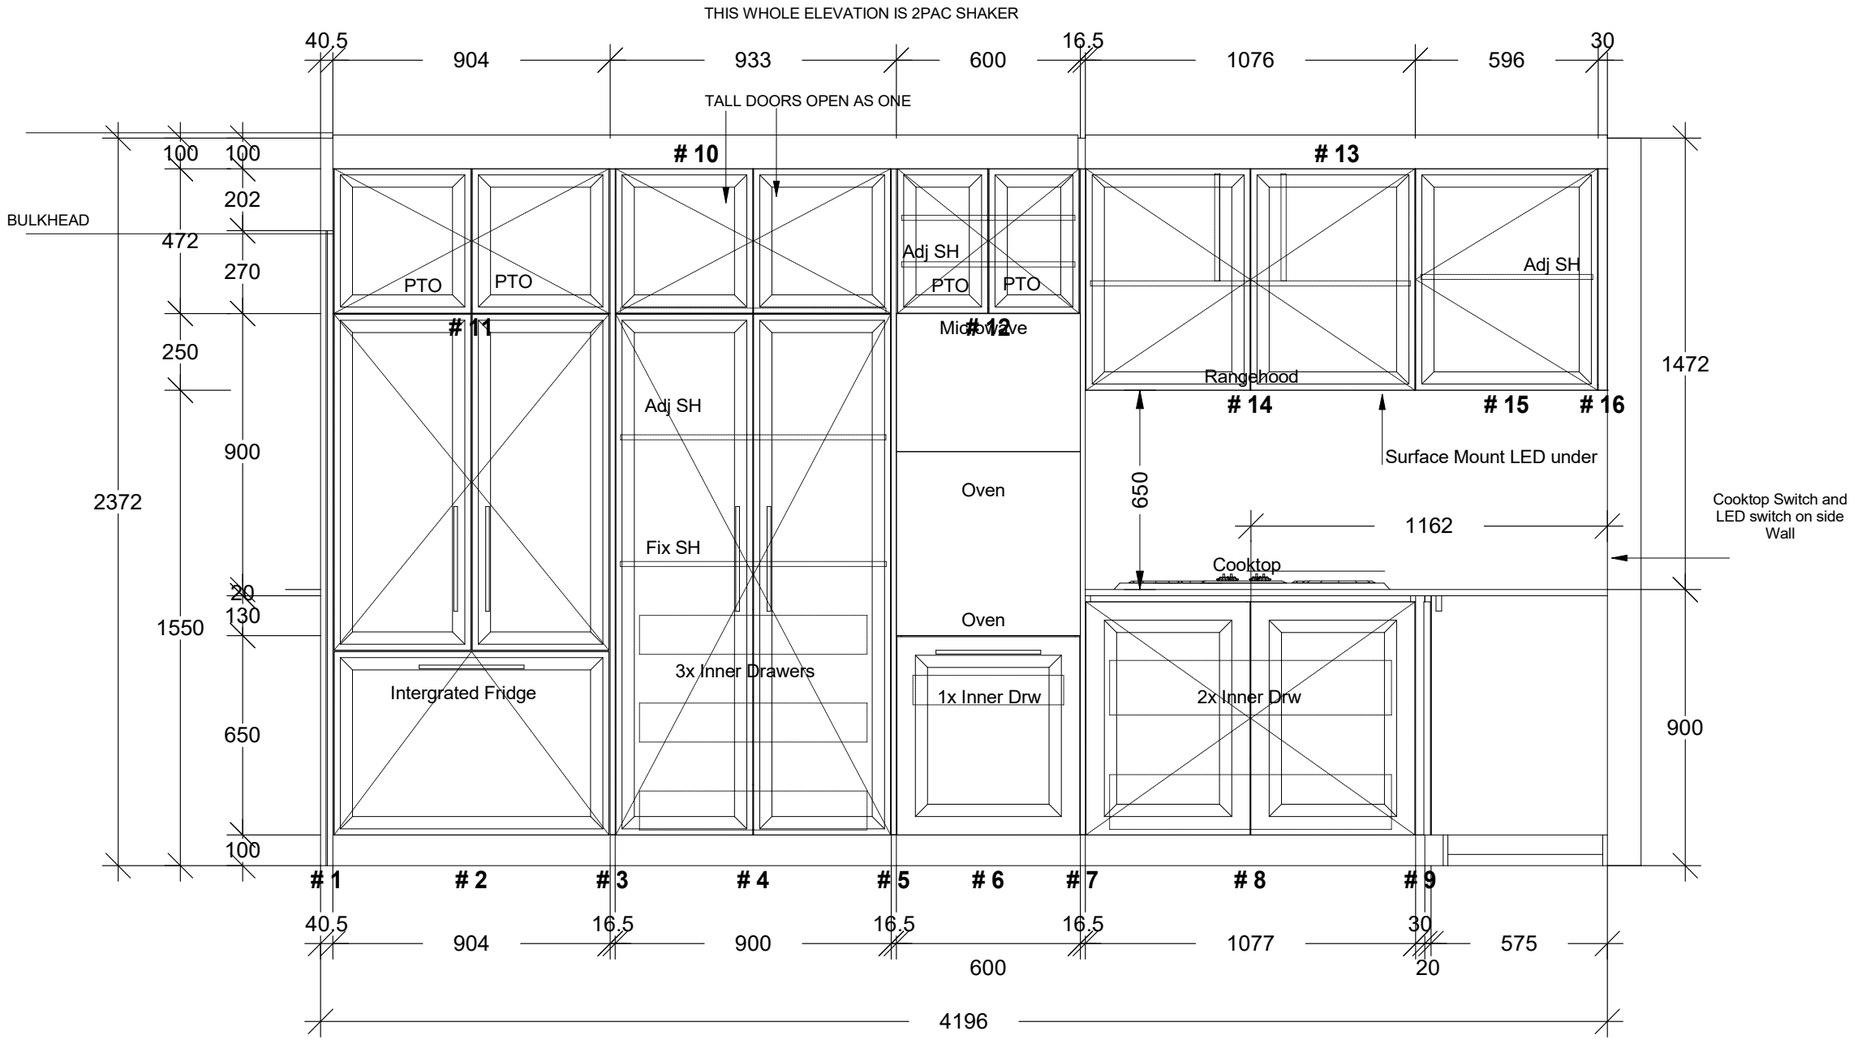



Client Approved Signature : ..... Date : .....


Kitchens By Resident Hero 32 Gateway Drive Noosaville, QLD 4566 Phone: Fax: www.residenthero.com.au	RHK6406 Tanya Rataj -	**Scale:1 : 20**	**Sheet 6 of 11**
	Joinery	Do not scale off this drawing.	Drawn By:
	20 Kyle Crt Doonan	, ,	Date: 16/06/26

All drawings are copyright & are owned & controlled by Kitchens By Resident Hero

Kitchen Elev 2 1 : 20
Kitchen Elev 3 1 : 20
Kitchen Elev 3 1 : 20

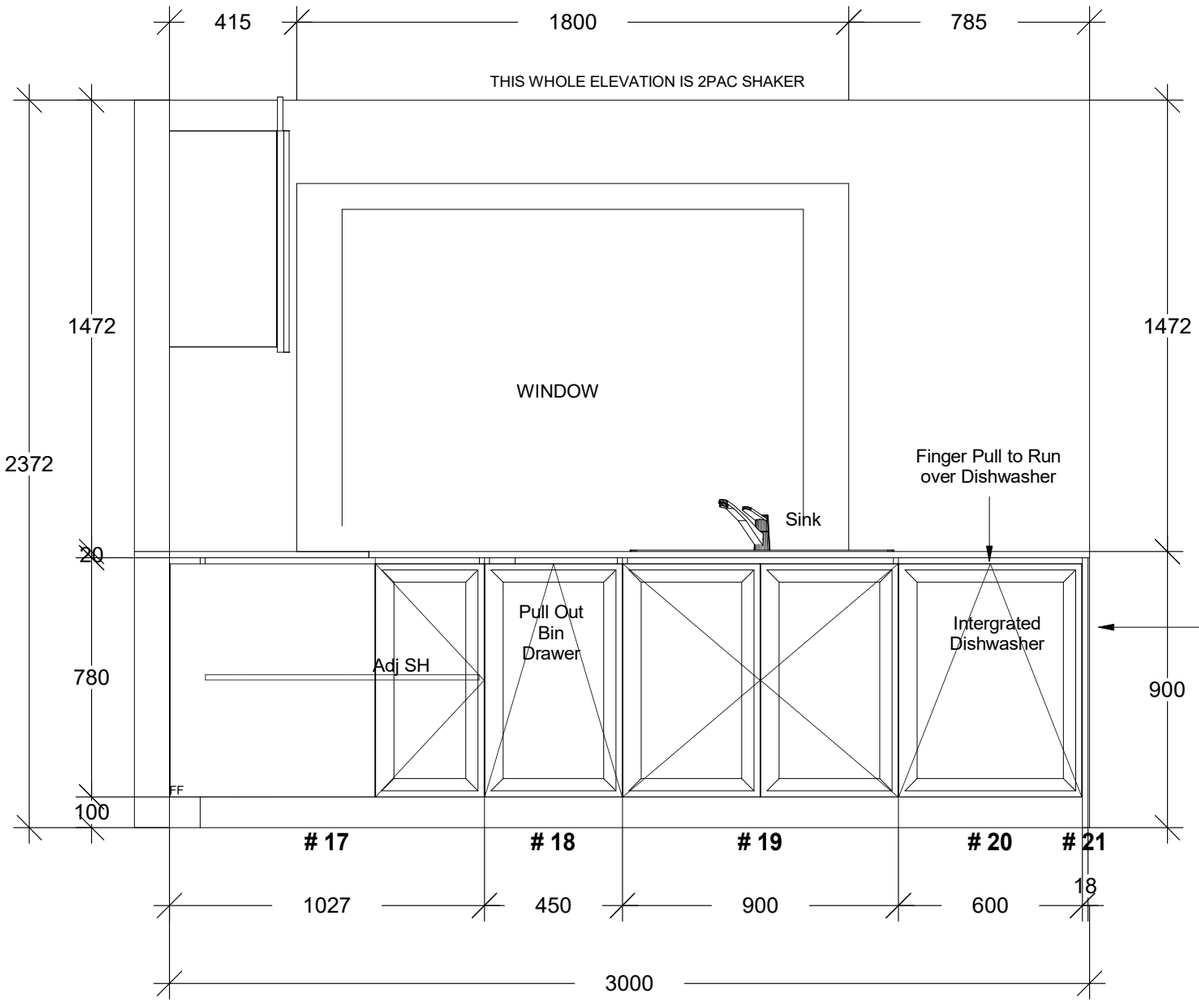

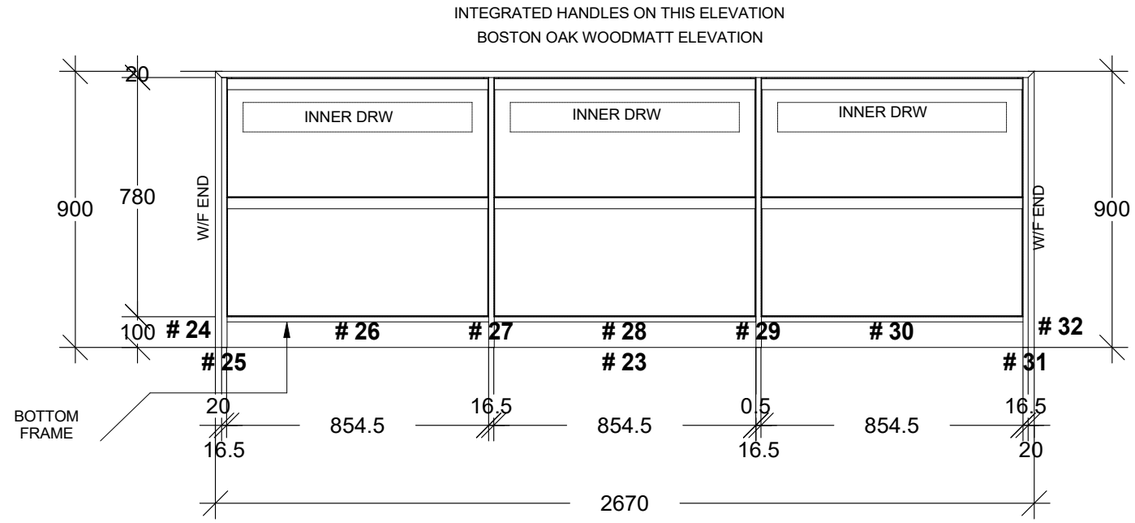

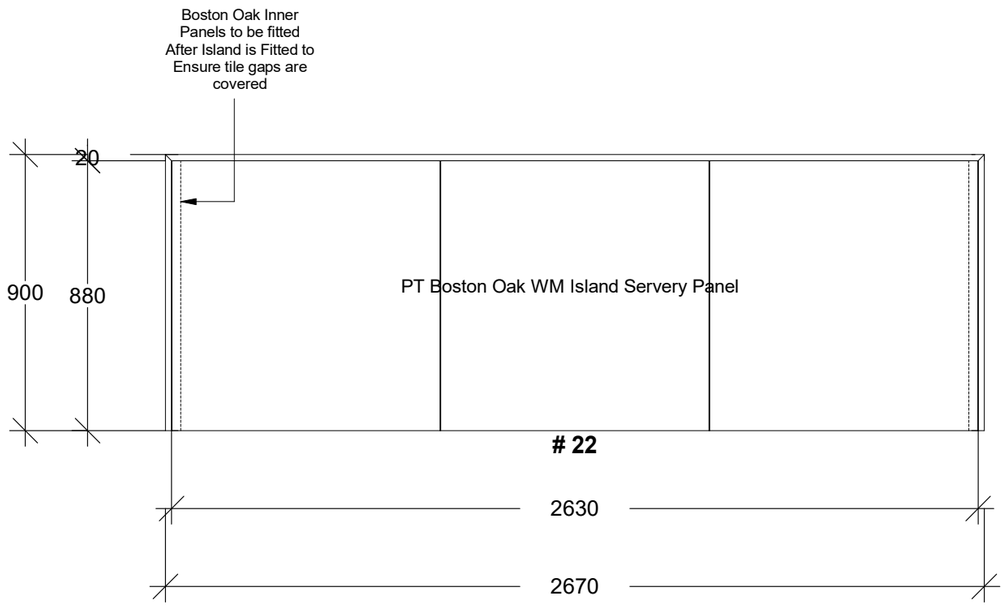


Client Approved Signature : ..... Date : .....

Kitchens By Resident Hero 32 Gateway Drive Noosaville, QLD 4566 Phone: Fax: www.residenthero.com.au	RHK6406 Tanya Rataj -	**Scale:1 : 20**	**Sheet 7 of 11**
	Joinery	Do not scale off this drawing.	Drawn By:
	20 Kyle Crt Doonan	, ,	Date: 16/06/26

All drawings are copyright & are owned & controlled by Kitchens By Resident Hero

Kitchen 3D 1 " = 1 '

Kitchen 3D 1 : 10

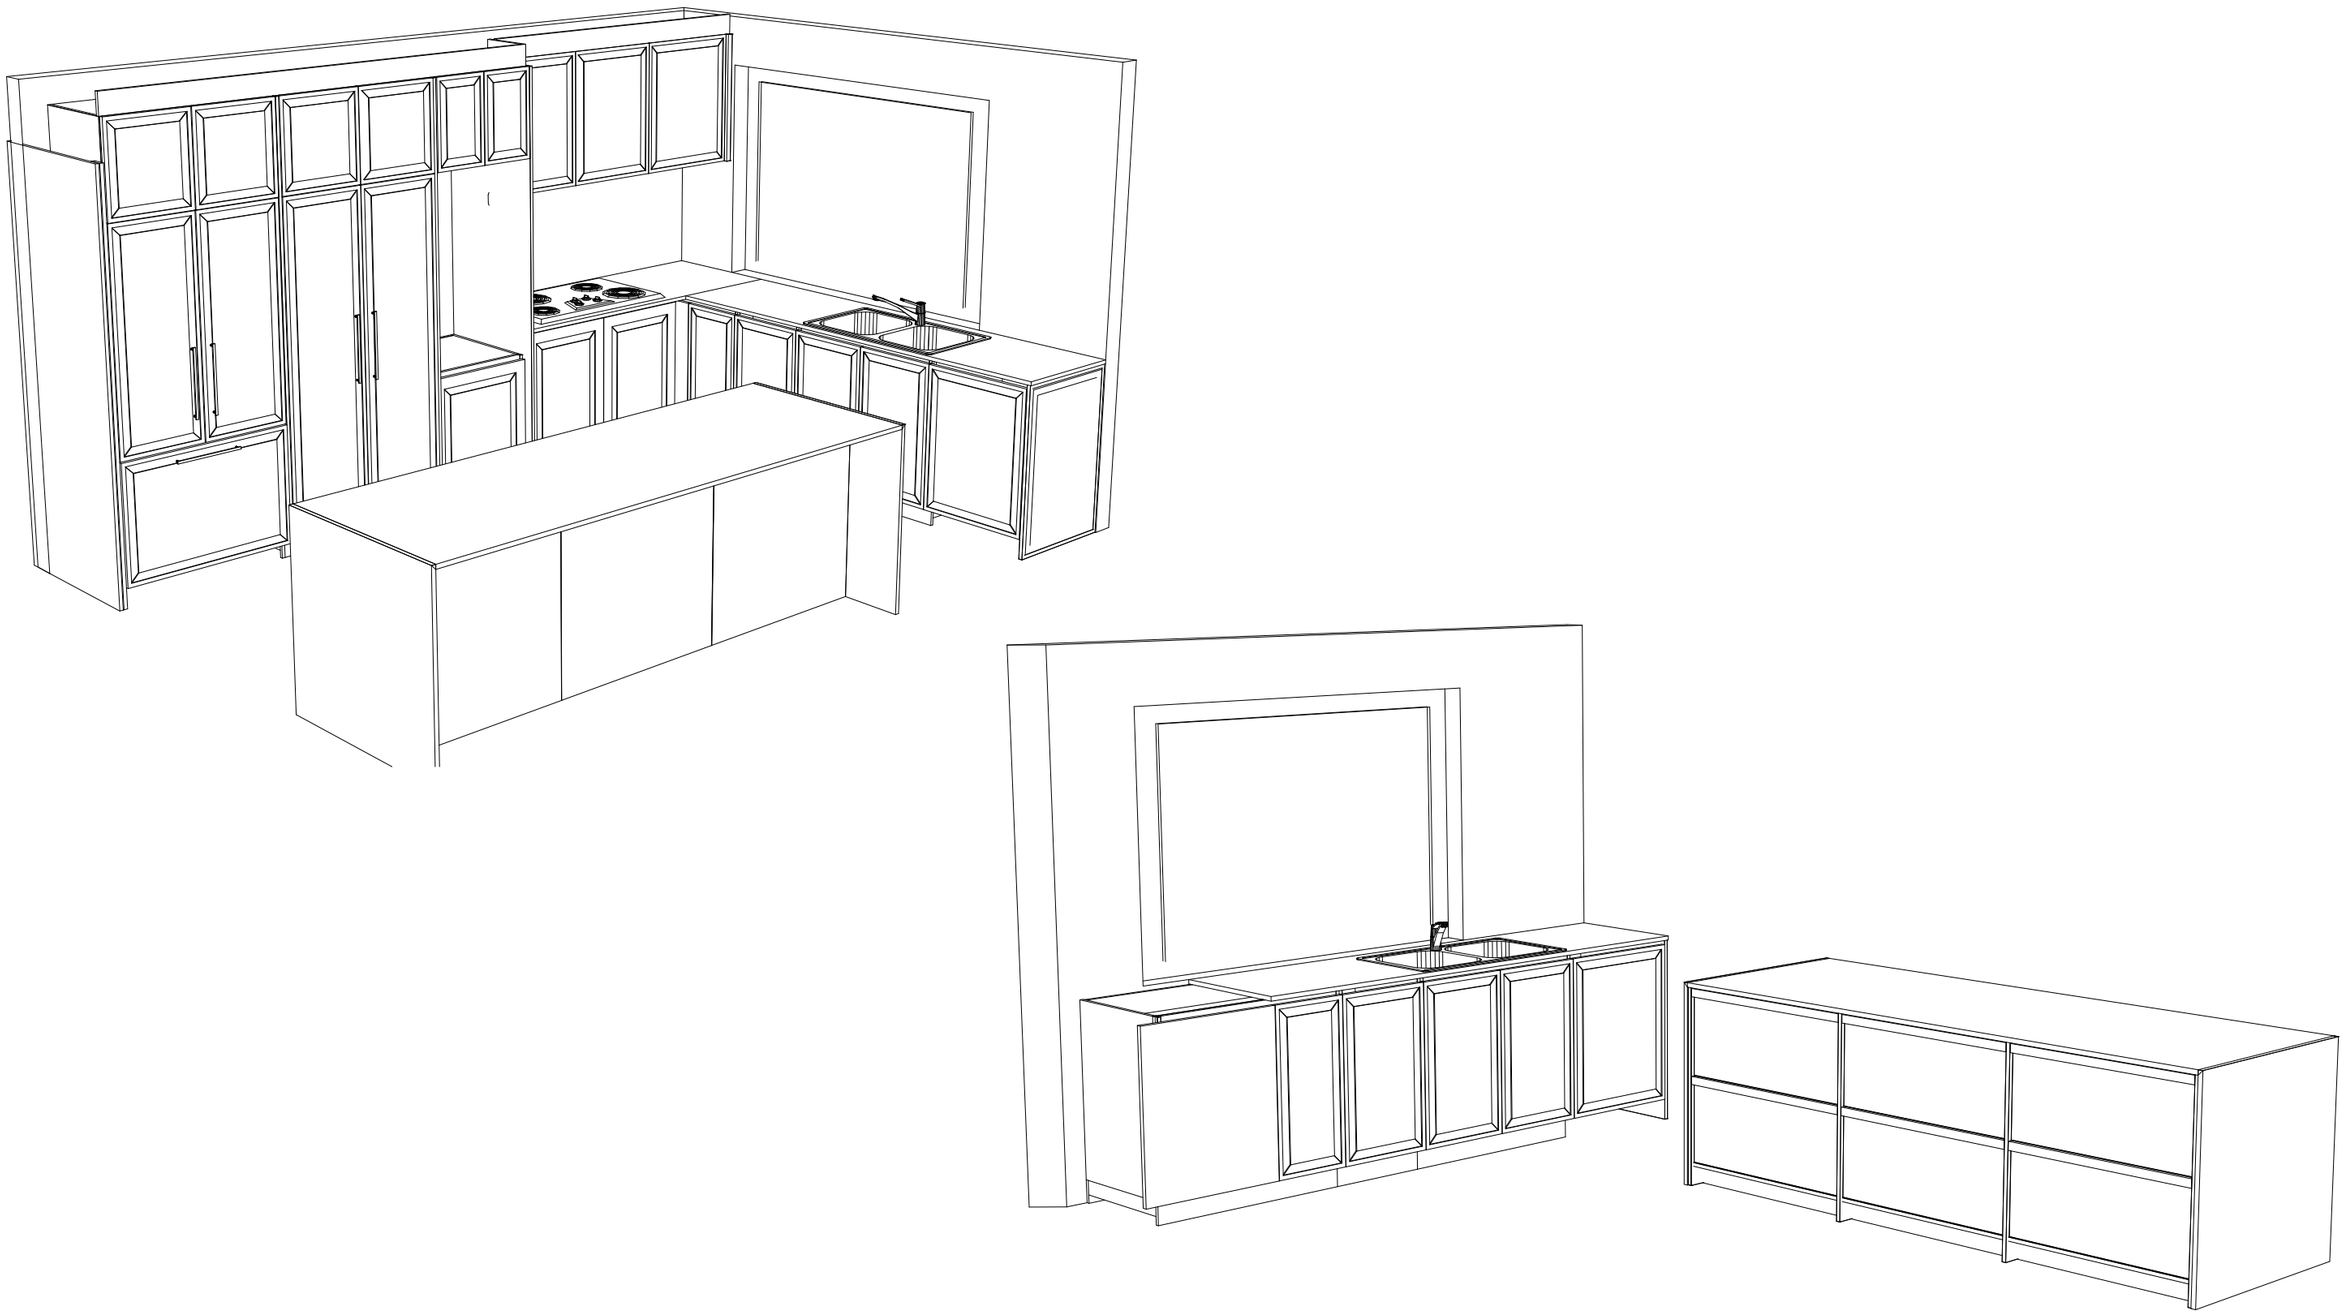


Client Approved Signature : ..... Date : .....

Kitchens By Resident Hero 32 Gateway Drive Noosaville, QLD 4566 Phone: Fax: www.residenthero.com.au	RHK6406 Tanya Rataj -	**Scale:**	**Sheet 8 of 11**
	Joinery	Do not scale off this drawing.	Drawn By:
	20 Kyle Crt Doonan	, ,	Date: 16/06/26

All drawings are copyright & are owned & controlled by Kitchens By Resident Hero

Kitchen 3D 1 : 10

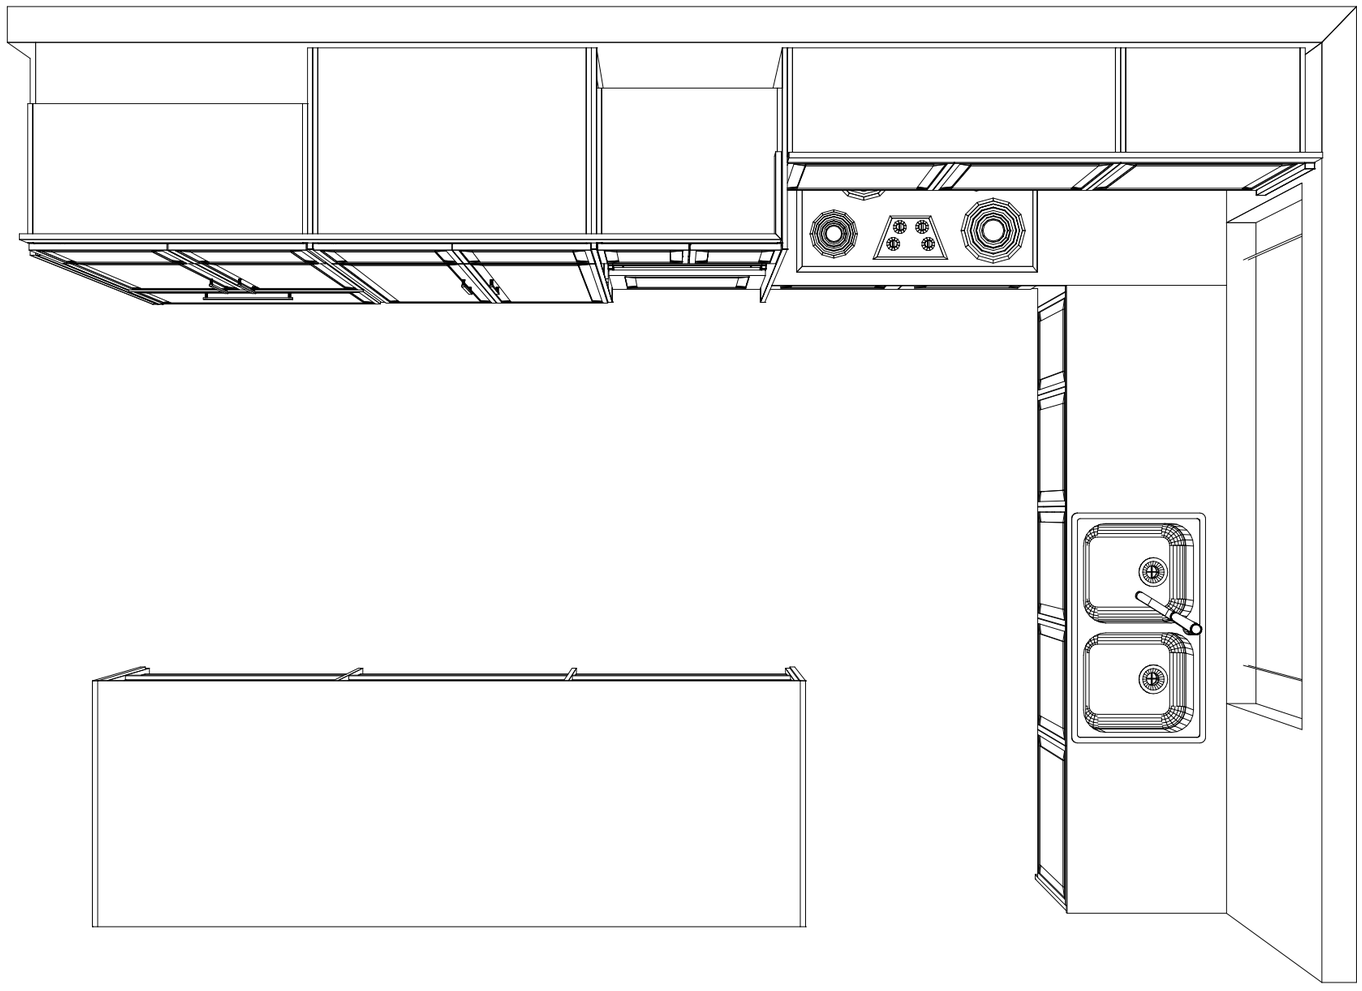

Client Approved Signature : ..... Date : .....

Kitchens By Resident Hero 32 Gateway Drive Noosaville, QLD 4566 Phone: Fax: www.residenthero.com.au	RHK6406 Tanya Rataj -	**Scale:1 : 10**	**Sheet 9 of 11**
	Joinery	Do not scale off this drawing.	Drawn By:
	20 Kyle Crt Doonan	, ,	Date: 16/06/26

All drawings are copyright & are owned & controlled by Kitchens By Resident Hero

Laundry 3D 1 : 10
Laundry Plan 1 : 20

INTERNAL CARCASE COLOUR: 16mm Whiteboard

BASE DOOR COLOUR : 21mm 2pac Shaker Style
Taubmans Almond Milk Satin


HANDLES : Set back Square Edge Finger Pulls


HANGING RAIL: 25mm Tasmanian Oak Dowel fixed to underside of cabinet

KICKS : To Match Doors Above

HARDWARE :

BLUM SOFT CLOSE HINGES
NIKPOL SOFT CLOSE DRAWERS

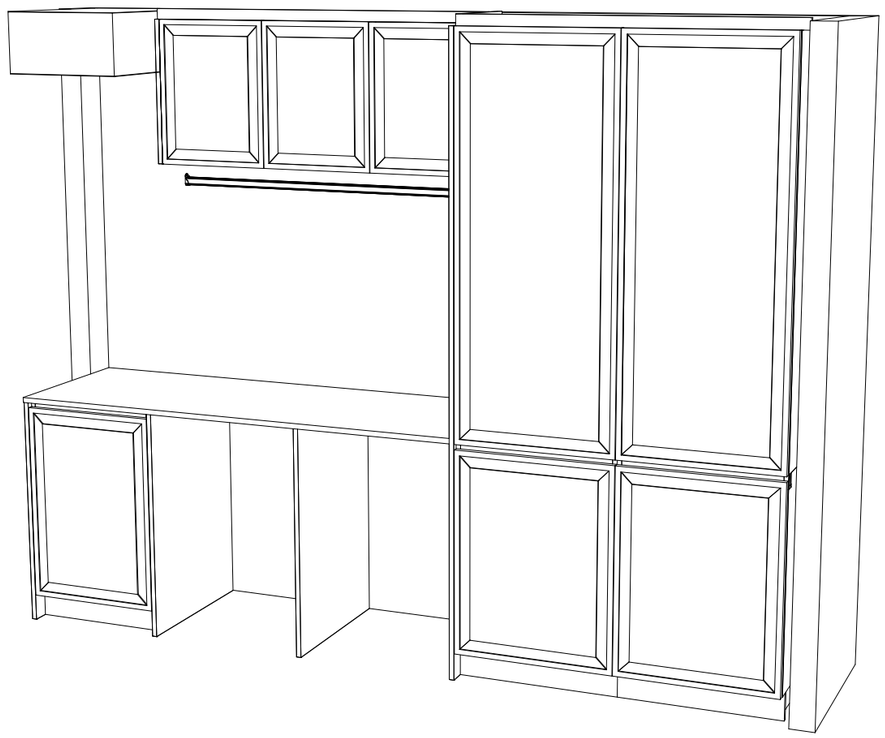

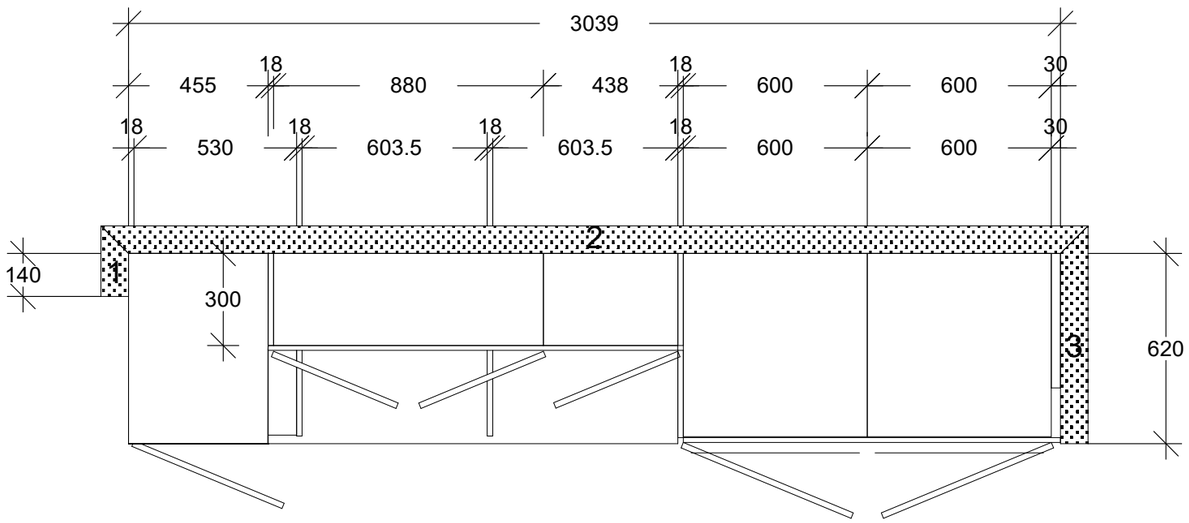


Client Approved Signature : ..... Date : .....

Kitchens By Resident Hero 32 Gateway Drive Noosaville, QLD 4566 Phone: Fax: www.residenthero.com.au	RHK6406 Tanya Rataj -	**Scale:**	**Sheet 10 of 11**
	Joinery	Do not scale off this drawing.	Drawn By:
	20 Kyle Crt Doonan	, ,	Date: 16/06/26

All drawings are copyright & are owned & controlled by Kitchens By Resident Hero

Laundry Elev 2

1 : 20

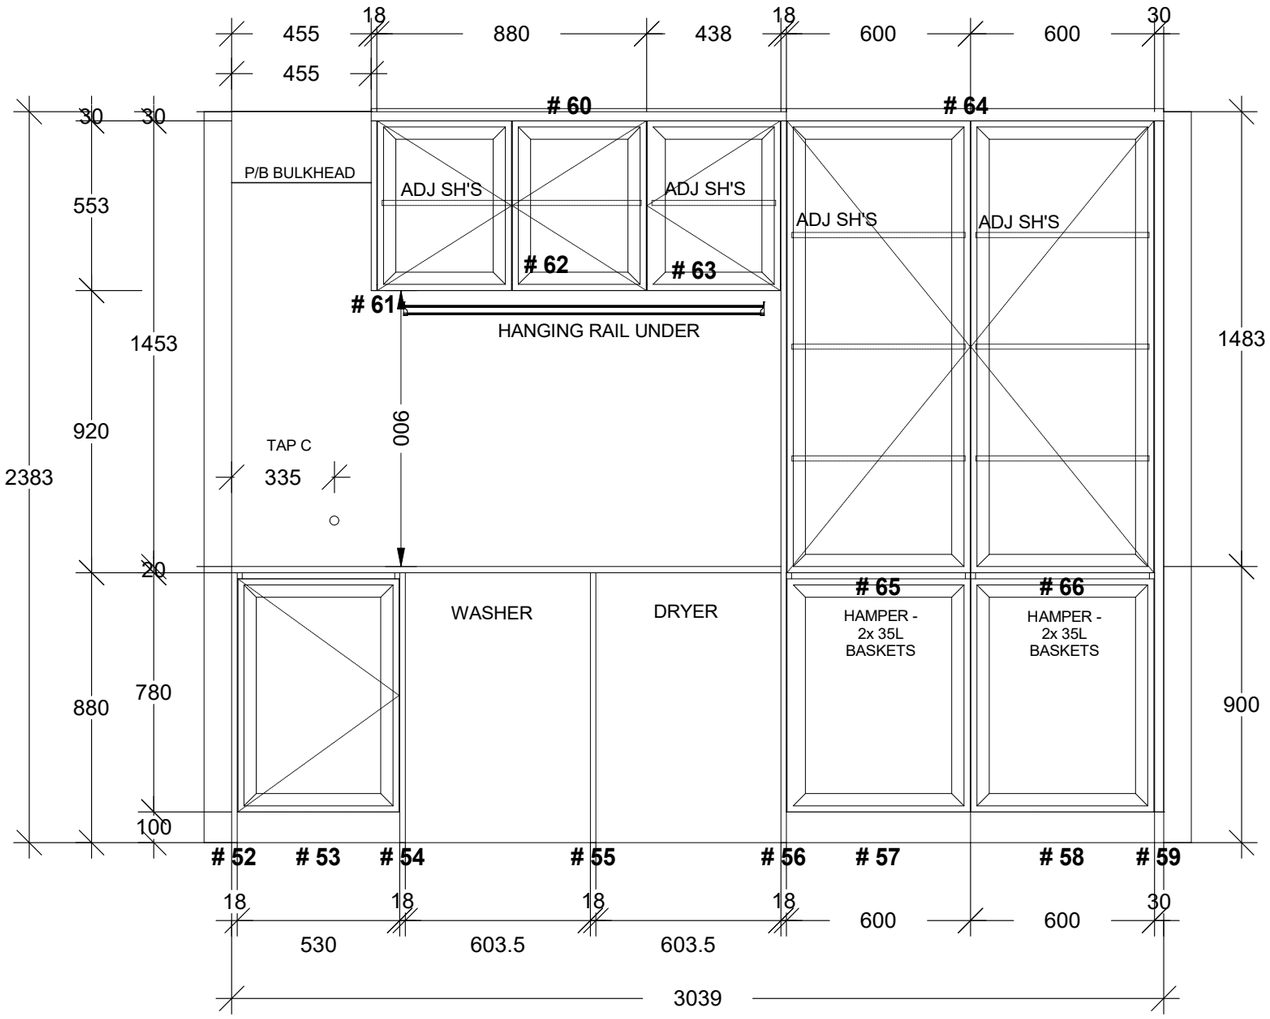

Client Approved Signature : ..... Date : .....

Kitchens By Resident Hero 32 Gateway Drive Noosaville, QLD 4566 Phone: Fax: www.residenthero.com.au	RHK6406 Tanya Rataj -	**Scale:1 : 20**	**Sheet 11 of 11**
	Joinery	Do not scale off this drawing.	Drawn By:
	20 Kyle Crt Doonan	, ,	Date: 16/06/26

All drawings are copyright & are owned & controlled by Kitchens By Resident Hero