Kitchen Plan

1 : 20

BENCH TOPS : 20mm STONE AMBASSADOR
"KIREC" WITH DROP IN SINK CUTOUT

INTERNAL CARCASE COLOUR: 16mm WHITEBOARD

BASE DOOR COLOUR : 2PAC SATIN FINISH
"RESENE ALABASTER"

OVERHEAD DOOR COLOUR: 2PAC SATIN FINISH
"RESENE ALABASTER"


BULKHEAD: RAW MDF PAINTED BY OTHERS OR
2PAC ALABASTER - SCRIBED TO CEILING

HANDLES : TBC

KICKS : TO MATCH BASE CUPBOARD FRONTS

HARDWARE :

BLUM SOFT CLOSE HINGES
NIKPOL DRAGON PRO SOFT CLOSE DRAWERS

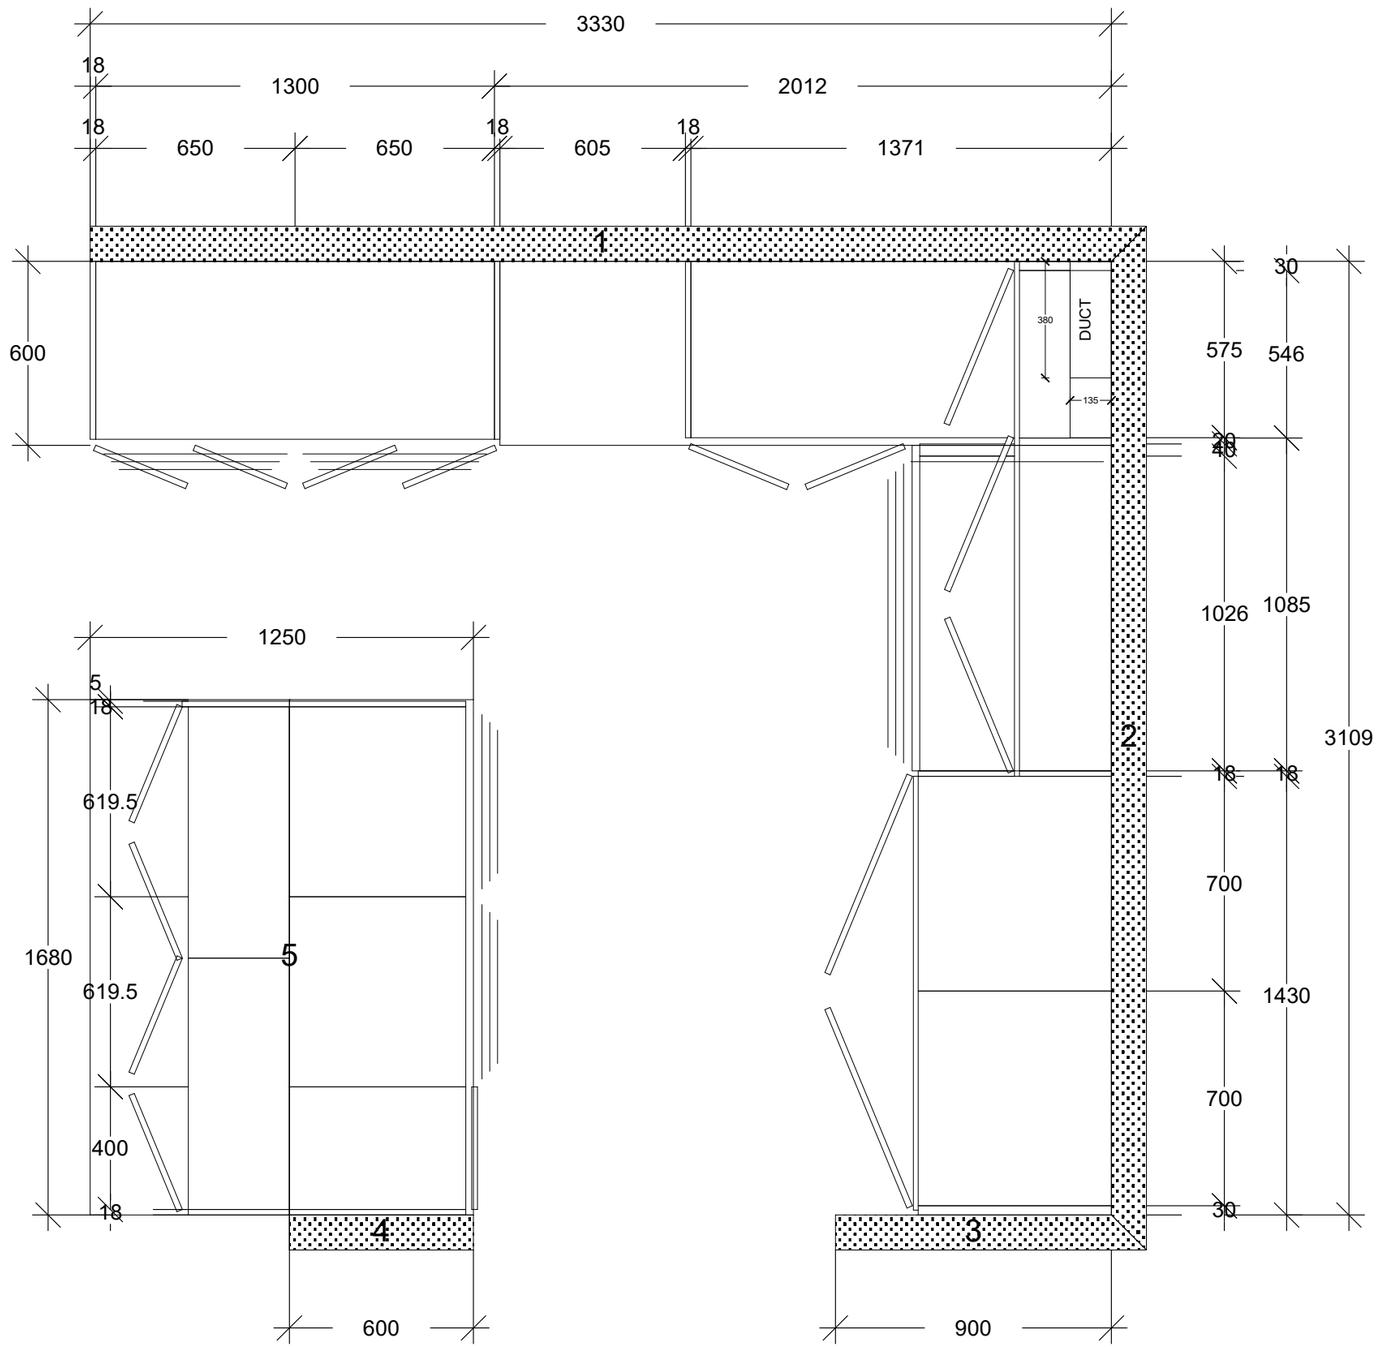


Client Approved Signature : ..... Date : .....

Kitchens By Resident Hero 32 Gateway Drive Noosaville, QLD 4566 Phone: Fax: www.residenthero.com.au	RHK6456 Jeff and Suzie Morris	**Scale:1 : 20**	**Sheet 1 of 6**
	Joinery	Do not scale off this drawing.	Drawn By:
	3/5 TINGIRA CRES SUNRISE BEACH	, ,	Date: 06/07/26

All drawings are copyright & are owned & controlled by Kitchens By Resident Hero

Kitchen Elev 1

1 : 15

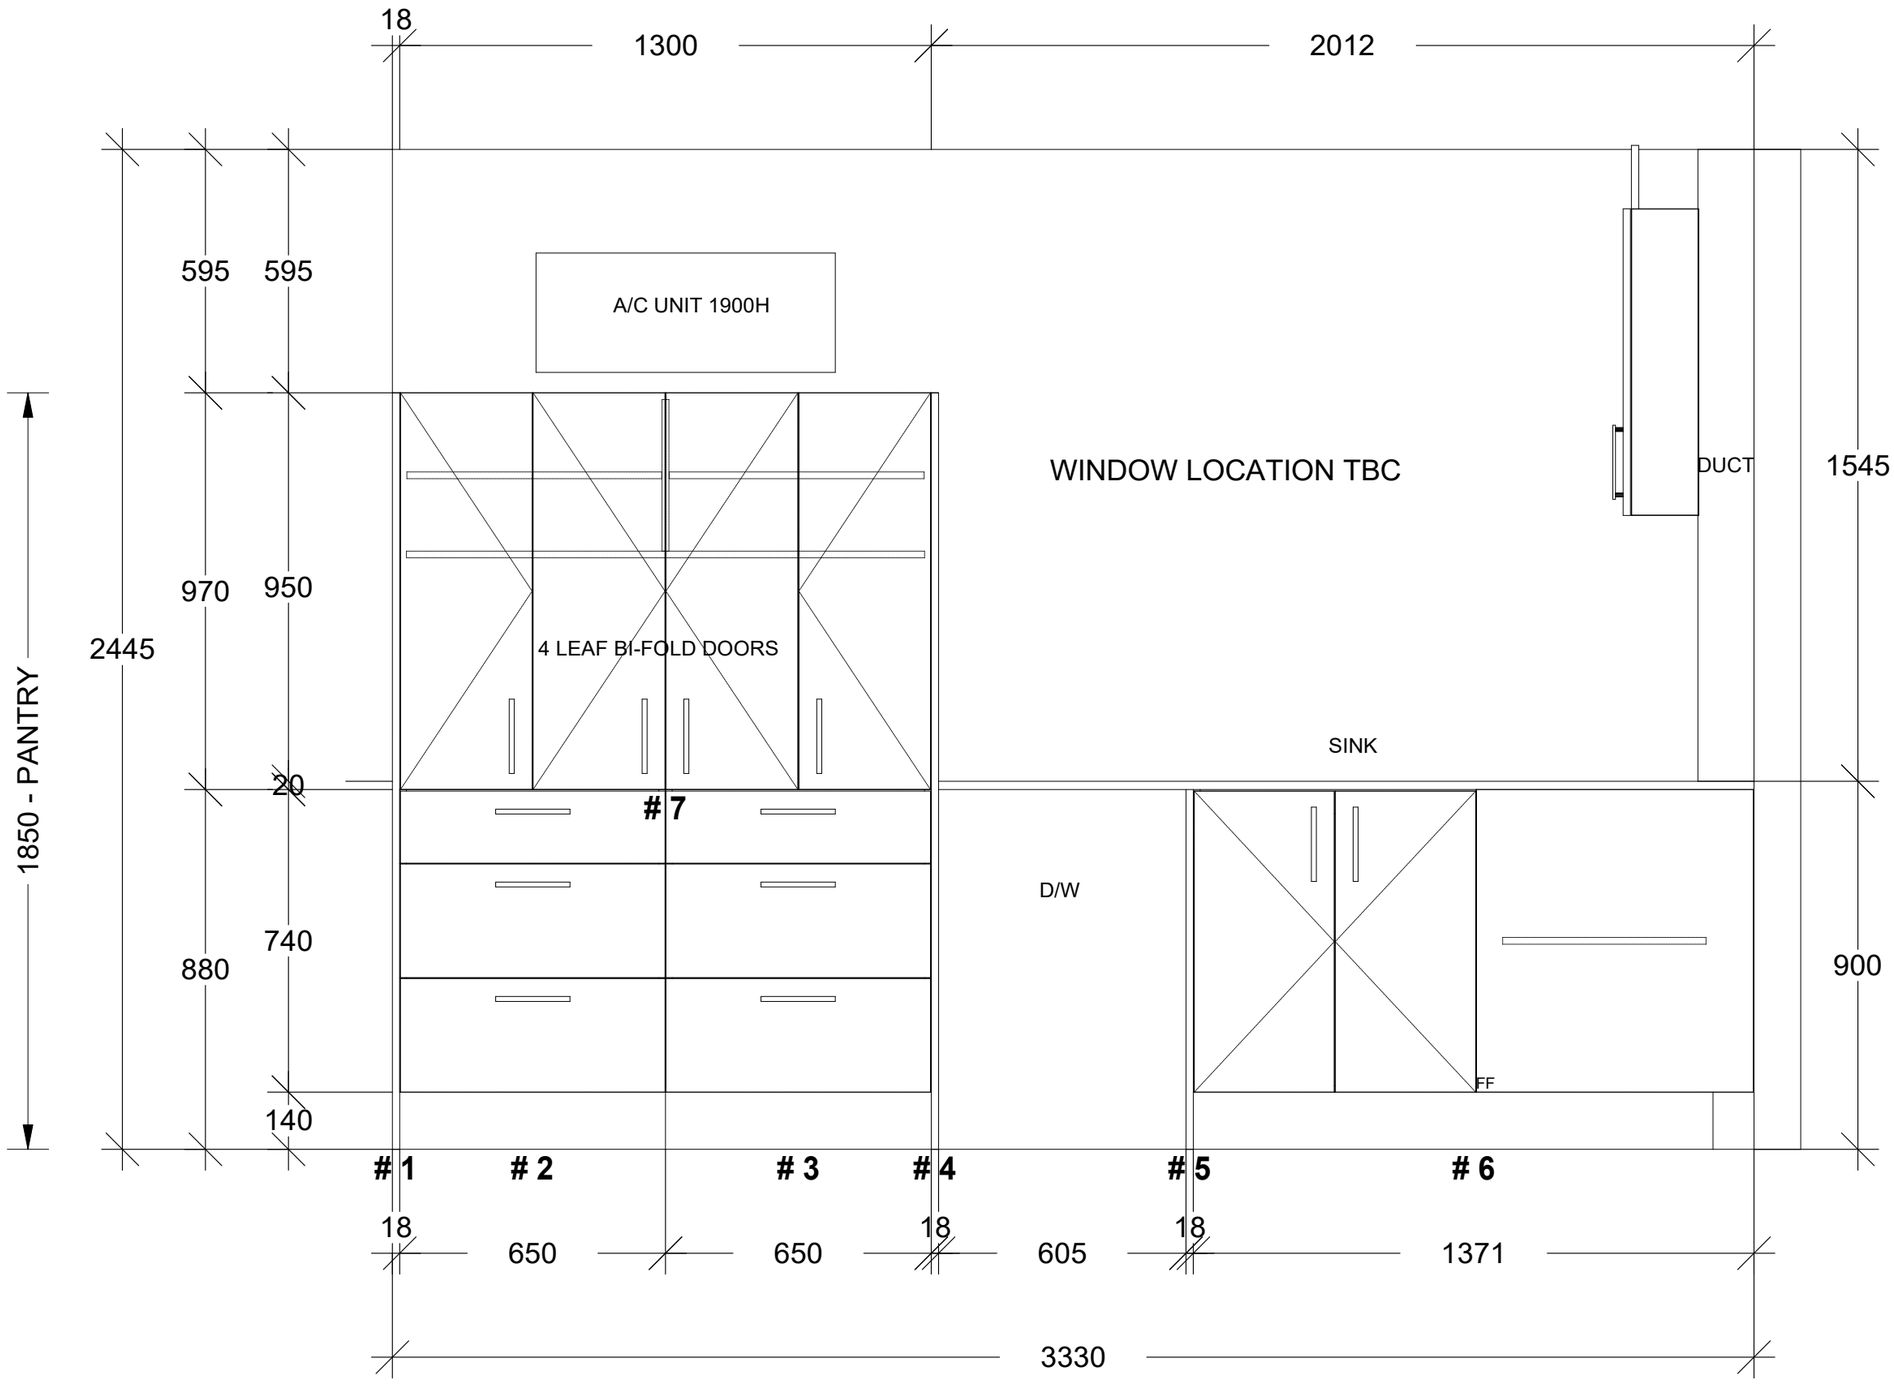

Client Approved Signature : ..... Date : .....


Kitchens By Resident Hero
32 Gateway Drive
Noosaville, QLD 4566
Phone: Fax:
www.residenthero.com.au

RHK6456 Jeff and Suzie Morris	**Scale:1 : 15**	**Sheet 2 of 6**
Joinery	Do not scale off this drawing.	Drawn By:
3/5 TINGIRA CRES SUNRISE BEACH	, ,	Date: 06/07/26

All drawings are copyright & are owned & controlled by Kitchens By Resident Hero

Kitchen Elev 2

1 : 15

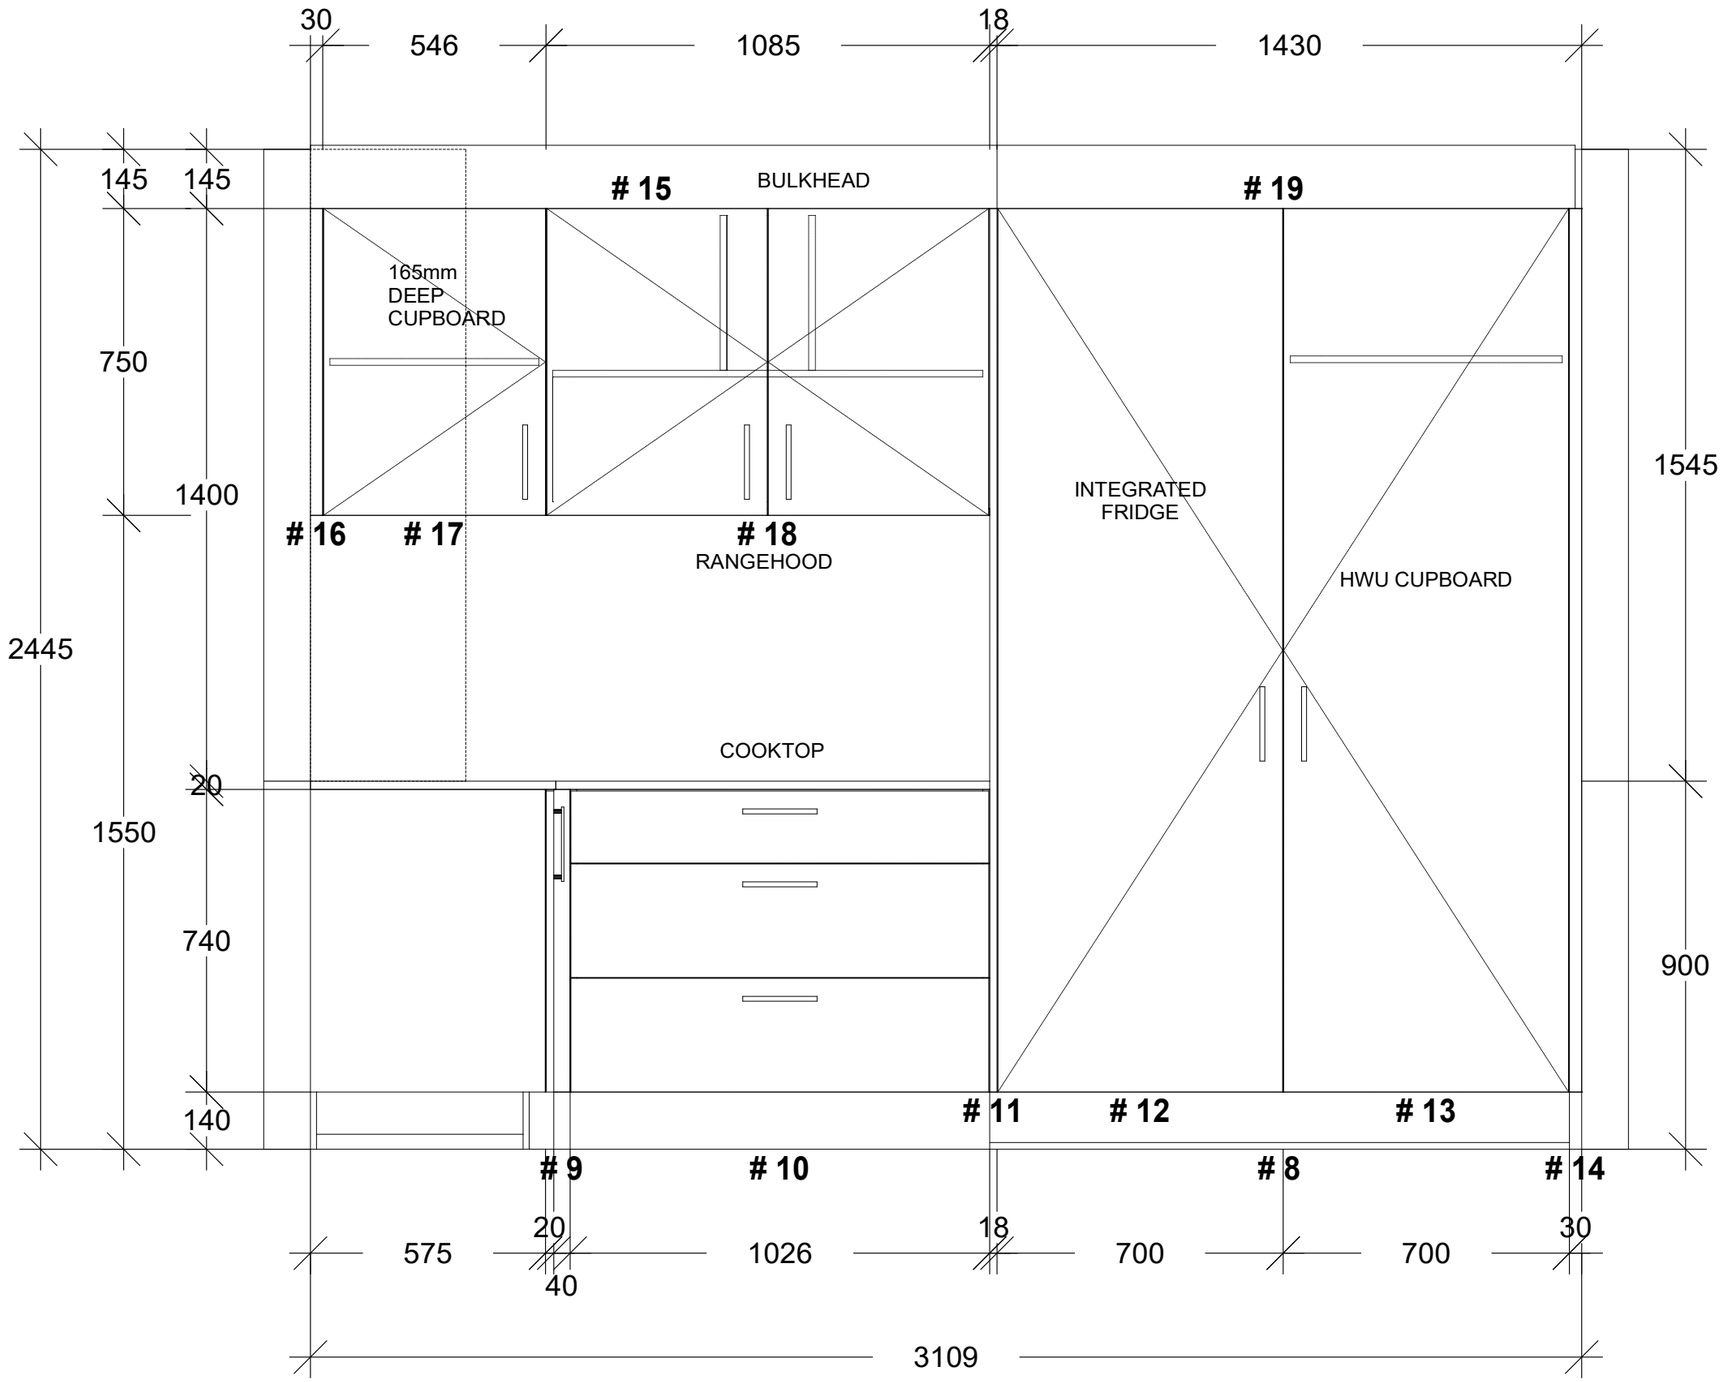


Client Approved Signature : ..... Date : .....


Kitchens By Resident Hero 32 Gateway Drive Noosaville, QLD 4566 Phone: Fax: www.residenthero.com.au	RHK6456 Jeff and Suzie Morris	**Scale:1 : 15**	**Sheet 3 of 6**
	Joinery	Do not scale off this drawing.	Drawn By:
	3/5 TINGIRA CRES SUNRISE BEACH	, ,	Date: 06/07/26

All drawings are copyright & are owned & controlled by Kitchens By Resident Hero

Kitchen Elev 5 1 : 15

Kitchen Elev 5 1 : 15

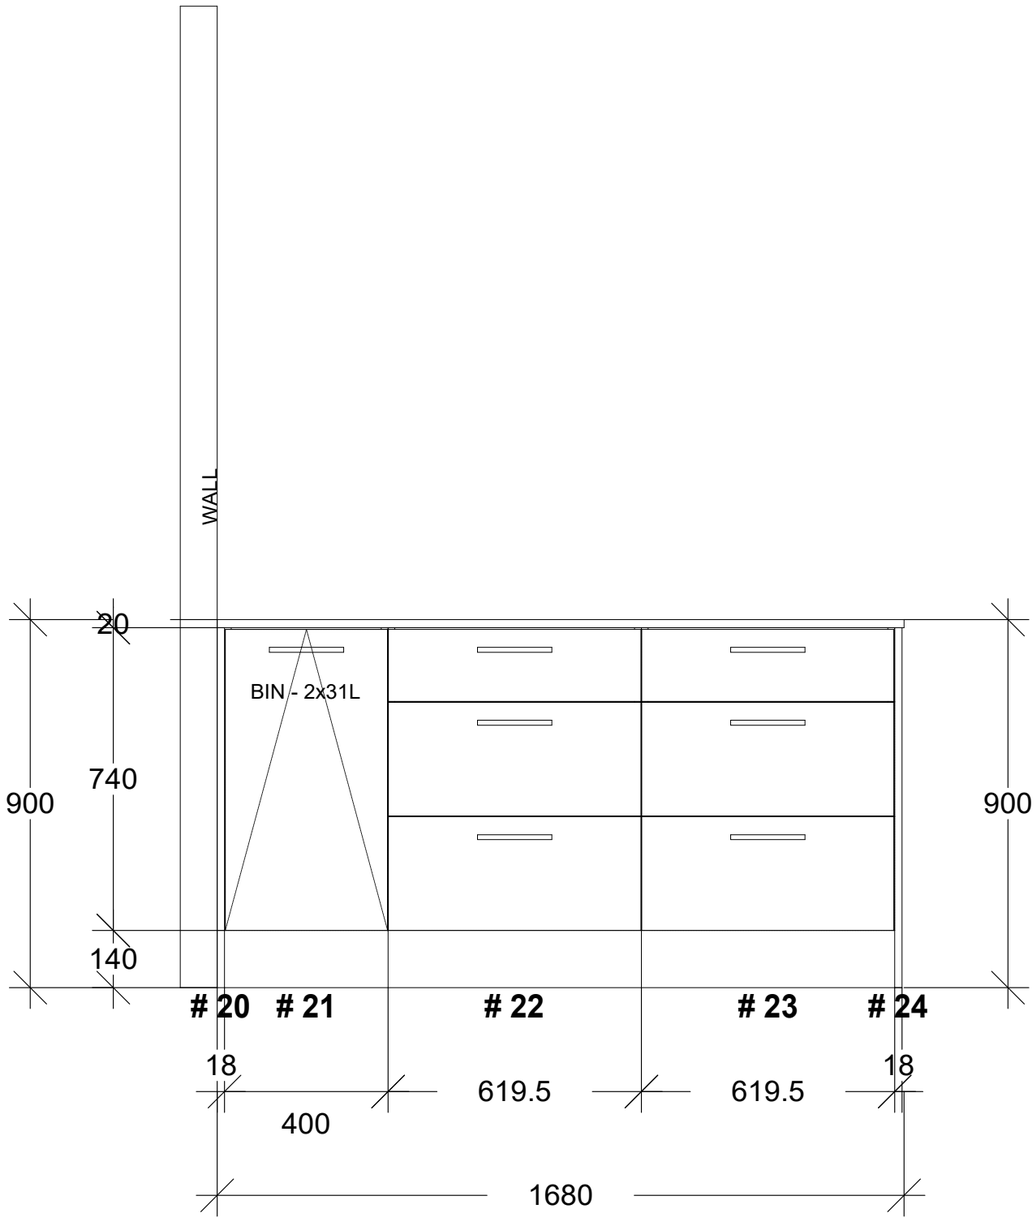

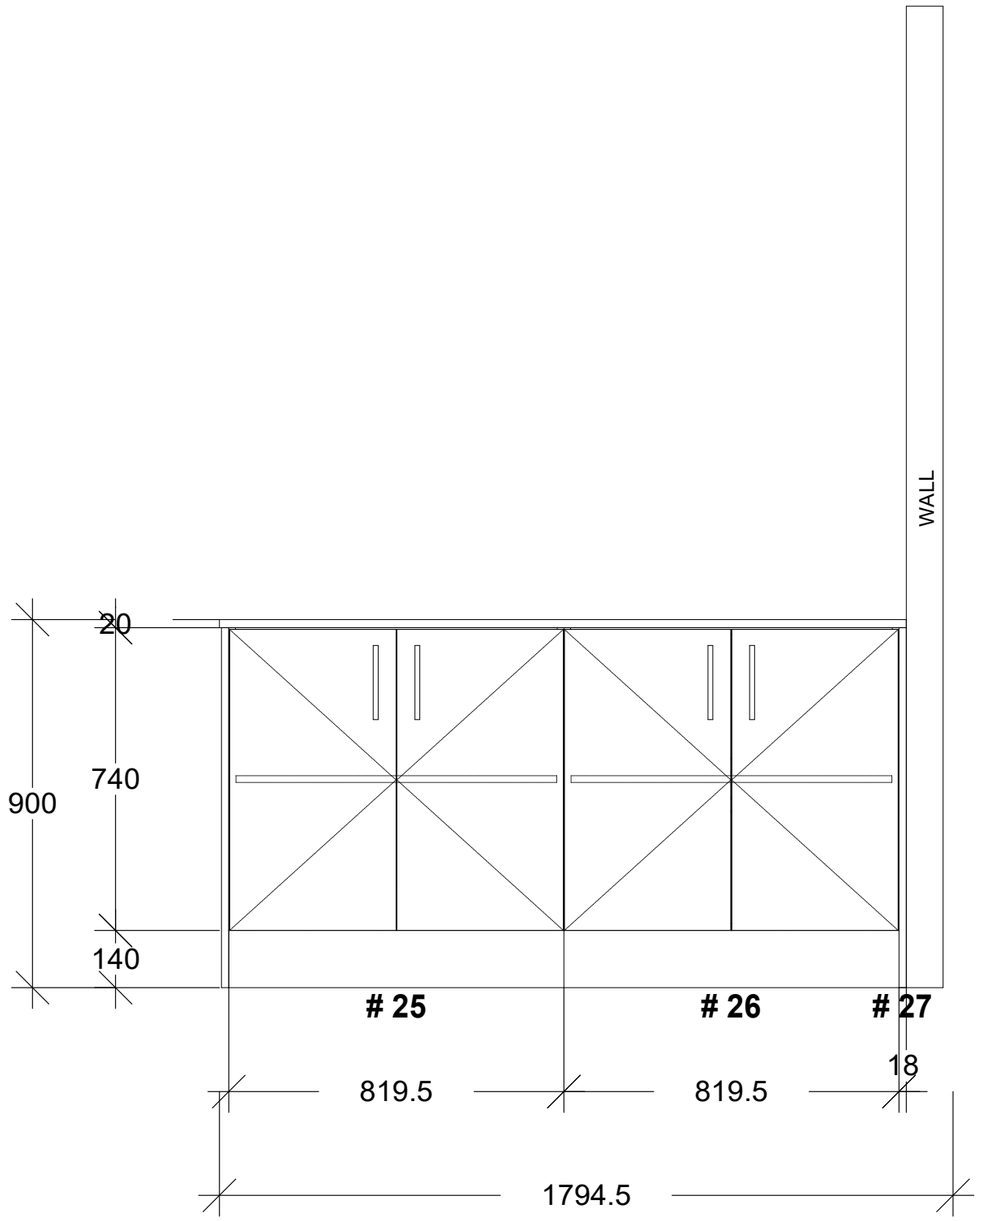



Client Approved Signature : ..... Date : .....


Kitchens By Resident Hero 32 Gateway Drive Noosaville, QLD 4566 Phone: Fax: www.residenthero.com.au	RHK6456 Jeff and Suzie Morris	**Scale:1 : 15**	**Sheet 4 of 6**
	Joinery	Do not scale off this drawing.	Drawn By:
	3/5 TINGIRA CRES SUNRISE BEACH	, ,	Date: 06/07/26

All drawings are copyright & are owned & controlled by Kitchens By Resident Hero

Kitchen 3D 1 " = 1 '
Kitchen 3D 1 " = 1 '
Kitchen 3D 1 " = 1 '

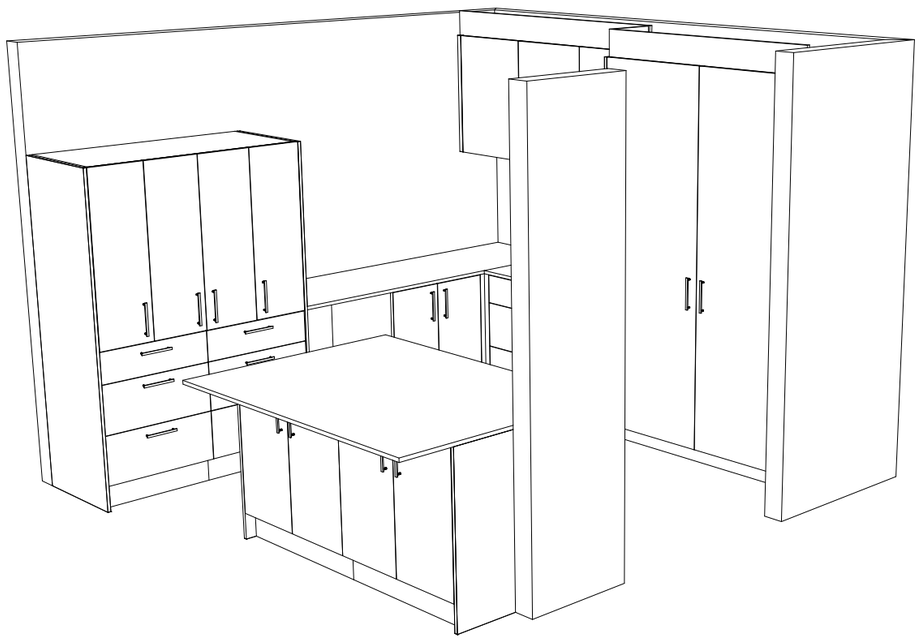

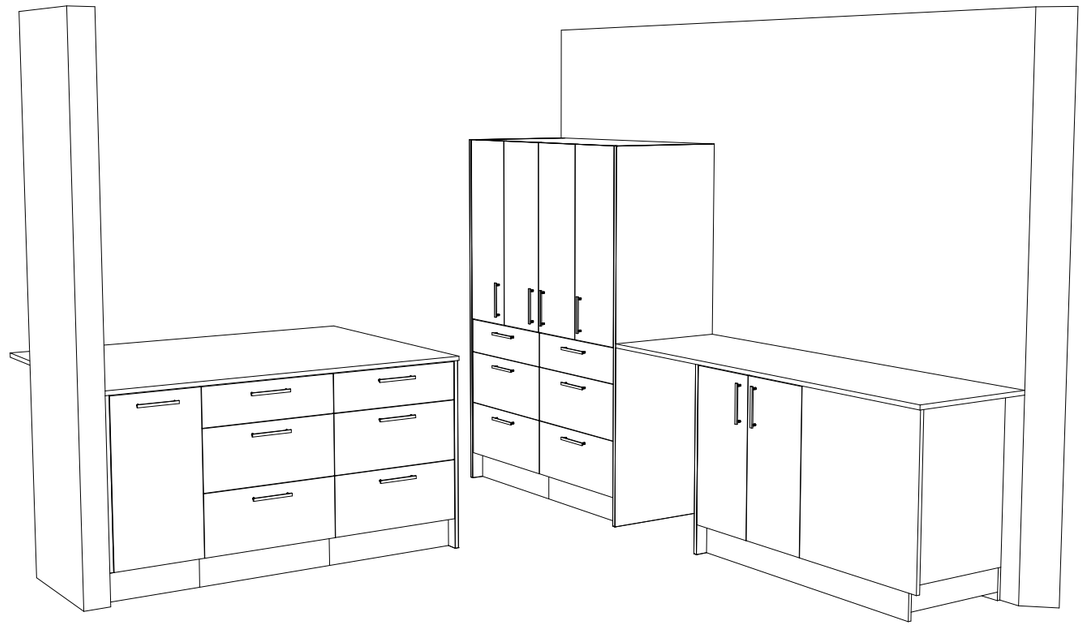

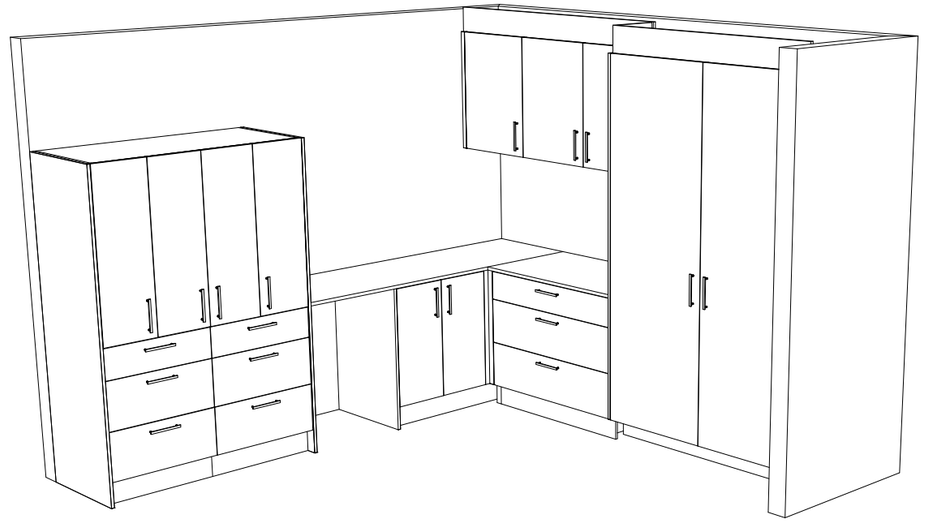

Client Approved Signature : ..... Date : .....


RESIDENT HERO
Kitchens By Resident Hero
32 Gateway Drive
Noosaville, QLD 4566
Phone: Fax:
www.residenthero.com.au

RHK6456 Jeff and Suzie Morris	**Scale:1 " = 1 '**	**Sheet 5 of 6**
Joinery	Do not scale off this drawing.	Drawn By:
3/5 TINGIRA CRES SUNRISE BEACH	, ,	Date: 06/07/26

All drawings are copyright & are owned & controlled by Kitchens By Resident Hero

Kitchen Elev 1 1 : 15

BI-FOLD DOORS OFF FOR CLARITY

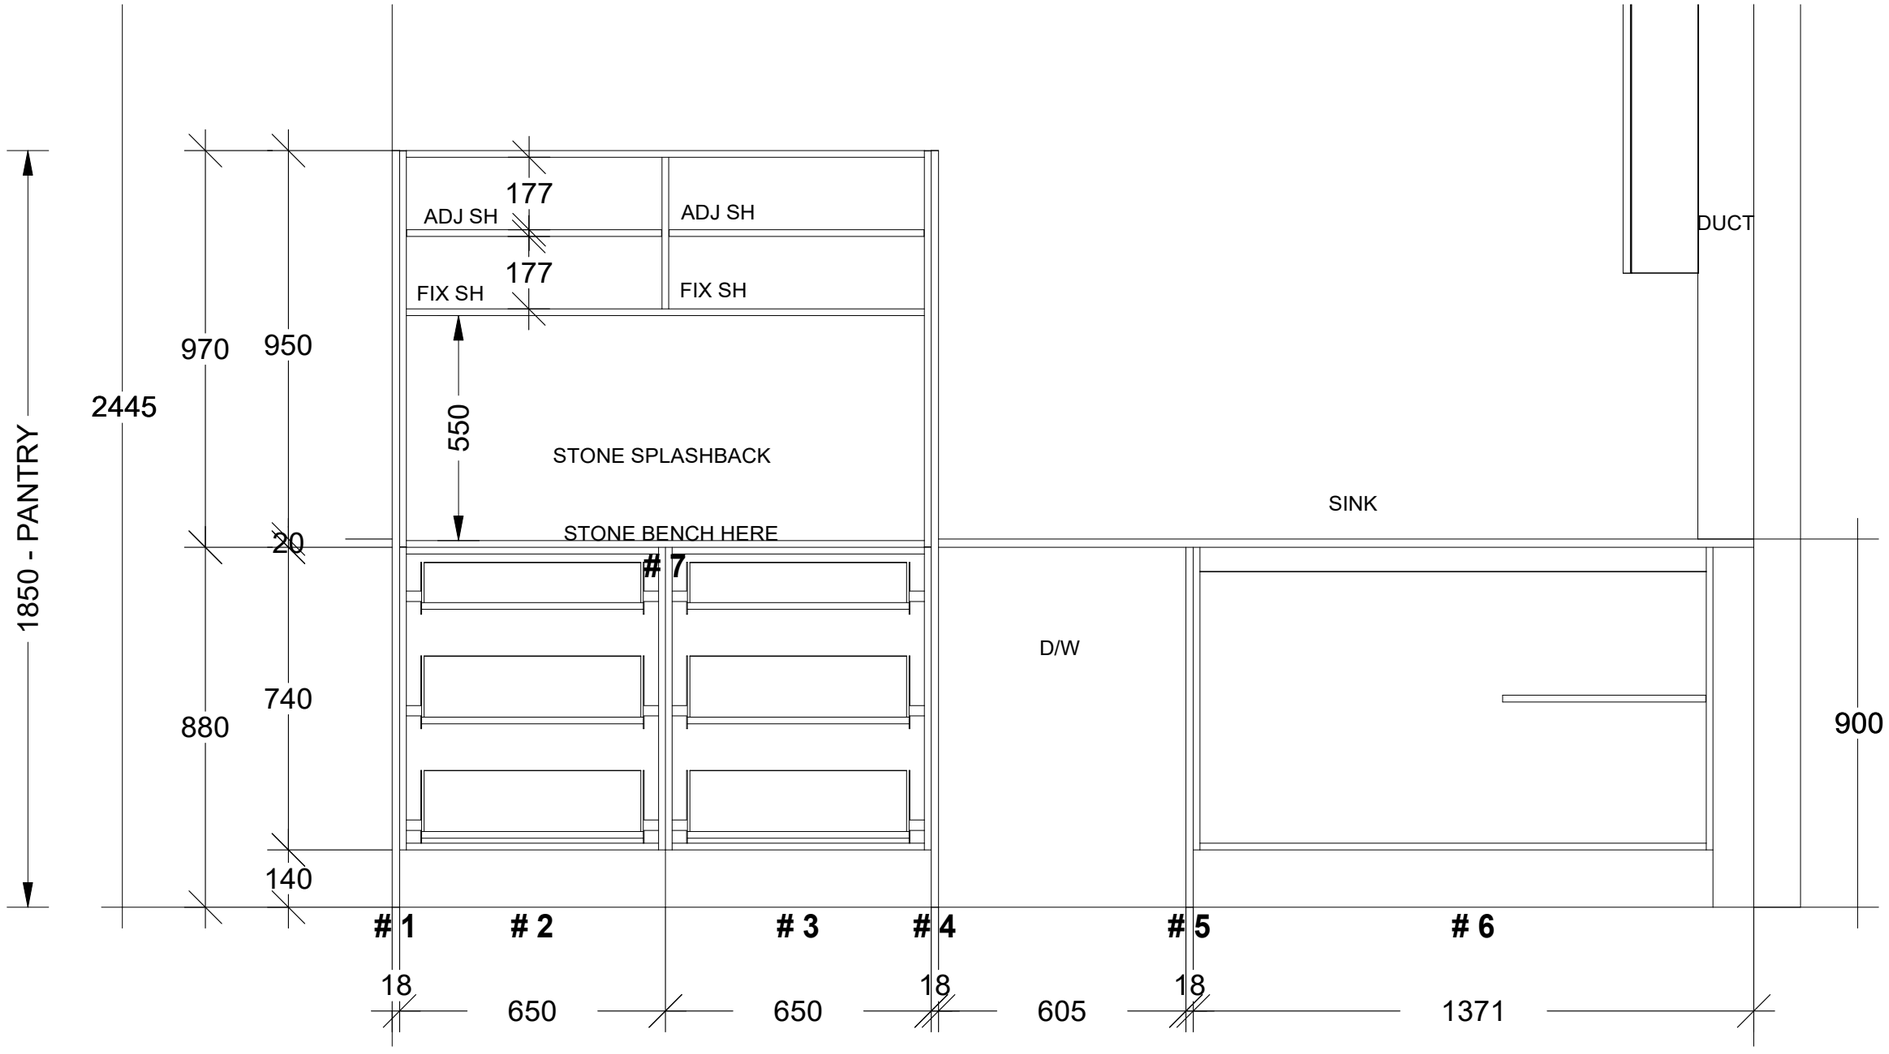

Client Approved Signature : ..... Date : .....

RESIDENT HERO Kitchens By Resident Hero 32 Gateway Drive Noosaville, QLD 4566 Phone: Fax: www.residenthero.com.au	RHK6456 Jeff and Suzie Morris	**Scale:1 : 15**	**Sheet 6 of 6**
	Joinery	Do not scale off this drawing.	Drawn By:
	3/5 TINGIRA CRES SUNRISE BEACH	, ,	Date: 06/07/26

All drawings are copyright & are owned & controlled by Kitchens By Resident Hero